

FÖRESKRIFTER

ALLMÄNNA ANVISNINGAR: K-01-1-D001

FÖRKLARINGAR


- 1 = HÅLTAGNING I BJÄLKLAG FÖR VENT
2 = HÅLTAGNING I BJÄLKLAG FÖR VS
3 = HÅLTAGNING I VÄGG VS, ø60. HÖJD ENLIGT VS-HANDLING.
4 = HÅLTAGNING I VÄGG VS, ø70. HÖJD ENLIGT VS-HANDLING.
5 = HÅLTAGNING I VÄGG VS, ø100. HÖJD ENLIGT VS-HANDLING.
6 = HÅLTAGNING I VÄGG VS, ø140. HÖJD ENLIGT VS-HANDLING.
7 = HÅLTAGNING I VÄGG VS, ø180. HÖJD ENLIGT VS-HANDLING.
8 = 2st VENTILATIONSKANALER ø420mm
DRAS I BEFINTLIGA SCHAKT. BEFINTLIGA SCHAKT
ANTAS VAR IGENGJUTNA RUNT INSTALLATIONER.
9 = 2st VENTILATIONSKANALER 340x440mm
DRAS I BEFINTLIGT SCHAKT.
BEFINTLIGA SCHAKT ANTAS VAR IGEN GJUTNA RUNT
INSTALLATIONER
10 = DÖRRÖPPNING, BALKONG. BREDDAS 100mm
11 = NY DÖRRÖPPNING 1280x2230mm I BEFINTLIG
BETONGVÄGG MED TJOCKLEK 150mm.
12 = 105MM BREDDNING AV BEFINTLIG
DÖRRÖPPNING
13 = NY DÖRRÖPPNING 910x2110mm I BEFINTLIG
BETONGVÄGG MED TJOCKLEK 150mm.
14 =BEF. DÖRRÖPPNING SÅGAS UPP TILL EN STÖRRE
ÖPPNING 2110x2295.
BETONGVÄGG MED TJOCKLEK 150mm.

MÄTT I HÖJD FÖR HÅLTAGNINGAR I VÄGG ENLIGT
RESPEKTIVE VS-, VENT- & EL-HANDLINGAR

HÄNVISNINGAR

PLANER	
GRUNDPLAN:	K-15-1-D090
KÄLLARPLAN -DEL 1:	K-20-1-D091
KÄLLARPLAN - DEL 2:	K-20-1-D092
PLAN 1 - DEL 1:	K-20-1-D101
PLAN 1 - DEL 2:	K-20-1-D102
PLAN 2 - DEL 1:	K-20-1-D201
PLAN 2 - DEL 2:	K-20-1-D202
FLÄKTRUM - DEL 1:	K-20-1-D301
FLÄKTRUM - DEL 2:	K-20-1-D302

GODKÄND		2025-02-26	MG
BET	ÄNDRING AVSER	DATUM	SIGN
FÖRFRÅGNINGSUNDERLAG			
BYGGHANDLING			
2025-02-26		GODKÄND	
STATUS		ÄNDRING	
CENTRUMHUSET HUS D			
KRÅKAN 1, ROBERTSFORS			
ÄF-Infrastructure AB			
Strandgatan 9A			
891. 39 Örnsköldsvik			
Tel: 010-505 00 00			
MARCUS GRANQVIST		SKAPAD AV	
ROBIN ÖSTMAN		UPPERAGSNUMMER	
D0192211		RITNINGSKATEGORI	
OMBYGGNAD BIBLIOTEK OCH LÄGENHETER			
BJÄLKLAG ÖVAN LÄGENHETSPLAN			
PLAN 2 - Del 1			
K-20-1-D201			
INNEHÅLL		FÖRSTAP	
A1		SKALA	
1		BET	

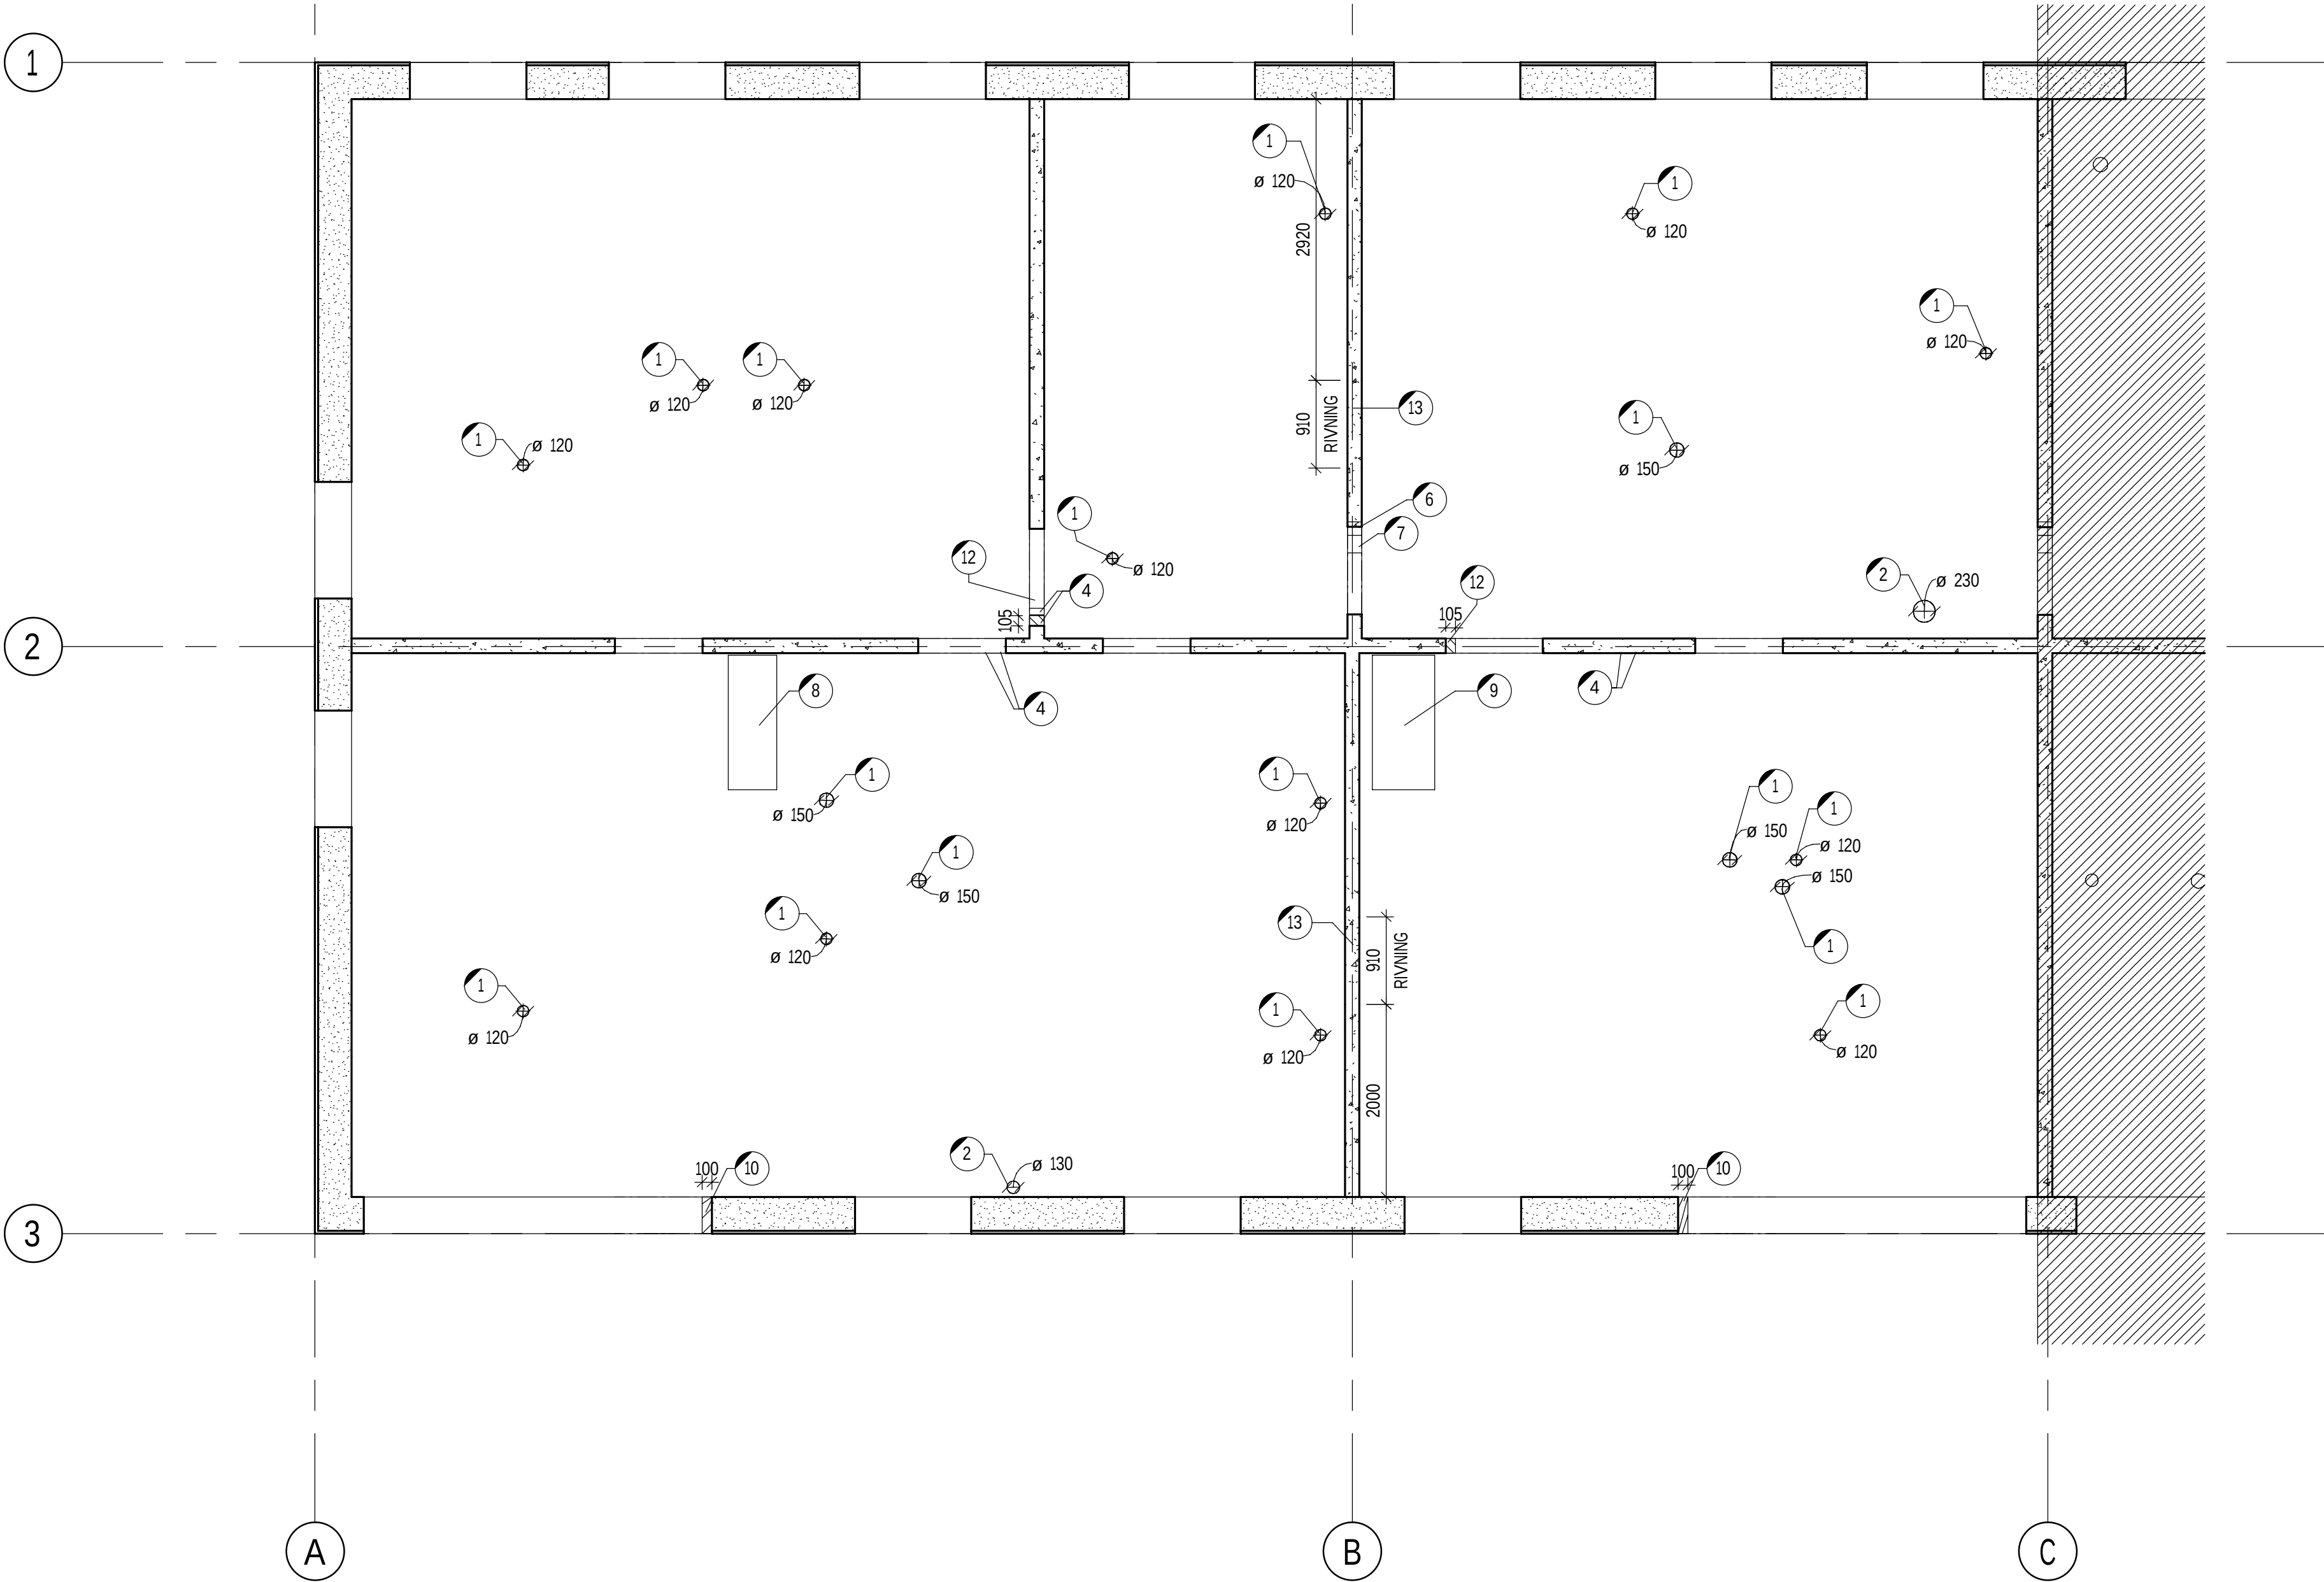

SKALA 1:50
0 1 2 5
METER