



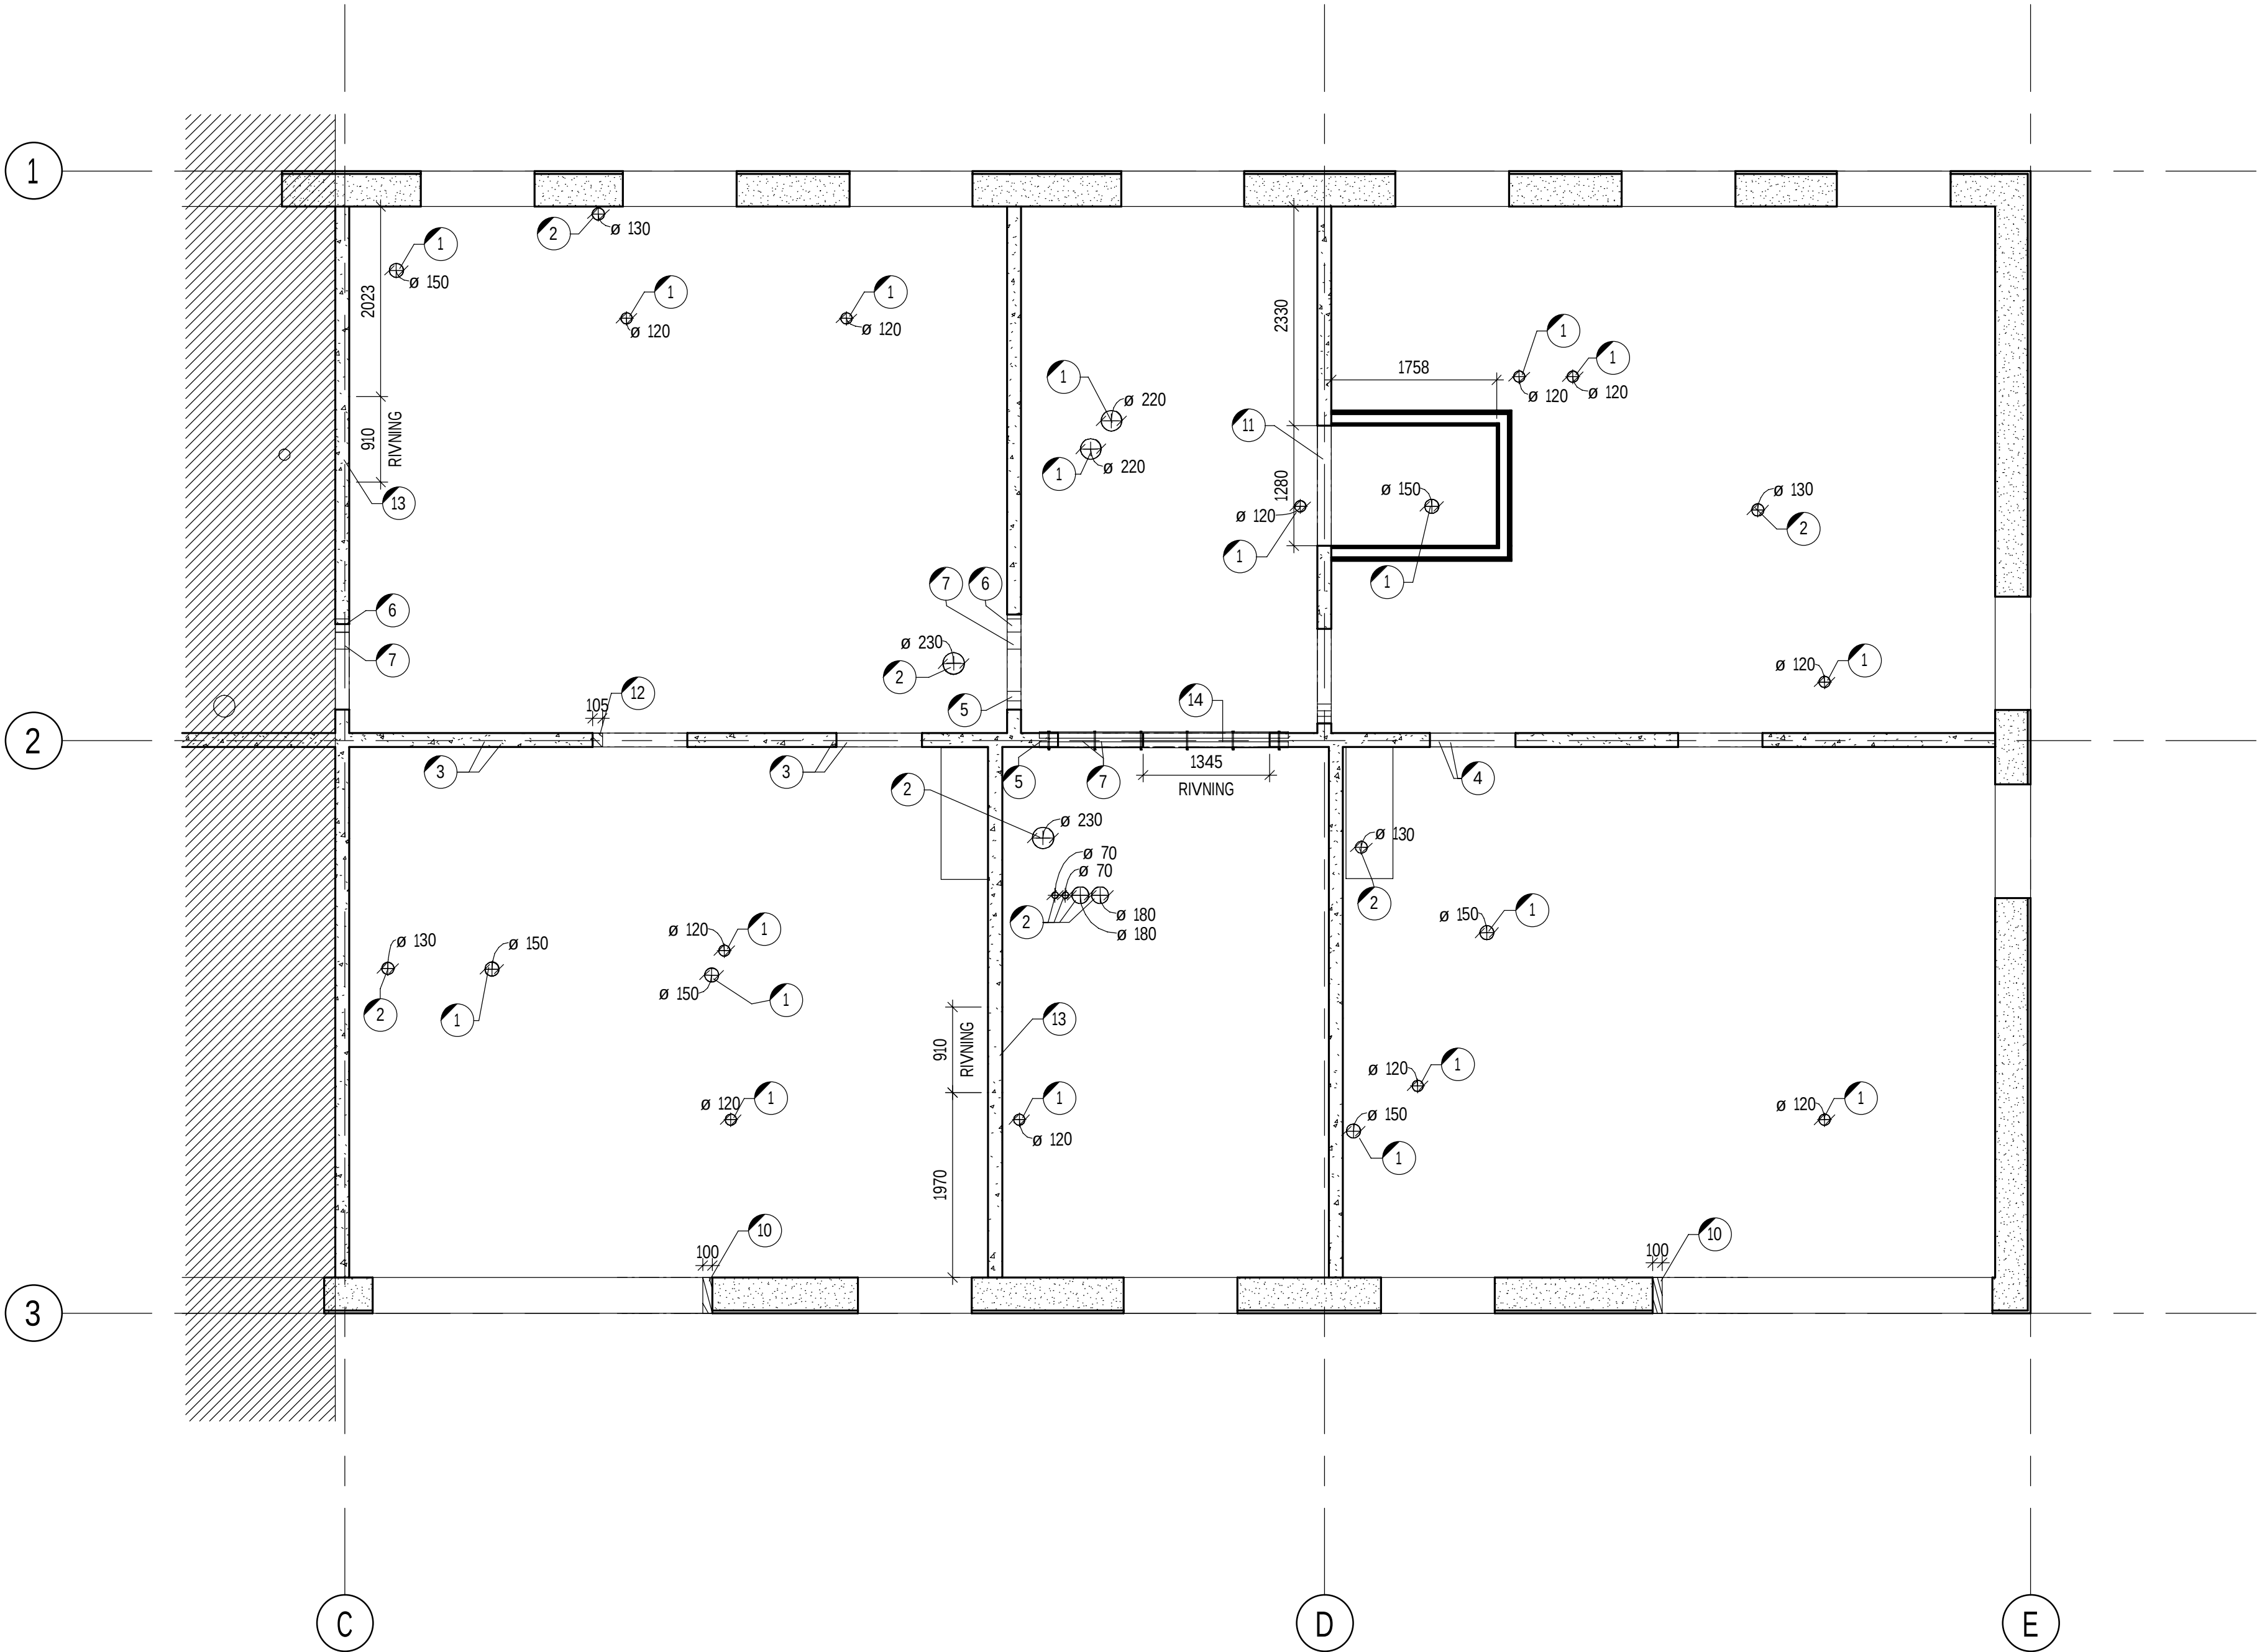

PLAN 2 LÄGENH. - Del 2
1 : 50

SKALA 1:50

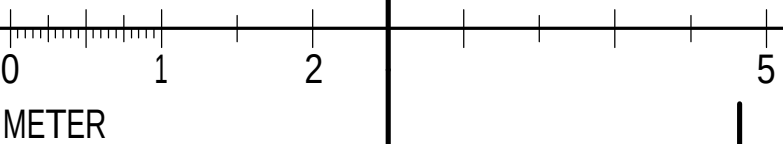

FÖRESKRIFTER

ALLMÄNNA ANVISNINGAR: K-01-1-D001

FÖRKLARINGAR

- 1 = HÅLTAGNING I BJÄLKLAG FÖR VENT
2 = HÅLTAGNING I BJÄLKLAG FÖR VS
3 = HÅLTAGNING I VÄGG VS, ø60. HÖJD ENLIGT VS-HANDLING.
4 = HÅLTAGNING I VÄGG VS, ø70. HÖJD ENLIGT VS-HANDLING.
5 = HÅLTAGNING I VÄGG VS, ø100. HÖJD ENLIGT VS-HANDLING.
6 = HÅLTAGNING I VÄGG VS, ø140. HÖJD ENLIGT VS-HANDLING.
7 = HÅLTAGNING I VÄGG VS, ø180. HÖJD ENLIGT VS-HANDLING.
8 = 2st VENTILATIONSKANALER ø420mm DRAS I BEFINTLIGA SCHAFT. BEFINTLIGA SCHAFT ANTAS VAR IGENGJUTNA RUNT INSTALLATIONER.
9 = 2st VENTILATIONSKANALER 340x440mm DRAS I BEFINTLIGT SCHAFT. BEFINTLIGA SCHAFT ANTAS VAR IGEN GJUTNA RUNT INSTALLATIONER
10 = DÖRRÖPPNING, BALKONG. BREDDAS 100mm
11 = NY DÖRRÖPPNING 1280x2230mm I BEFINTLIG BETONGVÄGG MED TJOCKLEK 150mm.
12 = 105MM BREDDNING AV BEFINTLIG DÖRRÖPPNING
13 = NY DÖRRÖPPNING 910x2110mm I BEFINTLIG BETONGVÄGG MED TJOCKLEK 150mm.
14 = BEF. DÖRRÖPPNING SÅGAS UPP TILL EN STÖRRE ÖPPNING 2110x2295. BETONGVÄGG MED TJOCKLEK 150mm.

MÄTT I HÖJD FÖR HÅLTAGNINGAR I VÄGG ENLIGT RESPEKTIVE VS-, VENT- & EL-HANDLINGAR

HÄNVISNINGAR

GRUNDPLAN:	K-15-1-D090
KÄLLARPLAN - DEL 1:	K-20-1-D091
KÄLLARPLAN - DEL 2:	K-20-1-D092
PLAN 1 - DEL 1:	K-20-1-D101
PLAN 1 - DEL 2:	K-20-1-D102
PLAN 2 - DEL 1:	K-20-1-D201
PLAN 2 - DEL 2:	K-20-1-D202
FLÅKTRUM - DEL 1:	K-20-1-D301
FLÅKTRUM - DEL 2:	K-20-1-D302

1	GODKÄND	2025-02-26	MG
BET	ÄNDRING AVSER	DATUM	SIGN
FÖRFRÅGNINGSUNDERLAG			
BYGGHANDLING			
DATUM	GODKÄND	ÄNDRING	STATUS
2025-02-26	GODKÄND		
CENTRUMHUSET HUS D			
KRÅKAN 1, ROBERTSFORS			
ÄF-Infrastructure AB			
Strandgatan 9A			
891 39 Örnsköldsvik			
Tel: 010-505 00 00			
MARCUS GRANQVIST			
MARCUS GRANQVIST			
ROBIN ÖSTMAN			
D0192211			
RITNINGSKATEGORI			
OMBYGGNAD BIBLIOTEK OCH LÄGENHETER			
BJÄLKLAG ÖVAN LÄGENHETSPLAN			
PLAN 2 - Del 2			
K-20-1-D202			
1			