

FÖRESKRIFTER

ALLMÄNNA ANVISNINGAR: K-01-1-D001

FÖRKLARINGAR


- 1 = HÅLTAGNING I VÄGG FÖR VENT $\varnothing$ 120mm
2 = HÅLTAGNING I VÄGG FÖR VENT $\varnothing$ 150mm
3 = HÅLTAGNING I VÄGG FÖR VENT $\varnothing$ 220mm
4 = HÅLTAGNING I VÄGG FÖR VENT $\varnothing$ 340mm
5 = HÅLTAGNING I VÄGG FÖR VENT $\varnothing$ 420mm
6 = HÅLTAGNING I VÄGG FÖR VENT $\varnothing$ 440mm
7 = HÅLTAGNING I VÄGG FÖR VENT $\varnothing$ 520mm
8 = NY TAKGENOMFÖRING VENT 520x520
KORTLINGAR 45x145 SÄTTS MELLAN BEF.
TAKSTOLAR OCH RUNT OM GENOMFÖRING
9 = NY TAKGENOMFÖRING VENT 520x320.

MÄTT I HÖJD FÖR HÅLTAGNINGAR I VÄGG ENLIGT
RESPEKTIVE VS-, VENT- & EL-HANDLINGAR

HÄNVISNINGAR

PLANER	
GRUNDPLAN:	K-15-1-D090
KÄLLARPLAN -DEL 1:	K-20-1-D091
KÄLLARPLAN - DEL 2:	K-20-1-D092
PLAN 1 - DEL 1:	K-20-1-D101
PLAN 1 - DEL 2:	K-20-1-D102
PLAN 2 - DEL 1:	K-20-1-D201
PLAN 2 - DEL 2:	K-20-1-D202
FLÅKTRUM - DEL 1:	K-20-1-D301
FLÅKTRUM - DEL 2:	K-20-1-D302

1	GODKÄND		2025-02-26	MG
BET	ÄNDRING AVSER		DATUM	SIGN
FÖRFRÅGNINGSUNDERLAG				
BYGGHANDLING				
2025-02-26		GODKÄND		ÄNDRING
CENTRUMHUSET HUS D				
KRÅKAN 1, ROBERTSFORS				
ÄF-Infrastructure AB				ANSVARIG PART
Strandgatan 9A				 AFRY
891 39 Örnsköldsvik				
Tel: 010-505 00 00				
MARCUS GRANQVIST		KONTAKTPERSON	MARCUS GRANQVIST	SKAPAD AV
ROBIN ÖSTMAN		GODKÄND AV	D0192211	UPPRAGSNUMMER
				RITNINGSKATEGORI
ÖMBYGGNAD BIBLIOTEK OCH LÄGENHETER				INNEHÅLL
FLÅKTRUM - Del 1				A1
K-20-1-D301				1:50
NUMBER				BET
1				

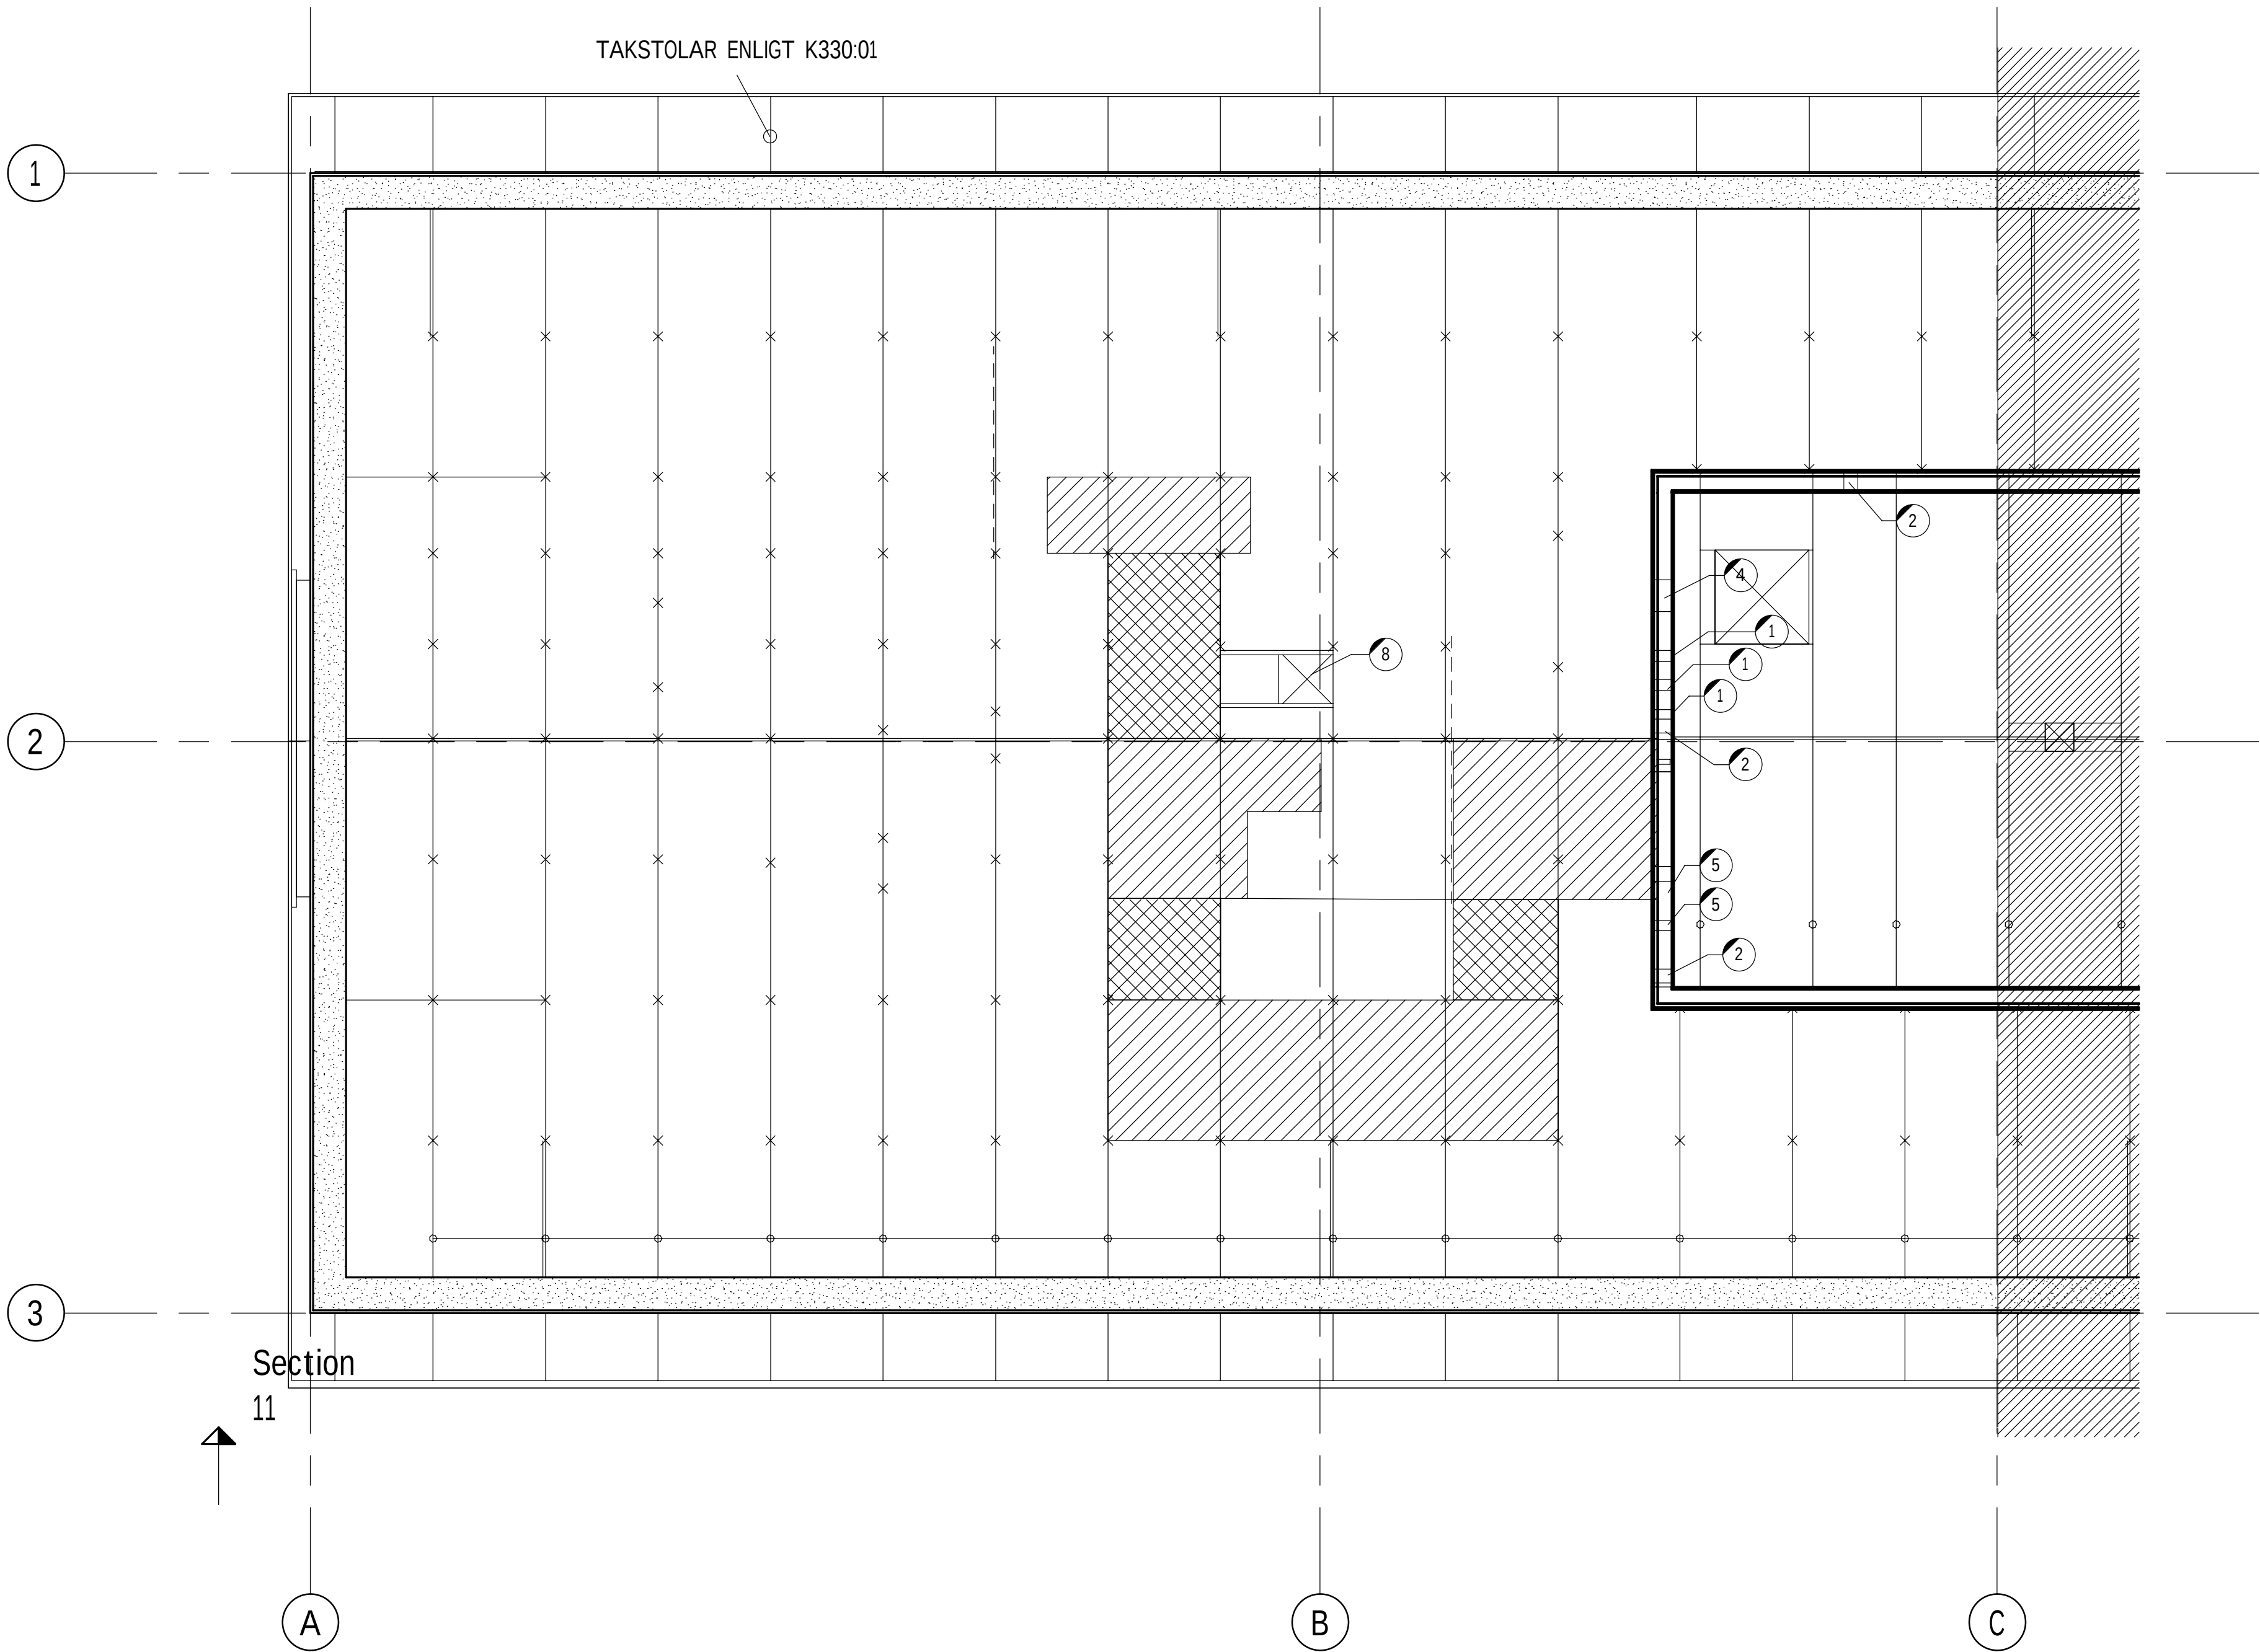

PLAN 3 FLÅKTRUM - Del 1
1 : 50

SKALA 1:50
0 1 2 5
METER