

FÖRESKRIFTER

ALLMÄNNA ANVISNINGAR: K-01-1-D001


FÖRKLARINGAR

- 1 = HÅLTAGNING I VÄGG FÖR VENT $\varnothing$ 120mm
- 2 = HÅLTAGNING I VÄGG FÖR VENT $\varnothing$ 150mm
- 3 = HÅLTAGNING I VÄGG FÖR VENT $\varnothing$ 220mm
- 4 = HÅLTAGNING I VÄGG FÖR VENT $\varnothing$ 340mm
- 5 = HÅLTAGNING I VÄGG FÖR VENT $\varnothing$ 420mm
- 6 = HÅLTAGNING I VÄGG FÖR VENT $\varnothing$ 440mm
- 7 = HÅLTAGNING I VÄGG FÖR VENT $\varnothing$ 520mm
- 8 = NY TAKGENOMFÖRING VENT 520x520
KORTLINGAR 45x145 SÄTTS MELLAN BEF.
TAKSTOLAR OCH RUNT OM GENOMFÖRING
- 9 = NY TAKGENOMFÖRING VENT 520x320.

MÄTT I HÖJD FÖR HÅLTAGNINGAR I VÄGG ENLIGT
RESPEKTIVE VS-, VENT- & EL-HANDLINGAR


HÄNVISNINGAR

PLANER	
GRUNDPLAN:	K-15-1-D090
KÄLLARPLAN -DEL 1:	K-20-1-D091
KÄLLARPLAN - DEL 2:	K-20-1-D092
PLAN 1 - DEL 1:	K-20-1-D101
PLAN 1 - DEL 2:	K-20-1-D102
PLAN 2 - DEL 1:	K-20-1-D201
PLAN 2 - DEL 2:	K-20-1-D202
FLÅKTRUM - DEL 1:	K-20-1-D301
FLÅKTRUM - DEL 2:	K-20-1-D302

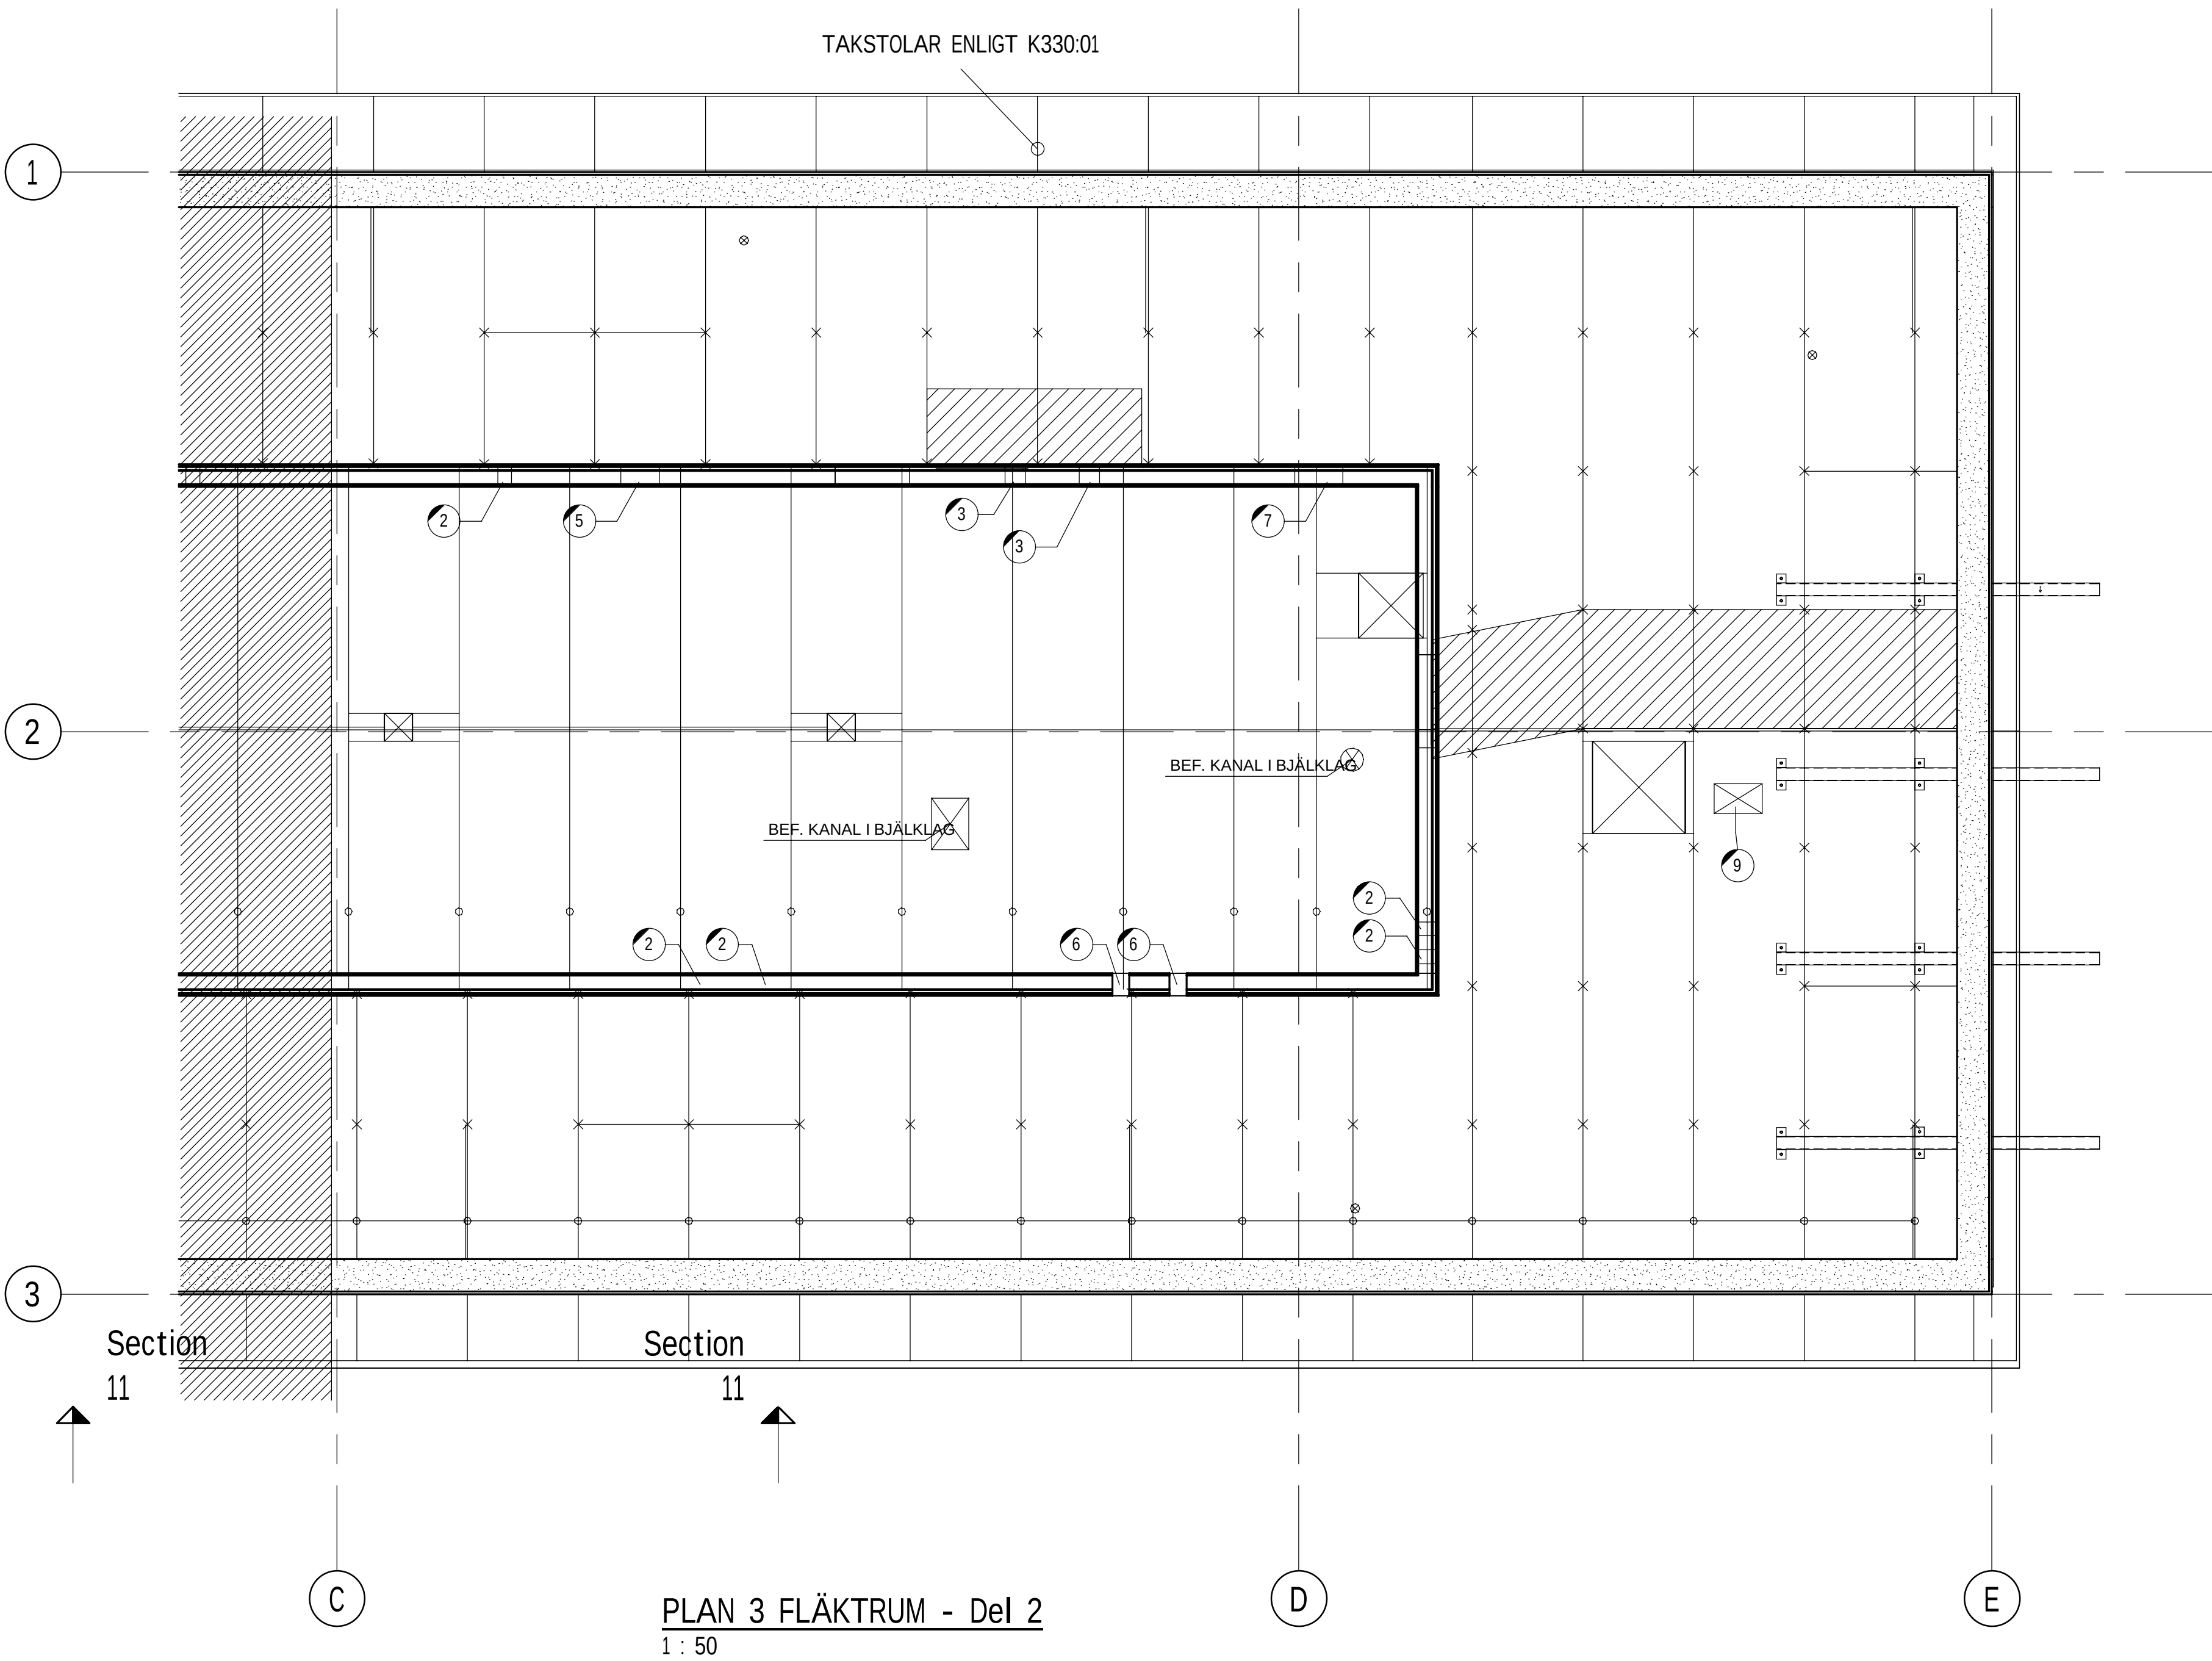

PLAN 3 FLÅKTRUM - Del 2
1 : 50

SKALA 1:50

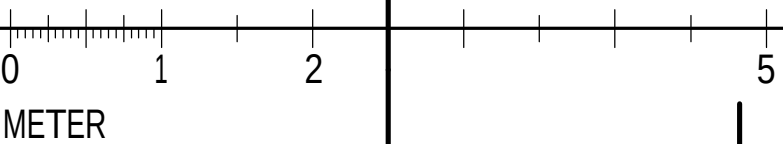

1	GODKÄND	2025-02-26	MG
BET	ÄNDRING AVSER	DATUM	SIGN
FÖRFRÅGNINGSUNDERLAG			
BYGGHANDLING			
2025-02-26	GODKÄND	ÄNDRING	STATUS
CENTRUMHUSET HUS D KRÅKAN 1, ROBERTSFORS			
ÄF-Infrastructure AB Strandgatan 9A			
891 39 Örnsköldsvik MARCUS GRANQVIST			
MARCUS GRANQVIST			
ROBIN ÖSTMAN			
D0192211			
OMBYGGNAD BIBLIOTEK OCH LÄGENHETER TAK OVAN BJÄLKLAG FLÅKTRUM - Del 2			
K-20-1-D302			