


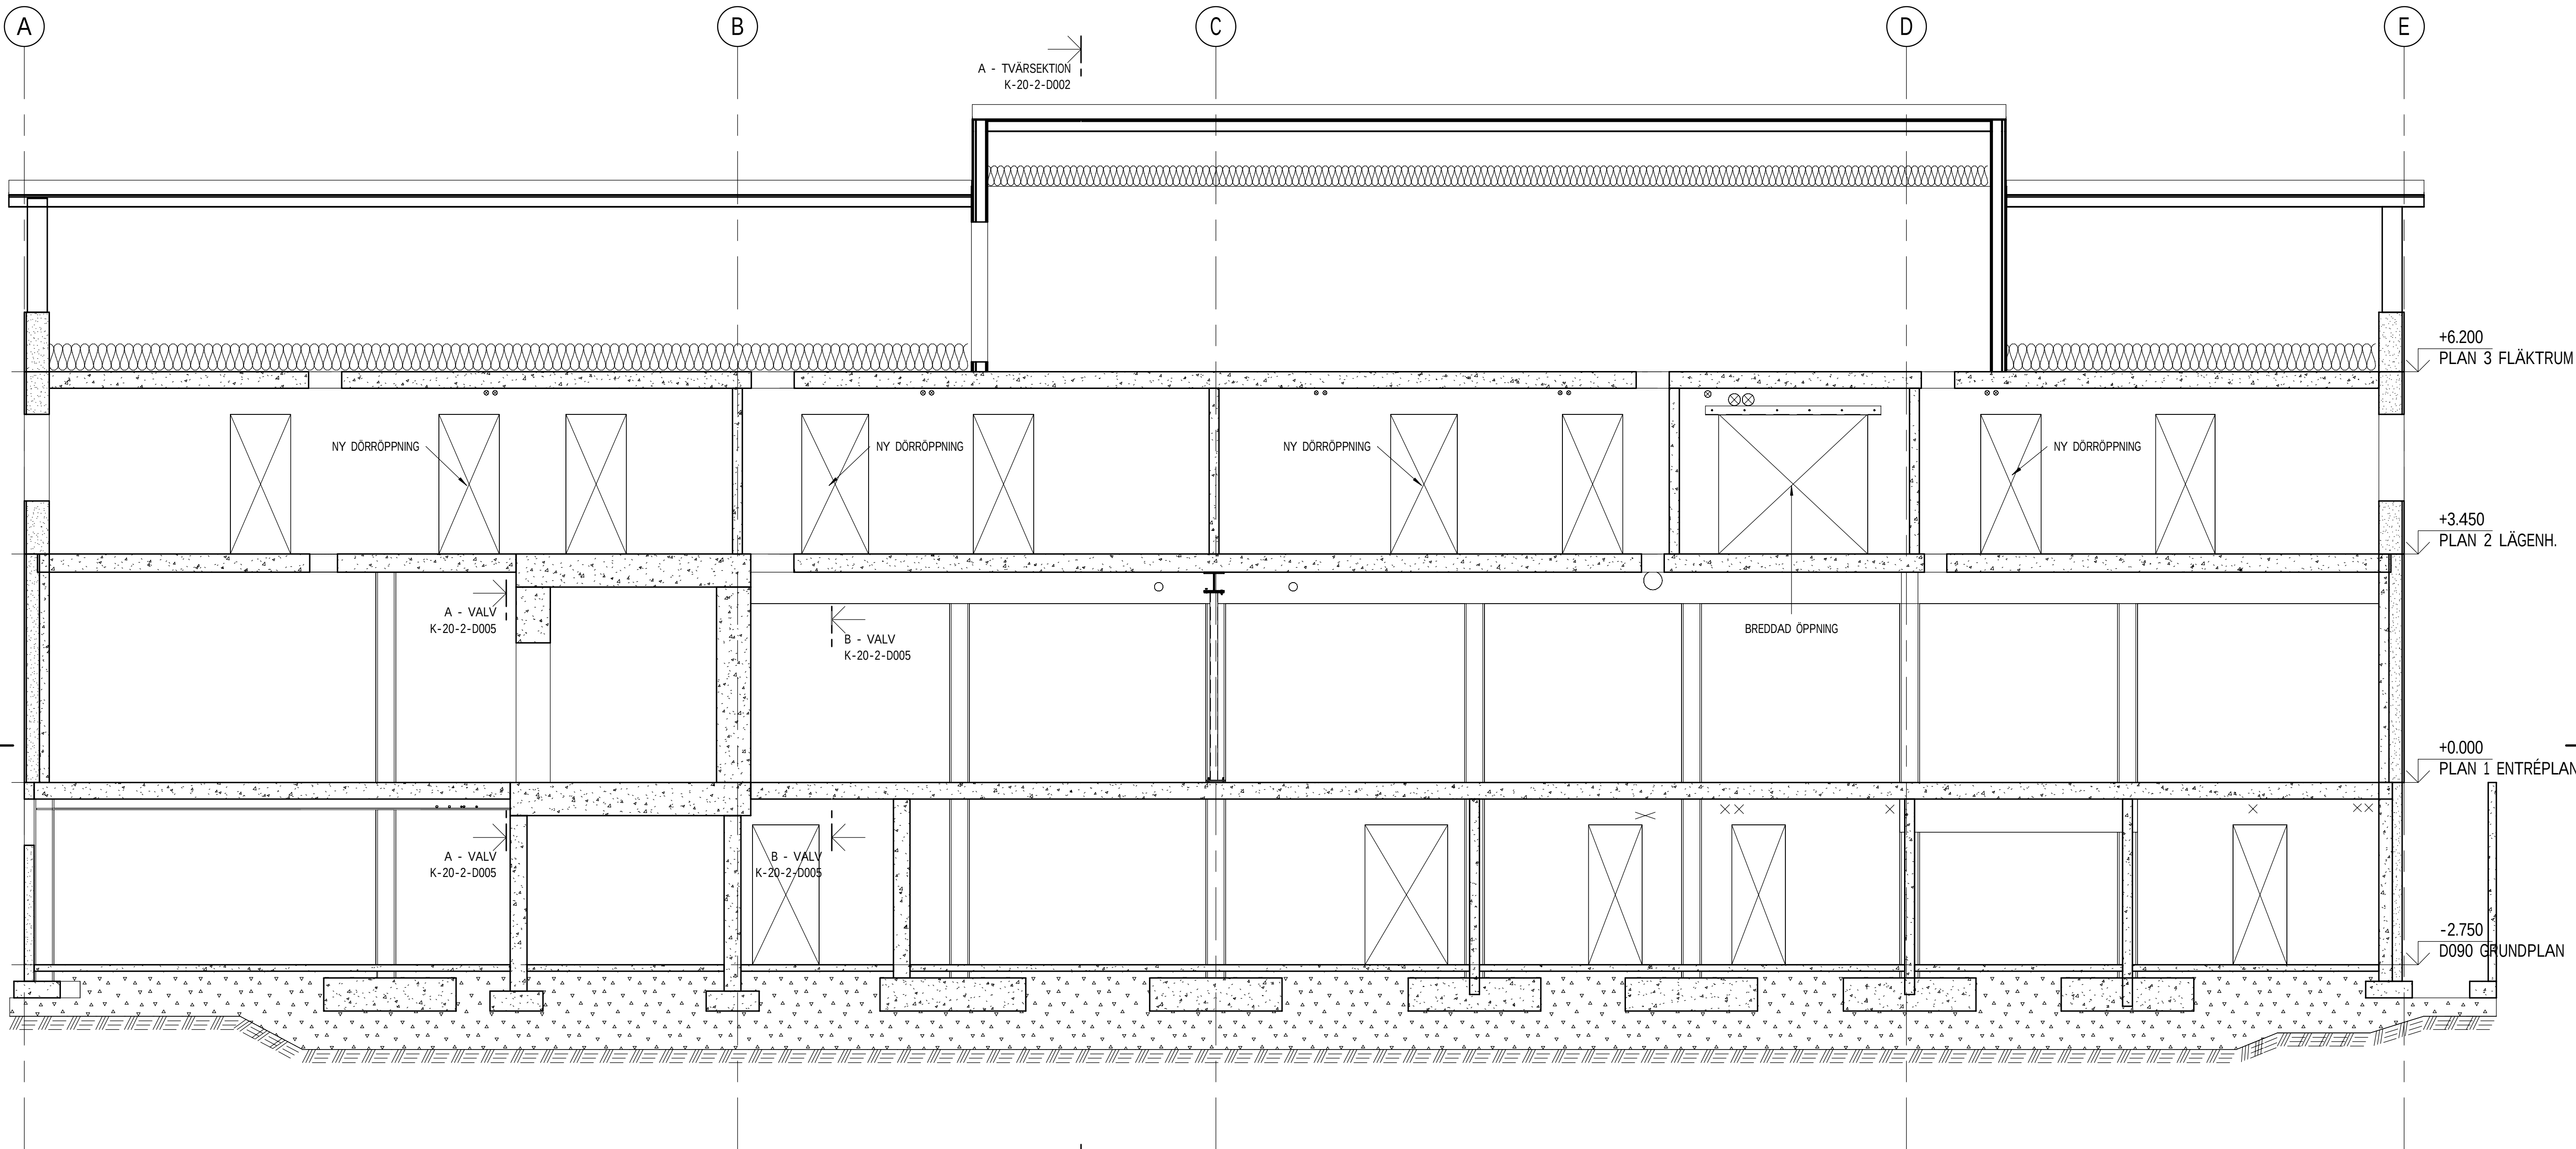

A - LÄNGDSEKTION  
1 : 50

A - TVÄRSEKTION  
K-20-2-D002

#### FÖRESKRIFTER

ALLMÄNNA ANVISNINGAR: K-01-1-D001

#### FÖRKLARINGAR

#### HÄNVISNINGAR

- PLANER**  
GRUNDPLAN: K-15-1-D090  
KÄLLARPLAN - DEL 1: K-20-1-D091  
KÄLLARPLAN - DEL 2: K-20-1-D092  
PLAN 1 - DEL 1: K-20-1-D101  
PLAN 1 - DEL 2: K-20-1-D102  
PLAN 2 - DEL 1: K-20-1-D201  
PLAN 2 - DEL 2: K-20-1-D202  
FLÄKTRUM - DEL 1: K-20-1-D301  
FLÄKTRUM - DEL 2: K-20-1-D302

|                                    |               |            |         |
|------------------------------------|---------------|------------|---------|
| 1                                  | GODKÄND       | 2025-02-26 | MG      |
| BET                                | ÄNDRING AVSER | DATUM      | SIGN    |
| FÖRFRÅGNINGSUNDERLAG               |               |            |         |
| BYGGHANDLING                       |               |            |         |
| DATUM                              | GODKÄND       | ÄNDRING    | PROJEKT |
| 2025-02-26                         | GODKÄND       |            |         |
| CENTRUMHUSET HUS D                 |               |            |         |
| KRÅKAN 1, ROBERTSFORS              |               |            |         |
| ANSVARIG PART                      |               |            |         |
| ÅF-Infrastructure AB               |               |            |         |
| Strandgatan 9A                     |               |            |         |
| 891 39 Örnsköldsvik                |               |            |         |
| Tel: 010-505 00 00                 |               |            |         |
| MARCUS GRANQVIST                   |               |            |         |
| JOEL OLOFSSON                      |               |            |         |
| ROBIN ÖSTMAN                       |               |            |         |
| D0192211                           |               |            |         |
| RITNINGSKATEGORI                   |               |            |         |
| OMBYGGNAD BIBLIOTEK OCH LÄGENHETER |               |            |         |
| A1                                 |               |            |         |
| LÄNGDSEKTION                       |               |            |         |
| 1:50                               |               |            |         |
| K-20-2-D001                        |               |            |         |
| 1                                  |               |            |         |

SKALA 1:50  
0 1 2 5  
METER