


FÖRESKRIFTER

ALLMÄNNA ANVISNINGAR: K-01-1-D001

FÖRKLARINGAR

HÄNVISNINGAR

PLANER	
GRUNDPLAN:	K-15-1-D090
KÄLLARPLAN -DEL 1:	K-20-1-D091
KÄLLARPLAN - DEL 2:	K-20-1-D092
PLAN 1 - DEL 1:	K-20-1-D101
PLAN 1 - DEL 2:	K-20-1-D102
PLAN 2 - DEL 1:	K-20-1-D201
PLAN 2 - DEL 2:	K-20-1-D202
FLÅKTRUM - DEL 1:	K-20-1-D301
FLÅKTRUM - DEL 2:	K-20-1-D302

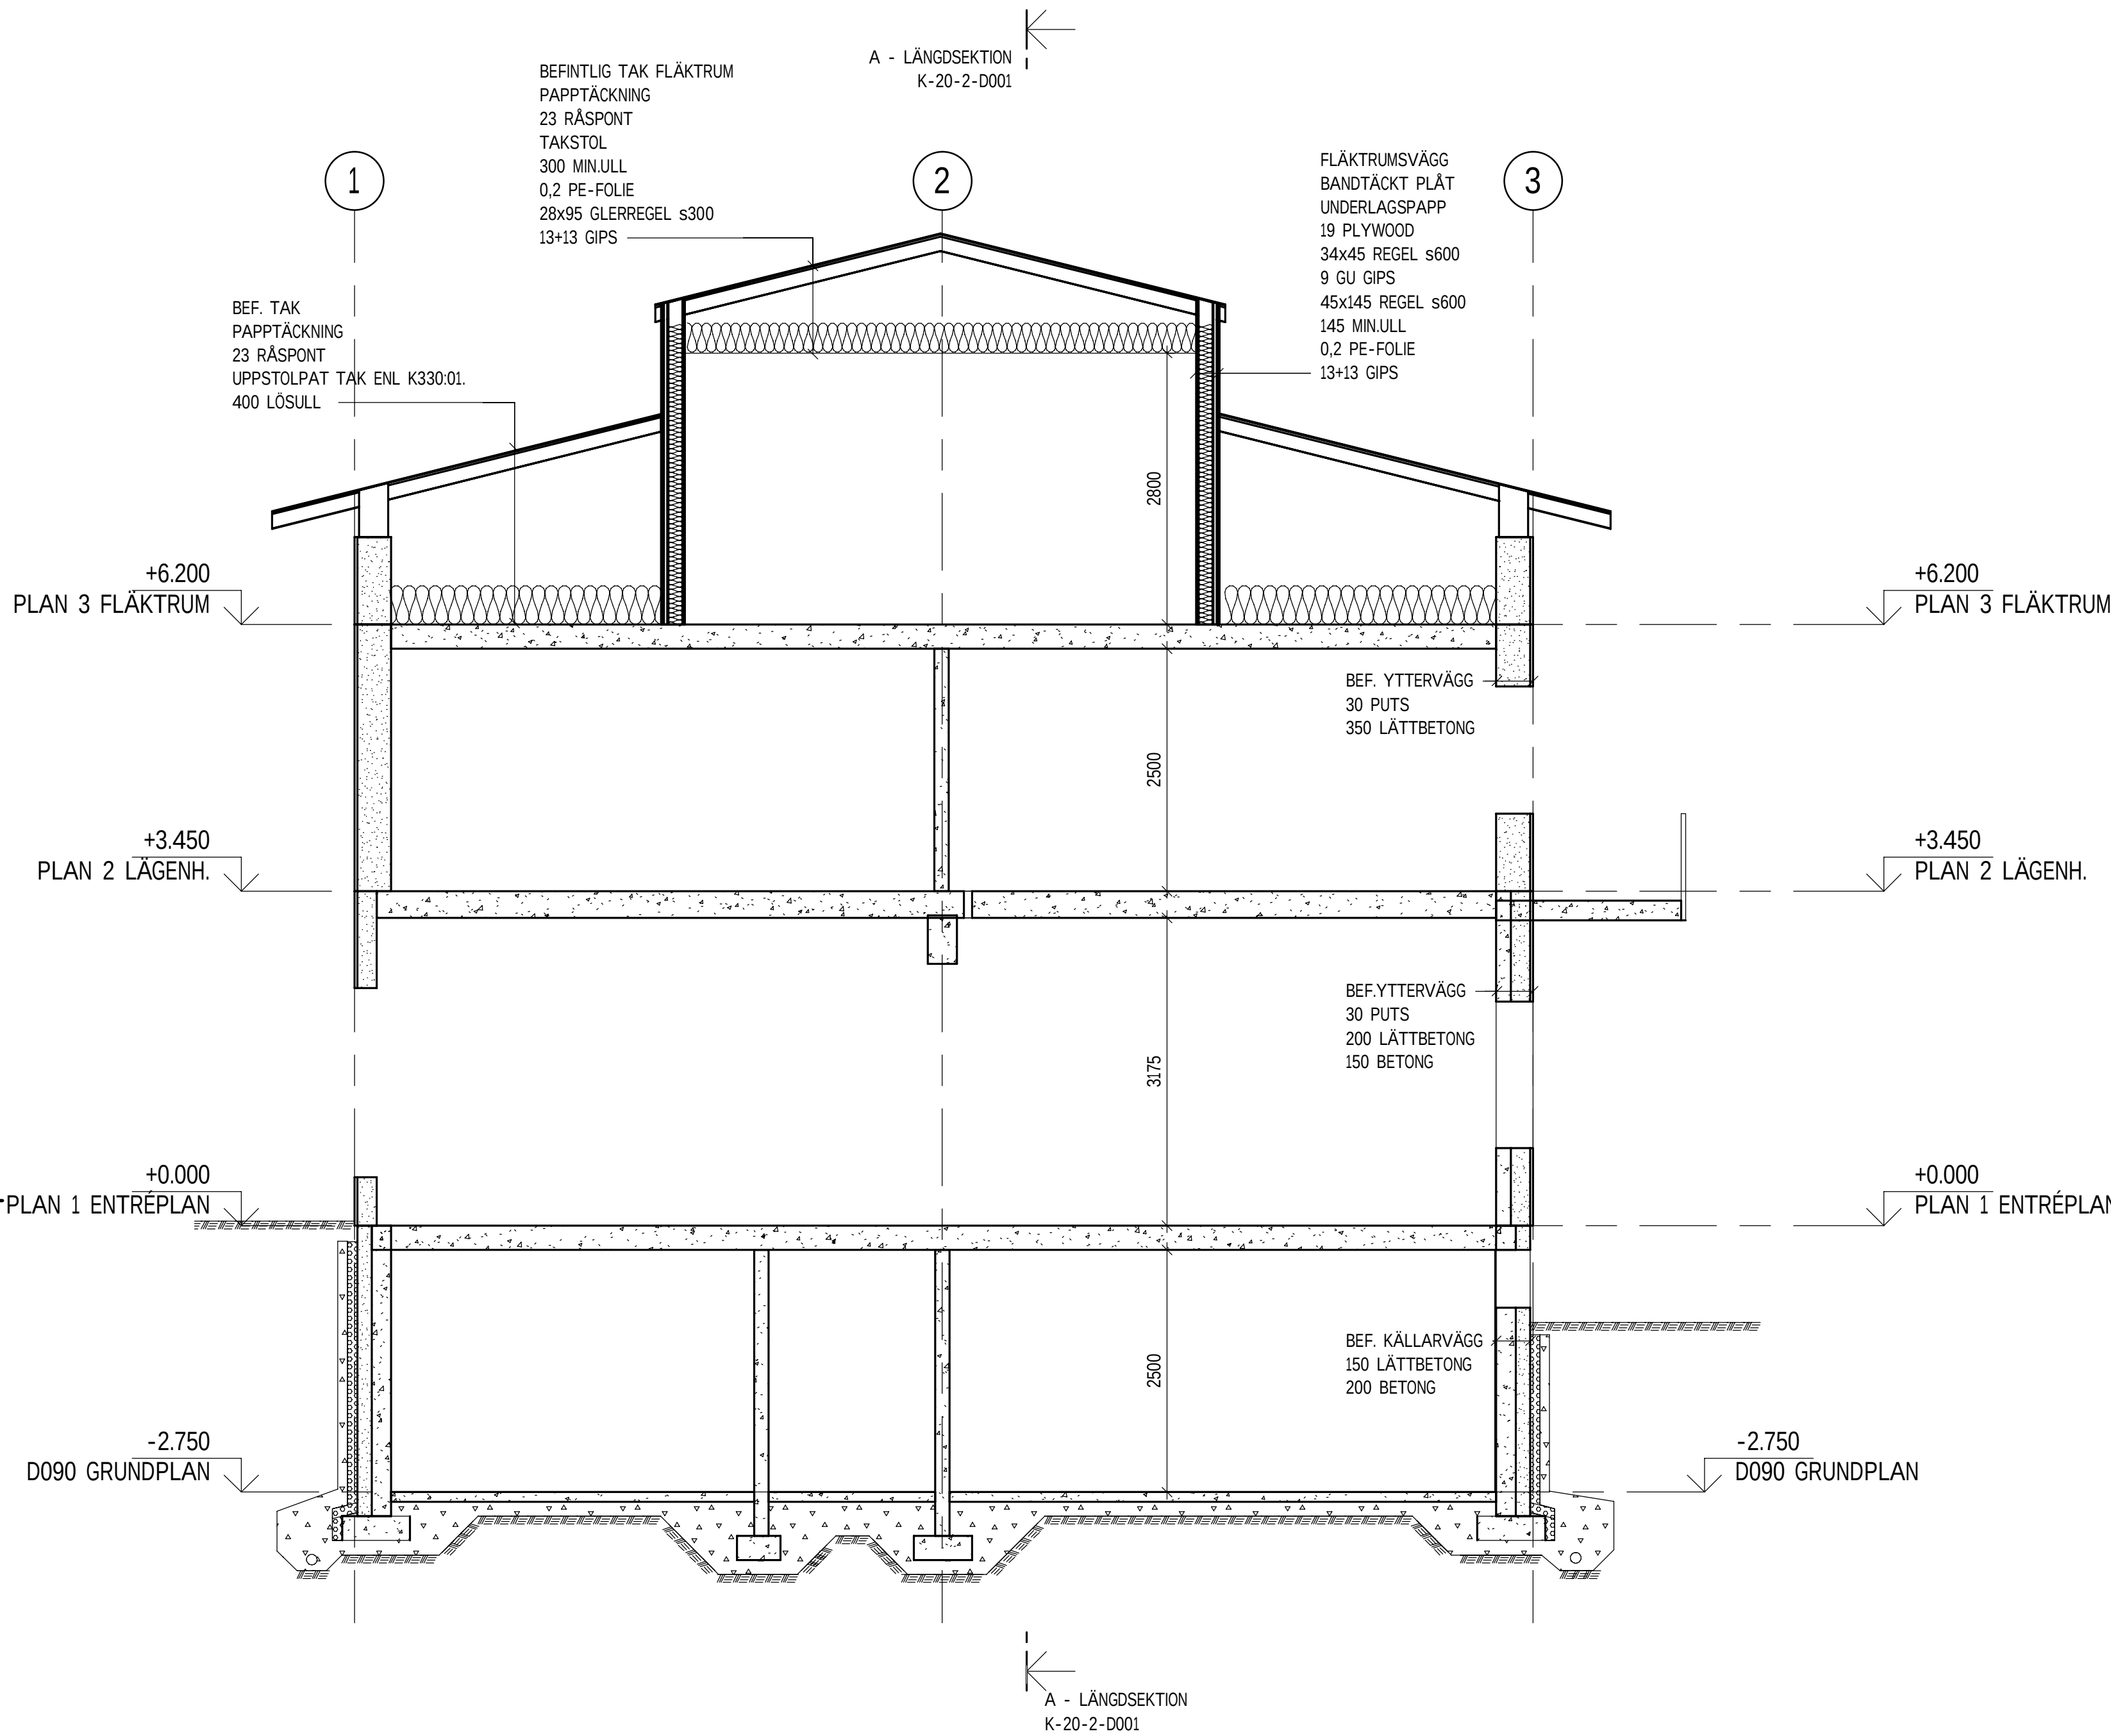

A - TVÄRSEKTION

1 : 50

SKALA 1:1

0 10 20
MILLIMETER

50

100

1	GODKÄND	2025-02-26	MG
BET	ÄNDRING AVSER	DATUM	SIGN
FÖRFRÅGNINGSUNDERLAG			
BYGGHANDLING			
2025-02-26	GODKÄND	ÄNDRING	STATUS
CENTRUMHUSET HUS D KRÅKAN 1, ROBERTSFORS			
ÄF-Infrastructure AB Strandgatan 9A			
891 39 Örnsköldsvik MARCUS GRANQVIST			
991 39 Örnsköldsvik MARCUS GRANQVIST			
ROBIN ÖSTMAN			
JOEL OLOFSSON			
D0192211			
OMBYGGNAD BIBLIOTEK OCH LÄGENHETER			
TVÄRSEKTION			
K-20-2-D002			
A1			
1:50			
1			