



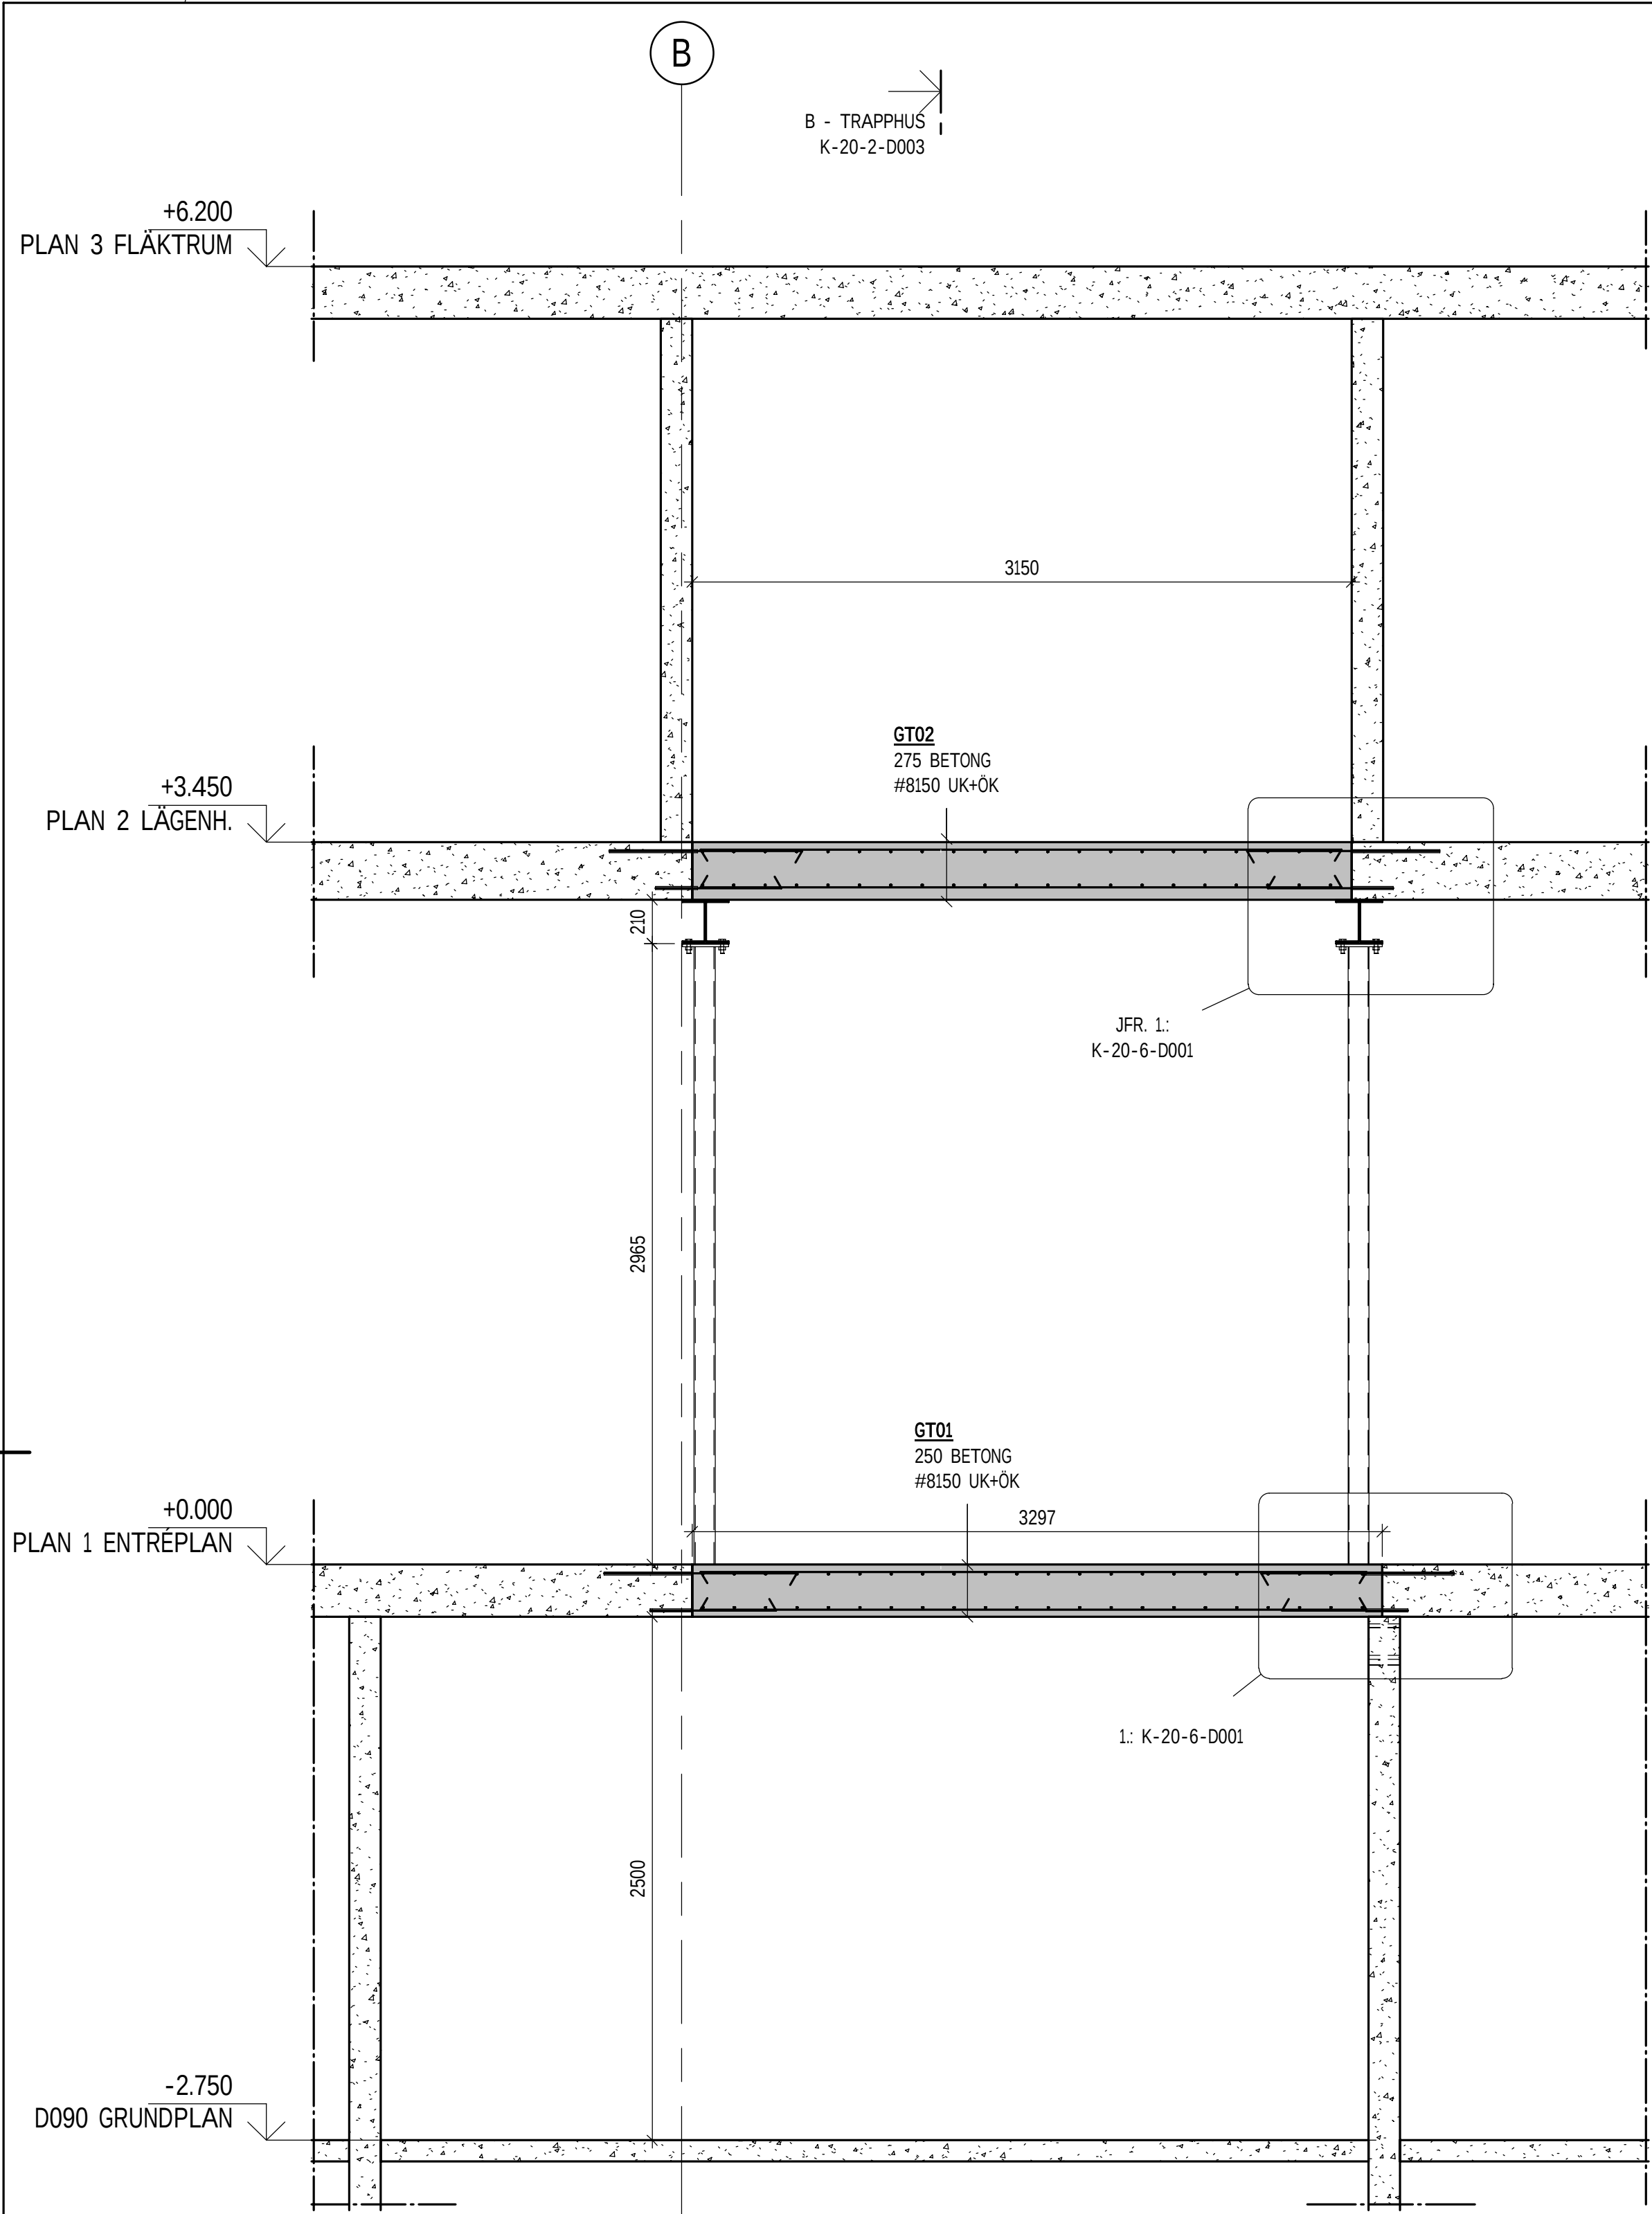

A-A
1 : 25

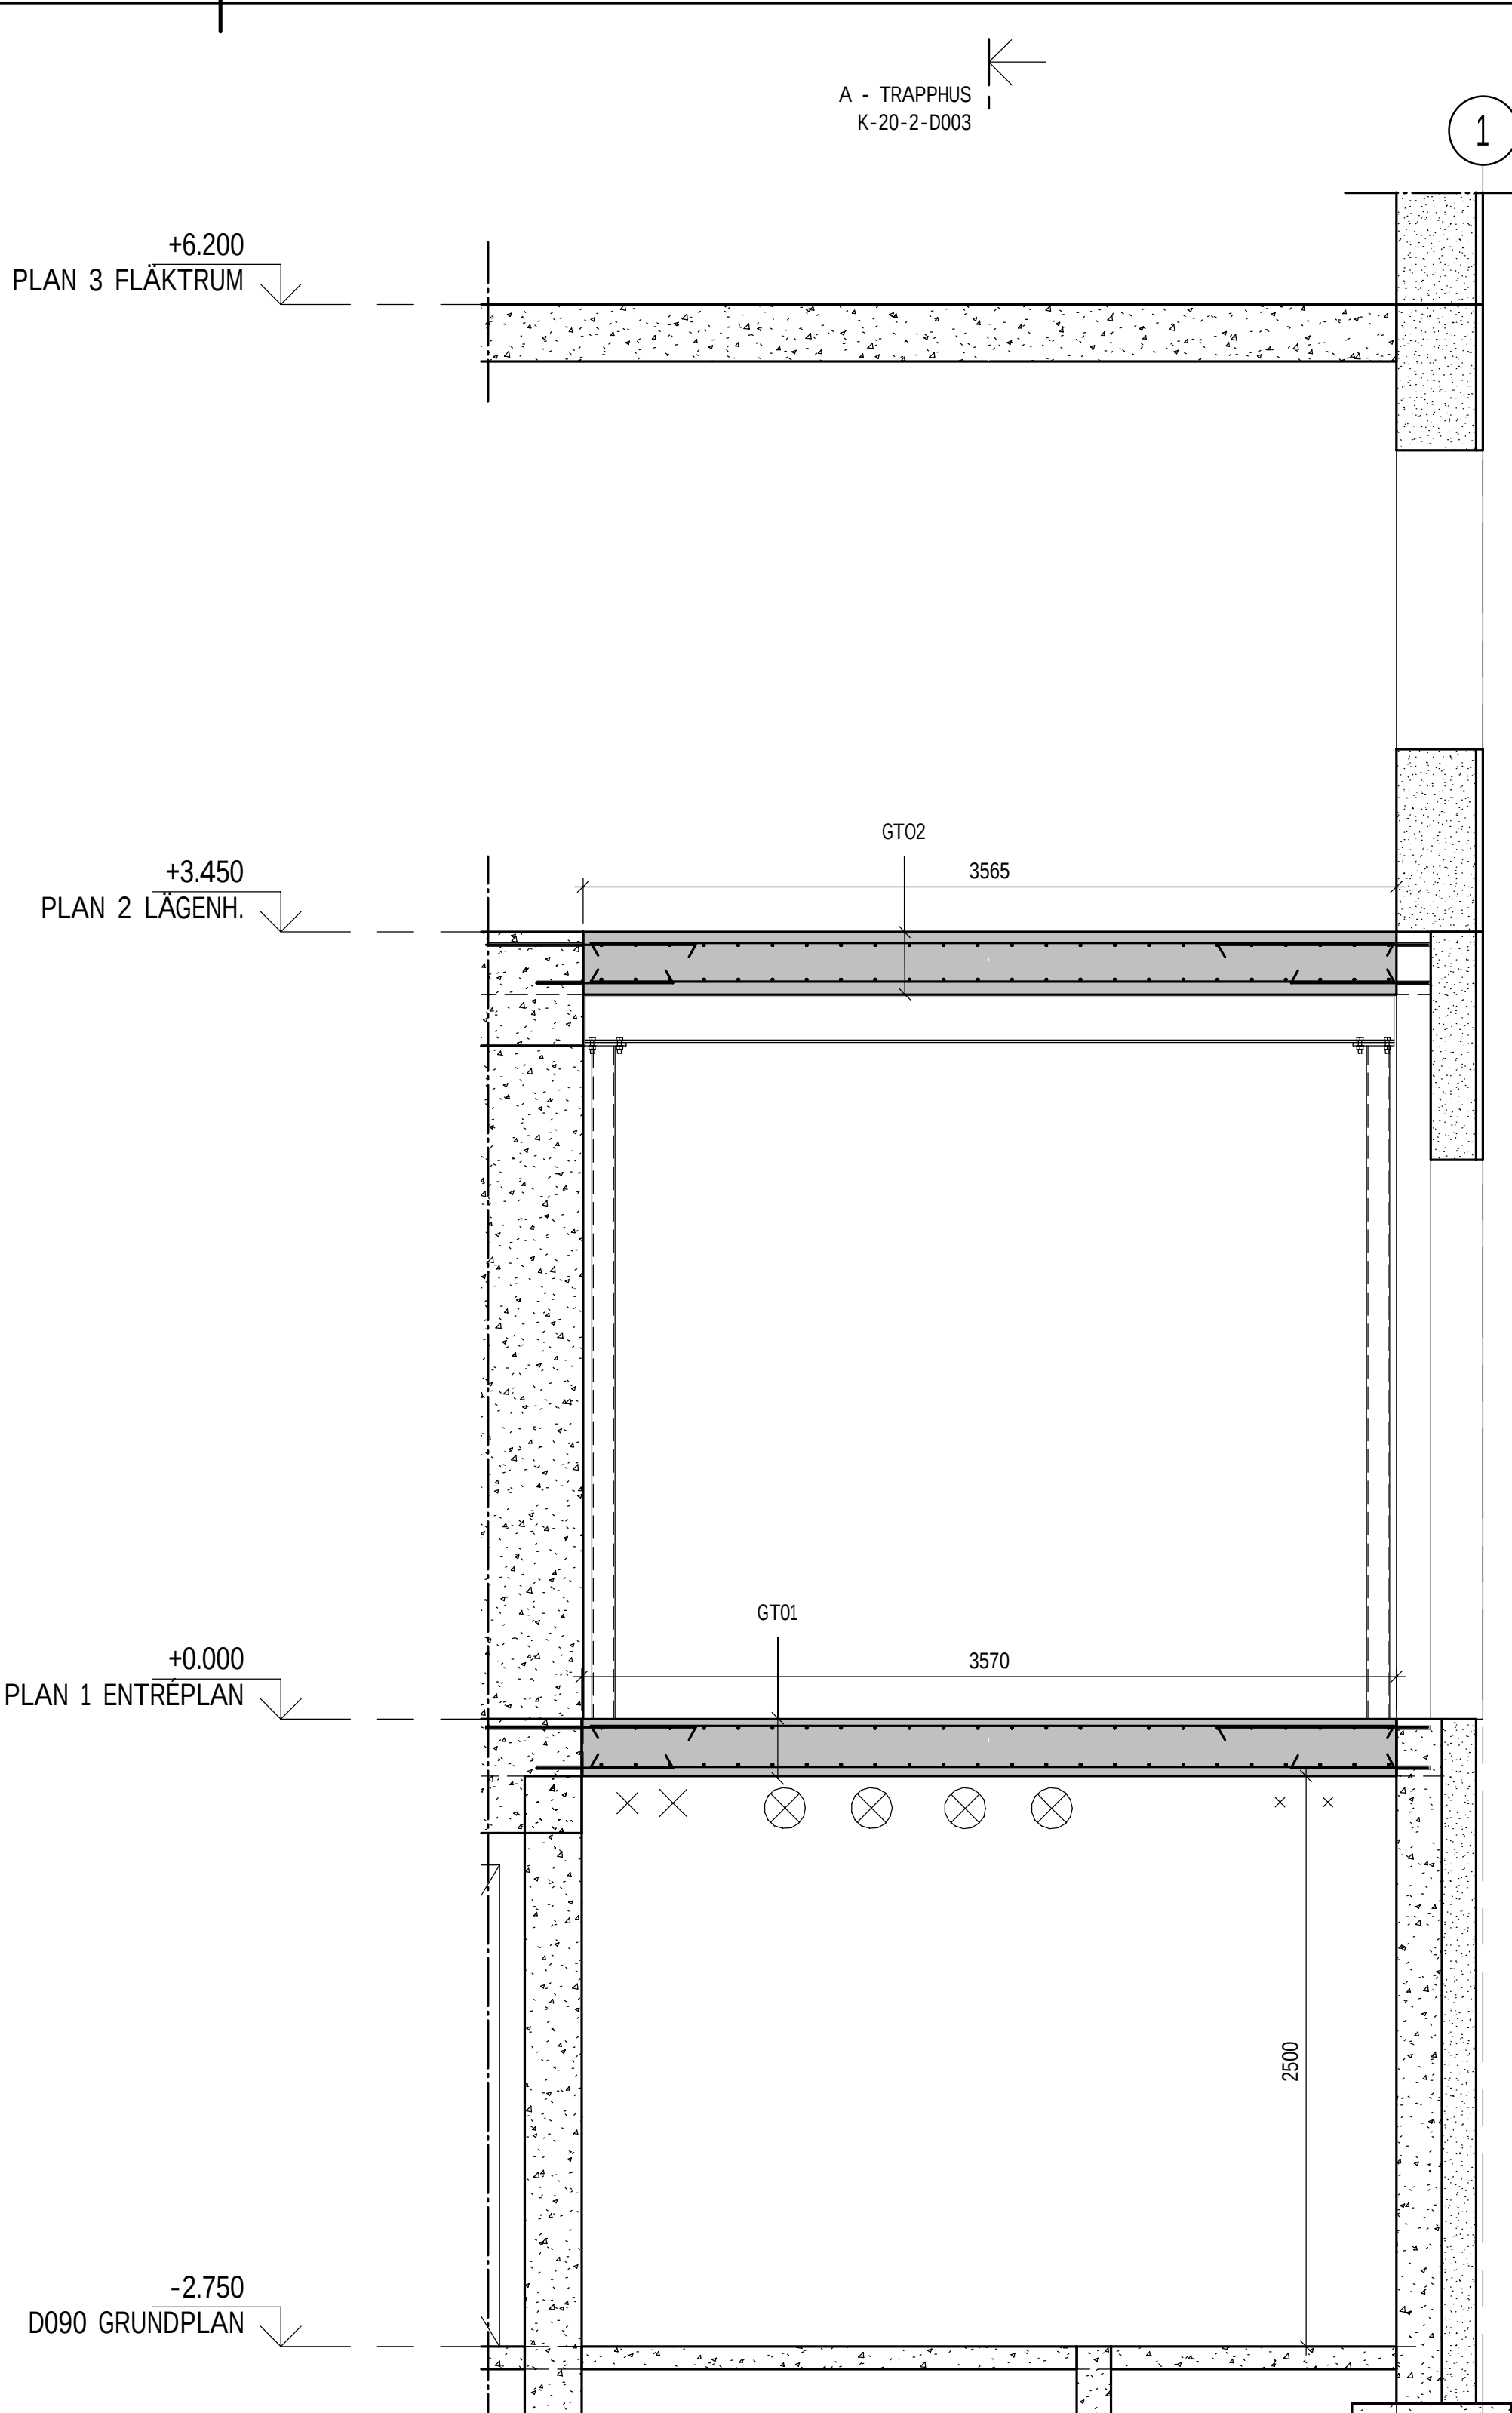

B-B
1 : 25

ARBETSORDNING, MONTERING AV NYTT STÅL TRAPPHUS

- RIVNING AV BEFINTLIG TRAPP, OCH TRAPPPLAN. TILL TRAPPHUS VÄGGAR.
- STÄMPNING MED BÄRLINA MONTERAS PÅ BÅDA SIDOR OM TRAPPHUS. OCH UNDER BETONGBJÄLKLAG. BÅDA VÅNINGAR.
- RIVNING AV BETONGVÄGGAR
- UPPBYGGNAD AV NYTT BETONGBJÄLKLAG PLAN 1
- MONTERING AV NYA STÅL
- UPPBYGGNAD AV NYTT BETONGBJÄLKLAG PLAN 2

STÅL BRANDSKYDDAS FÖR BRANDEKTEKNIK KLASS R30.

VKR-PELARE BRANDSKYDDSMÅLAS MED ELD OCH VATTEN CON-RFB DFT 381μ

HEA-BALK BRANDSKYDDSMÅLAS MED ELD OCH VATTEN CON-RFB DFT 292μ

SKALA 1:25

0 0,5 1
METER

2,5

FÖRESKRIFTER

ALLMÄNNA ANVISNINGAR K-01-1-D001

FÖRKLARINGAR

	BEFINTLIG BETONG
	PLATSGJUTEN BETONG
	BEFINTLIG LÄTTBETONG
	DRÄNERANDE PÖRDRÄN
	CELLPLAST EPS
	CELLPLAST XPS

HÄNVISNINGAR

ARMERINGSPLAN: K-22-1-D001

1	GODKÄND	2025-02-26	MG
BET	ÄNDRING AVSER	DATUM	SIGN
FÖRFRÅGNINGSUNDERLAG			
BYGGHANDLING			
2025-02-26	GODKÄND	ÄNDRING	STATUS
CENTRUMHUSET HUS D			
KRÅKAN 1, ROBERTSFORS			
ÄF-Infrastructure AB			
Strandgatan 9A			
891 39 Örnsköldsvik			
Tel: 010-505 00 00			
MARCUS GRANQVIST	KONTAKTPERSON	MARCUS GRANQVIST	SKAPAD AV
ROBIN ÖSTMAN	GODKÄND AV	D0192211	UPPRAGSNUMMER
RITNINGSKATEGORI			
OMBYGGNAD BIBLIOTEK OCH LÄGENHETER			
TRAPPHUS			
K-20-2-D003			
1			