



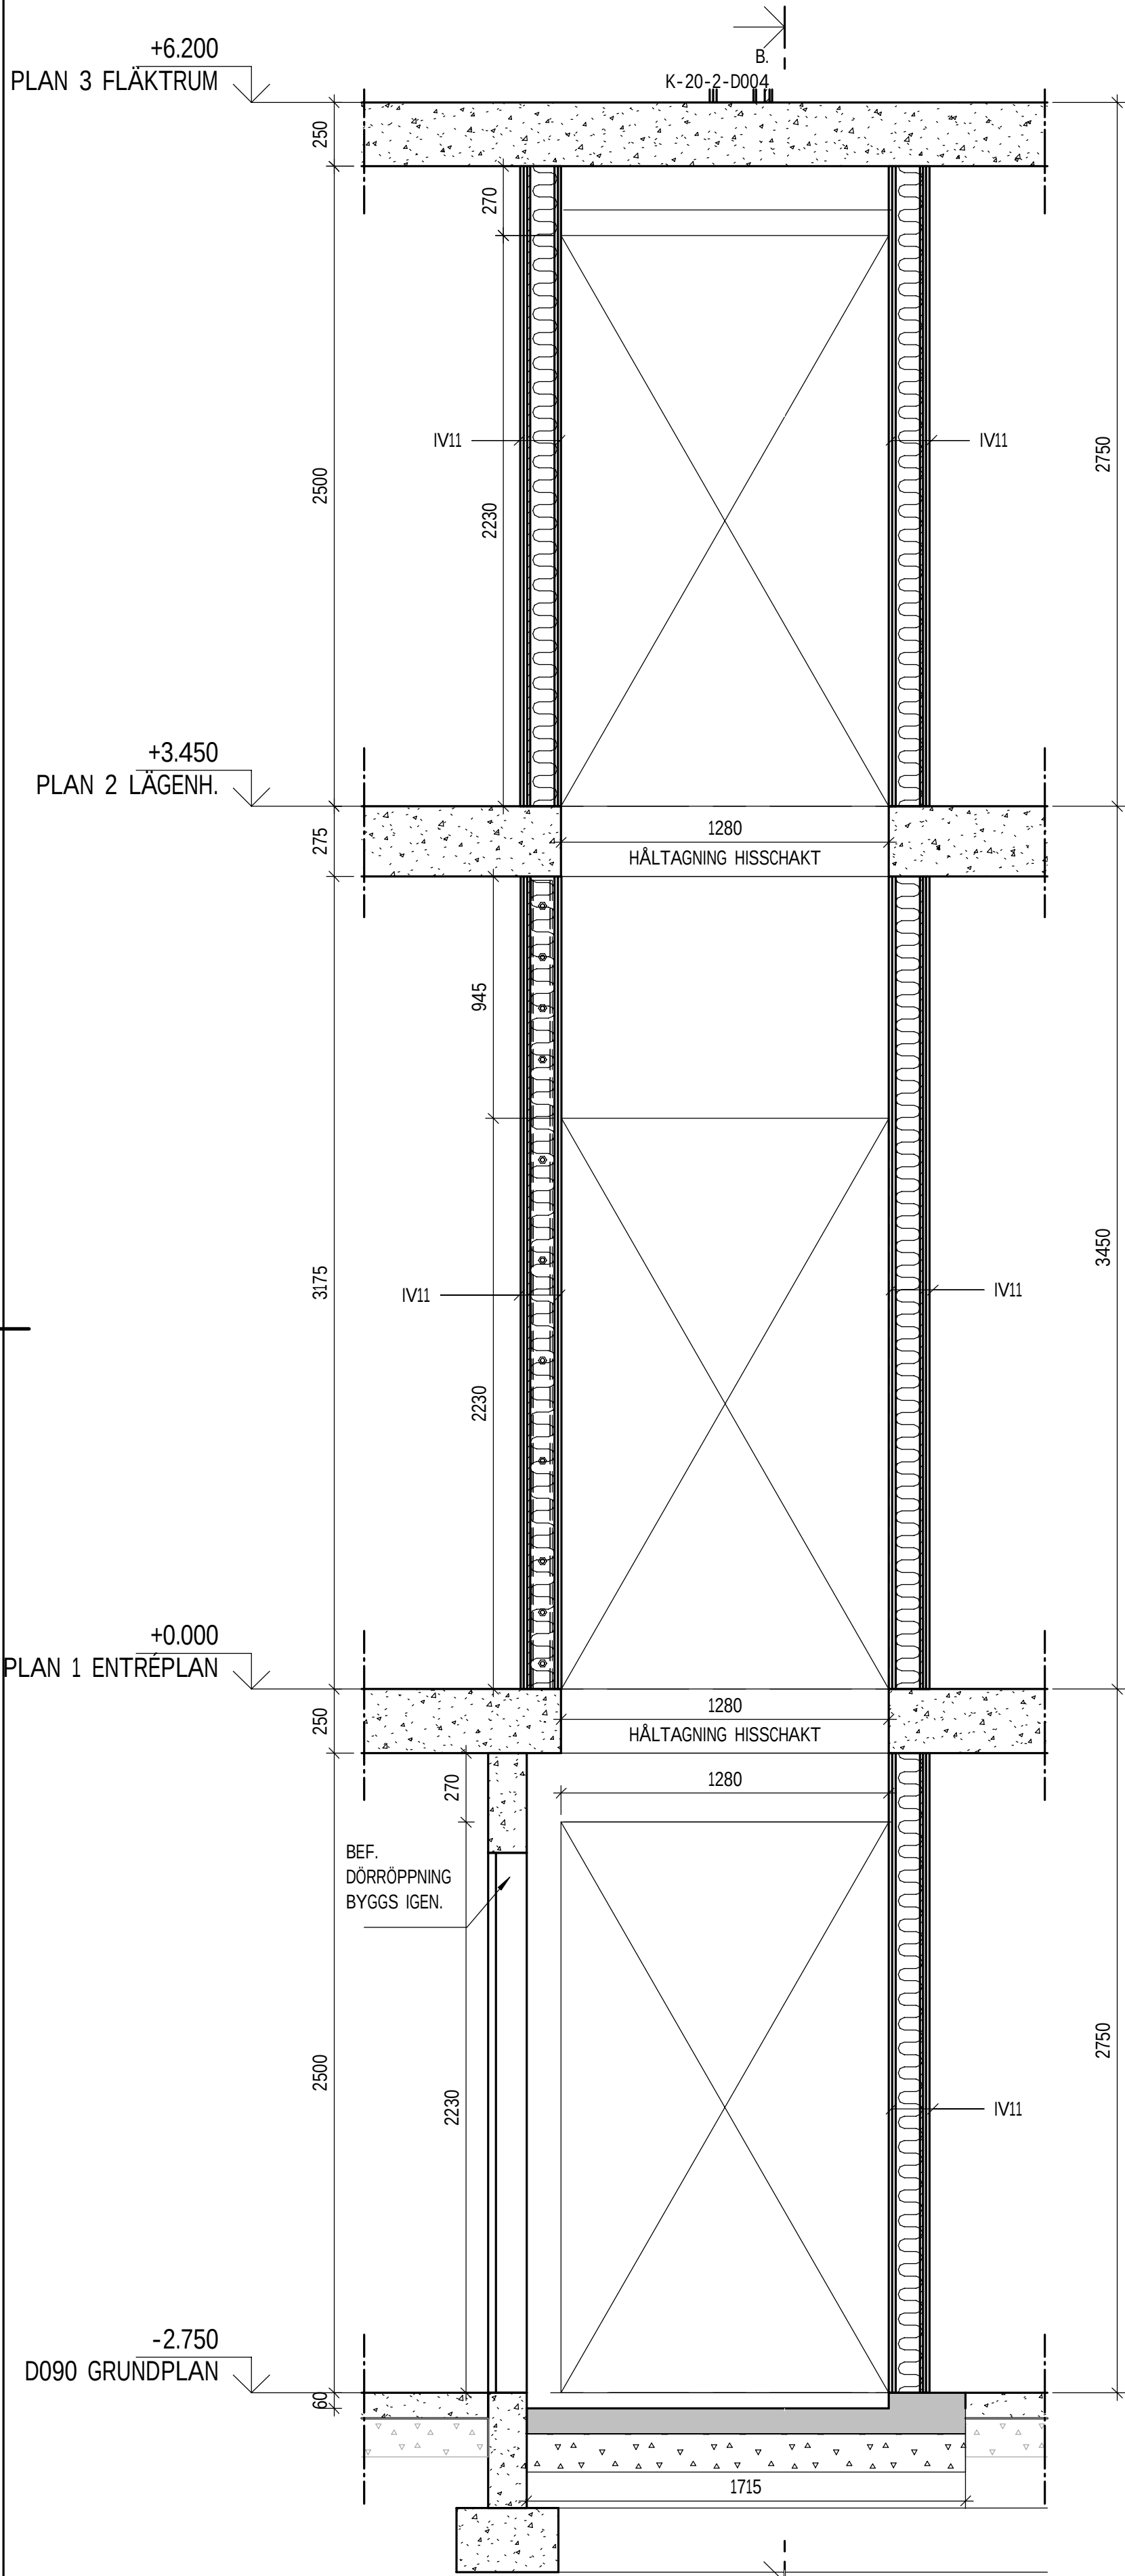

A-A
1 : 20

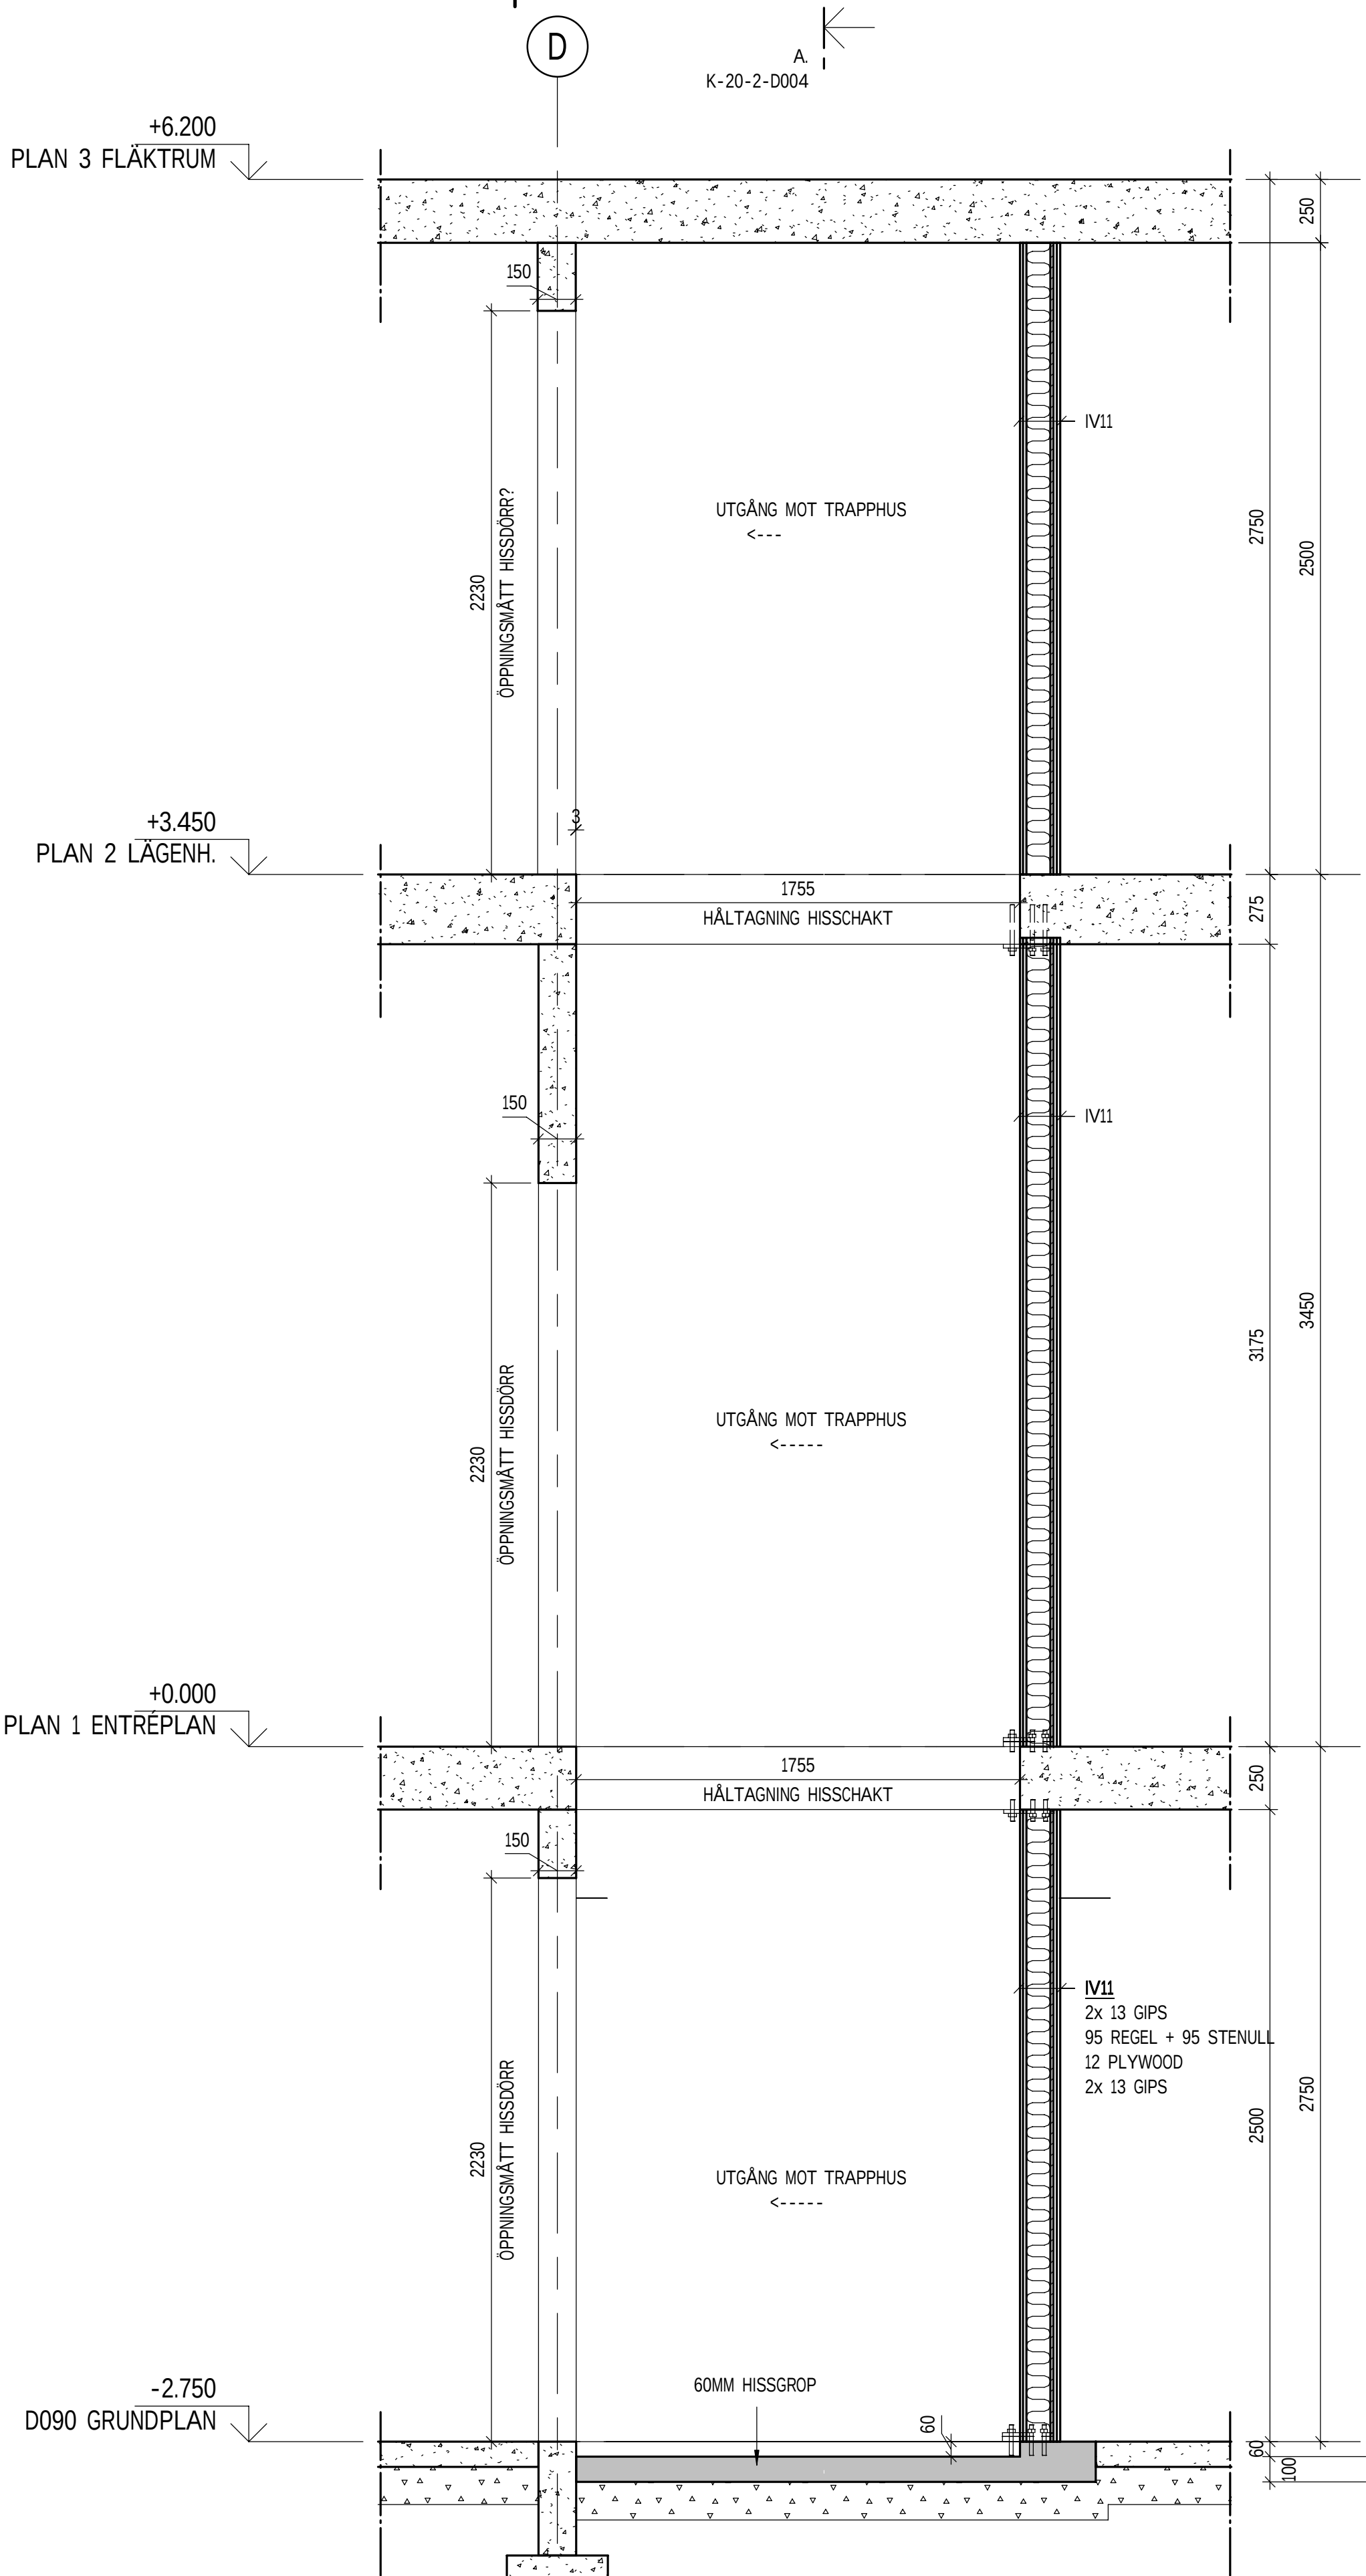

B-B
1 : 20

SKALA 1:1

0 10 20
MILLIMETER

50

100

FÖRESKRIFTER

ALLMÄNNA ANVISNINGAR: K-01-1-D001

FÖRKLARINGAR

HÄNVISNINGAR

PLANER

GRUNDPLAN:	K-15-1-D090
KÄLLARPLAN -DEL 1:	K-20-1-D091
KÄLLARPLAN - DEL 2:	K-20-1-D092
PLAN 1 - DEL 1:	K-20-1-D101
PLAN 1 - DEL 2:	K-20-1-D102
PLAN 2 - DEL 1:	K-20-1-D201
PLAN 2 - DEL 2:	K-20-1-D202
FLÅKTRUM - DEL 1:	K-20-1-D301
FLÅKTRUM - DEL 2:	K-20-1-D302

1	GODKÄND	2025-02-26	MG
BET	ÄNDRING AVSER	DATUM	SIGN
FÖRFRÅGNINGSUNDERLAG			
BYGGHANDLING			
2025-02-26	GODKÄND		
CENTRUMHUSET HUS D			
KRÅKAN 1, ROBERTSFORS			
ÄF-Infrastructure AB			
Strandgatan 9A			
891 39 Örnsköldsvik			
Tel: 010-505 00 00			
MARCUS GRANQVIST	MARCUS GRANQVIST	SKAPAD AV	
ROBIN ÖSTMAN	GODKÄND AV	UPPDRAGSNUMMER	
	D0192211		
OMBYGGNAD BIBLIOTEK OCH LÄGENHETER			
HISS			
K-20-2-D004			