
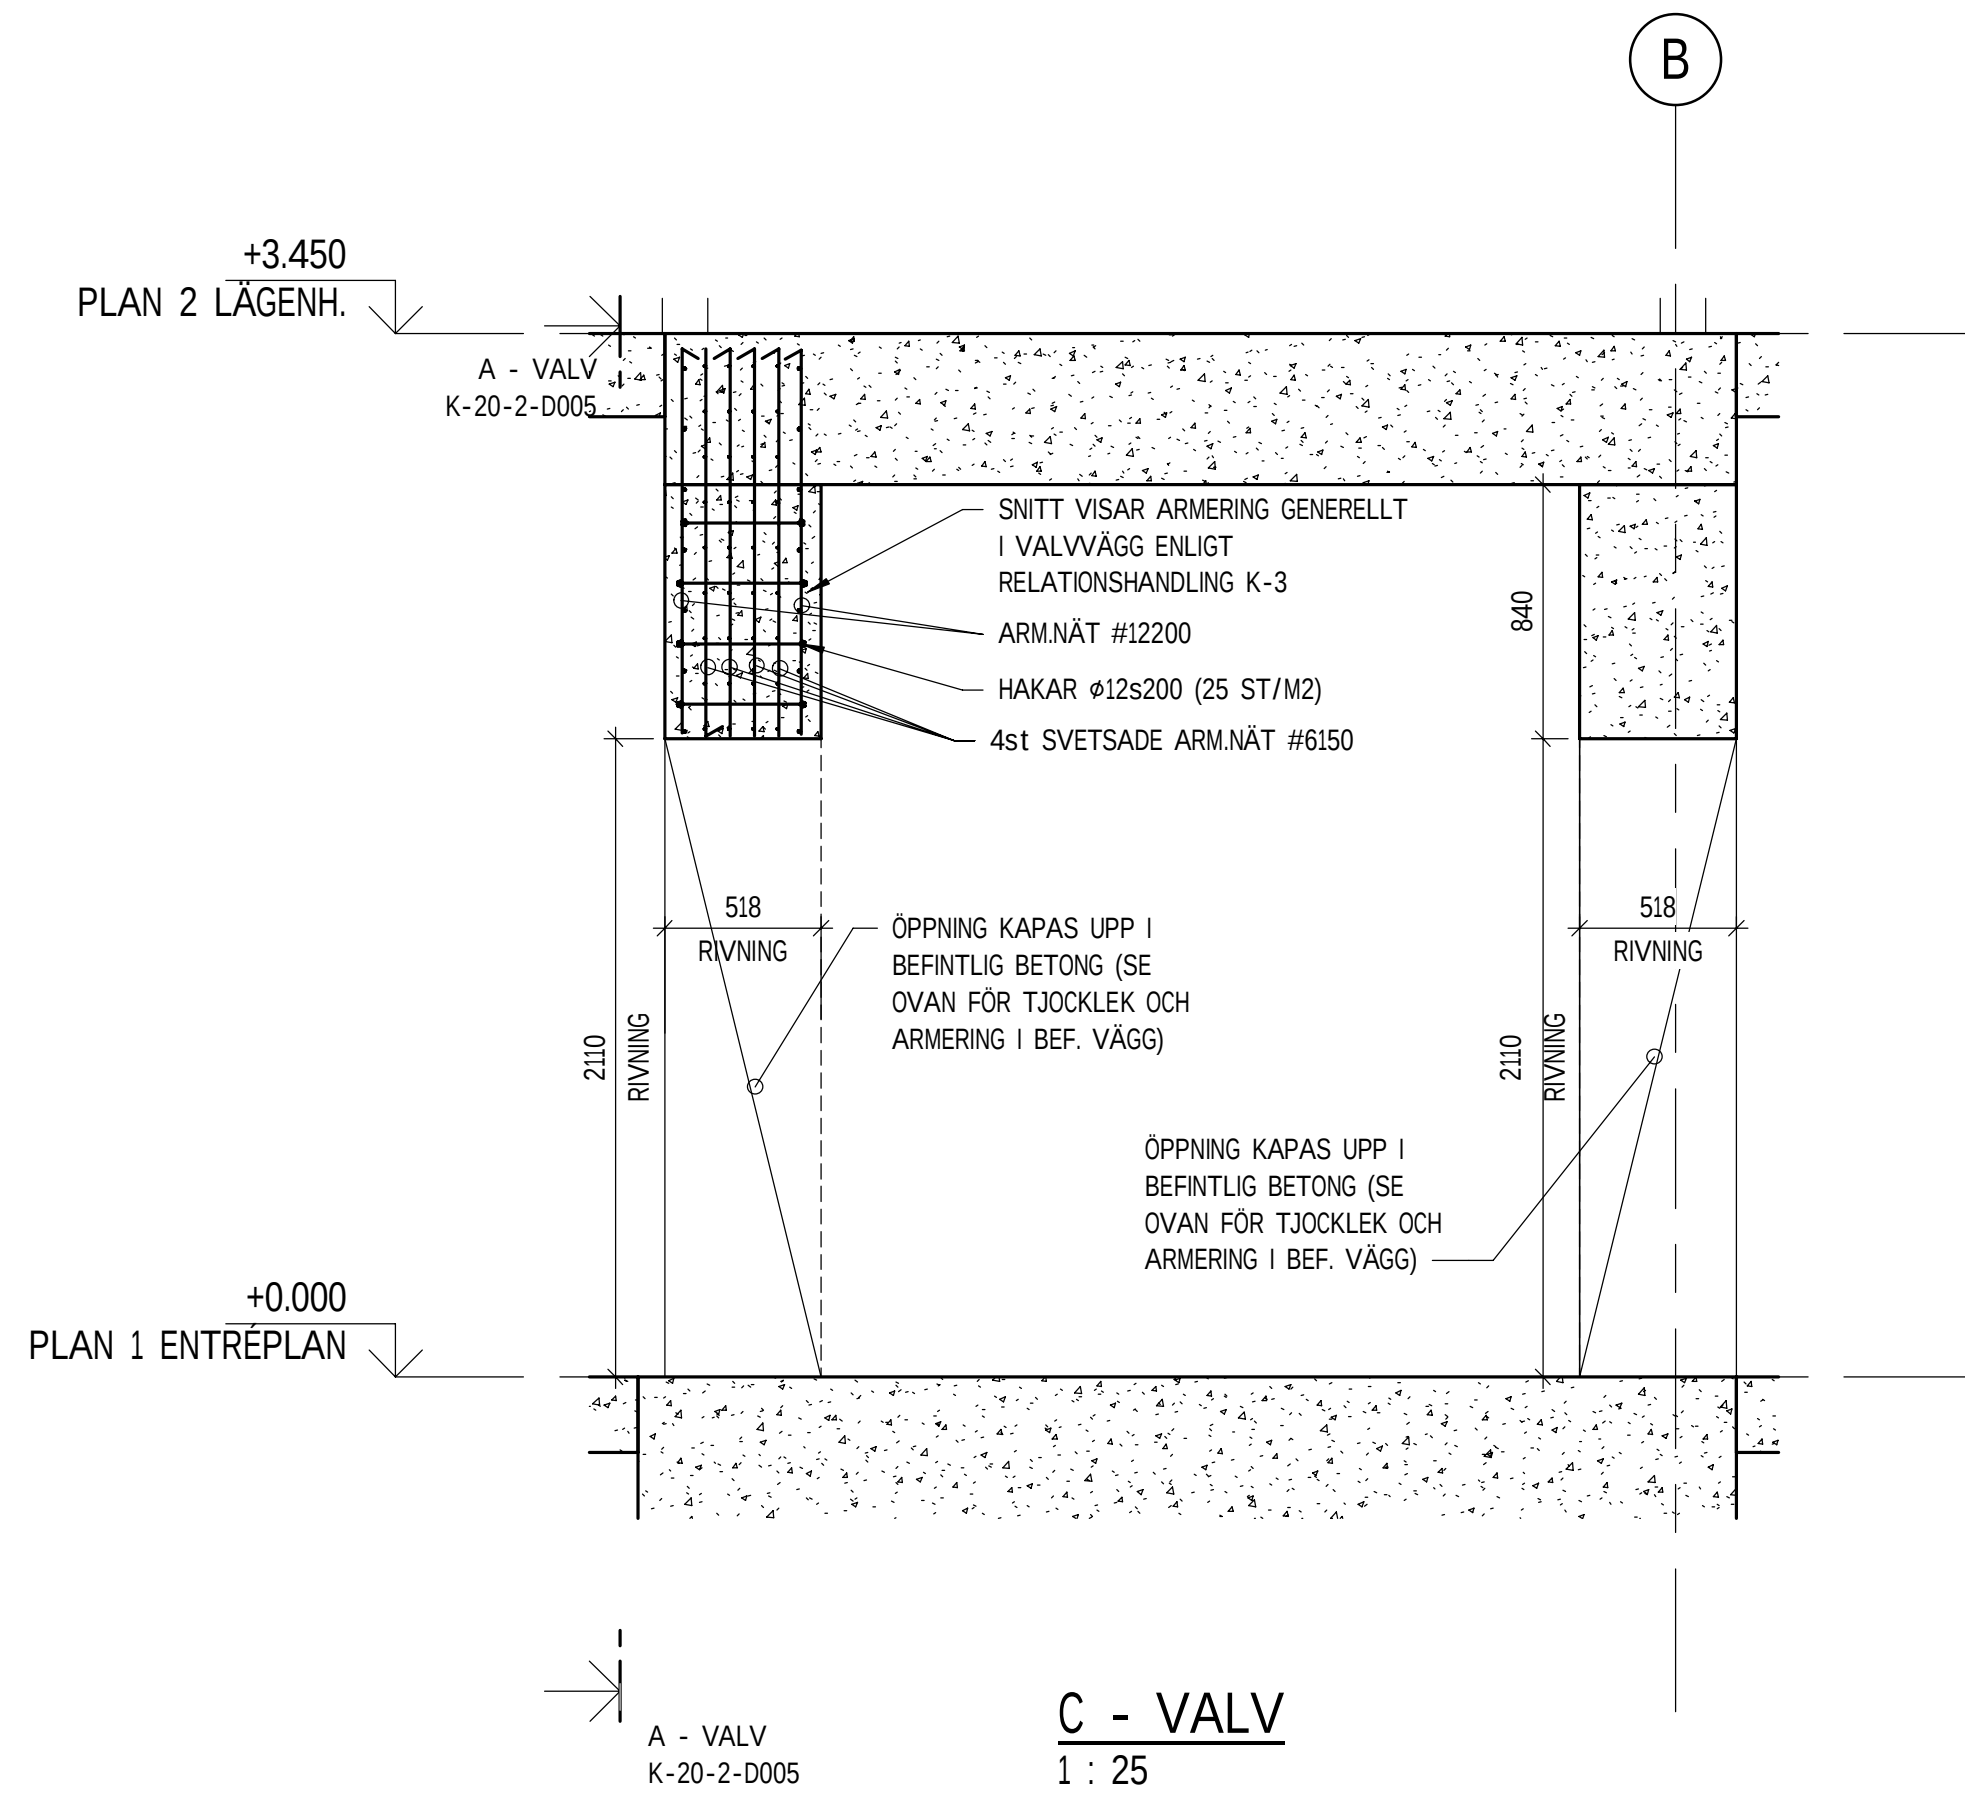
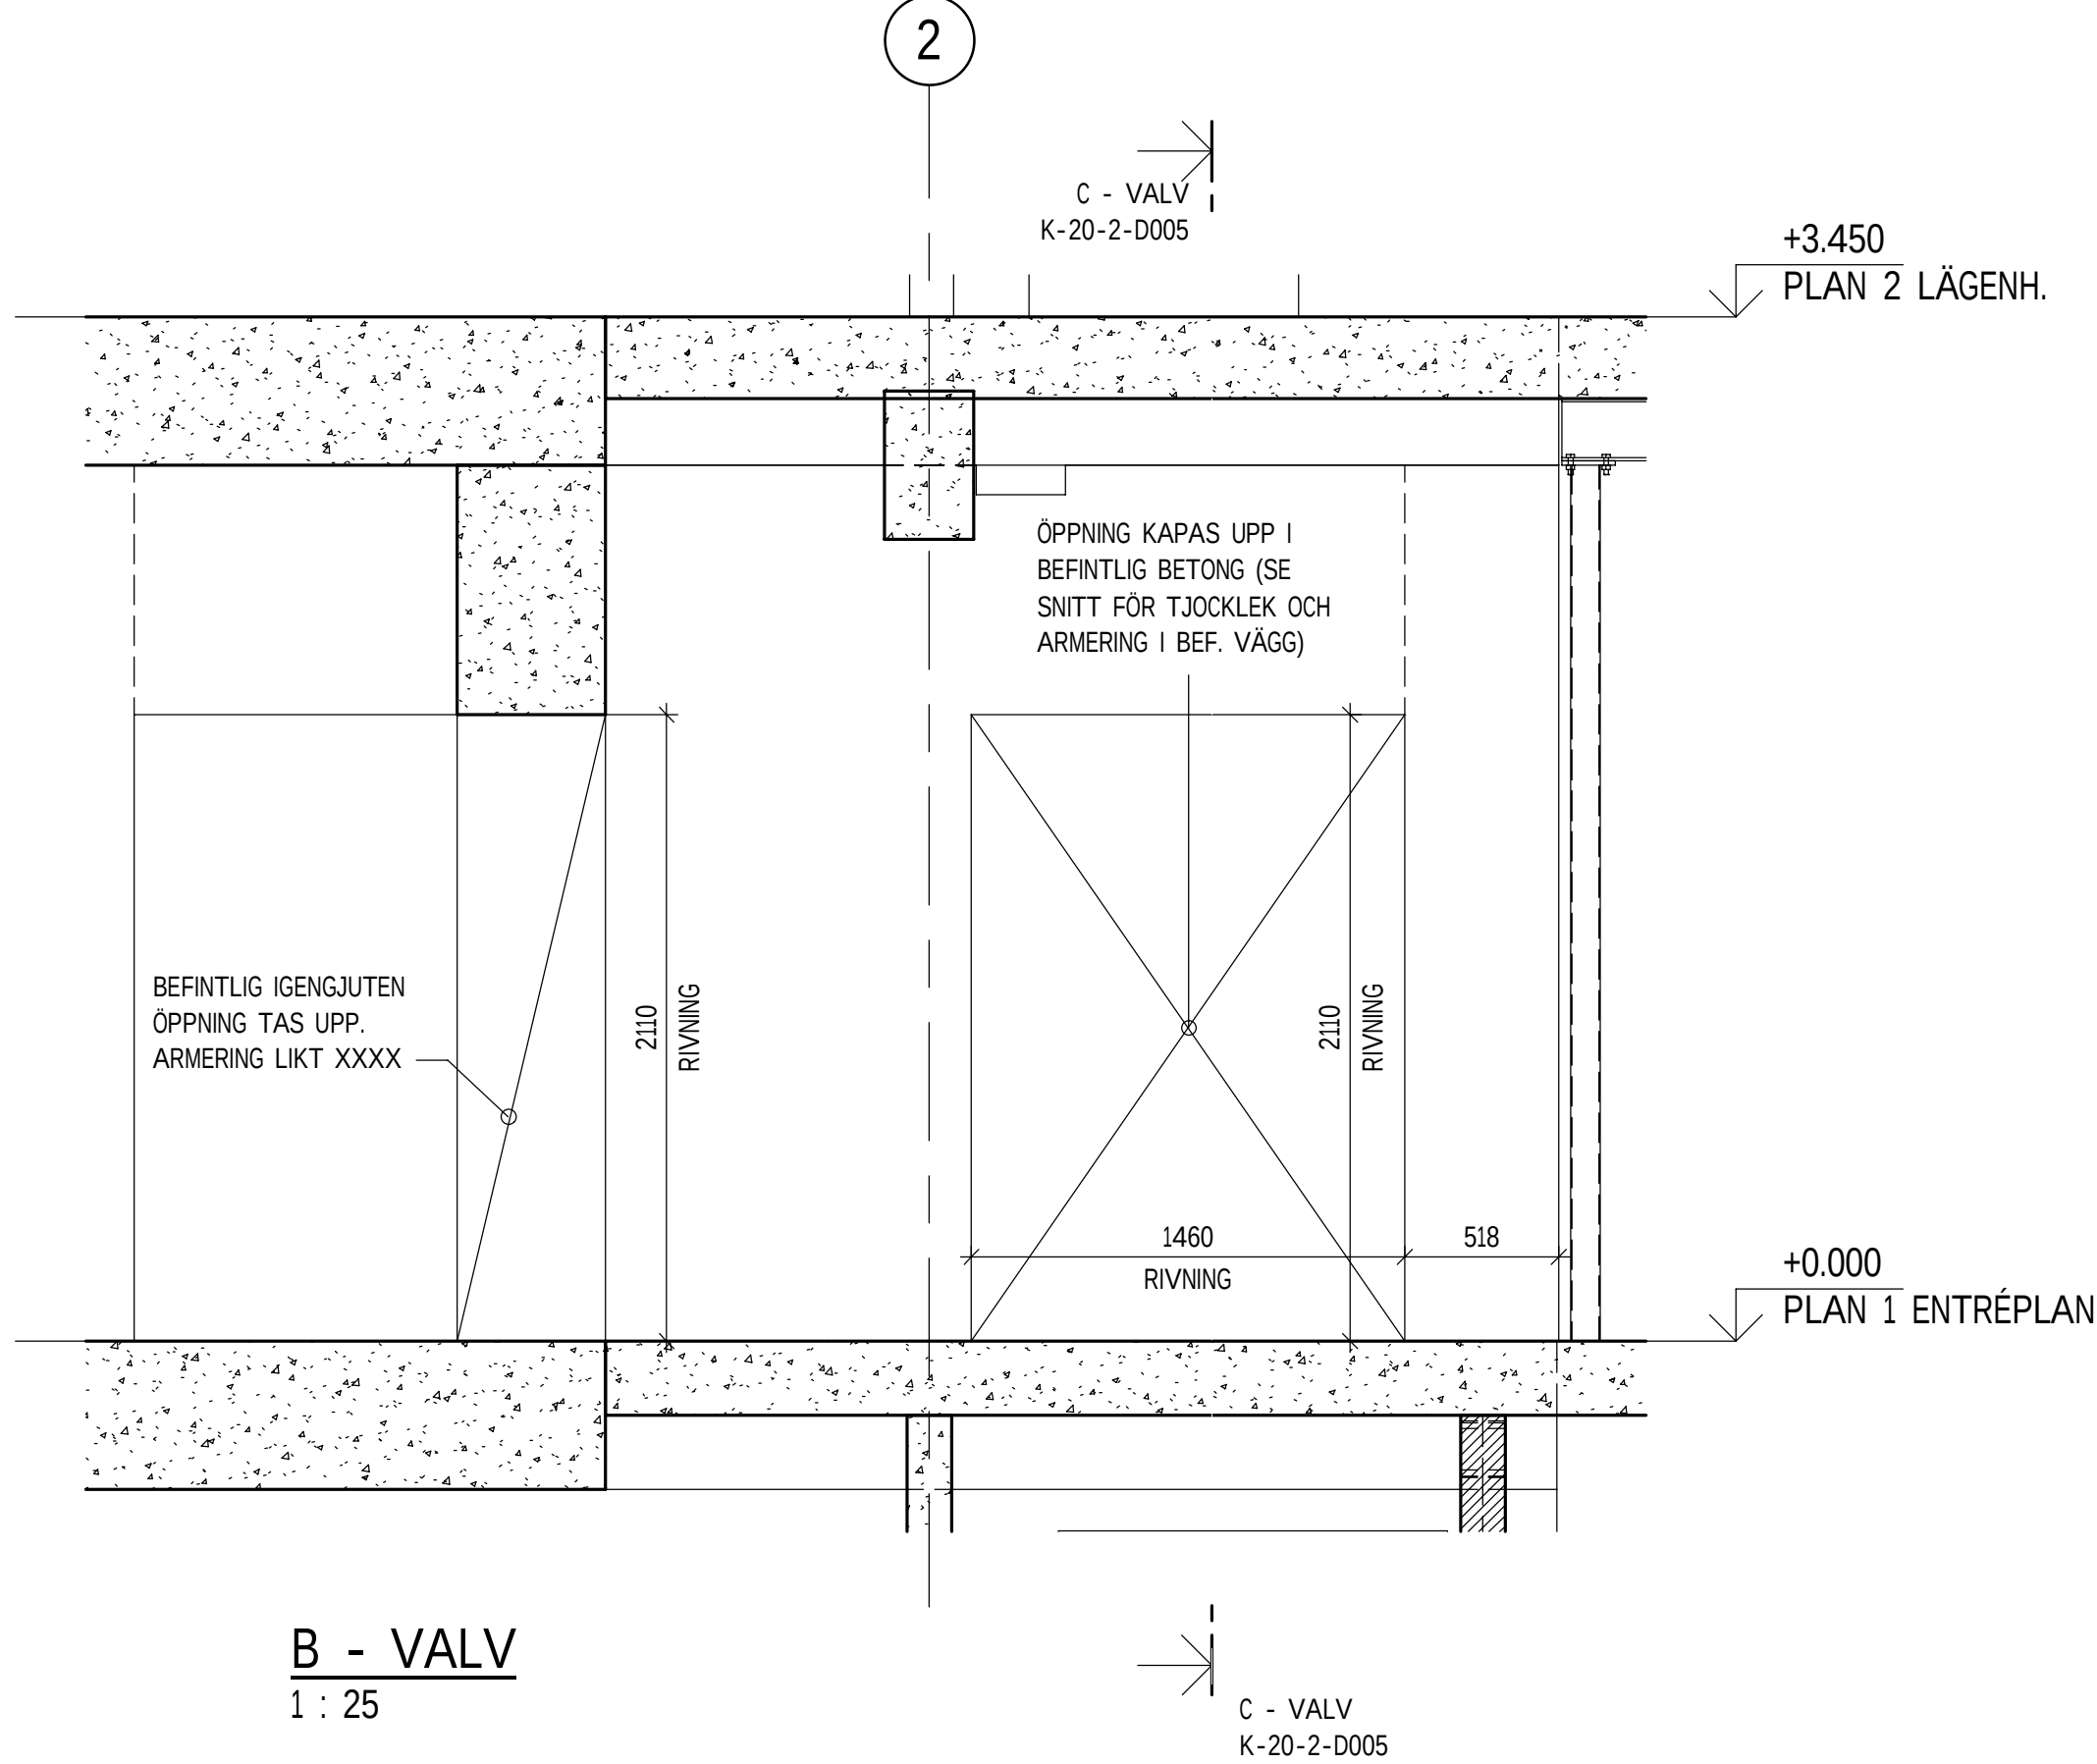


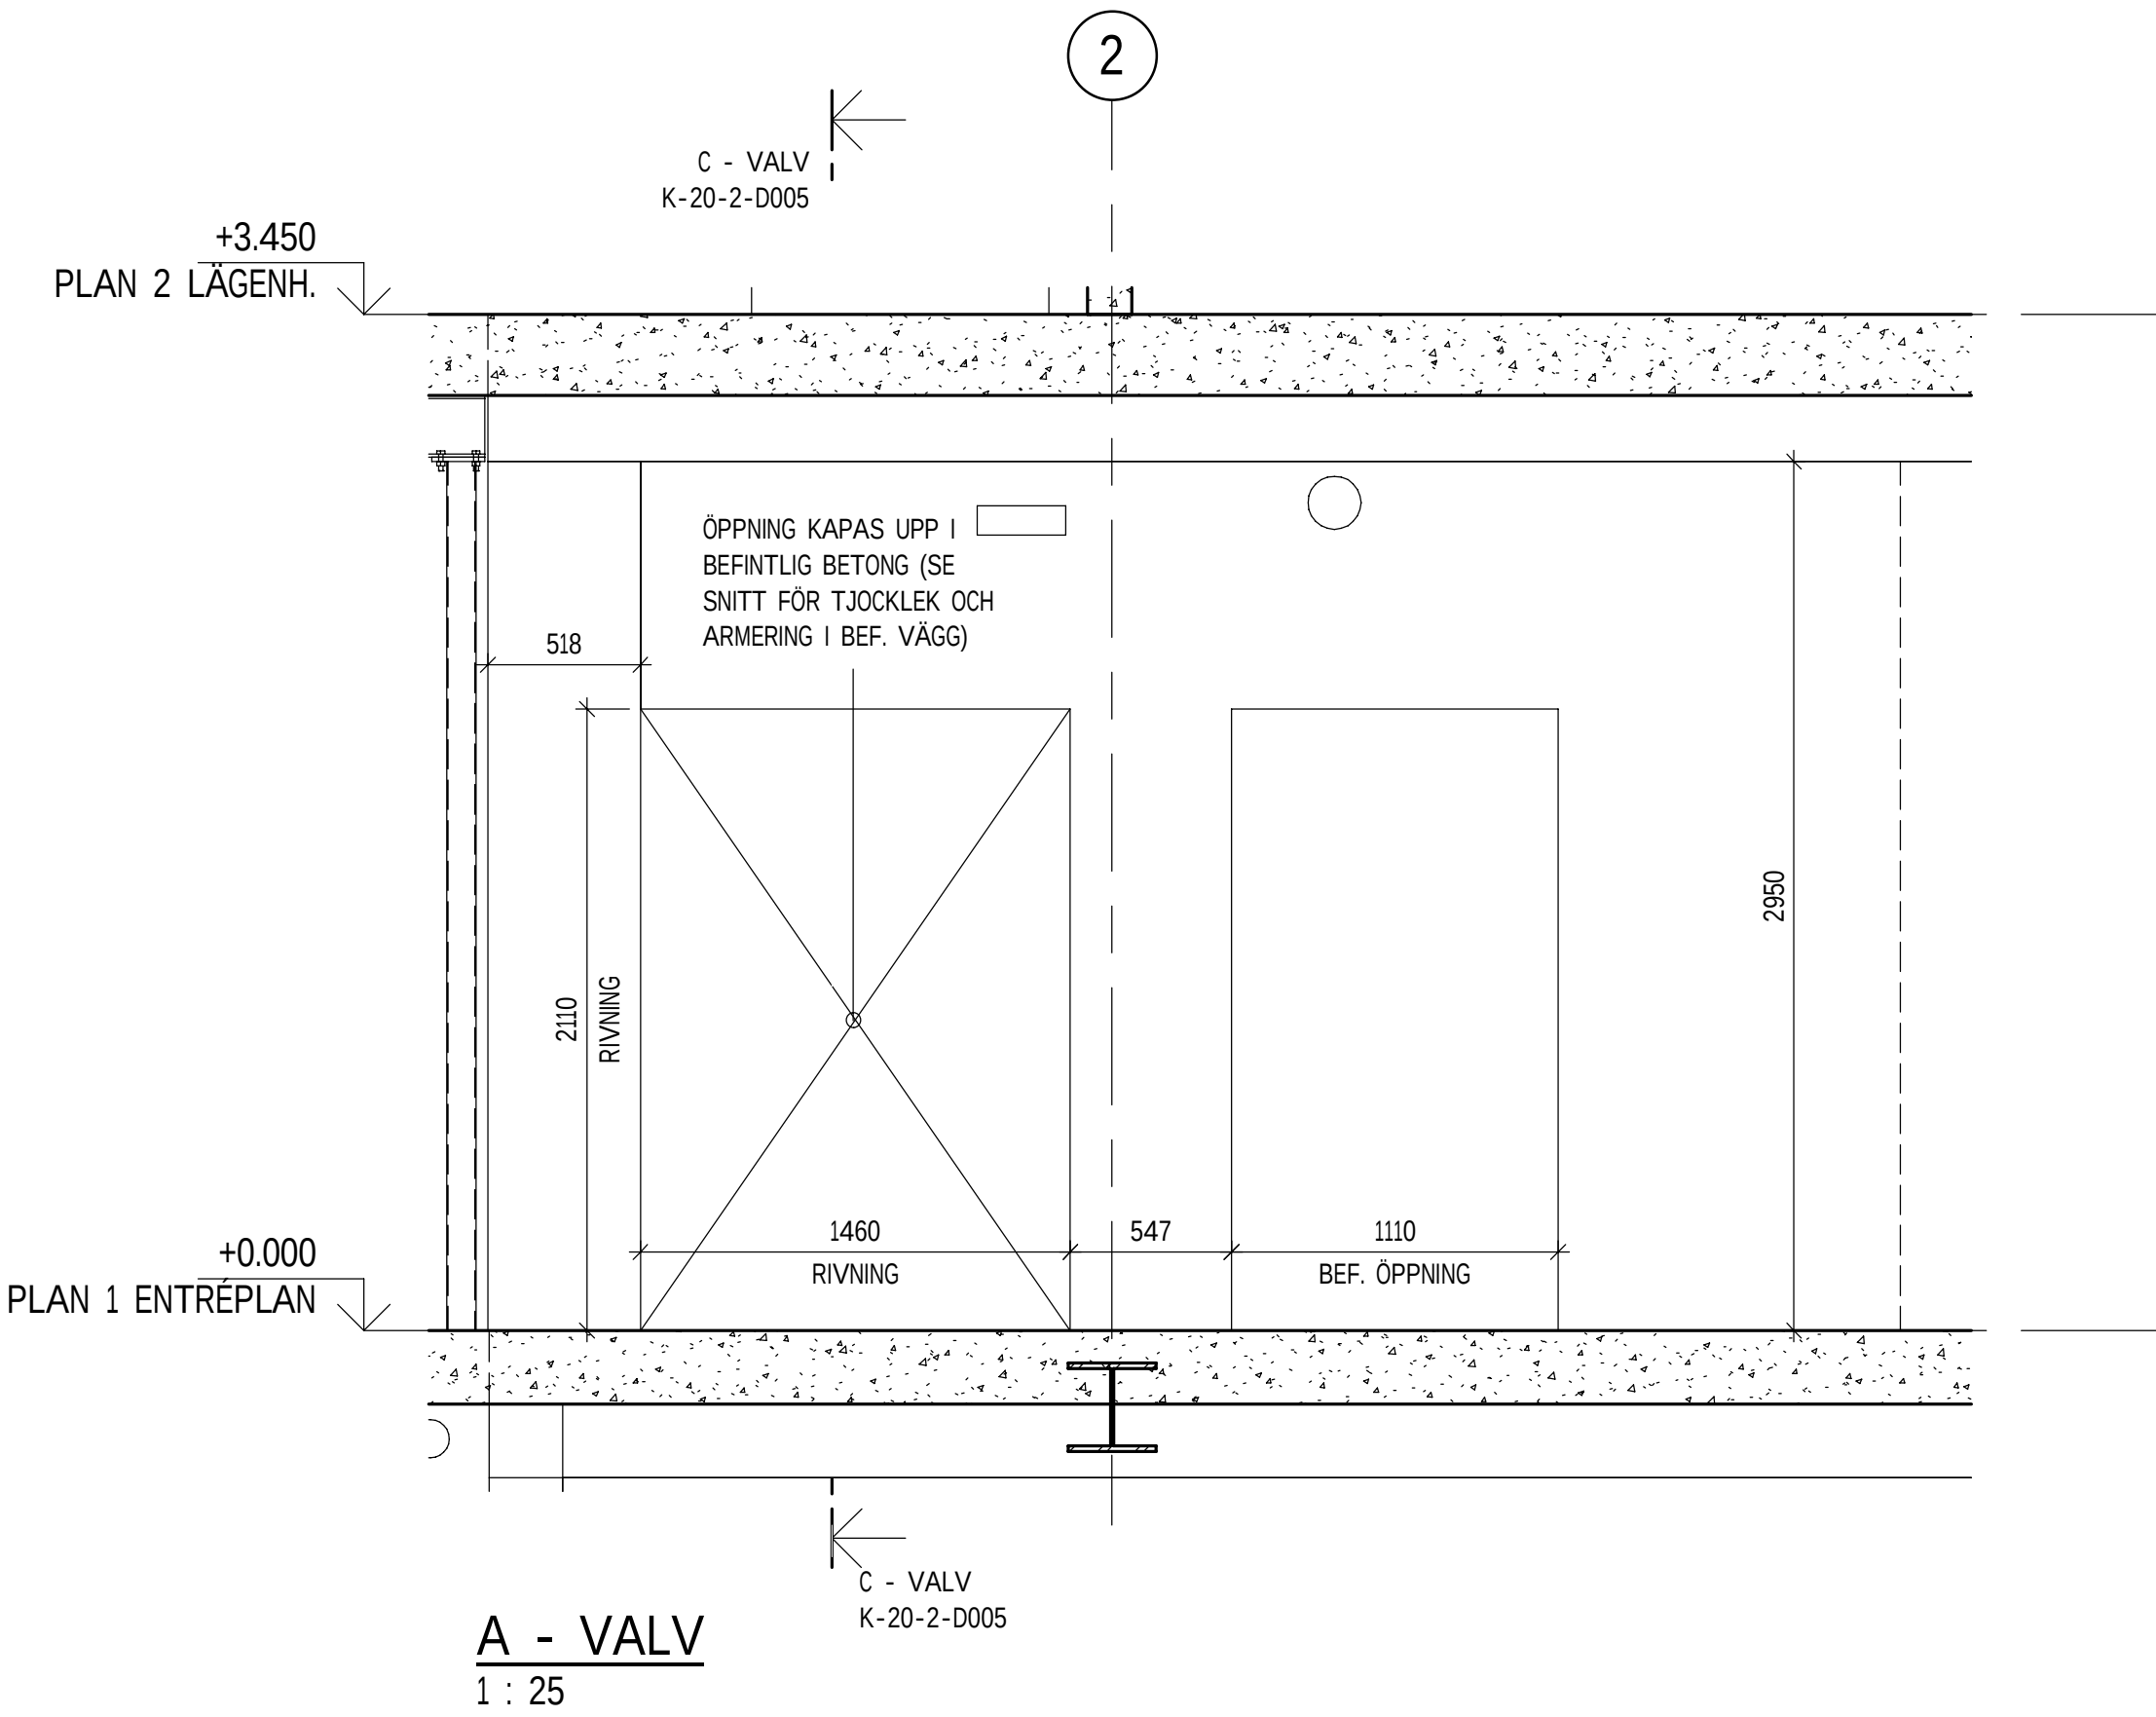

FÖRESKRIFTER

ALLMÄNNA ANVISNINGAR K-01-1-D001

FÖRKLARINGAR

	BEFINTLIG BETONG
	PLATSGJUTEN BETONG
	BEFINTLIG LÄTTBETONG
	DRÄNERANDE PORDRÄN
	CELLPLAST EPS
	CELLPLAST XPS

HÄNVISNINGAR

ARMERINGSPLAN: K-22-1-D001

SKALA 1:25
0 0,5 1 2,5
METER

1	GODKÄND	2025-02-26	MG
BET	ÄNDRING AVSER	DATUM	SIGN
FÖRFRÅGNINGSUNDERLAG			
BYGGHANDLING			
2025-02-26	GODKÄND	ÄNDRING	STATUS
CENTRUMHUSET HUS D KRÅKAN 1, ROBERTSFORS			
ÄF-Infrastructure AB Strandgatan 9A			
891 39 Örnsköldsvik Tel: 010-505 00 00			
MARCUS GRANQVIST	JOEL OLOFSSON	SKAPAD AV	ANSVARIG PART
ROBIN ÖSTMAN	DO192211	UPPRAGSNUMMER	AFRY
RITNINGSKATEGORI			
OMBYGGNAD BIBLIOTEK OCH LÄGENHETER	ÄNDRING	A1	FORMAT
PLAN 1		1:25	SKALA
VALV		1	BET
K-20-2-D005			