

FÖRESKRIFTER





ALLMÄNNA ANVISNINGAR K-01-1-D001

FÖRKLARINGAR


- BEFINTLIG BETONG
- PLATSGJUTEN BETONG
- BEFINTLIG LÄTTBETONG
- DRÄNERANDE PORDRÄN
- CELLPLAST EPS
- CELLPLAST XPS

HÄNVISNINGAR

GRUNDPLAN: K-15-1-D090
ARMERINGSPLAN K-22-1-D001

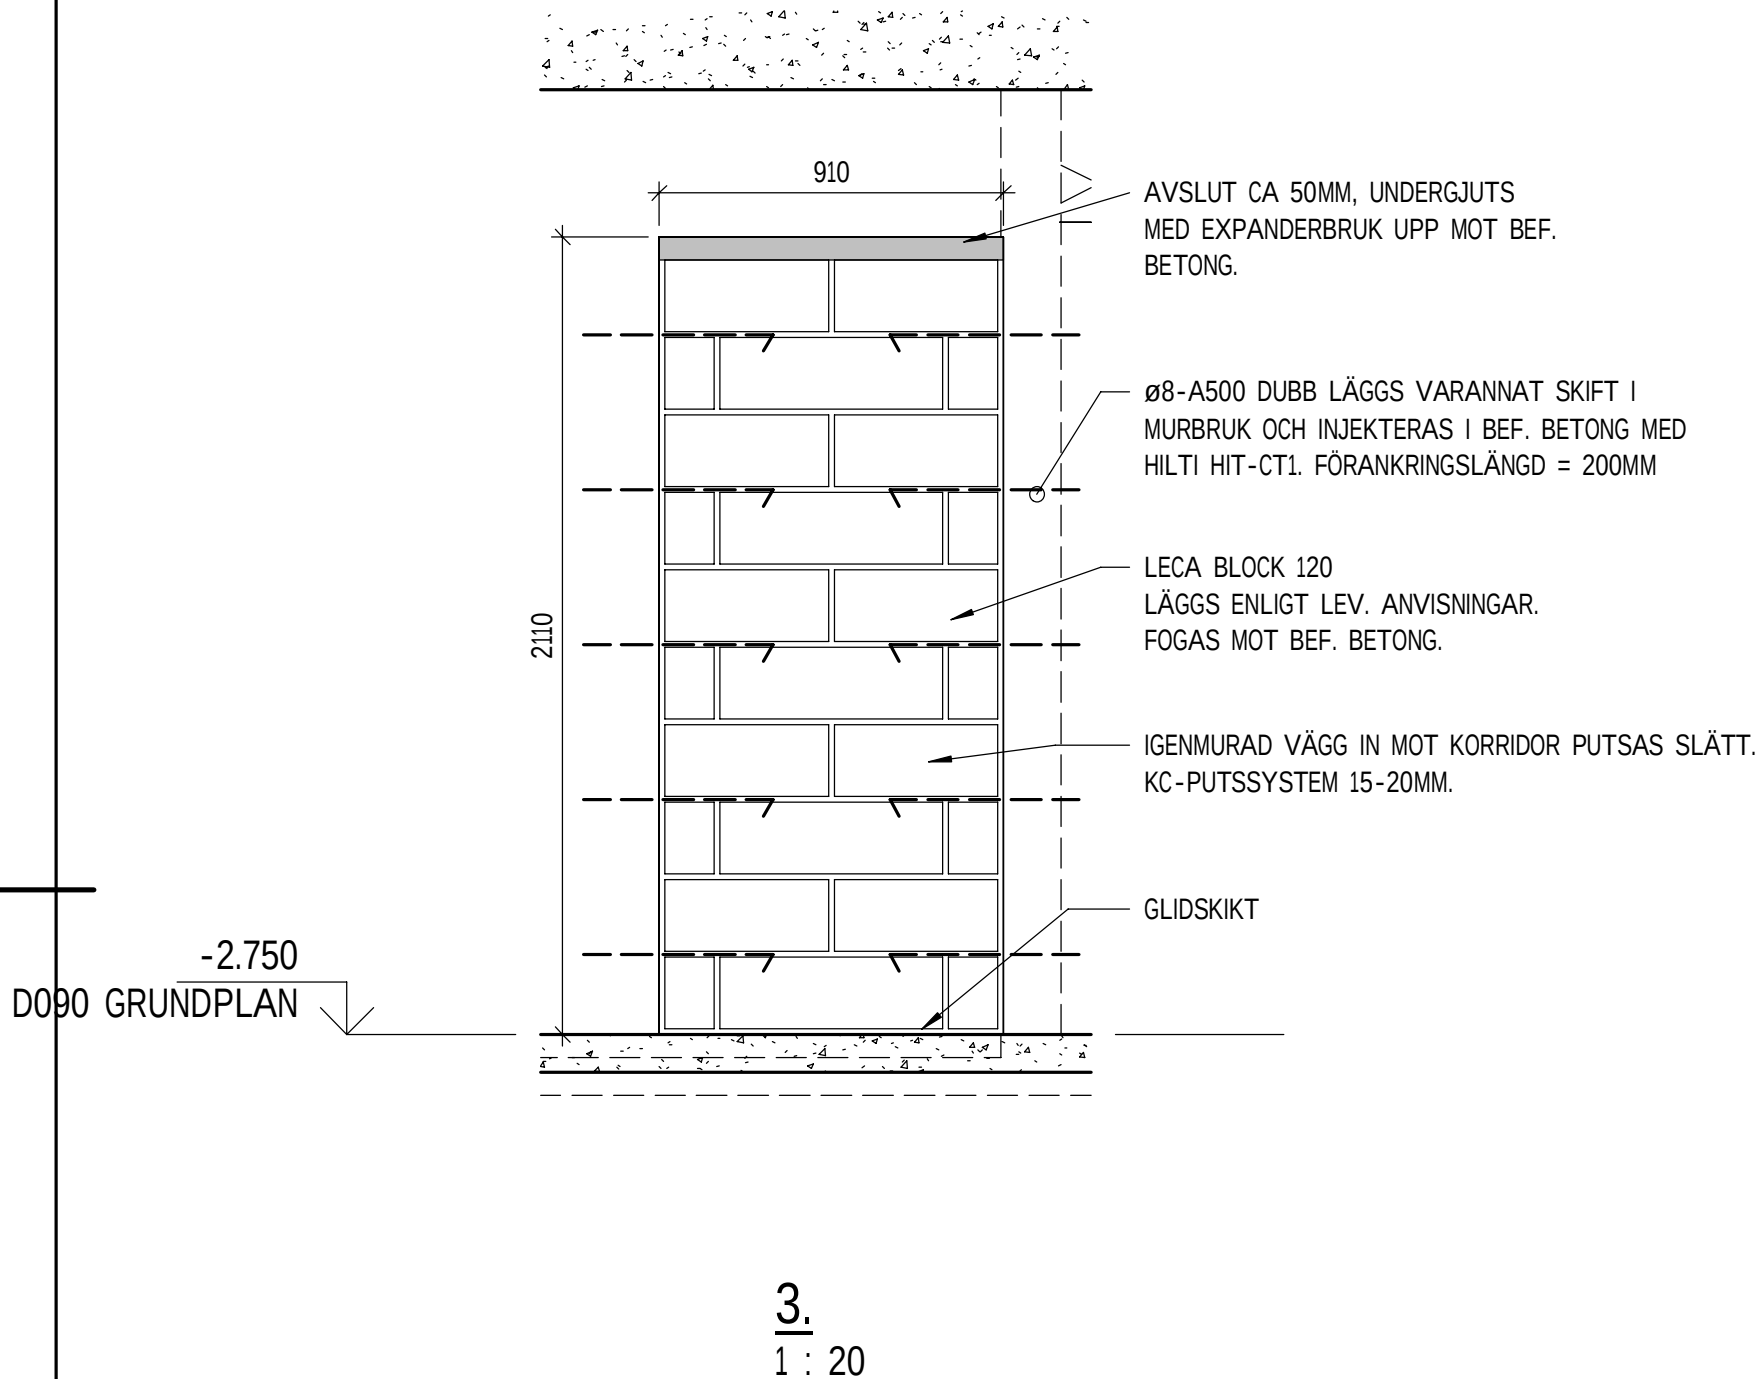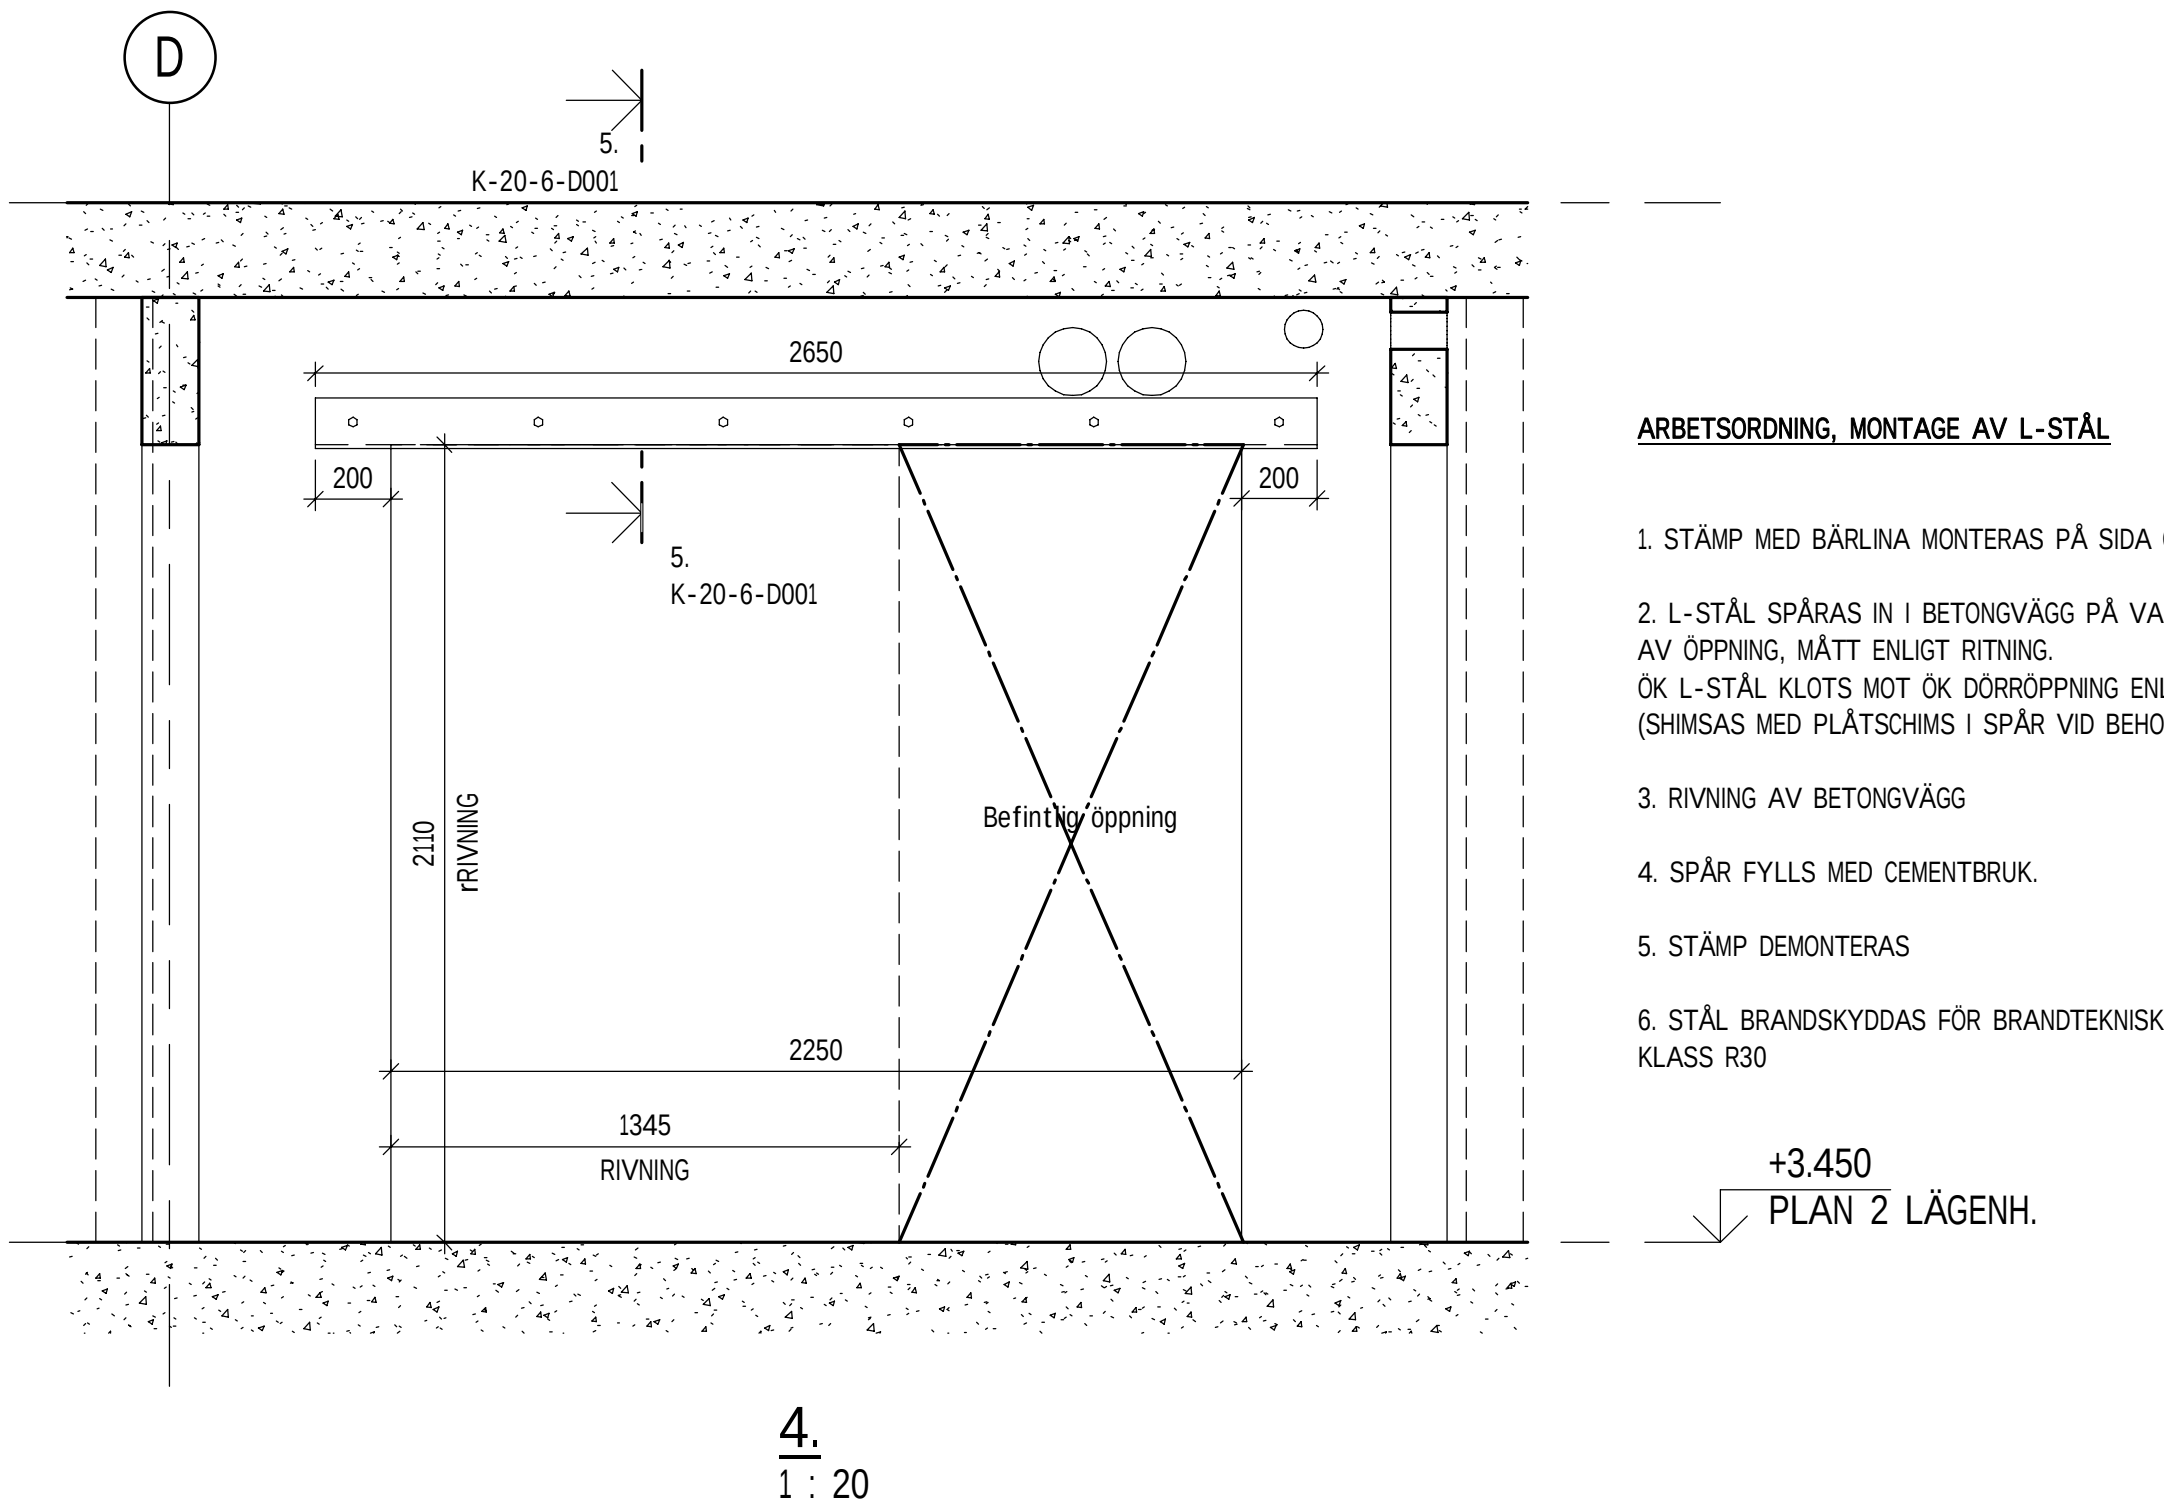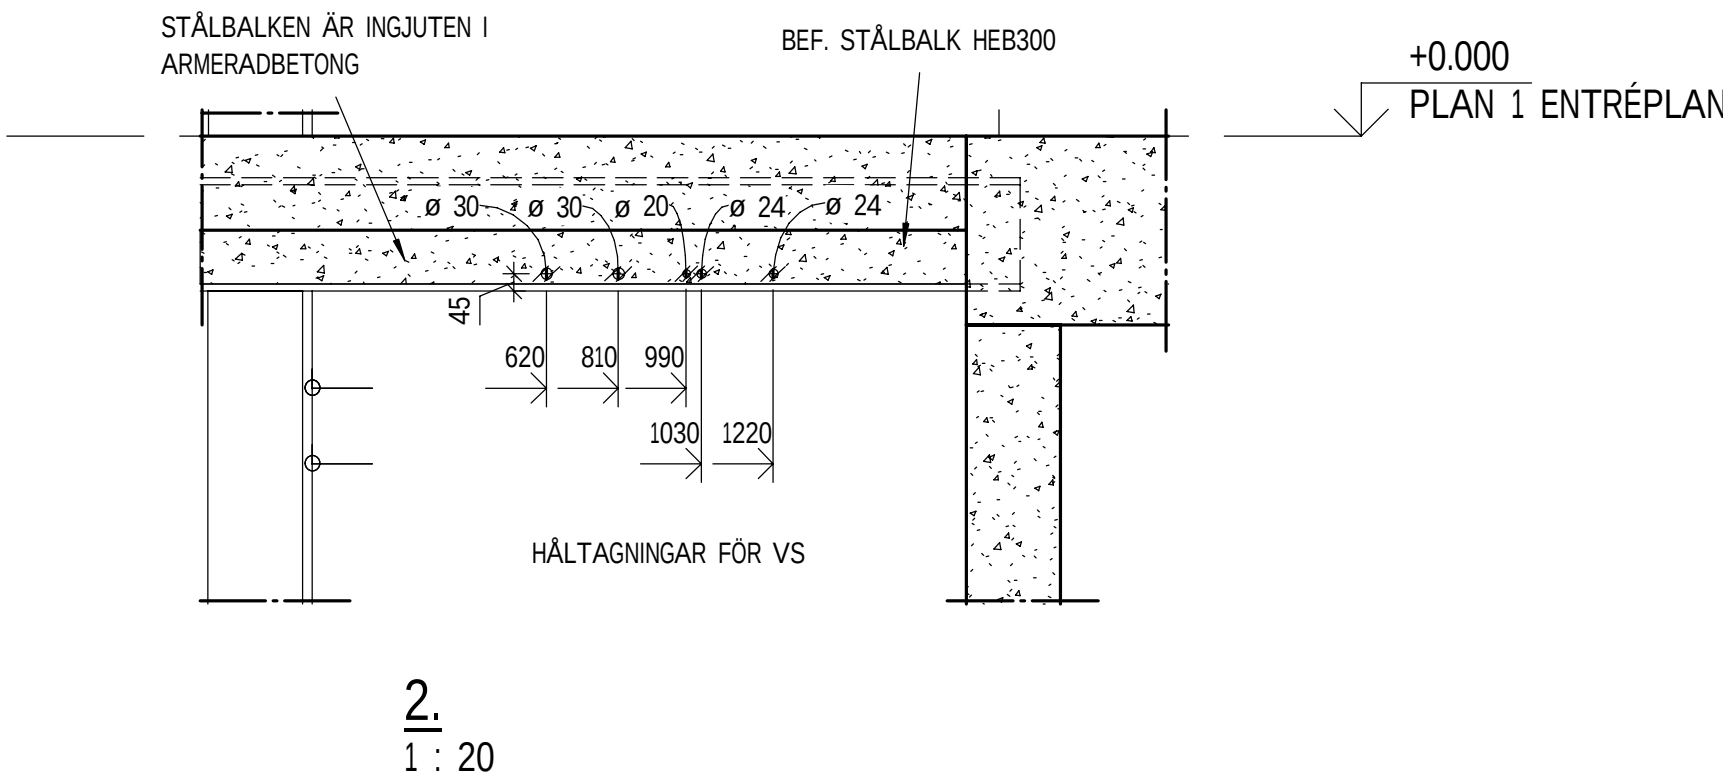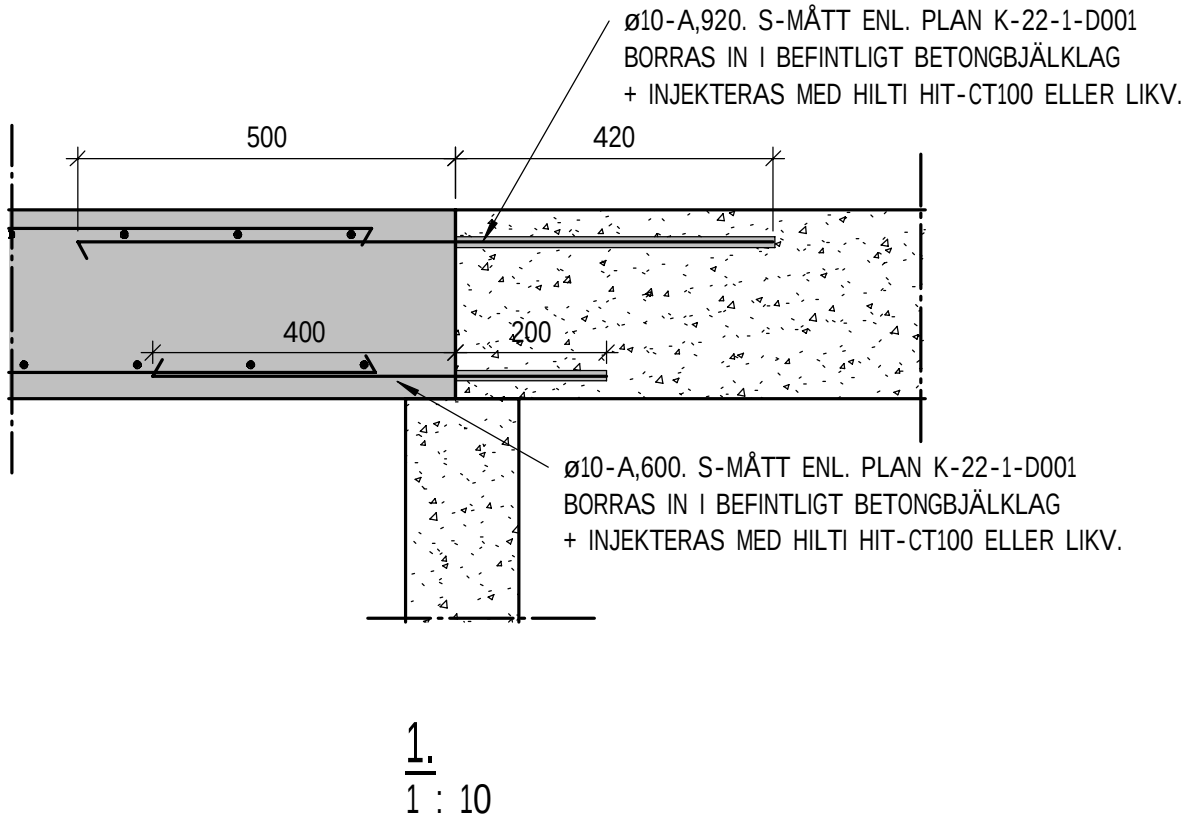

-2.750
D090 GRUNDPLAN

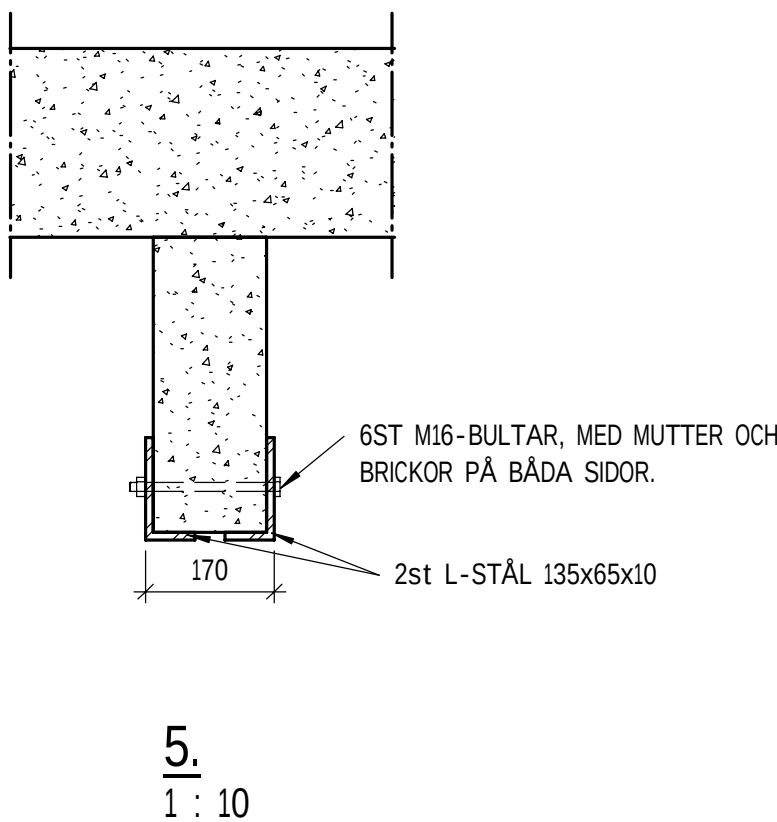

SKALA 1:20

0 0.1 0.5 1 1.5 2
METER

1	GODKÄND		2025-02-26	MG
BET	ÄNDRING AVSER		DATUM	SIGN
FÖRFRÅGNINGSUNDERLAG				
BYGGHANDLING				
2025-02-26		GODKÄND		ÄNDRING
CENTRUMHUSET HUS D				PROJEKT
KRÅKAN 1, ROBERTSFORS				
ÄF-Infrastructure AB				ANSVARIG PART
Strandgatan 9A				
891 39 Örnsköldsvik				Tel: 010-505 00 00
MARCUS GRANQVIST		KONTAKTPERSON	MARCUS GRANQVIST	SKAPAD AV
ROBIN ÖSTMAN		GODKÄND AV	D0192211	UPPRAGSNUMMER
				RITNINGSKATEGORI
ÖMBYGGNAD BIBLIOTEK OCH LÄGENHETER				INNEHÅLL
				FORMAT
DETALJER				1:20
				SKALA
K-20-6-D001				NUMMER
				BET