


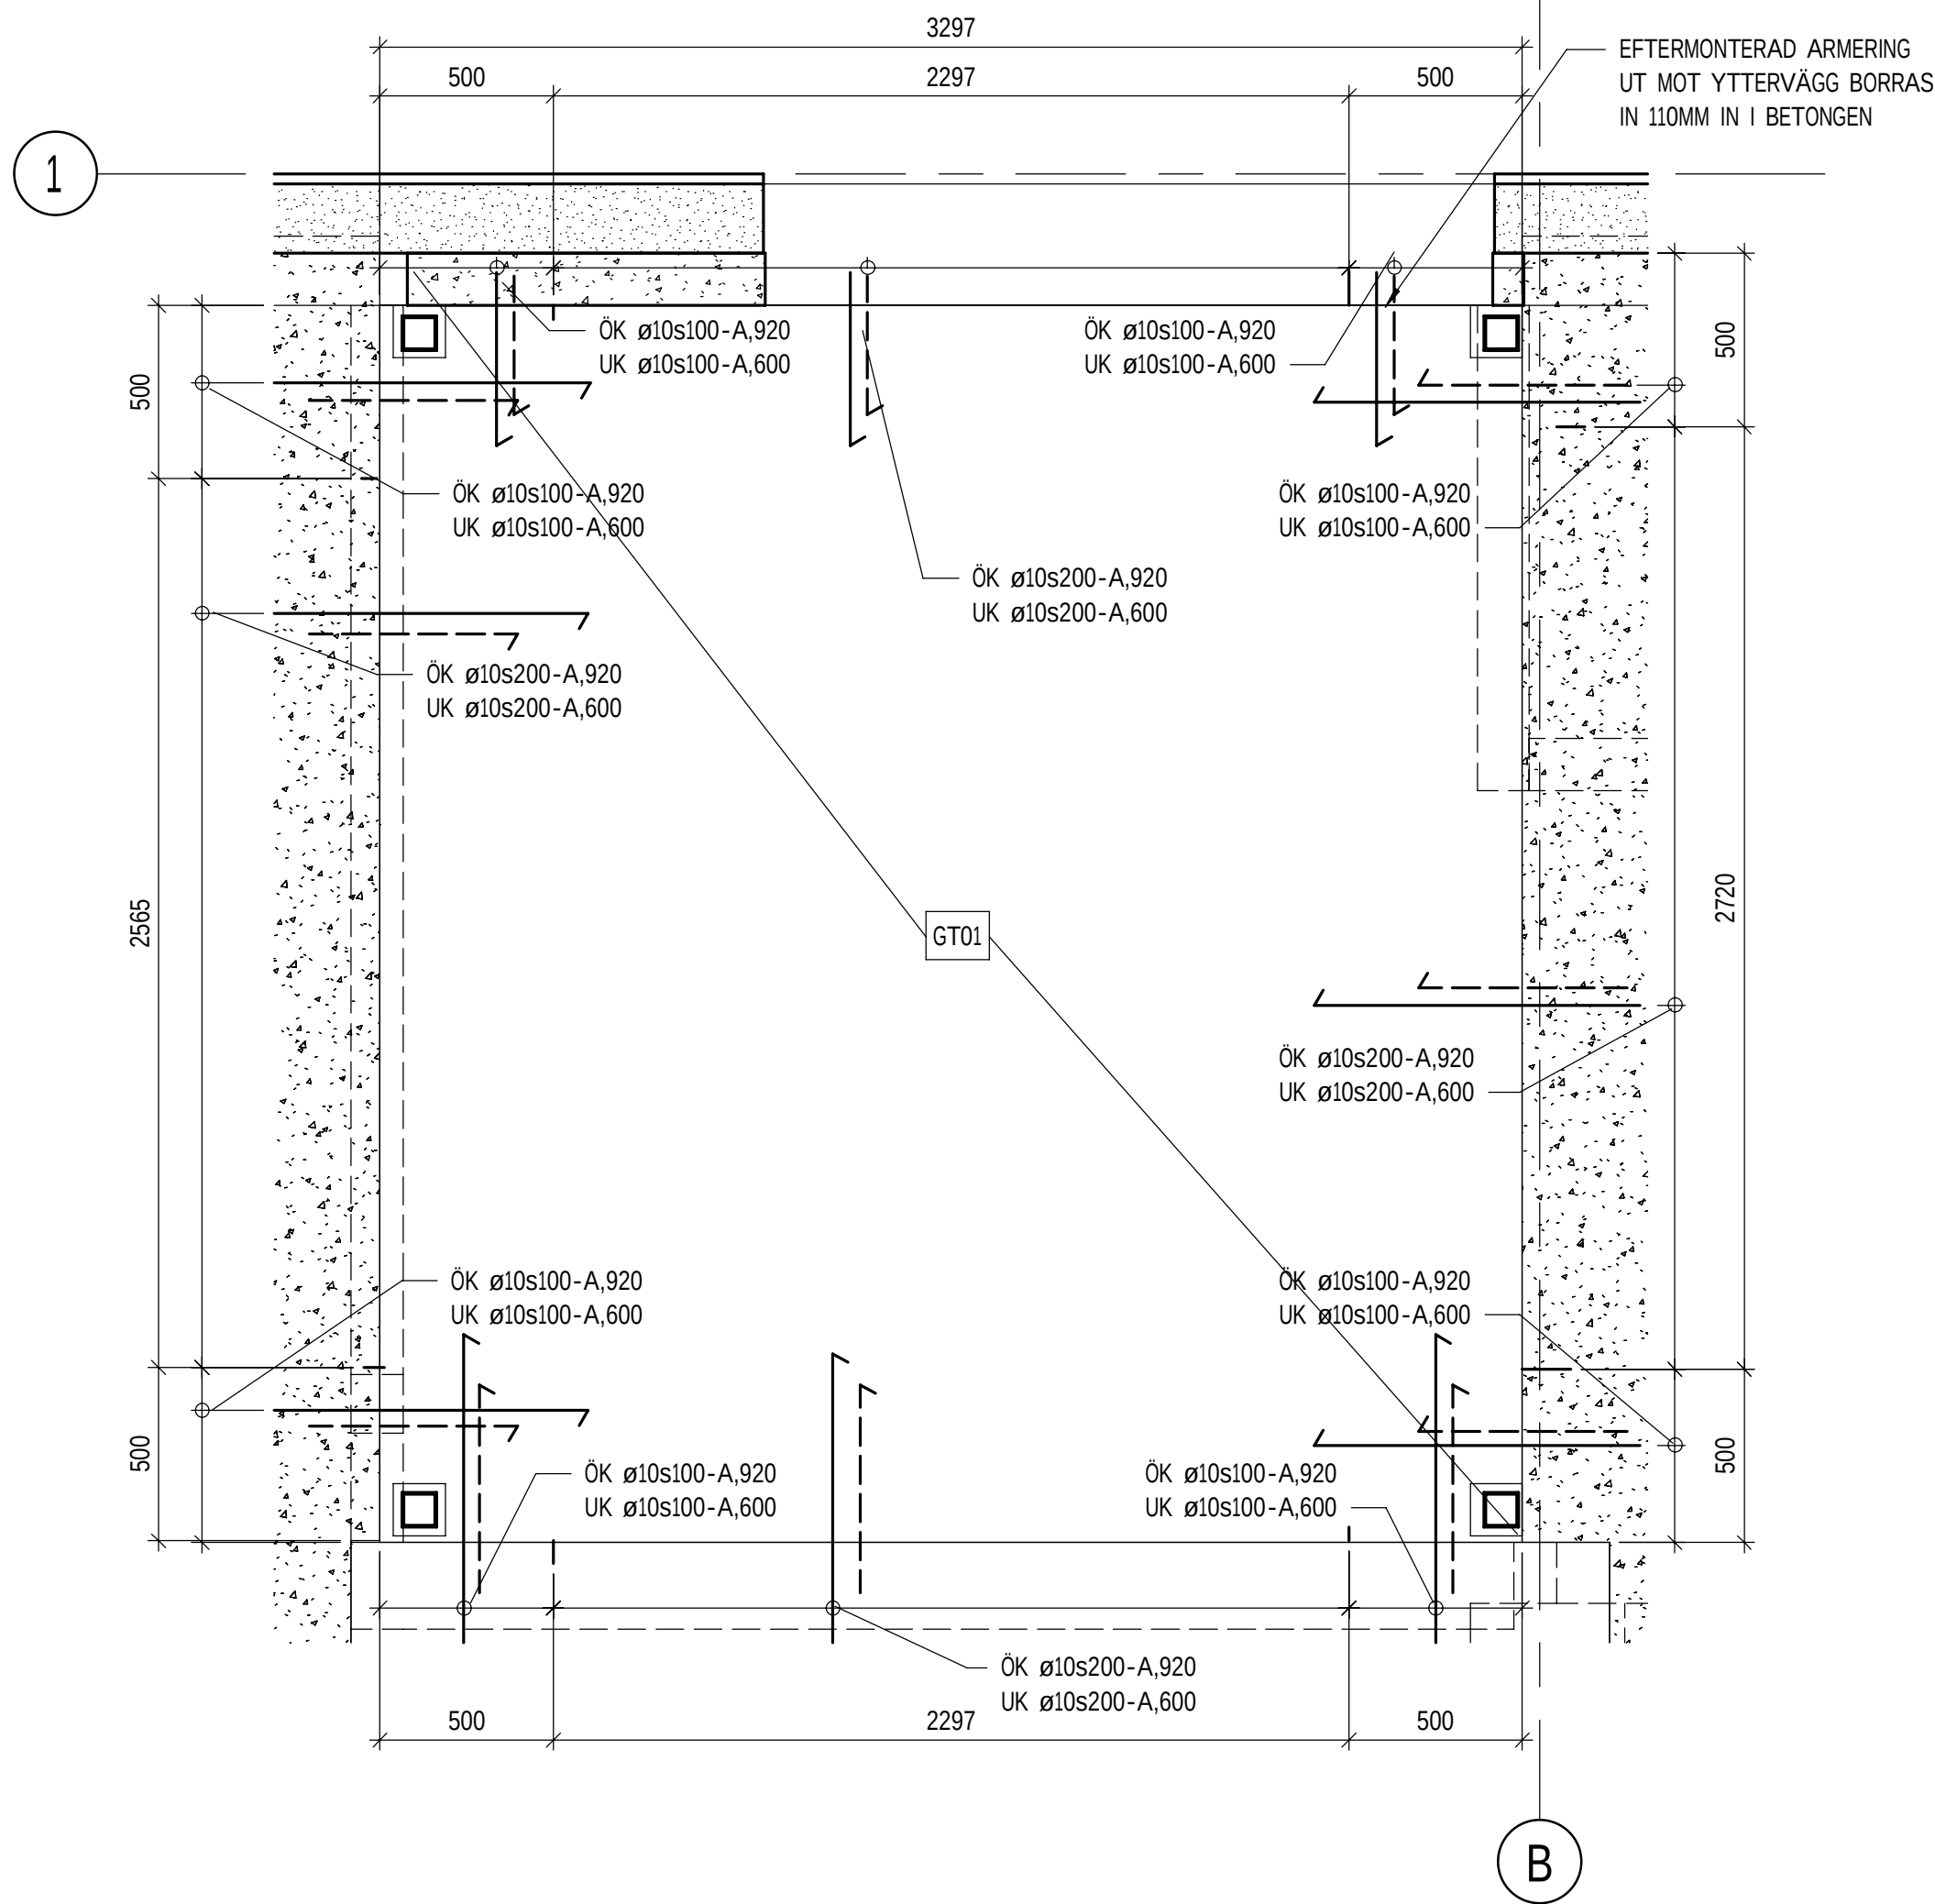


TRAPPHUS PLAN 1
1 : 20

ARBETSORDNING, NYA BJÄLKLAG OCH NYTT STÅL

- RIVNING AV BEFINTLIG TRAPP, OCH TRAPPLAN. TILL TRAPPHUS VÄGGAR.
- STÄMPNING MED BÄRLINA MONTERAS PÅ BÅDA SIDOR OM TRAPPHUS. OCH UNDER BETONGBJÄLKLAG. BÅDA VÅNINGAR.
- RIVNING AV BETONGVÄGGAR
- UPPBYGGNAD AV NYTT BETONGBJÄLKLAG PLAN 1
- MONTERING AV NYA STÅL
- UPPBYGGNAD AV NYTT BETONGBJÄLKLAG PLAN 2

STÅL BRANDSKYDDAS FÖR BRANDTEKNISK
KLASS R30

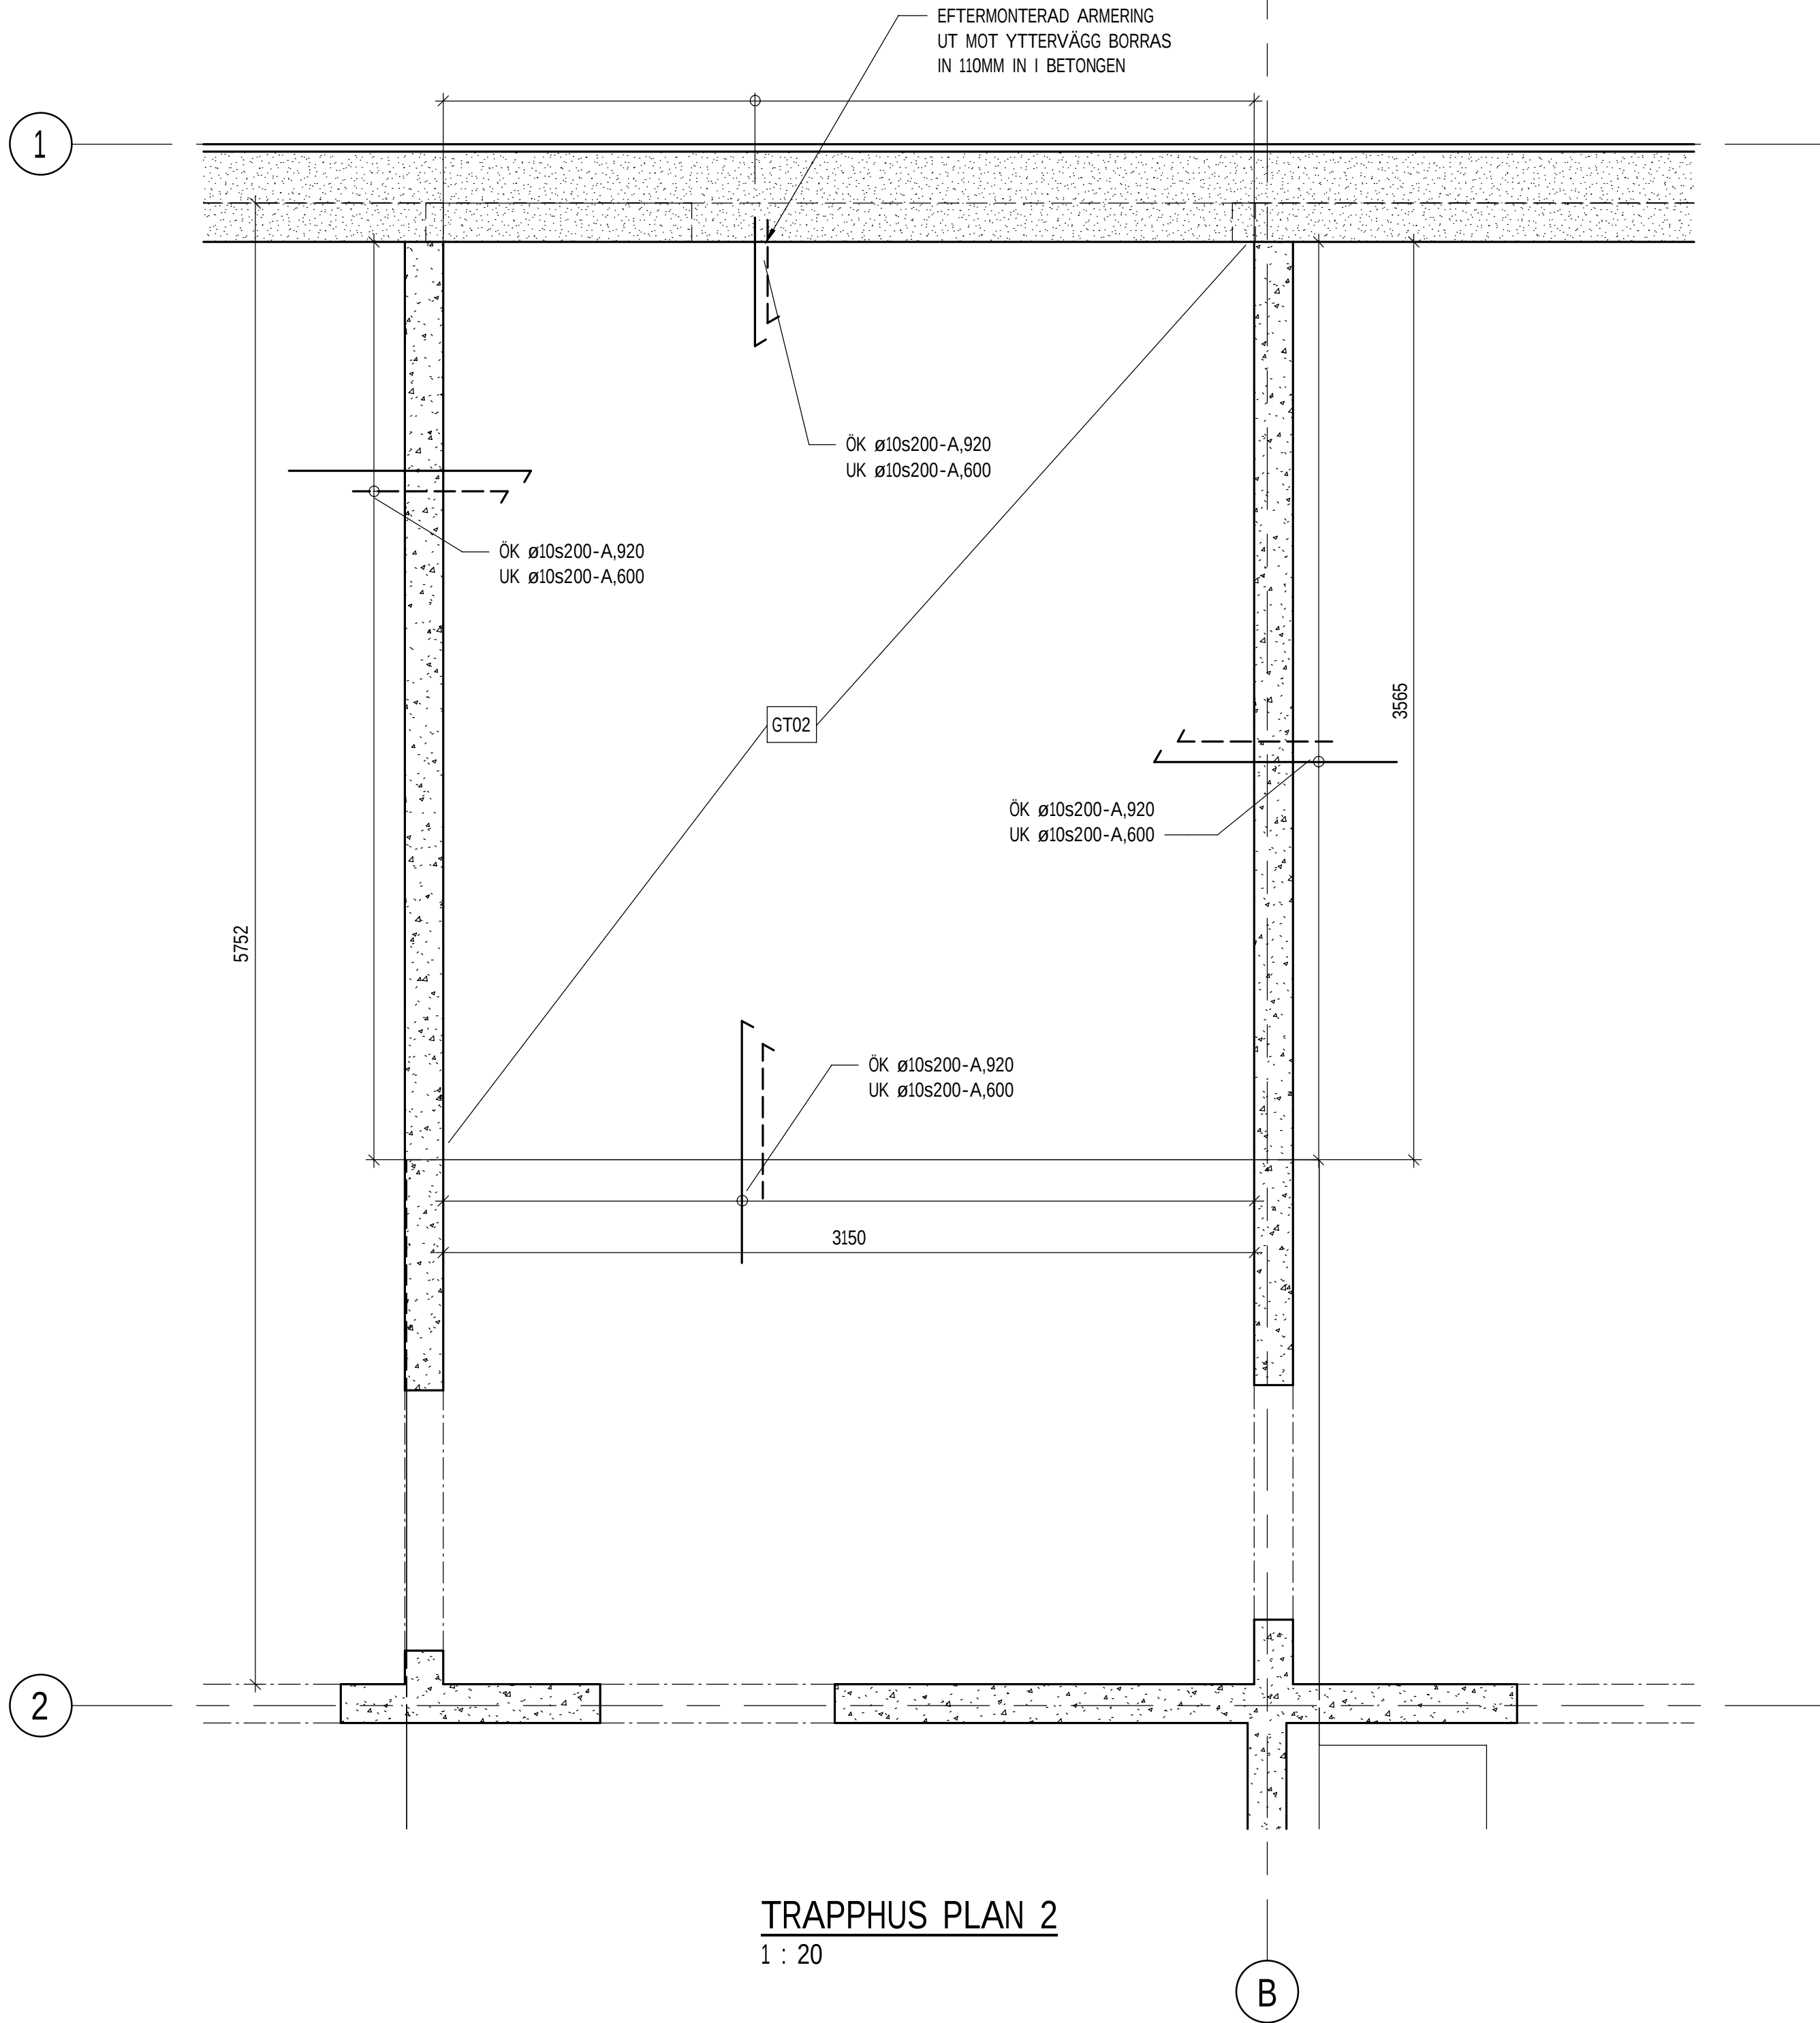

TRAPPHUS PLAN 2
1 : 20

FÖRESKRIFTER

ALLMÄNNA ANVISNINGAR: K-01-1-D001

HÄNVISNINGAR

PLANER

GRUNDPLAN:
KÄLLARPLAN -DEL 1:
KÄLLARPLAN - DEL 2:
PLAN 1 - DEL 1:
PLAN 1 - DEL 2:
PLAN 2 - DEL 1:
PLAN 2 - DEL 2:
FLÅKTRUM - DEL 1:
FLÅKTRUM - DEL 2:

K-15-1-D090
K-20-1-D091
K-20-1-D092
K-20-1-D101
K-20-1-D102
K-20-1-D201
K-20-1-D202
K-20-1-D301
K-20-1-D302

1	GODKÄND	2025-02-26	MG
BET	ÄNDRING AVSER	DATUM	SIGN
FÖRFRÅGNINGSUNDERLAG			
BYGGHANDLING			
DATUM	2025-02-26	GODKÄND	ÄNDRING
CENTRUMHUSET HUS D			
KRÅKAN 1, ROBERTSFORS			
ÄF-Infrastructure AB			
Strandgatan 9A			
891 39 Örnsköldsvik			
Tel: 010-505 00 00			
MARCUS GRANQVIST			
MARCUS GRANQVIST			
ROBIN ÖSTMAN			
D0192211			
RITNINGSKATEGORI			
OMBYGGNAD BIBLIOTEK OCH LÄGENHETER			
TRAPPHUS			
K-22-1-D001			

SKALA 1:1

0 10 20
MILLIMETER

50

100