




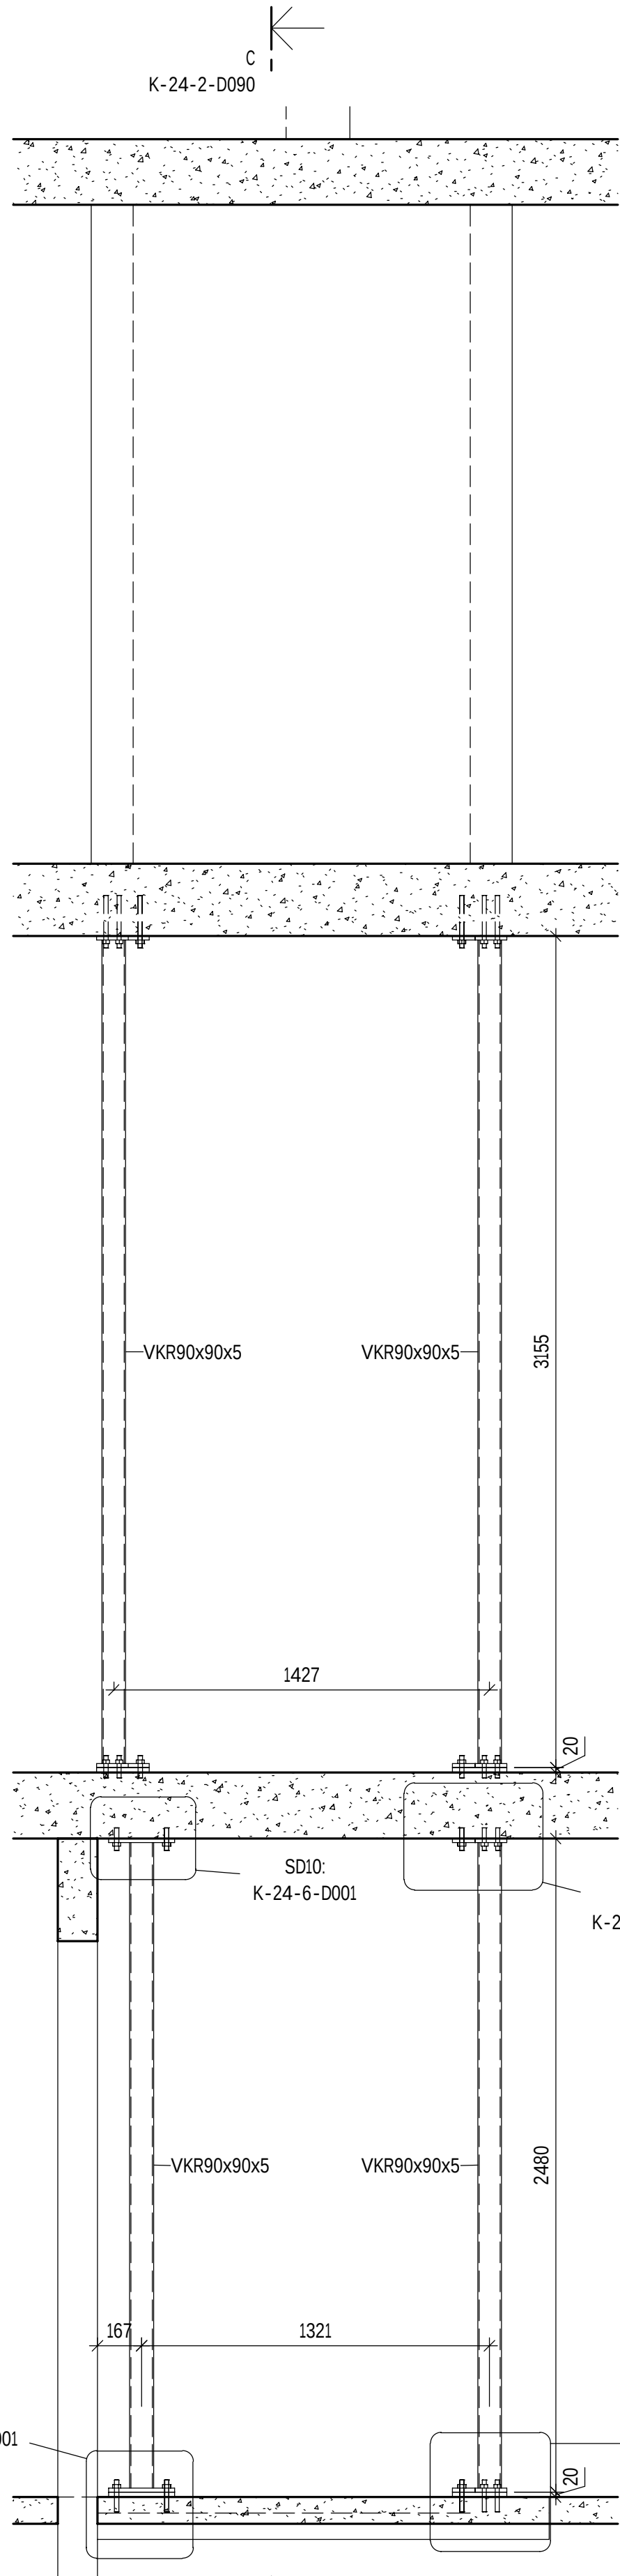


A-A
1 : 20

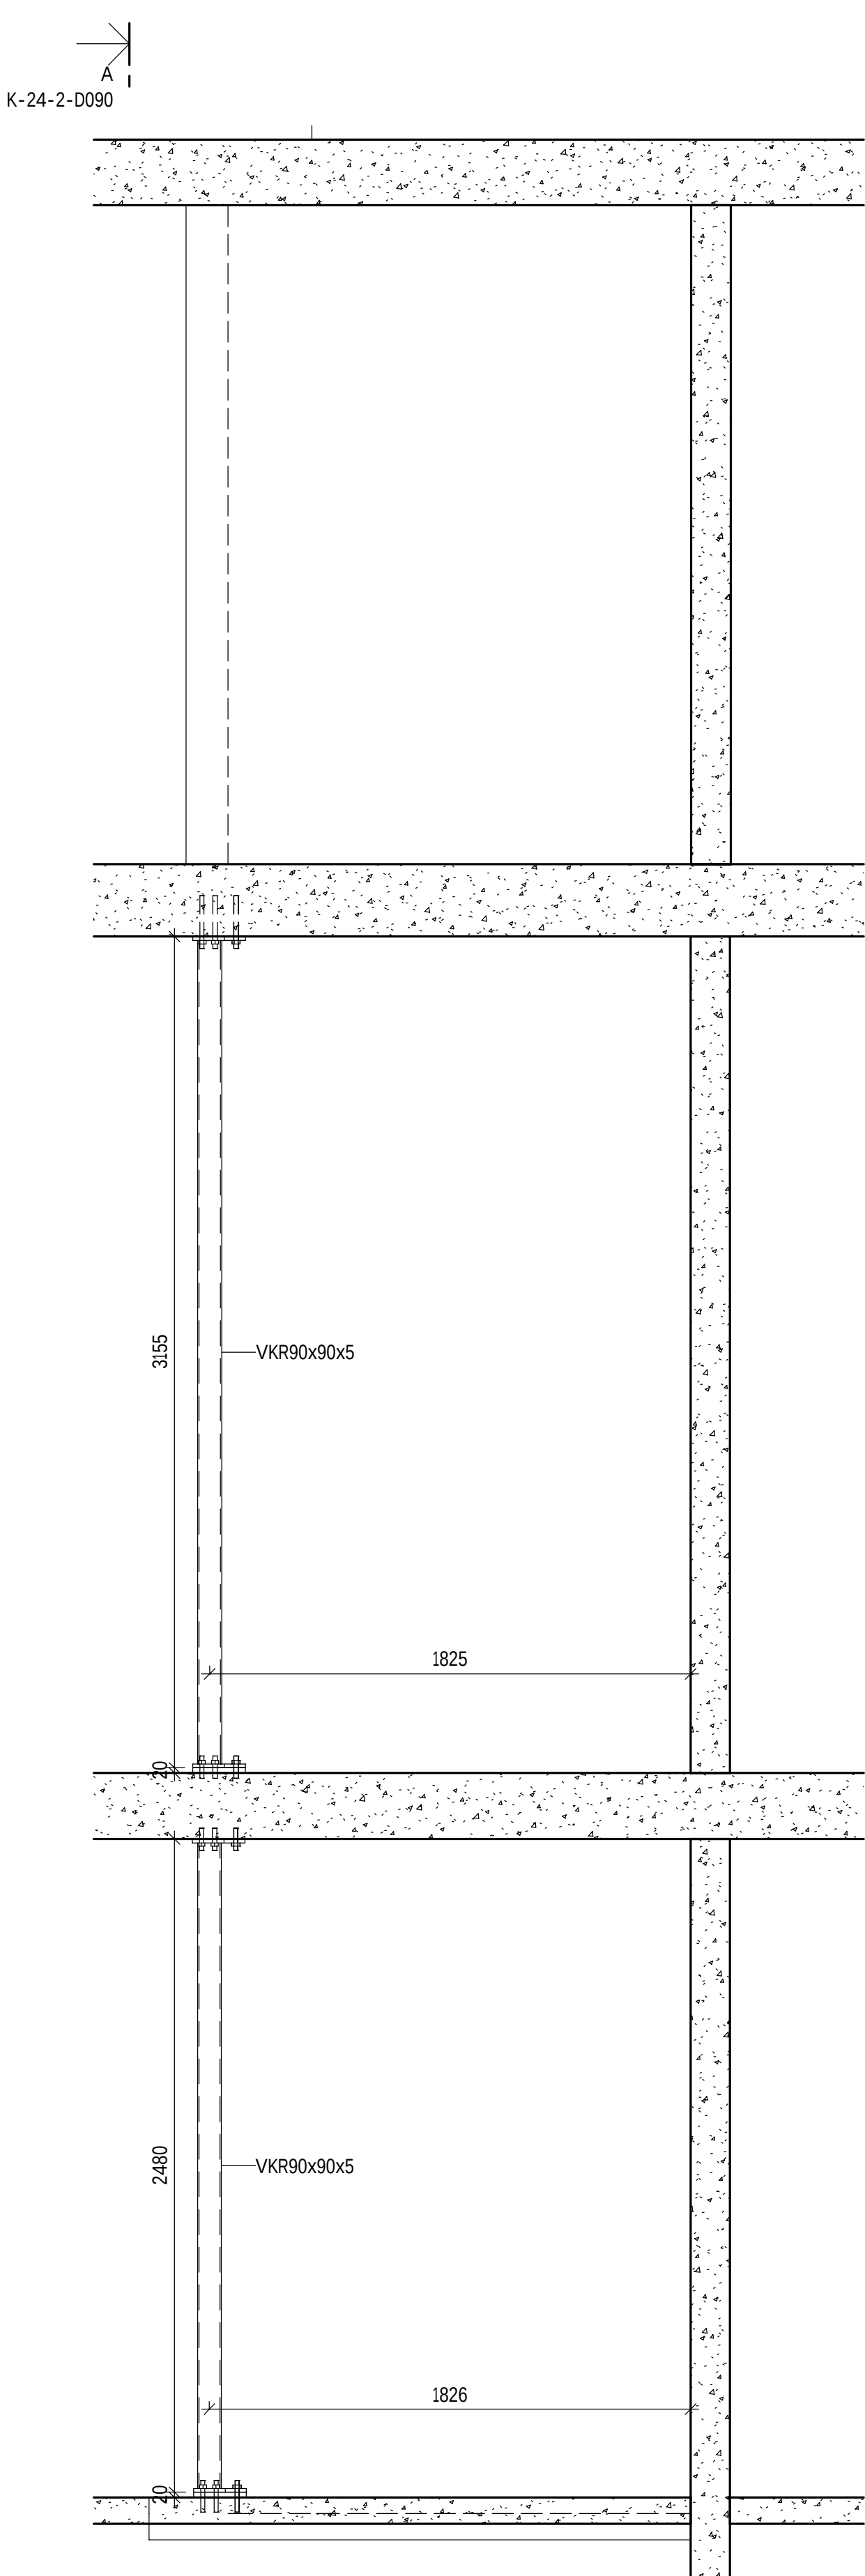


B-B
1 : 20

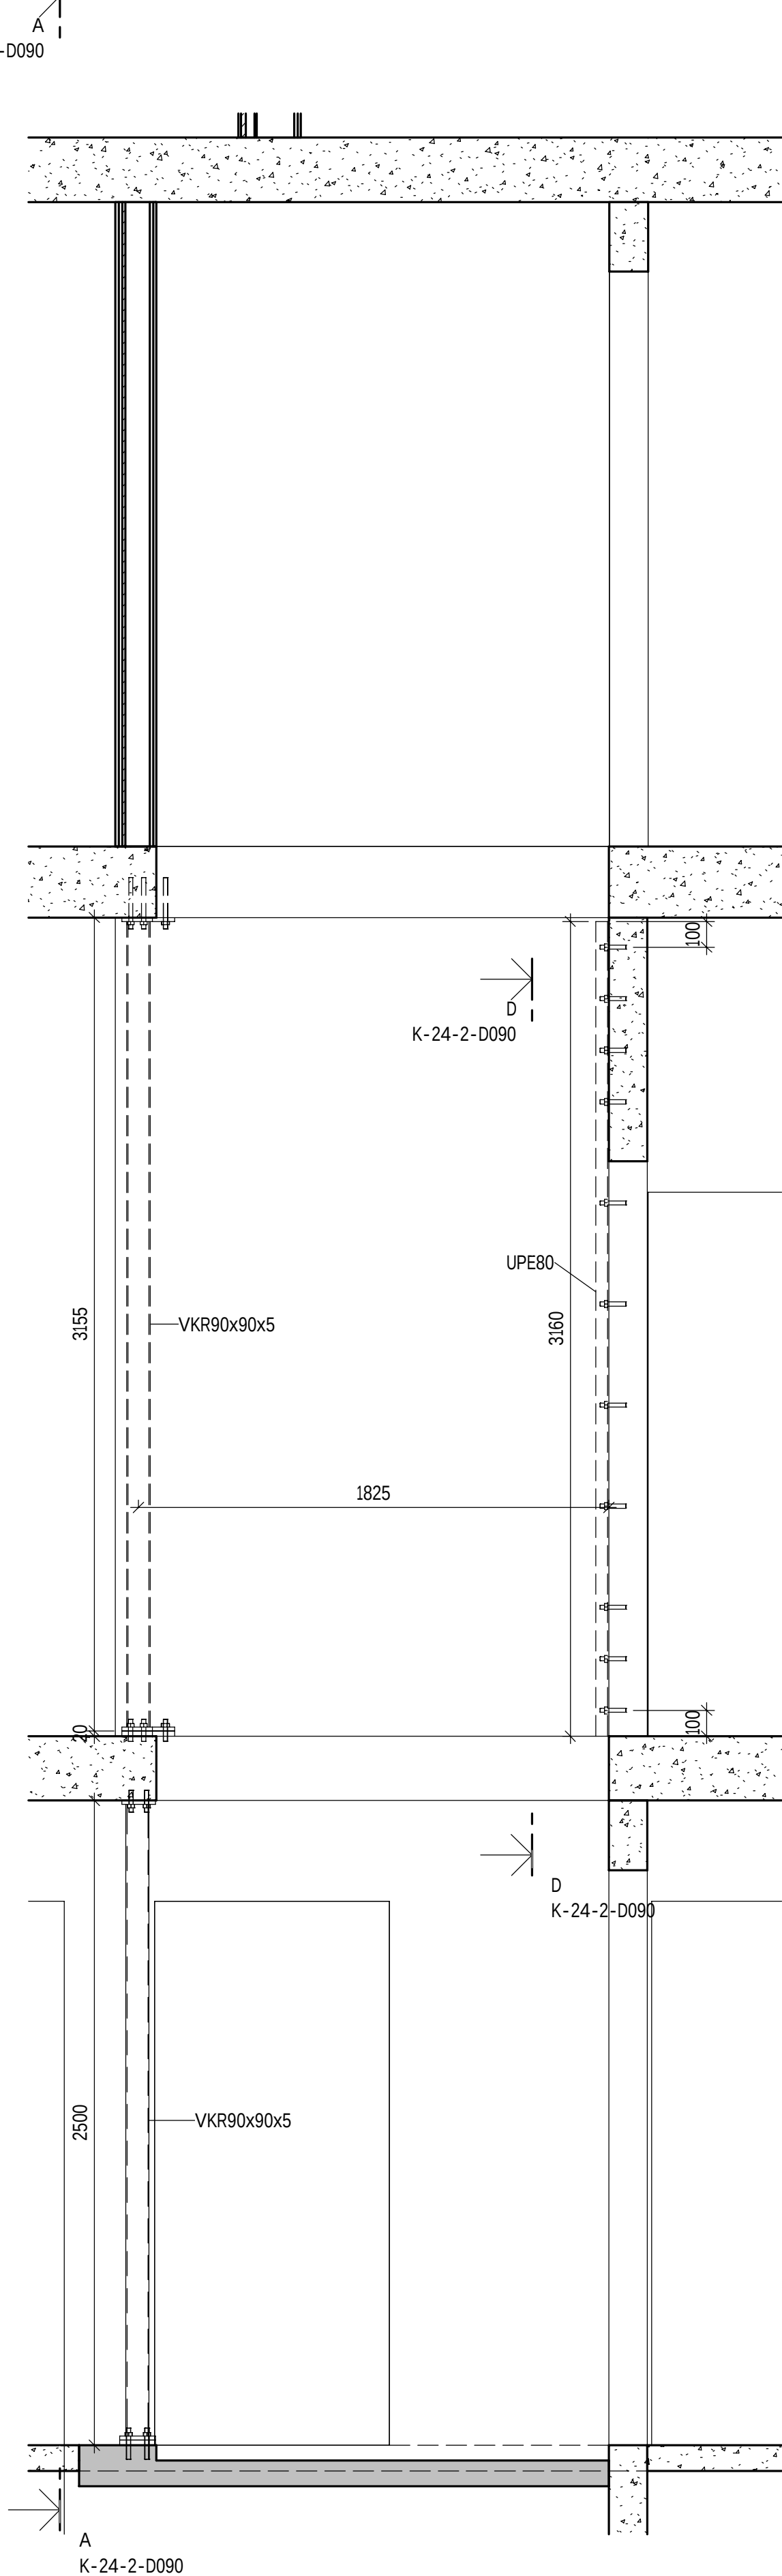

C-C
1 : 20

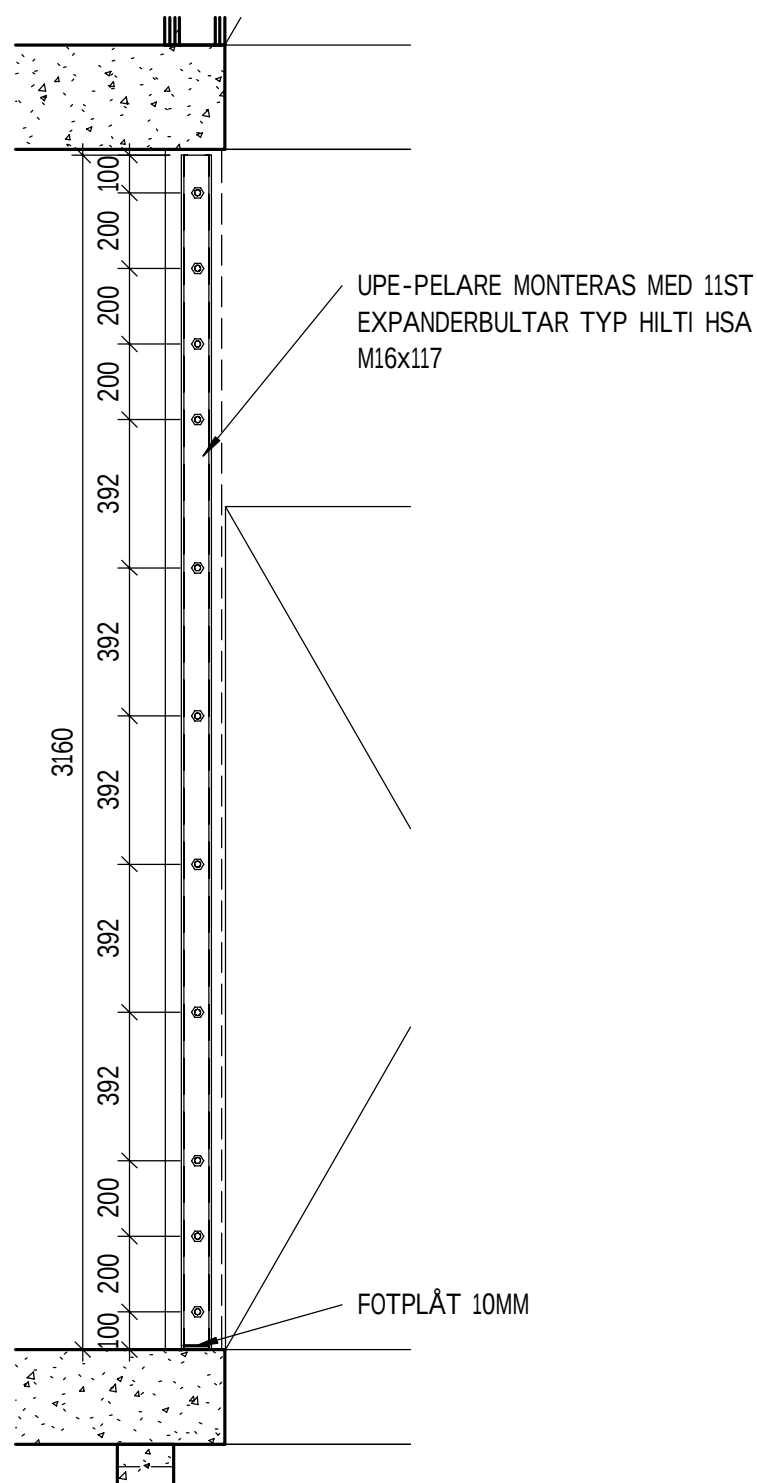

D-D
1 : 20

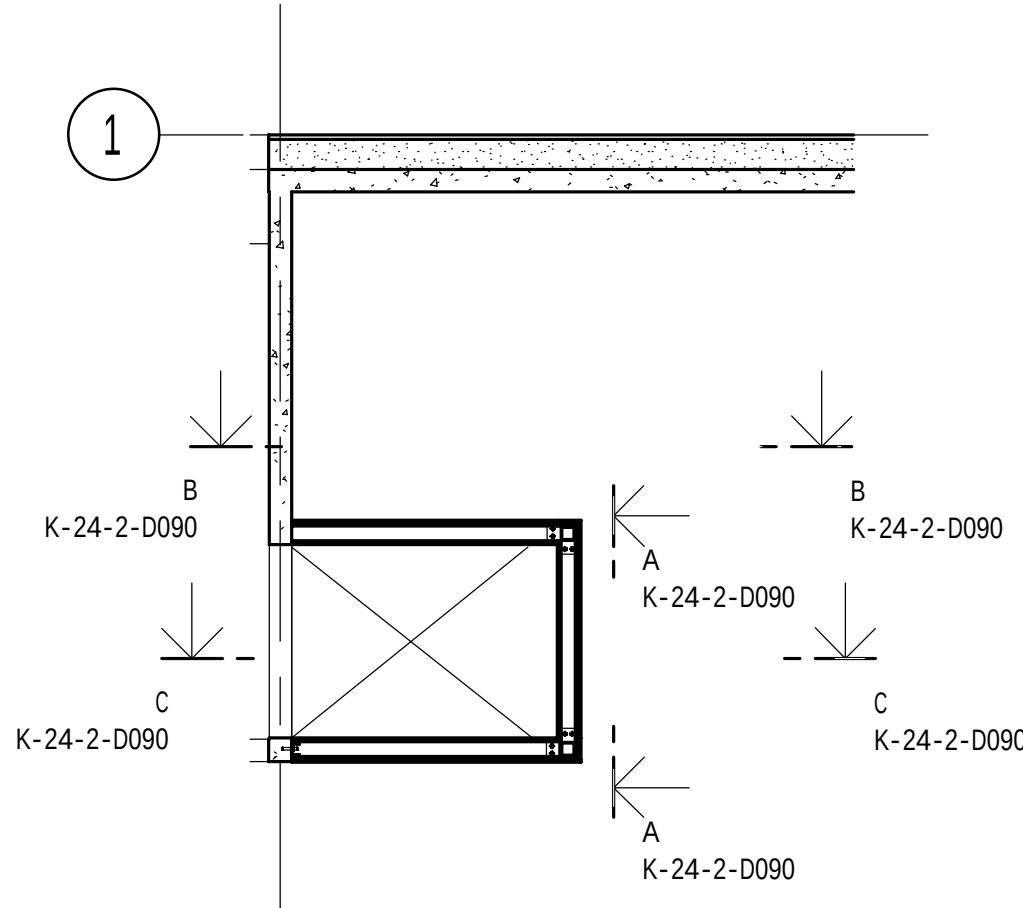

PLAN STÅLSEKTIONER HISS
1 : 50

FÖRESKRIFTER

ALLMÄNNA ANVISNINGAR K-01-1-D001

FÖRKLARINGAR

	BEFINTLIG BETONG
	PLATSGJUTEN BETONG
	BEFINTLIG LÄTTBETONG
	DRÄNERANDE PORDRÅN
	CELLPLAST EPS
	CELLPLAST XPS

HÄNVISNINGAR

1	GODKÄND	2025-02-26	MG
BET	ÄNDRING AVSER	DATUM	SIGN
FÖRFRÅGNINGSUNDERLAG			
BYGGHANDLING			
2025-02-26	GODKÄND	ÄNDRING	STATUS
CENTRUMHUSET HUS D			
KRÅKAN 1, ROBERTSFORS			
ÄF-Infrastructure AB			
Strandgatan 9A			
891 39 Örnsköldsvik			
Tel: 010-505 00 00			
MARCUS GRANQVIST	MARCUS GRANQVIST	SKAPAD AV	ANSVARIG PART
ROBIN ÖSTMAN	D0192211	UPPRAGSNUMMER	RITNINGSKATEGORI
OMBYGGNAD BIBLIOTEK OCH LÄGENHETER			
KÄLLARE			
STÅLELEVATIONER			
K-24-2-D090			