



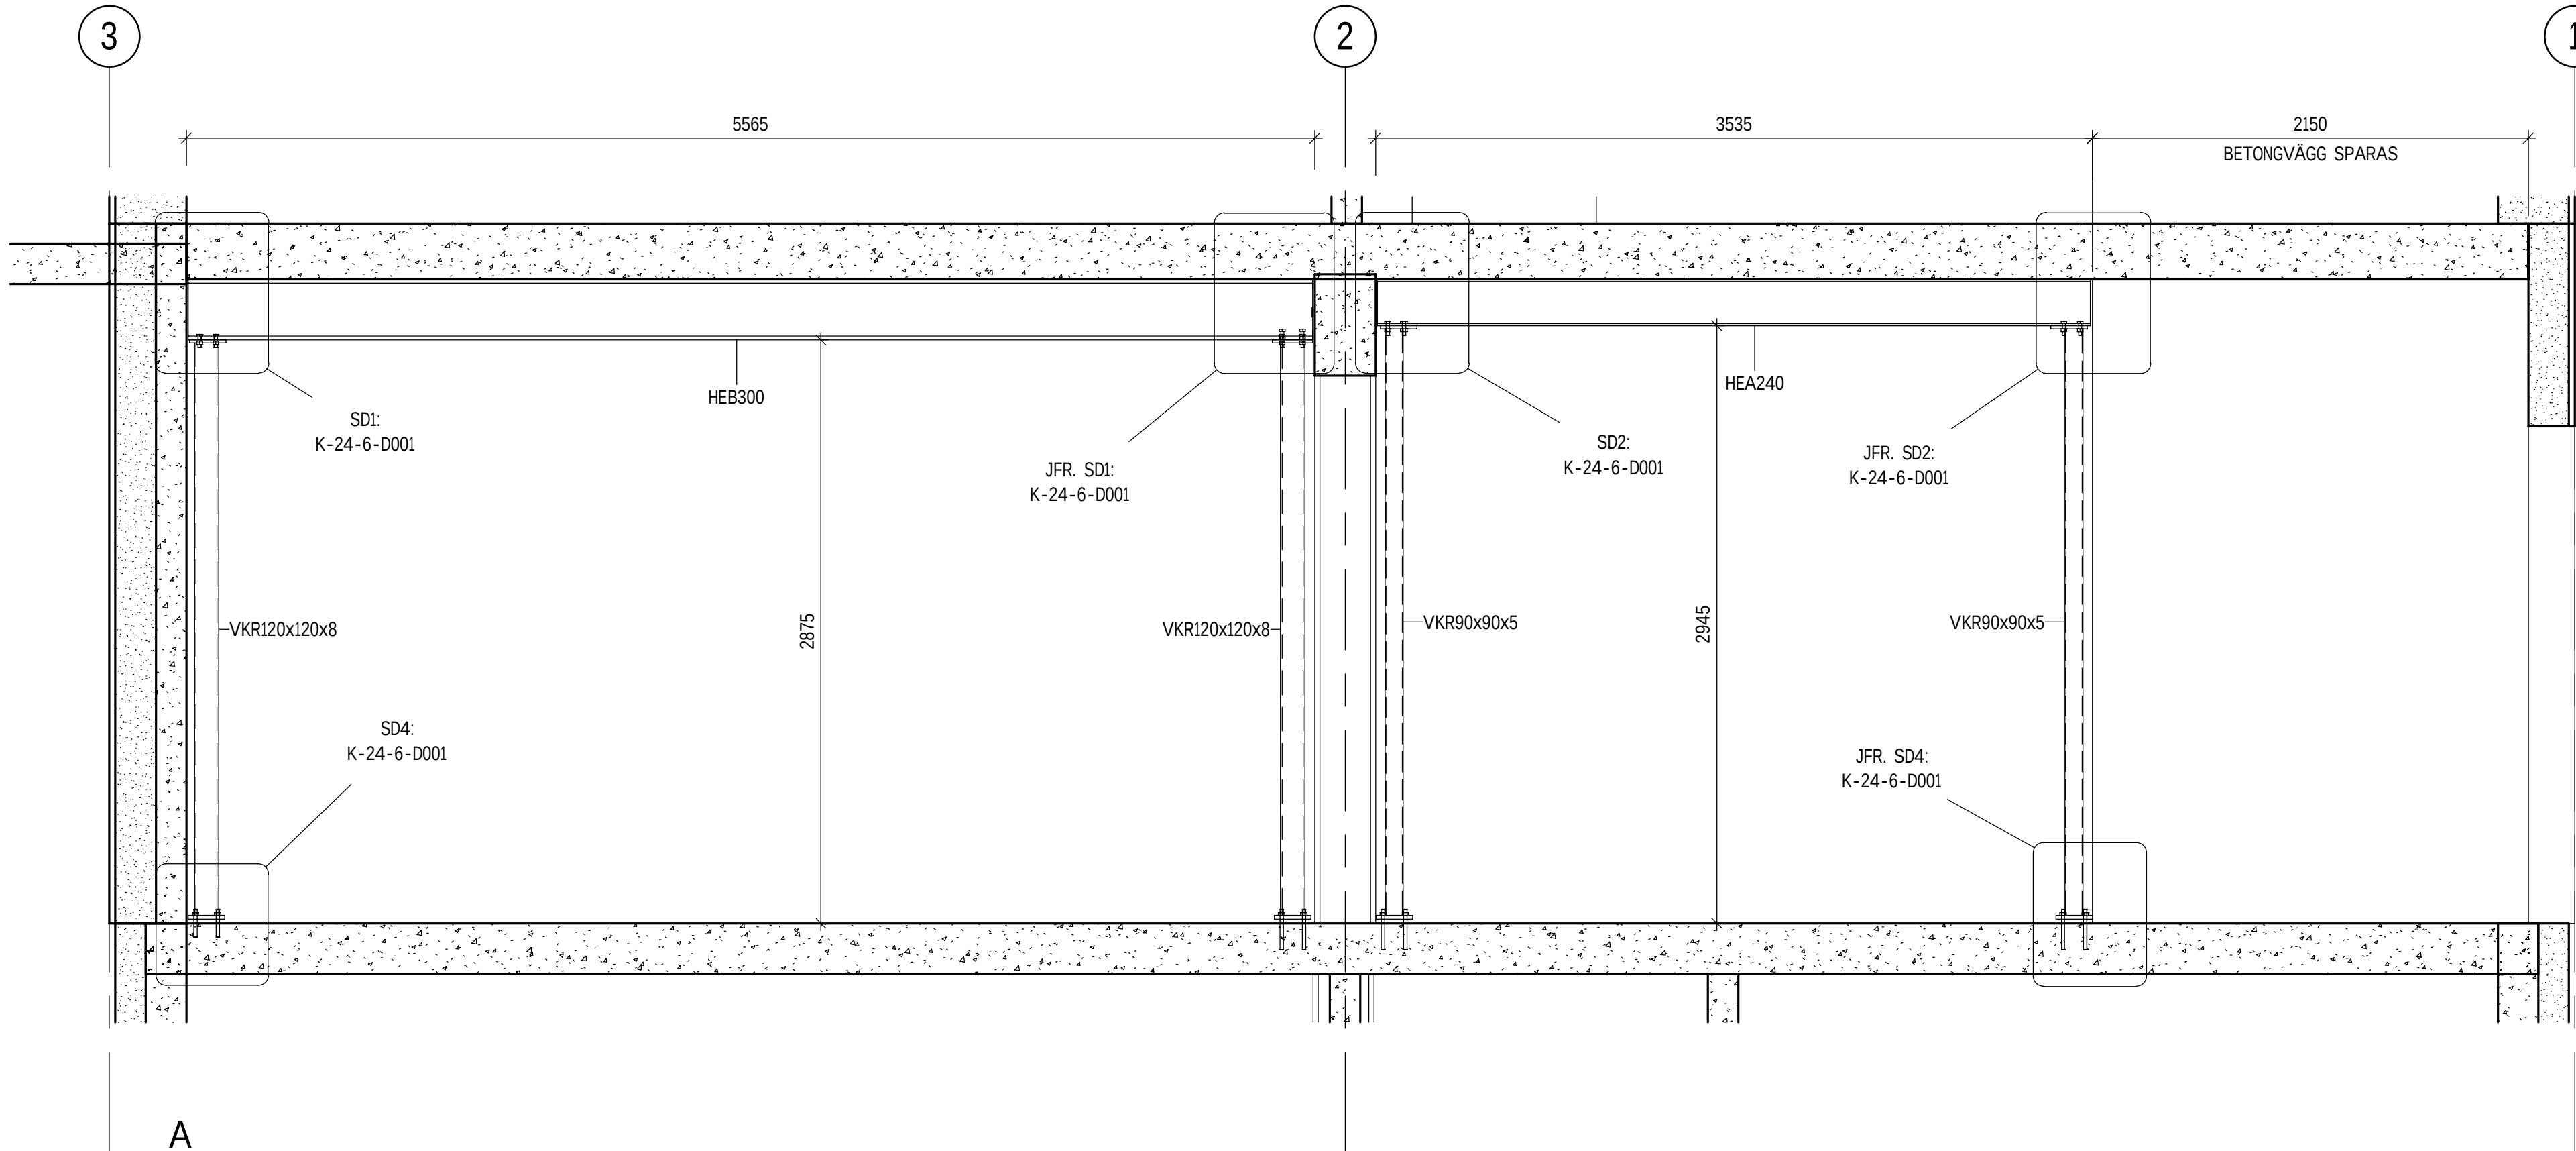

A
1 : 25

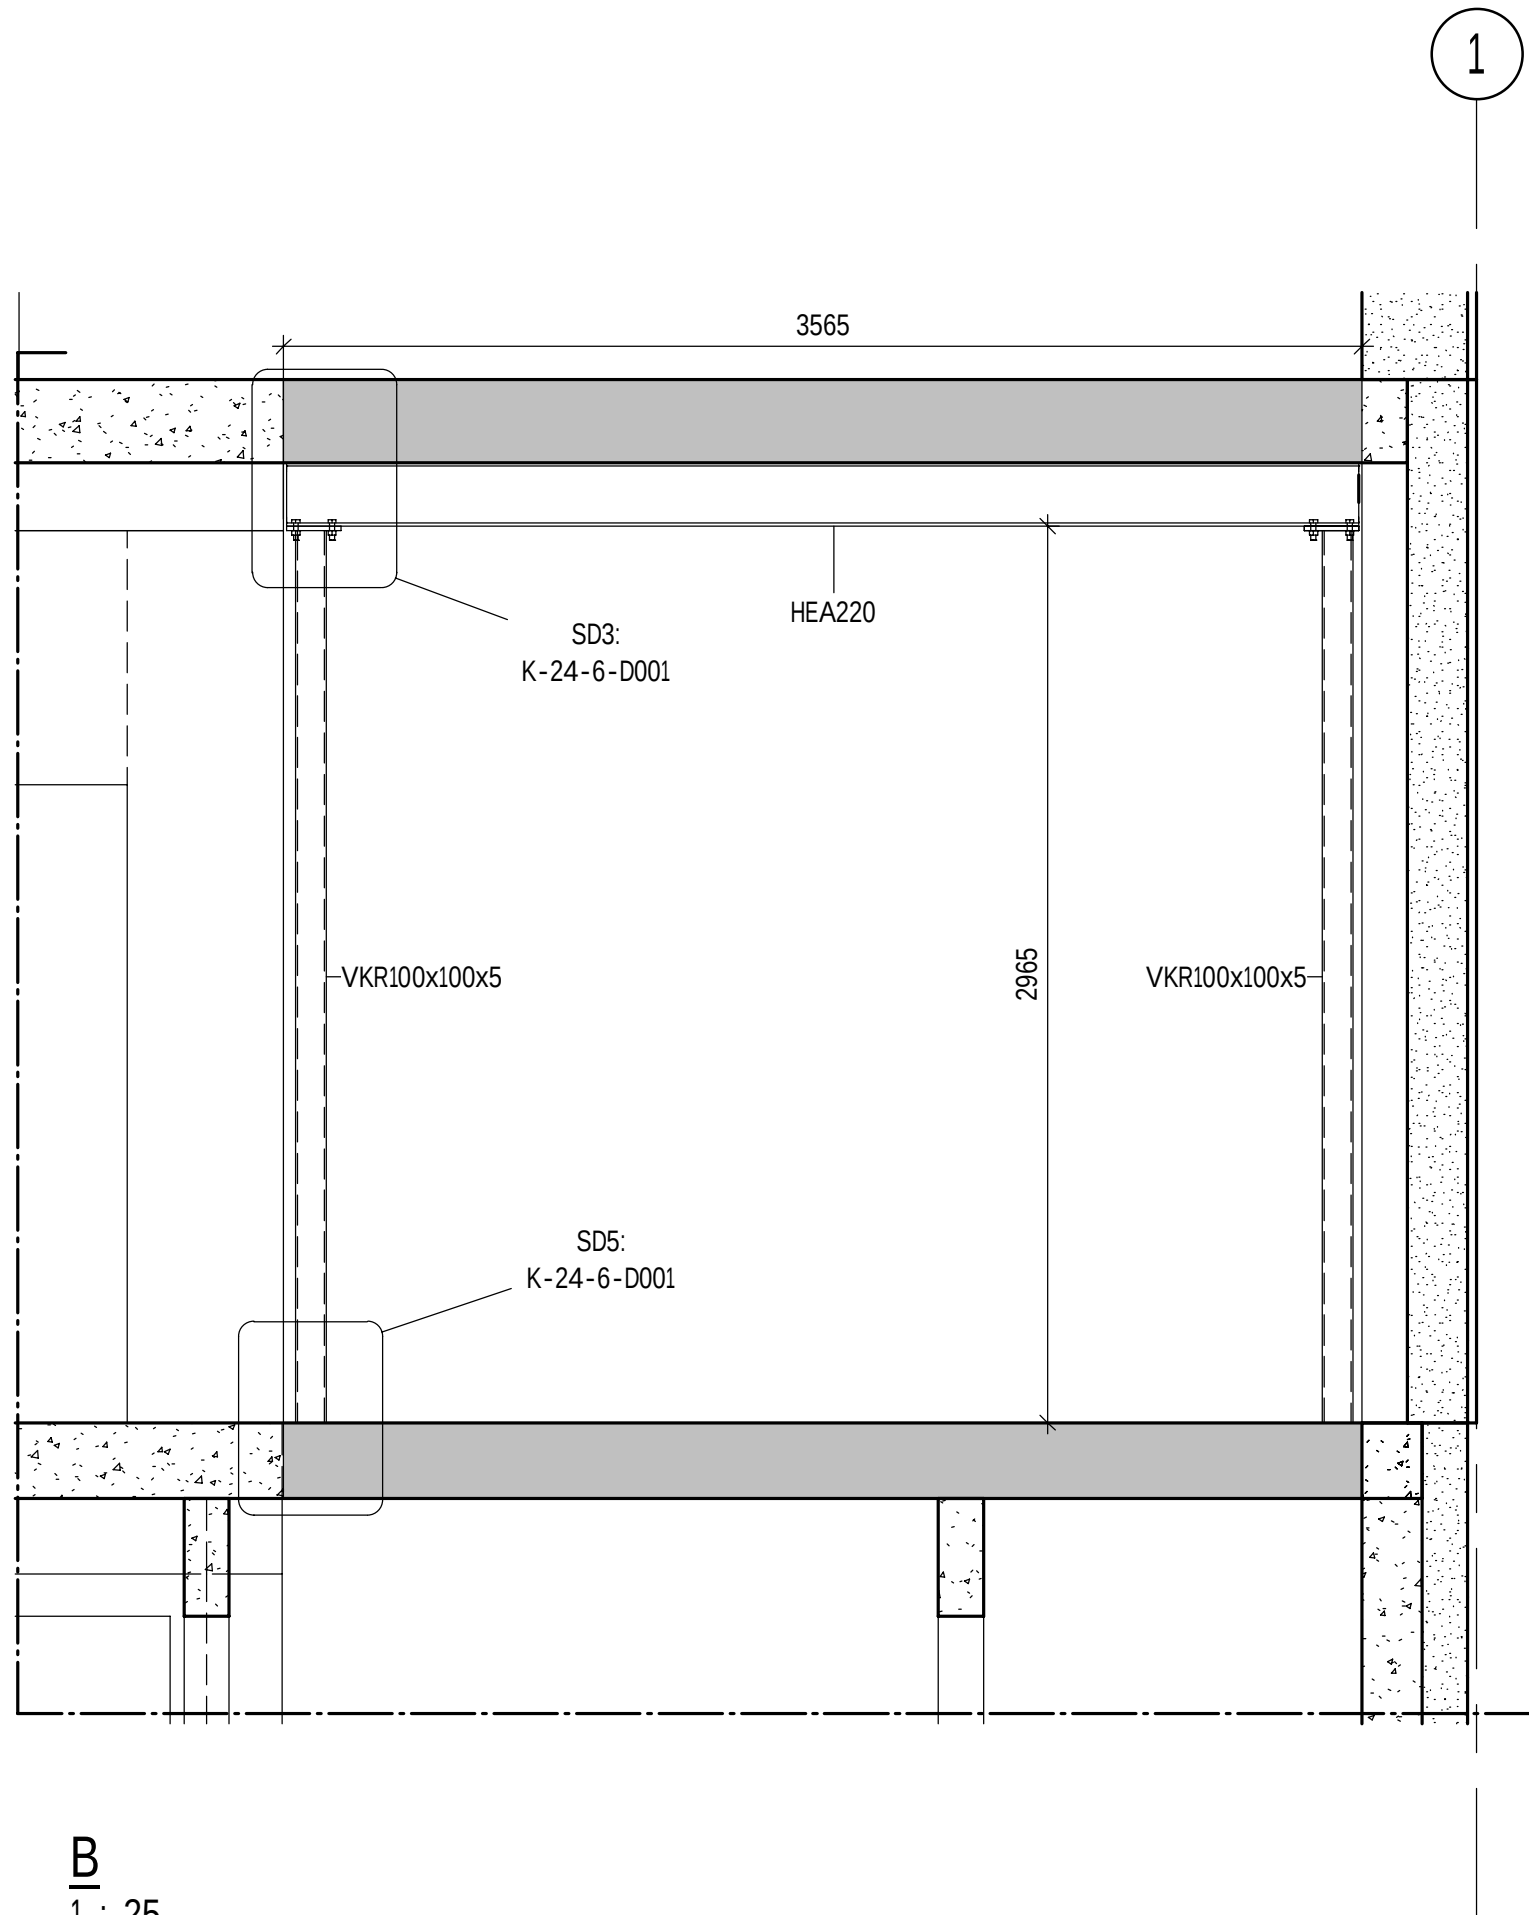

B
1 : 25

FÖRESKRIFTER

ALLMÄNNA ANVISNINGAR K-01-1-D001

FÖRKLARINGAR

	BEFINTLIG BETONG
	PLATSGJUTEN BETONG
	BEFINTLIG LÄTTBETONG
	DRÄNERANDE PÖRDRÄN
	CELLPLAST EPS
	CELLPLAST XPS

ARBETSORDNING, NYTT STÅL LINJE C.

- STÄMPNING MED BÄRLINA MONTERAS PÅ BÅDA SIDOR OM BETONGVÄGG.
- RIVNING AV BEFINTLIG BETONGVÄGG
- UPPBYGGNAD AV NYTT STÅL ENL. HANDLING.

STÅL BRANDSKYDDAS FÖR BRANDTEKNISK
KLASS R60

VKR-PELARE BRANDSKYDDSMÅLAS MED ELD OCH VATTEN CON-RFB DFT 1086μ
ELLER LIKV.

HEA-BALK BRANDSKYDDSMÅLAS MED ELD OCH VATTEN CON-RFB DFT 1001μ
ELLER LIKV.

HEB-BALK BRANDSKYDDSMÅLAS MED ELD OCH VATTEN CON-RFB DFT 982μ
ELLER LIKV.

HÄNVISNINGAR

SKALA 1:1

0 10 20
MILLIMETER

50

100

1	GODKÄND	2025-02-26	MG
BET	ÄNDRING AVSER	DATUM	SIGN
FÖRFRÅGNINGSUNDERLAG			
BYGGHANDLING			
2025-02-26	GODKÄND	ÄNDRING	STATUS
CENTRUMHUSET HUS D KRÅKAN 1, ROBERTSFORS			
ÄF-Infrastructure AB Strandgatan 9A			
891 39 Örnsköldsvik MARCUS GRANQVIST			
991 010-505 00 00 JOEL OLOFSSON			
ROBIN ÖSTMAN			
D0192211			
OMBYGGNAD BIBLIOTEK OCH LÄGENHETER			
PLAN 1			
STÅLELEVATIONER			
K-24-2-D100			