


GODKÄND		STATUS
FÖRFRÅGNINGSUNDERLAG		HANDLING
DATUM 2025-02-26	ÄNDRING/PM	ÄNDRING
CENTRUMHUSET HUS D KRÅKAN 1, ROBERTSFORS		PROJEKT
ÅF-Infrastructure AB Storgatan 103 921 32 Lycksele Tel: 010-505 00 00		ANSVARIG PART
CONNY LARSSON	GABRIEL STENLUND	SKAPAD AV
GODKÄND AV	UPPDRAGSNUMMER D0191802 (210550)	UPPDRAGSNUMMER
PLANRITNING		RITNINGSKATEGORI
OMBYGGNAD BIBLIOTEK OCH LÄGENHETER PLAN 1 TR, PLAN 2, DEL 1 KANALISATION, PUS, TELE OCH SÄKERHET		FORMAT A1
E-61-1-D201		SKALA 1:50
		NUMMER BET

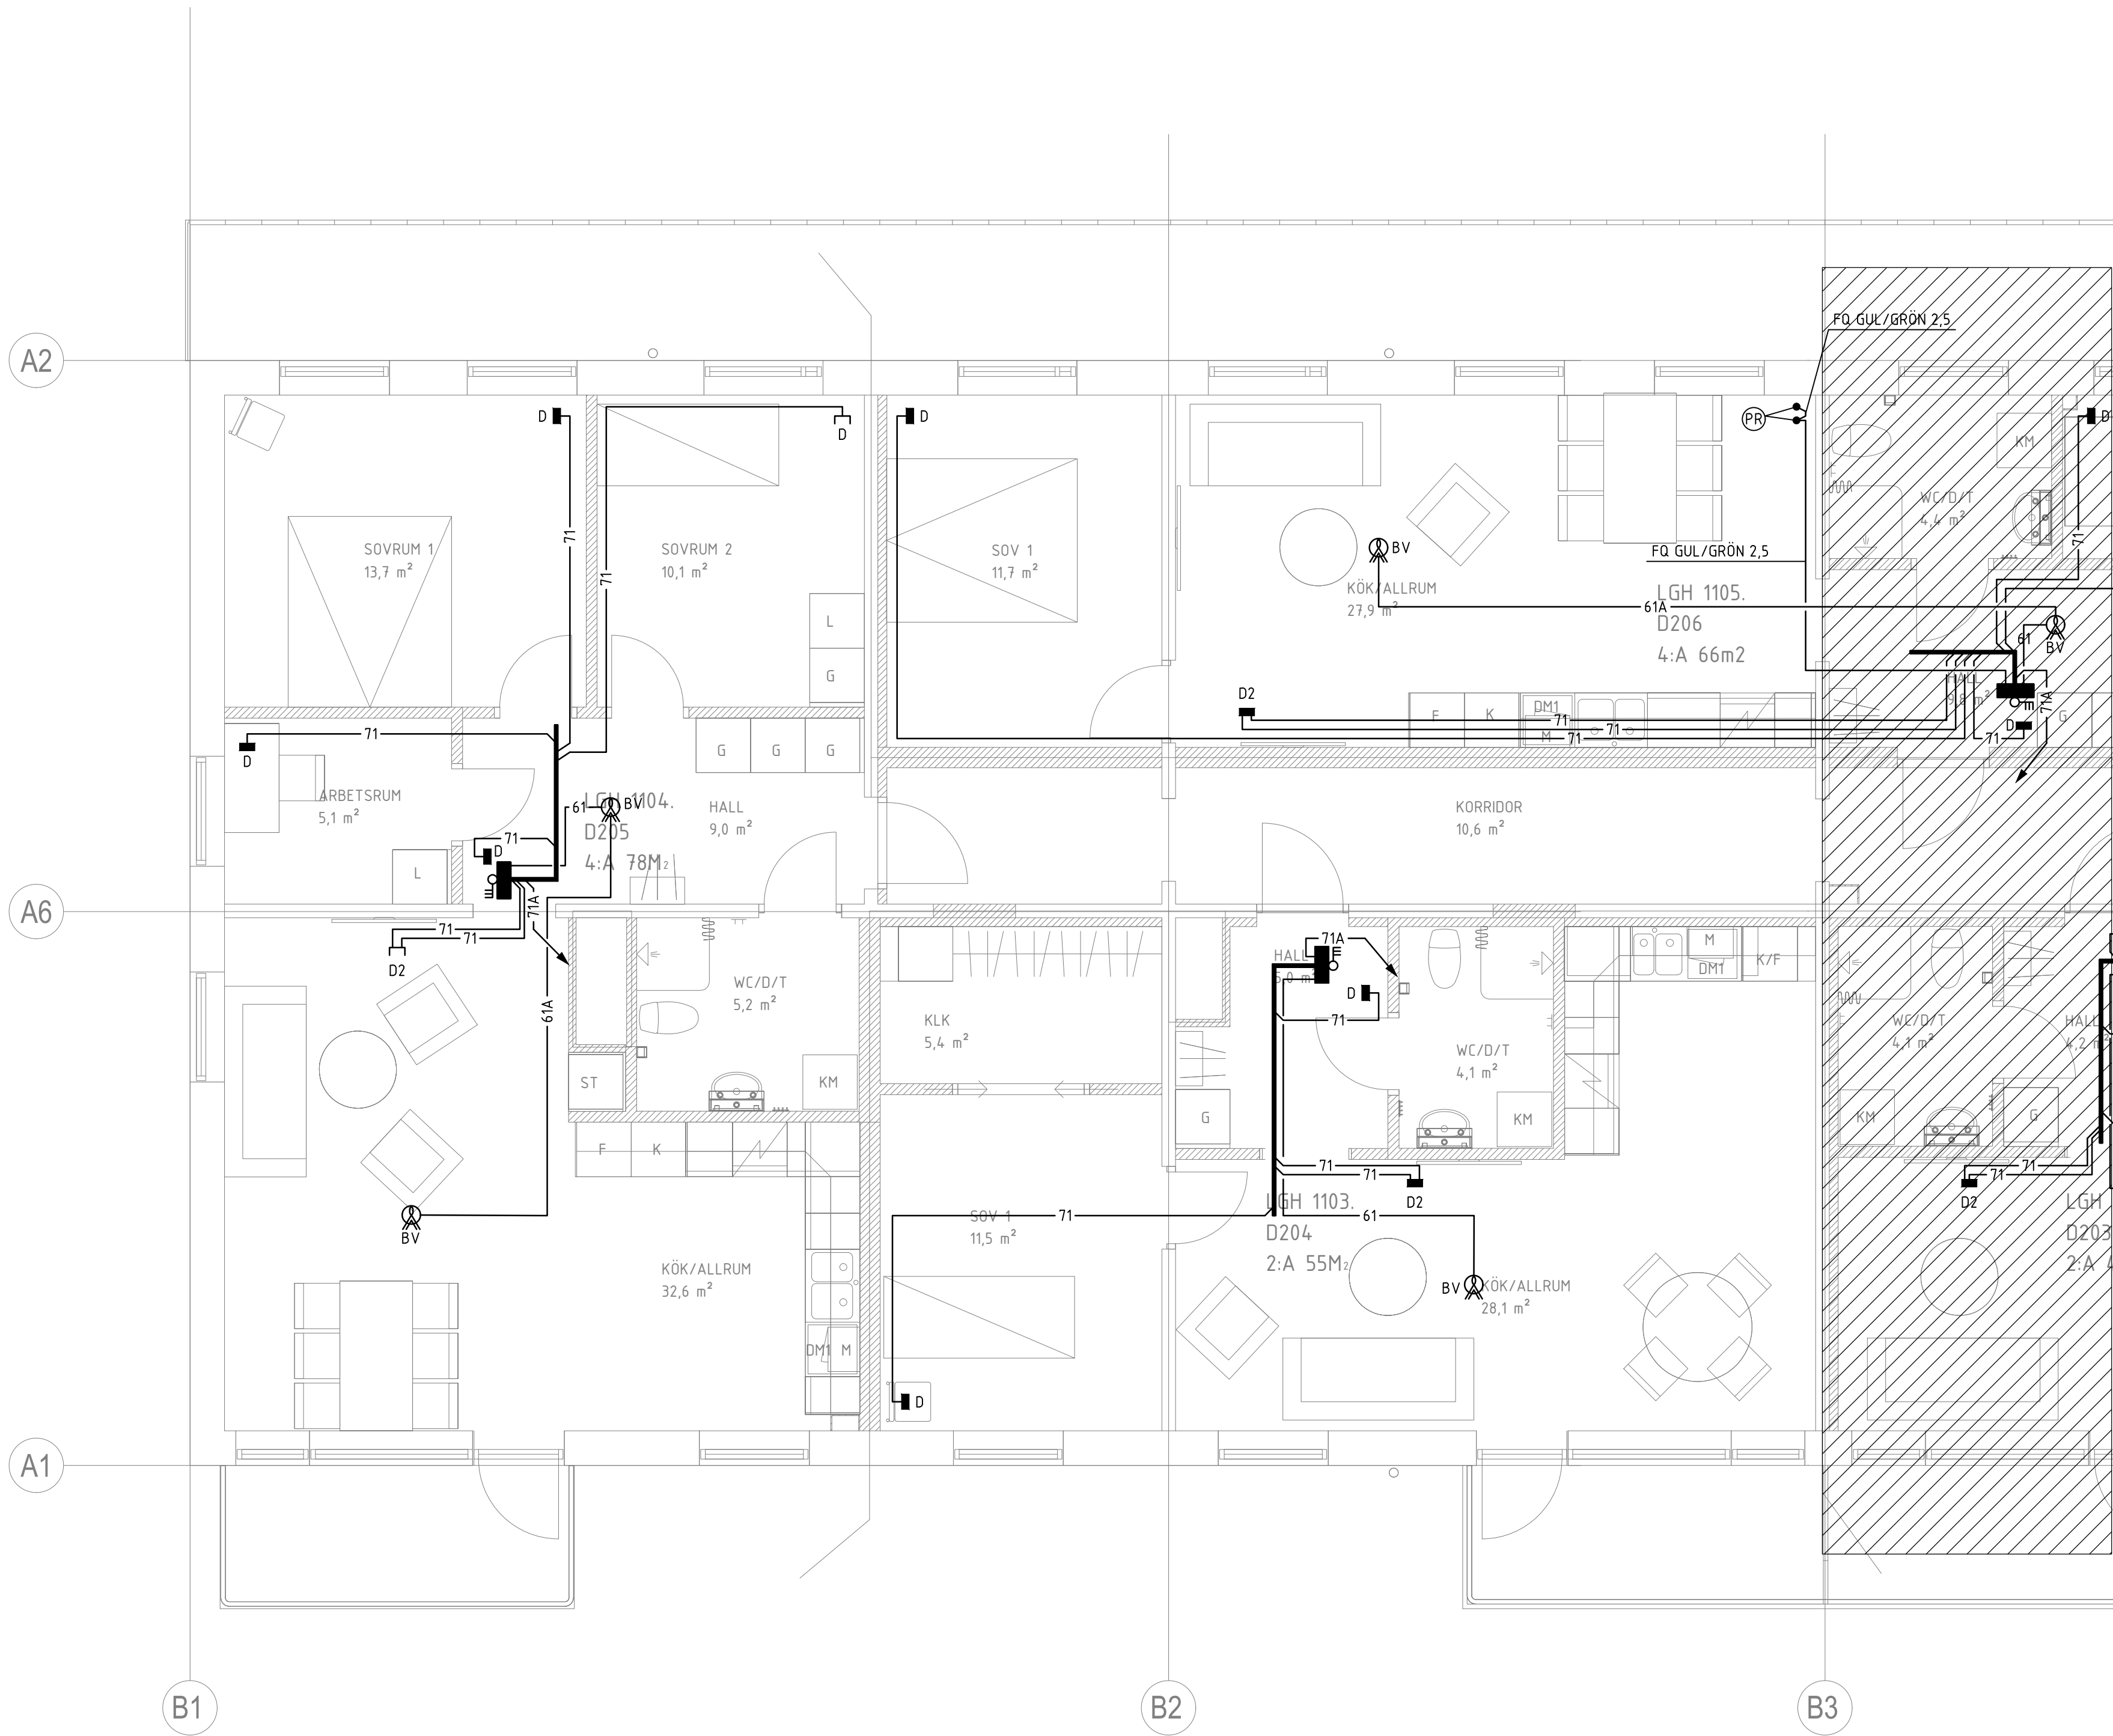