



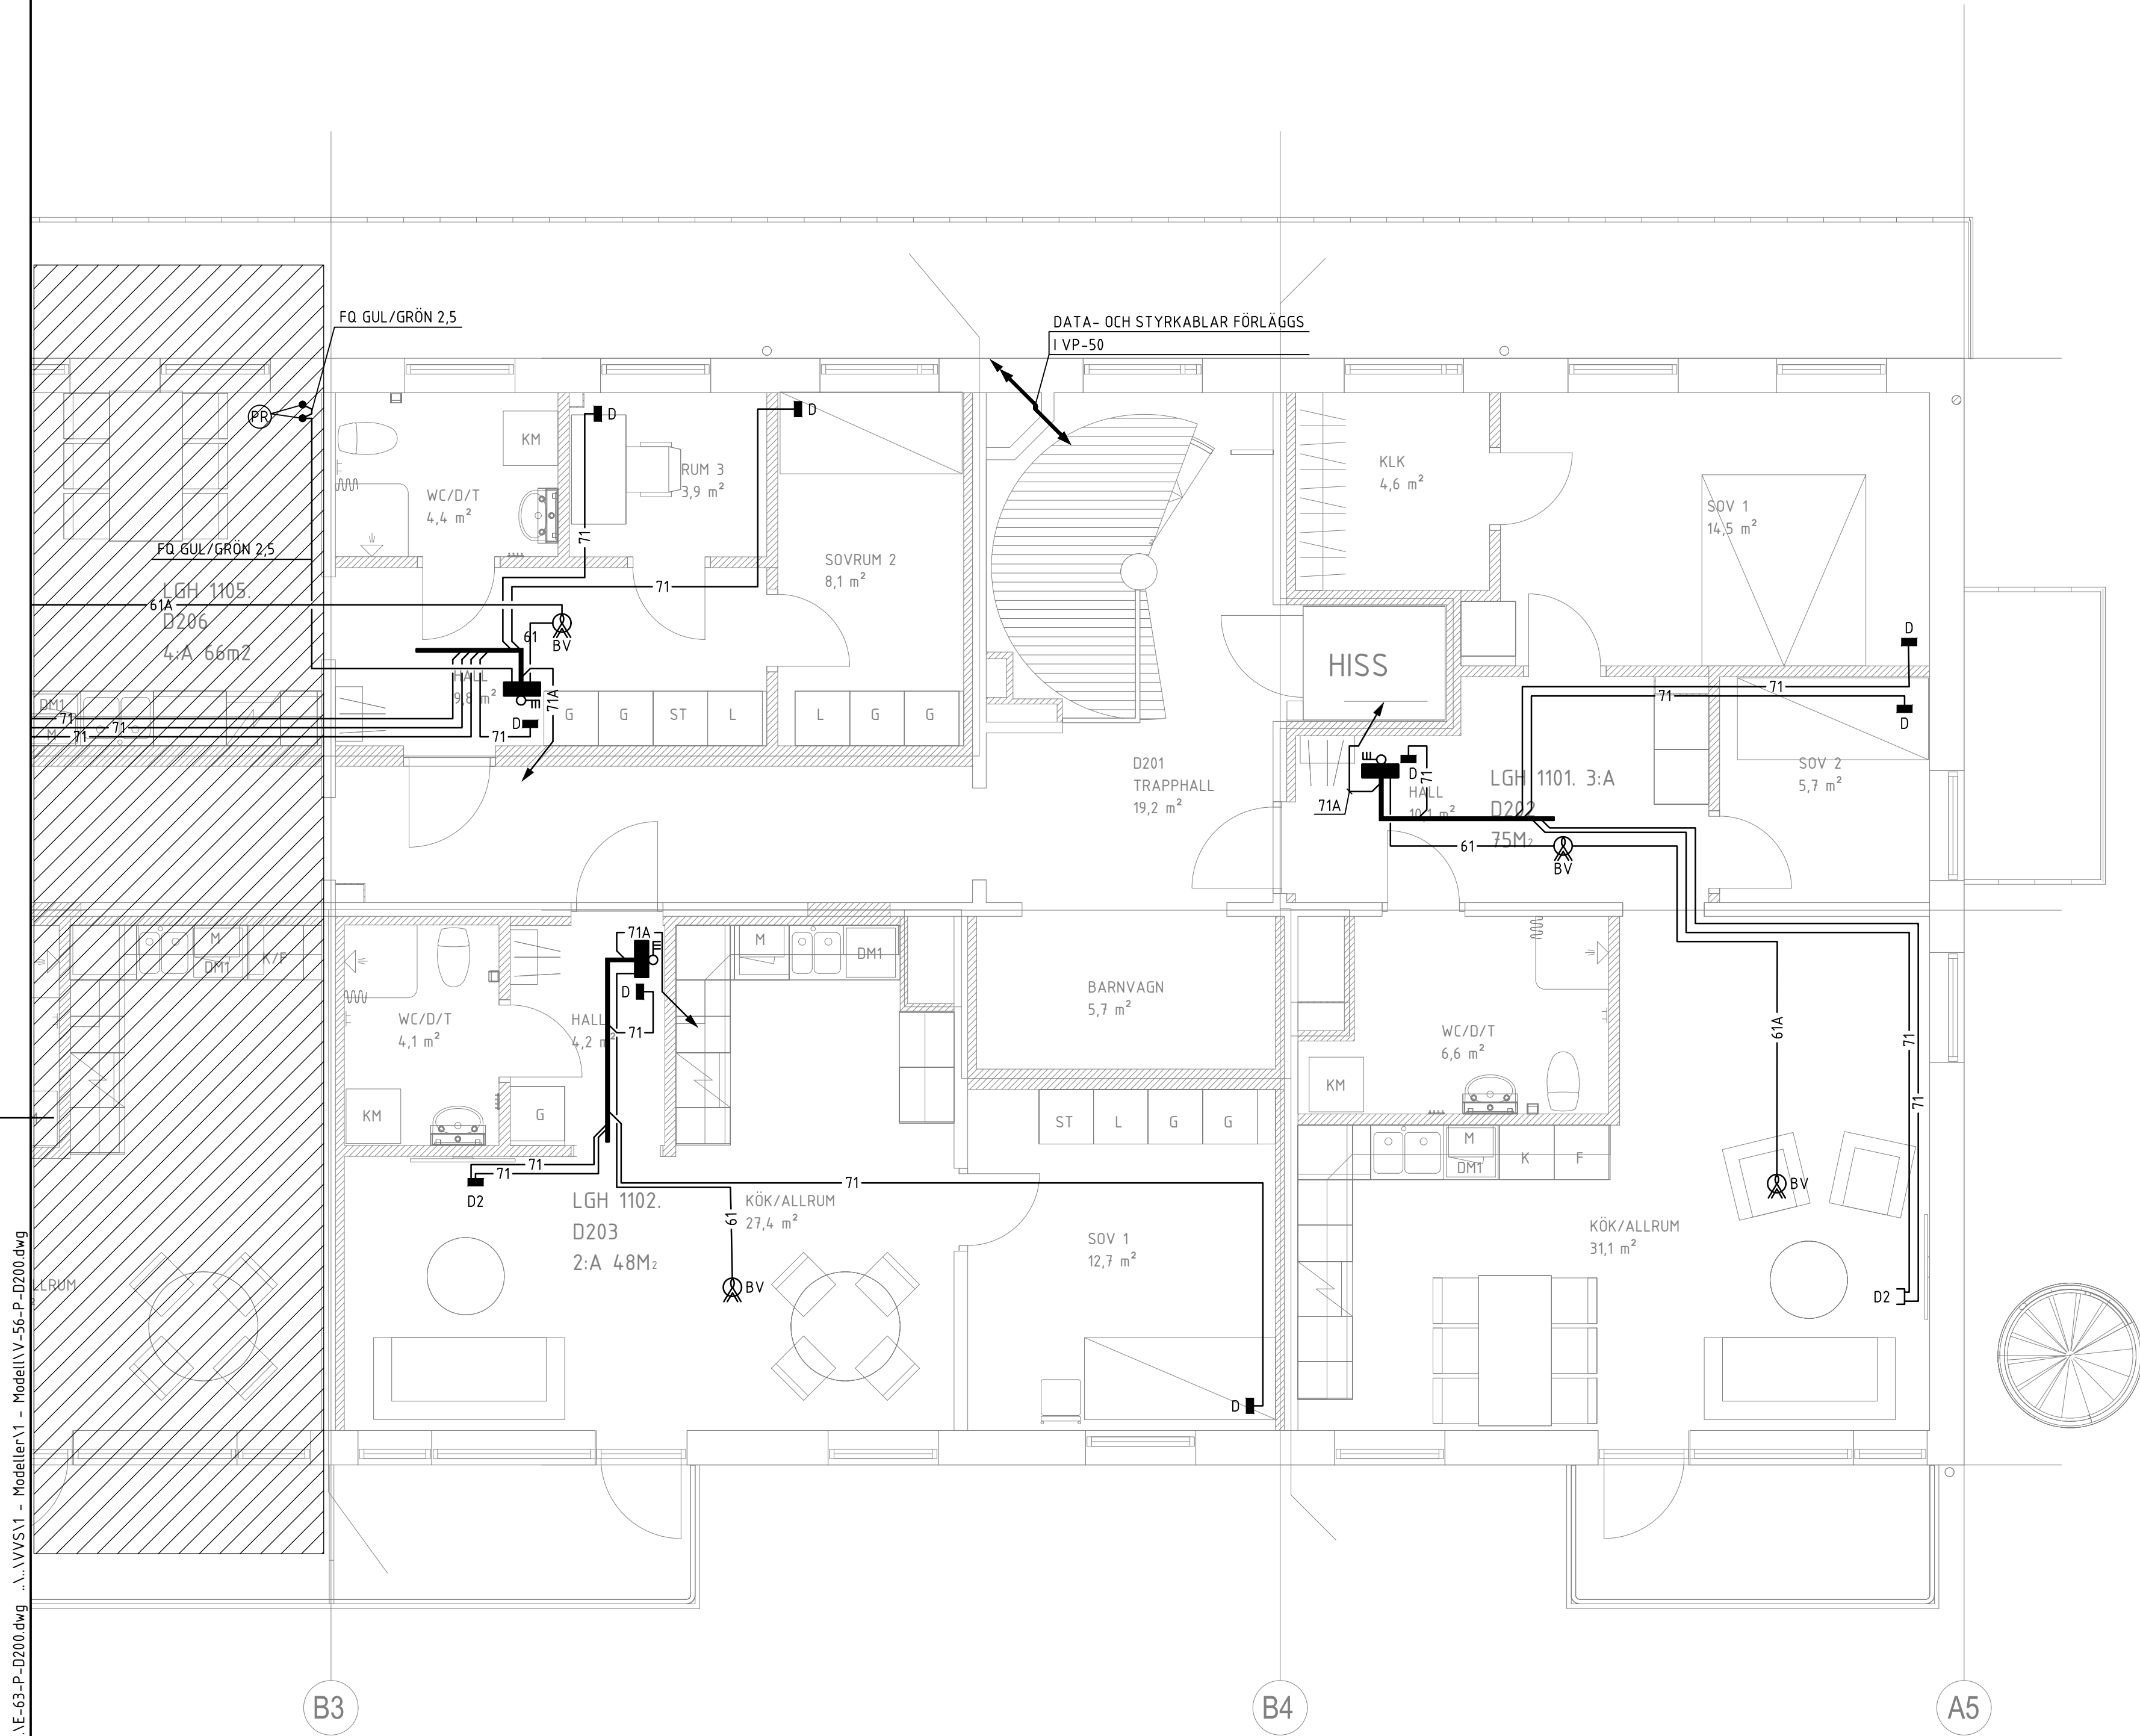

\\NA1 - Modeller\Export\DWG\A-40-P-D200.dwg \_VE-43-P-D200.dwg \_Förklaringar 2023-12-06.dwg \_VVS\1 - Modeller\1 - Modell\1 - 56-P-D200.dwg

LAGER: SB11

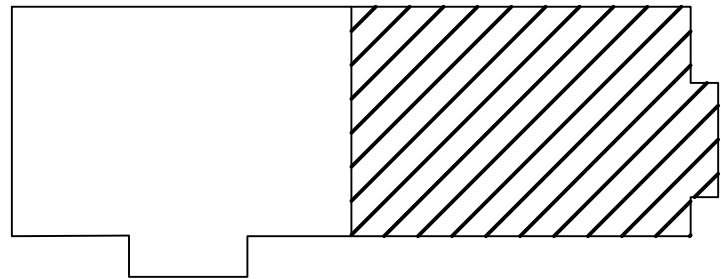

|   |               |                                     |
|---|---------------|-------------------------------------|
| GODKÄND                                                                                                |               | STATUS                              |
| FÖRFRÅGNINGSUNDERLÄG                                                                                   |               | HANDLING                            |
| DATUM<br>2025-02-26                                                                                    | ÄNDRING/PM    | ÄNDRING                             |
| CENTRUMHUSET HUS D<br>KRÅKAN 1, ROBERTSFORS                                                            |               | PROJEKT                             |
| ÅF-Infrastructure AB<br>Storgatan 103<br>921 32 Lycksele<br>Tel: 010-505 00 00                         |               | ANSVARIG PART                       |
| CONNY LARSSON                                                                                          | KONTAKTPERSON | GABRIEL STENLUND                    |
| CONNY LARSSON                                                                                          | GODKÄND AV    | UPPDRAGSNUMMER<br>D0191802 (210550) |
| PLANRITNING                                                                                            |               | RITNINGSKATEGORI                    |
| OMBYGGNAD BIBLIOTEK OCH LÄGENHETER<br>PLAN 1 TR, PLAN 2, DEL 2<br>KANALISATION, PUS, TELE OCH SÄKERHET |               | FORMAT<br>A1                        |
| E-61-1-D202                                                                                            |               | SKALA<br>1:50                       |
|   |               | BET                                 |