
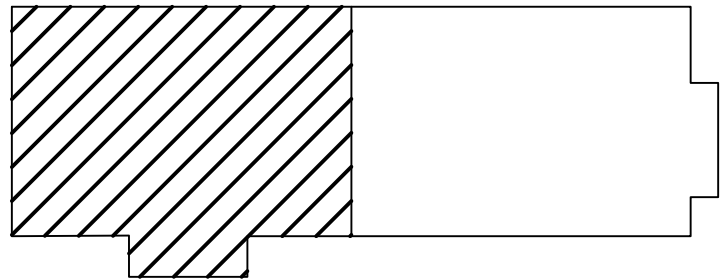


\\AFRY-Desktop\Bilder\Centrumhuset\Robban\DWG\A-40-P-D300-Centrumhuset\Inledning - Bygglöv-rv1-1-A-40-P-D300.dwg - AFRY Desktop\Bilder\Centrumhuset\Robban\DWG\A-40-P-D300-Centrumhuset\Inledning - Bygglöv-rv1-1-A-40-P-D300.dwg

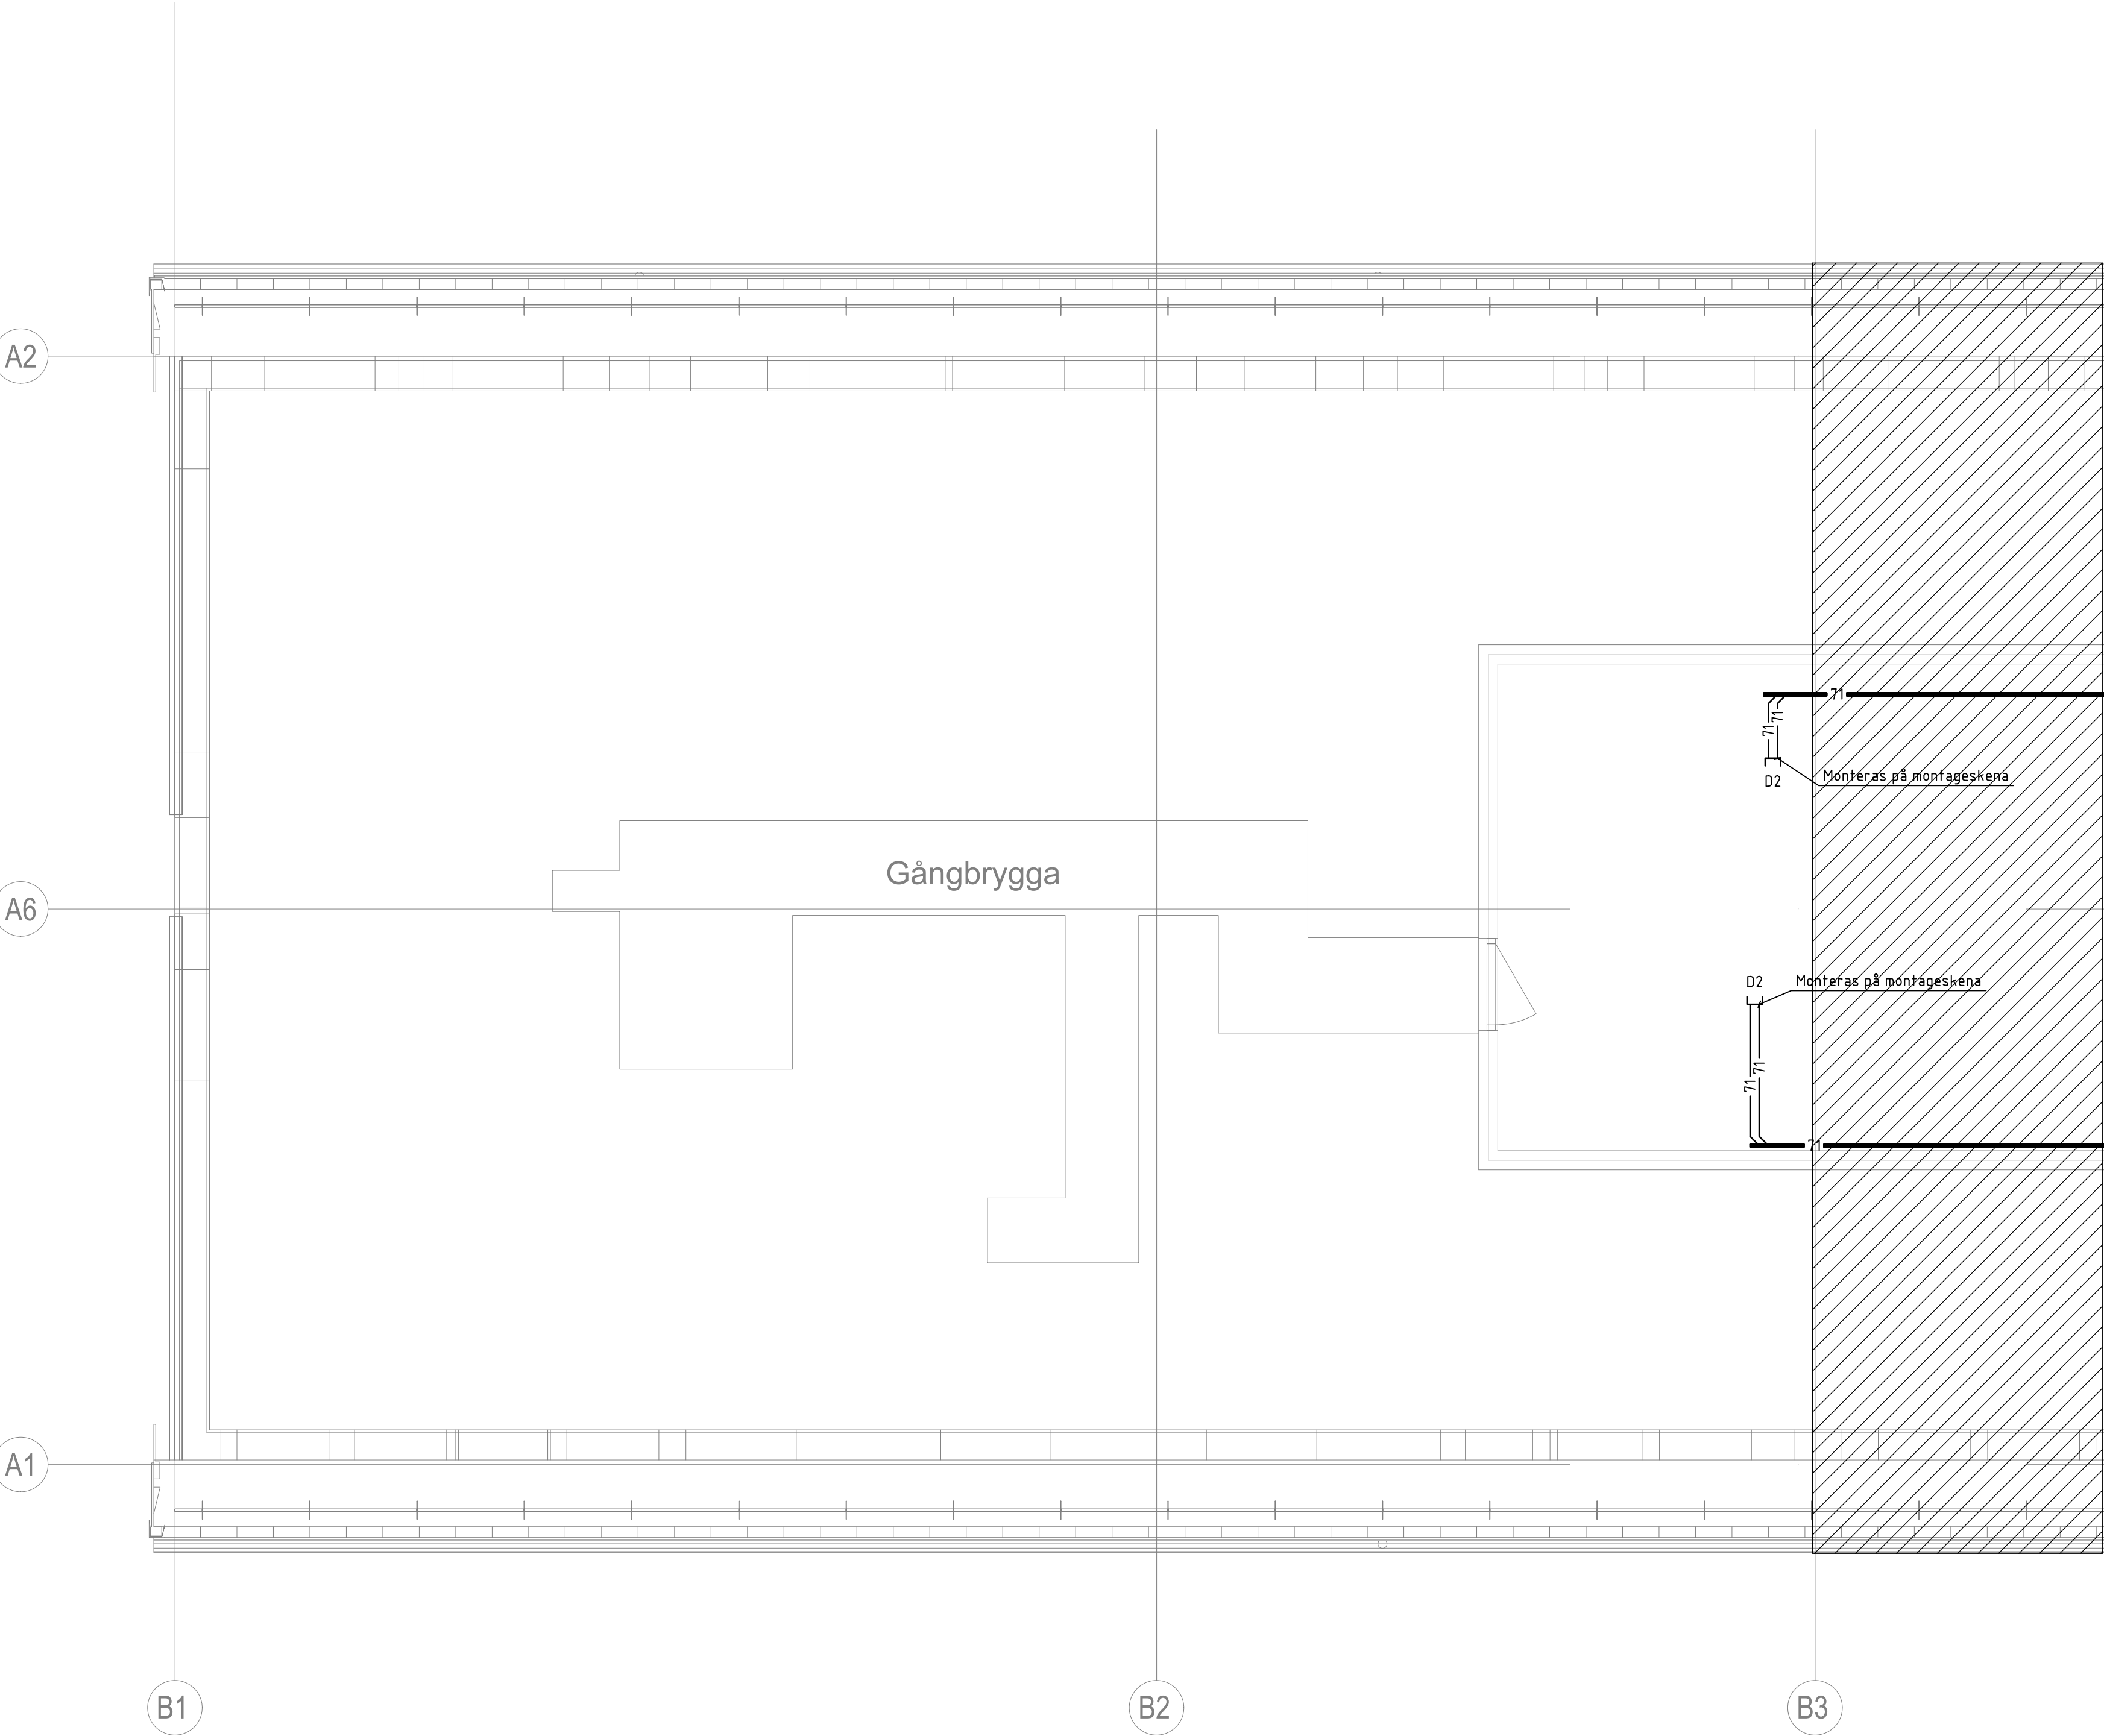

FÖRKLARINGAR

SE RITNING E-69-5-01

GODKÄND		STATUS
FÖRFRÅGNINGSUNDERLAG		HANDLING
DATUM 2025-02-26	ÄNDRING/PM	ÄNDRING
CENTRUMHUSET HUS D KRÅKAN 1, ROBERTSFORS		PROJEKT
ÅF-Infrastructure AB Storgatan 103 921 32 Lycksele Tel: 010-505 00 00		ANSVARIG PART
CONNY LARSSON	KONTAKTPERSON	GABRIEL STENLUND
CONNY LARSSON	GODKÄND AV	UPPDRAGSNUMMER D0191802 (210550)
PLANRITNING		RITNINGSKATEGORI
OMBYGGNAD BIBLIOTEK OCH LÄGENHETER VINDSVÄNING, PLAN 3, DEL 1 KANALISATION, PUS, TELE OCH SÄKERHET		FORMAT A1
E-61-1-D301		SKALA 1:50
		NUMMER BET

