



\\na1 - Modeller\Export\DWG\A-40-P-D090.dwg - AFRY Documents\A-40-P-D090-Lerfrunhuset\Inredning - Bygglöv-vv\1-A-40-P-D090.dwg

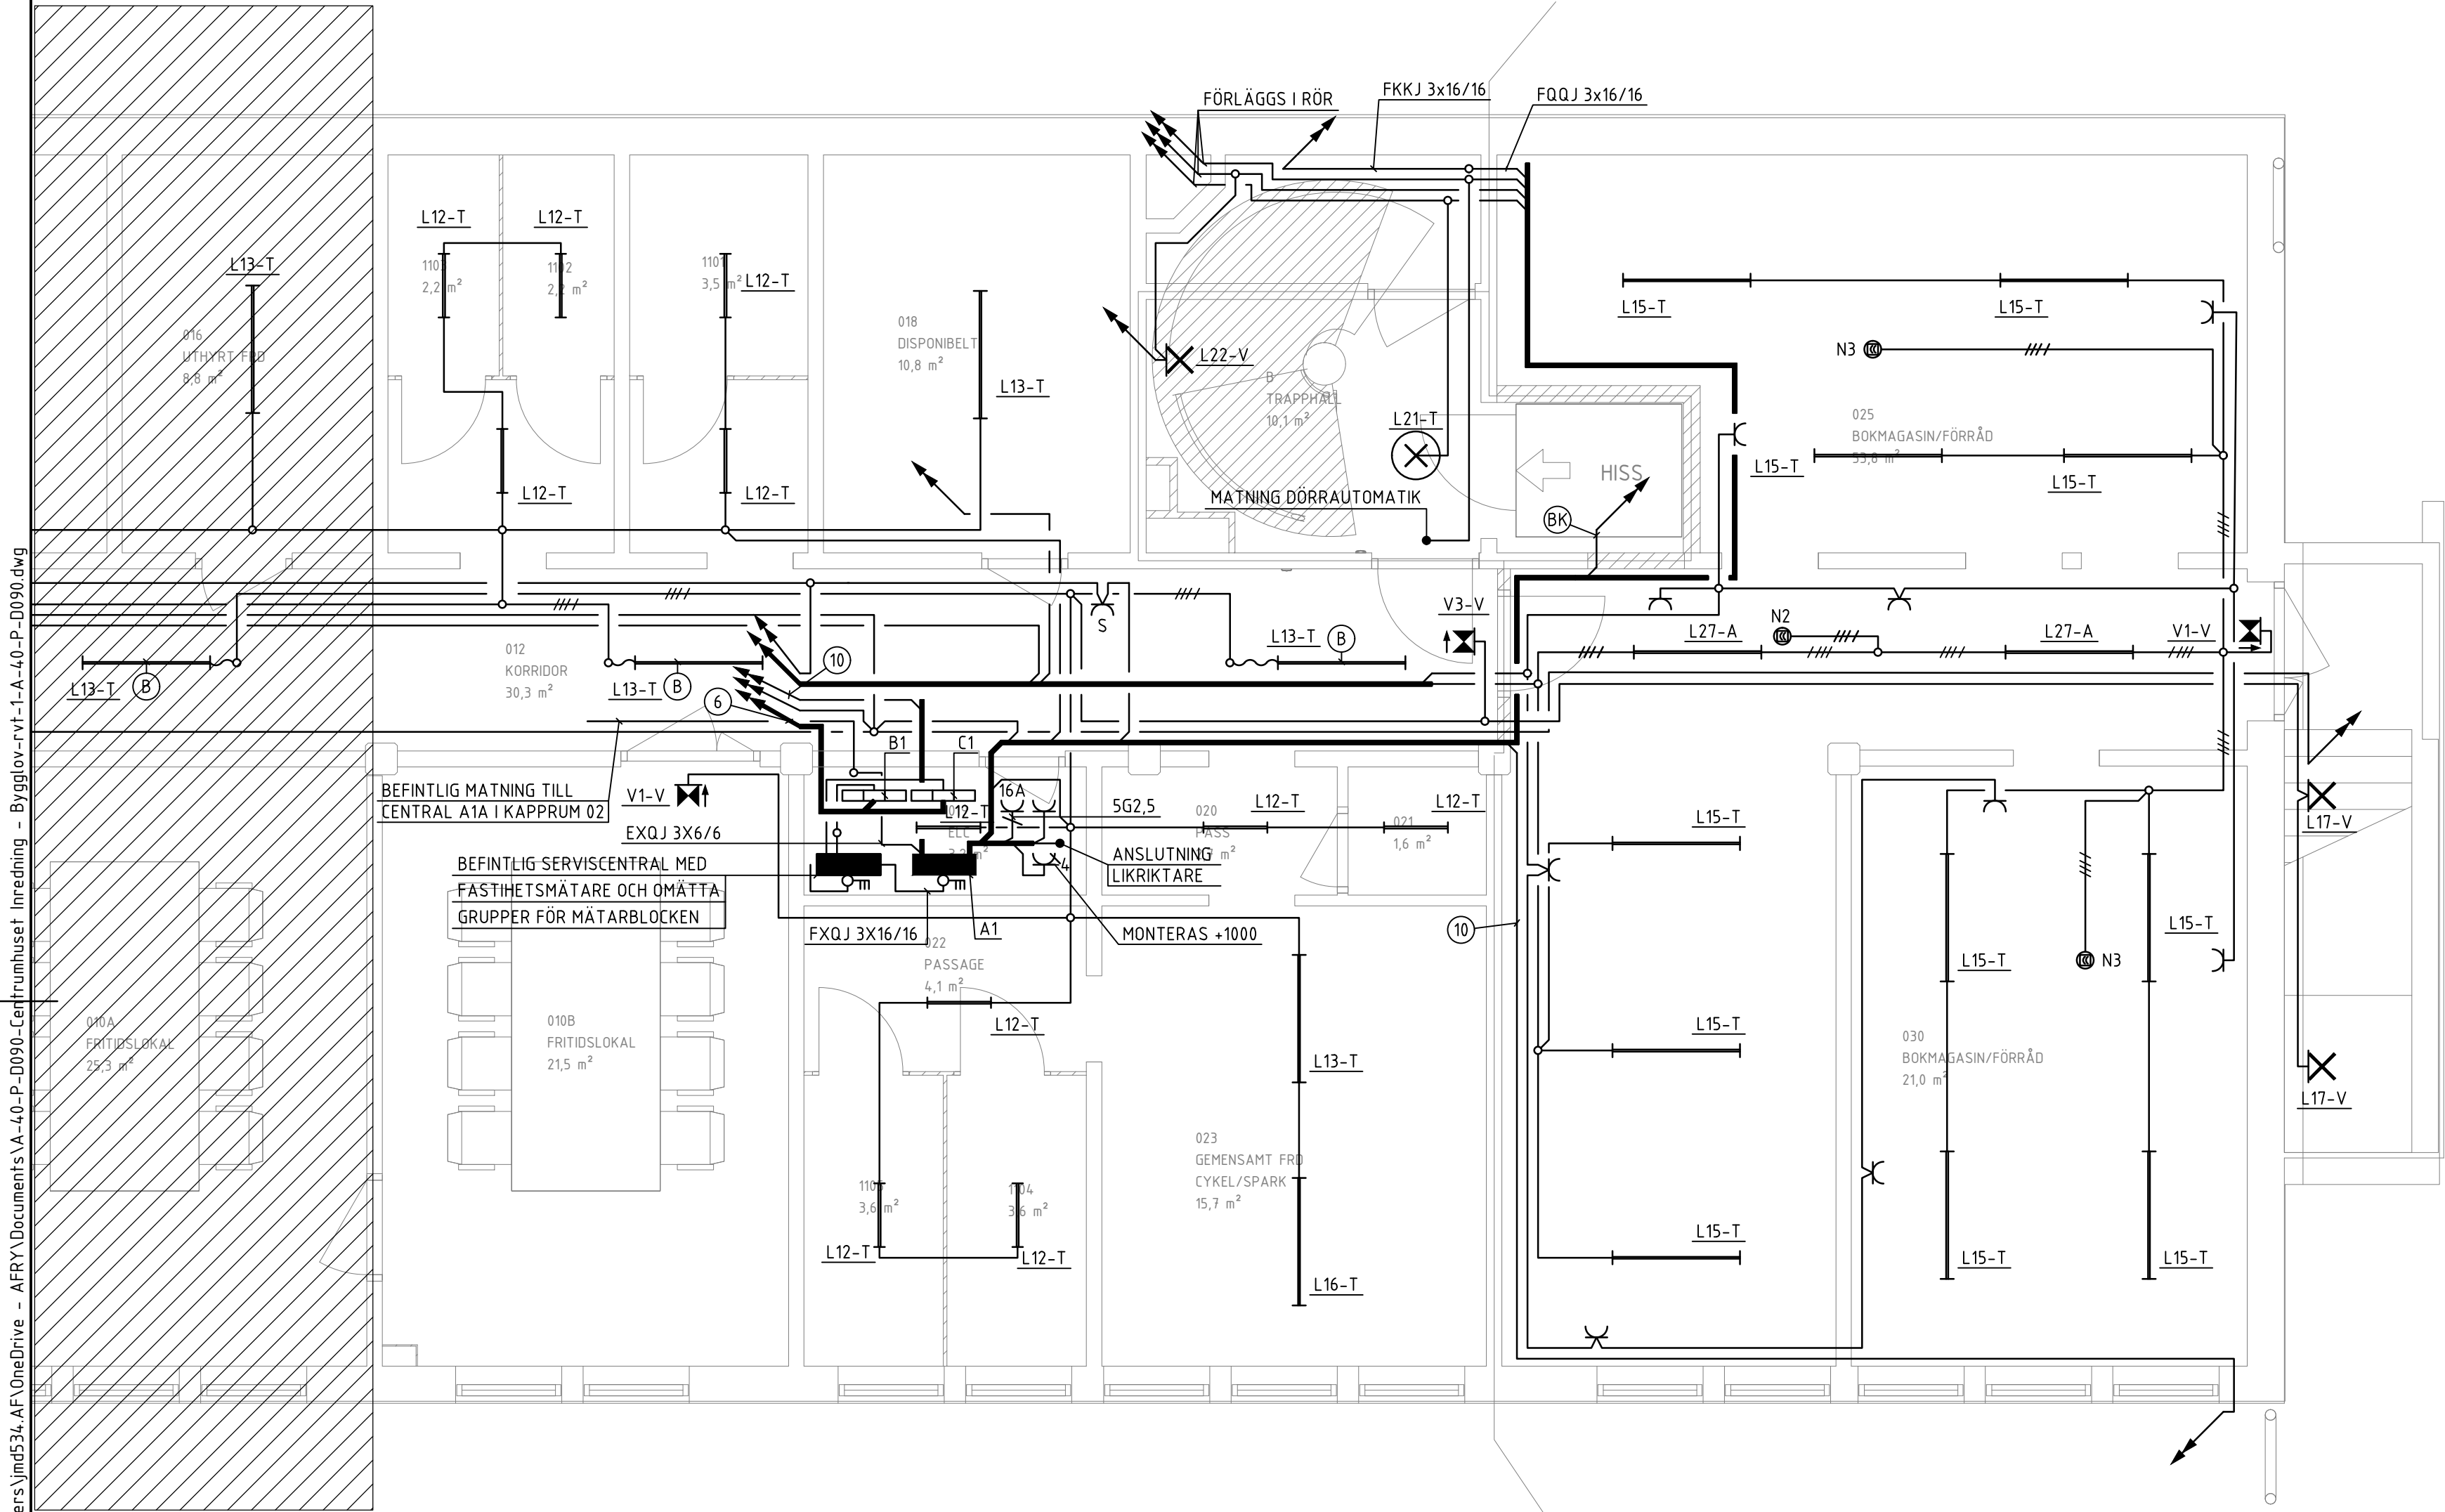

LAGER: SB11

FÖRKLARINGAR

SE RITNING E-69-5-01

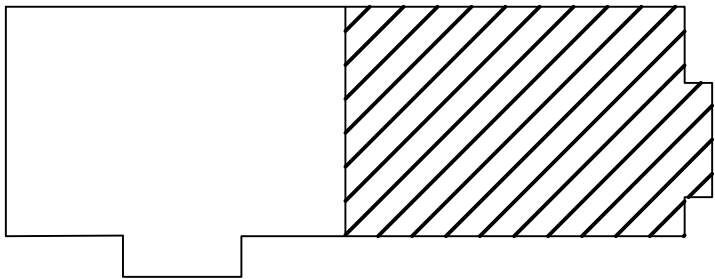

GODKÄND		STATUS
FÖRFRÅGNINGSUNDERLAG		HANDLING
DATUM 2025-02-26	ÄNDRING/PM	ÄNDRING
CENTRUMHUSET HUS D KRÅKAN 1, ROBERTSFORS		PROJEKT
ÅF-Infrastructure AB Storgatan 103 921 32 Lycksele Tel: 010-505 00 00		ANSVARIG PART
CONNY LARSSON	ROBIN MOLIN	SKAPAD AV
CONNY LARSSON	D0191802 (210550)	UPPDRAGSNUMMER
PLANRITNING		RITNINGSKATEGORI
OMBYGGNAD BIBLIOTEK OCH LÄGENHETER KÄLLARPLAN, PLAN 0, DEL 2 BELYSNING, KRAFT		FORMAT A1
E-63-1-D092		SKALA 1:50
		BET