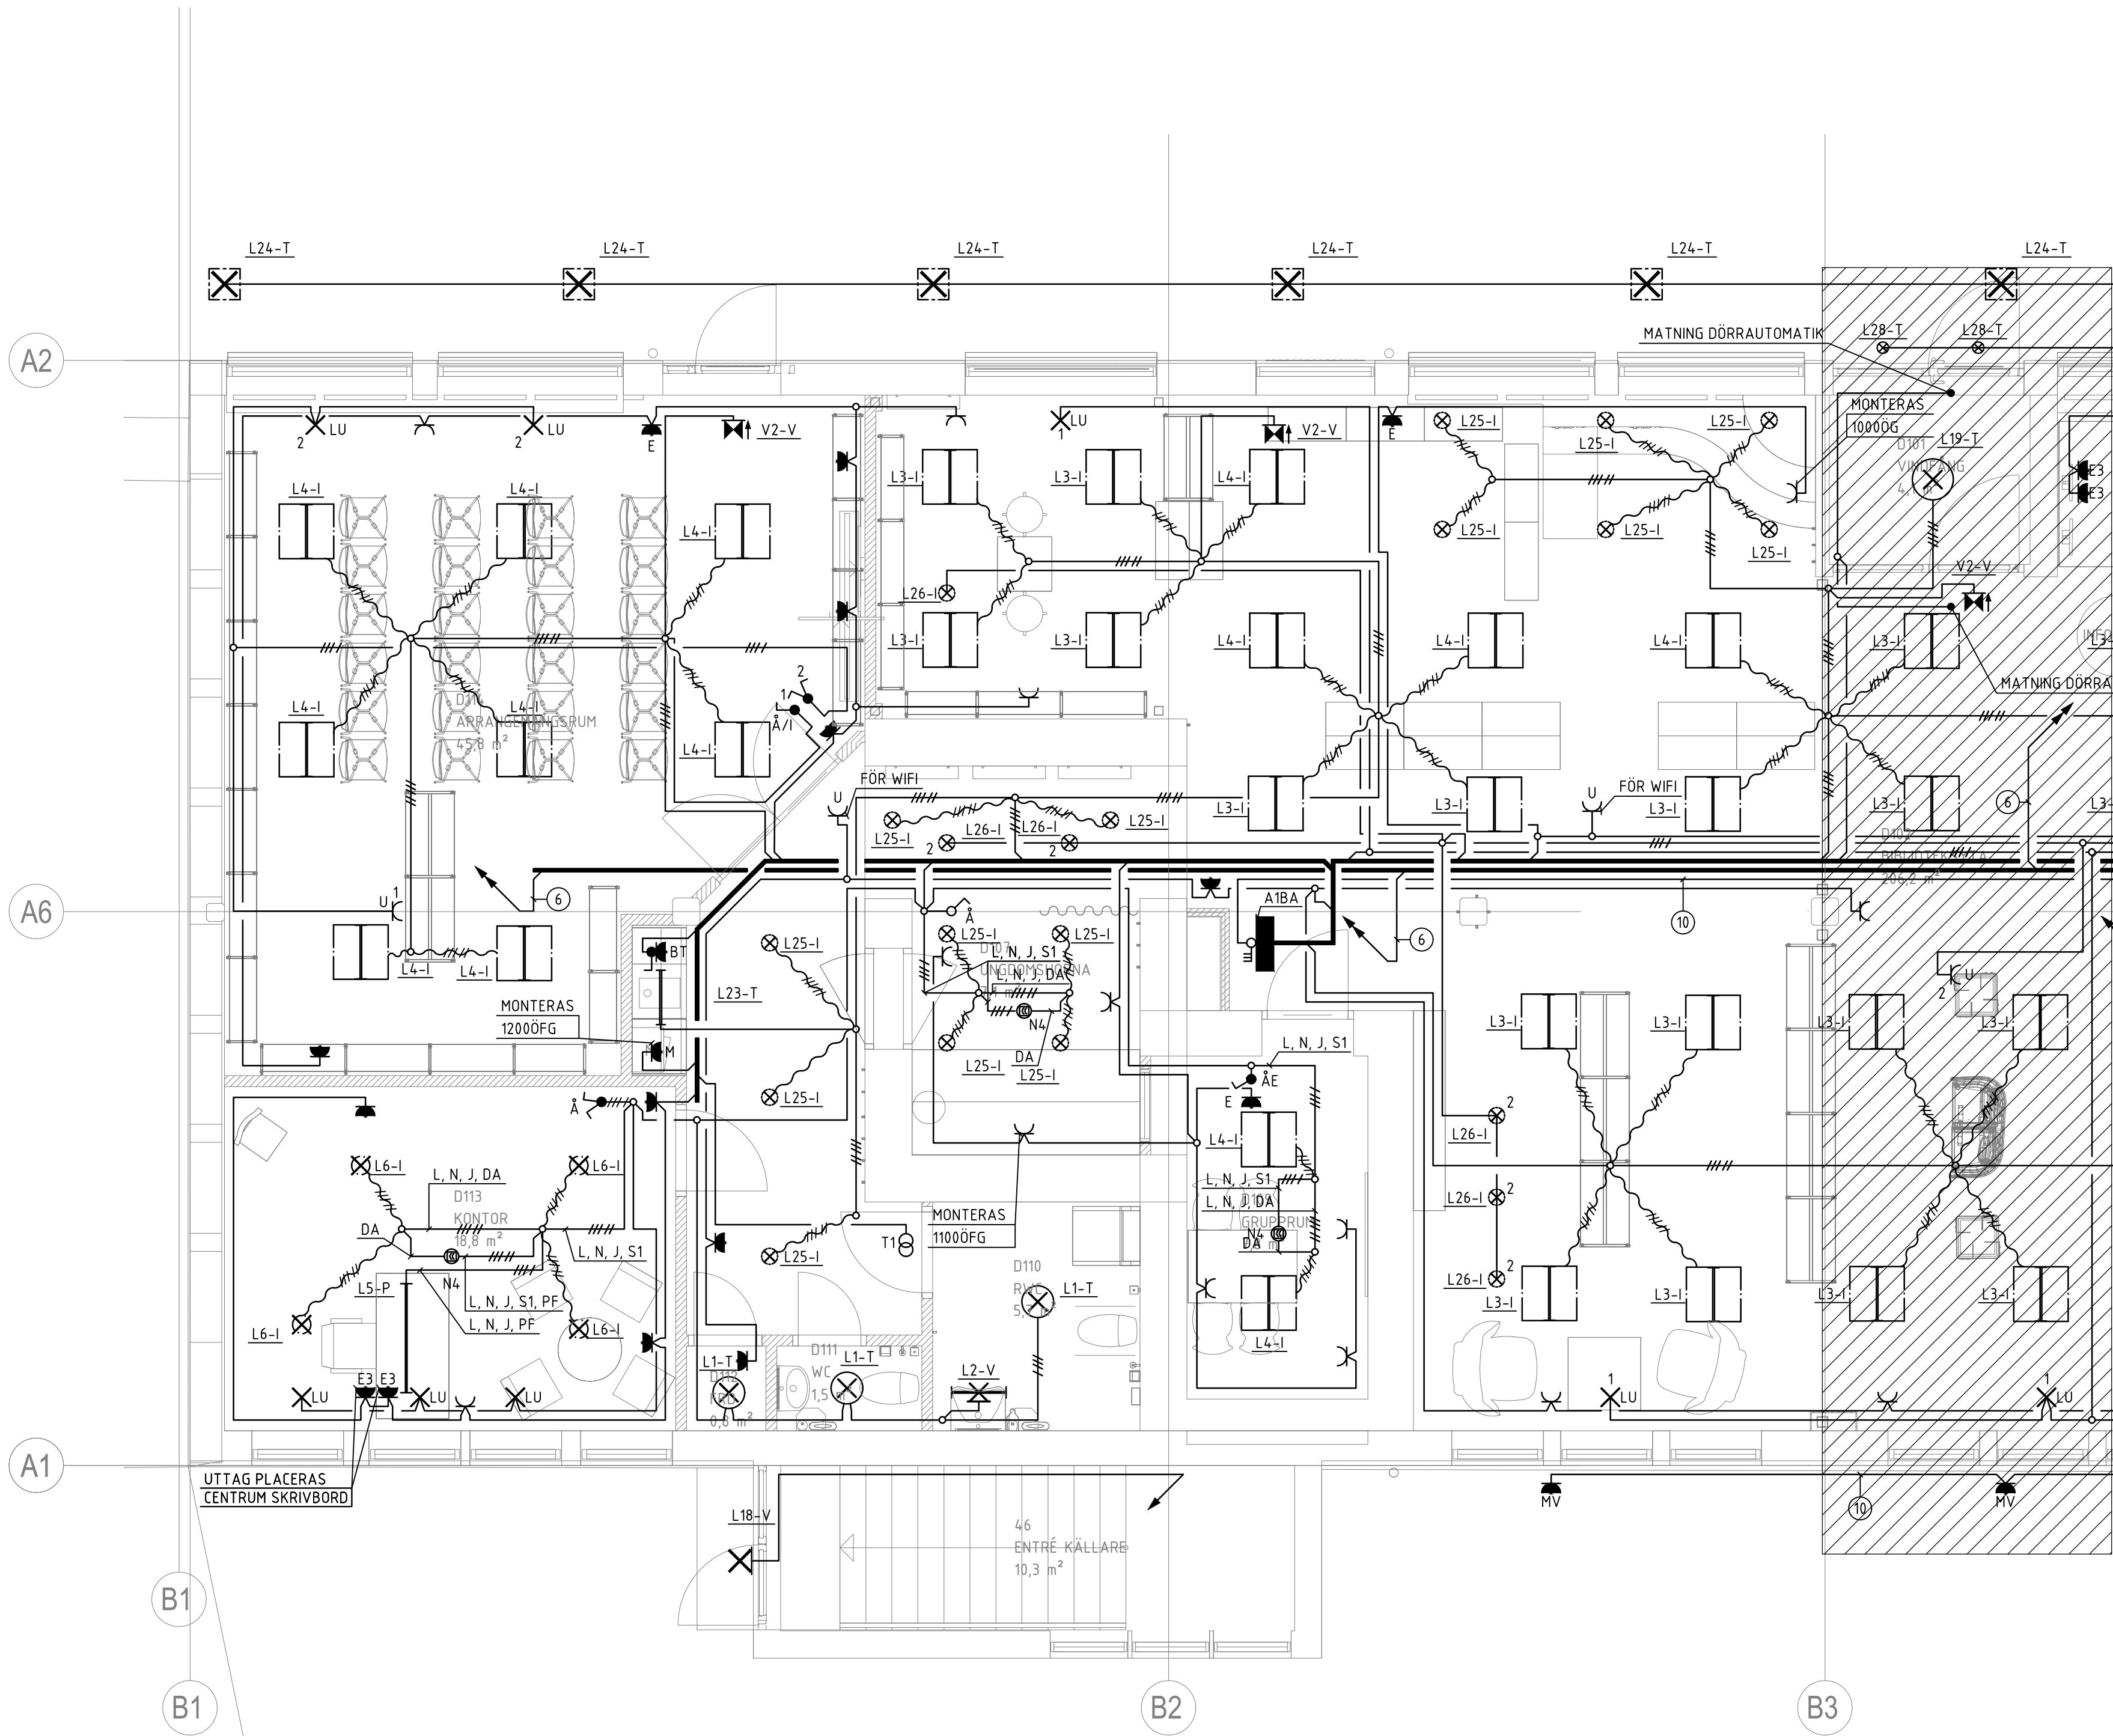


GODKÄND		STATUS
FÖRFRÅGNINGSUNDERLÄG		HANDLING
DATUM 2025-02-26	ÄNDRING/PM	ÄNDRING
CENTRUMHUSET HUS D KRÅKAN 1, ROBERTSFORS		PROJEKT
ÅF-Infrastructure AB Storgatan 103 921 32 Lycksele Tel: 010-505 00 00		ANSVARIG PART
CONNY LARSSON	ROBIN MOLIN	SKAPAD AV
CONNY LARSSON	D0191802 (210550)	UPPDRAGSGNUMMER
PLANRITNING		RITNINGSKATEGORI
OMBYGGNAD BIBLIOTEK OCH LÄGENHETER BOTTENPLAN, PLAN 1, DEL 1 BELYSNING, KRAFT		FORMAT A1
E-63-1-D101		SKALA 1:50
		BET