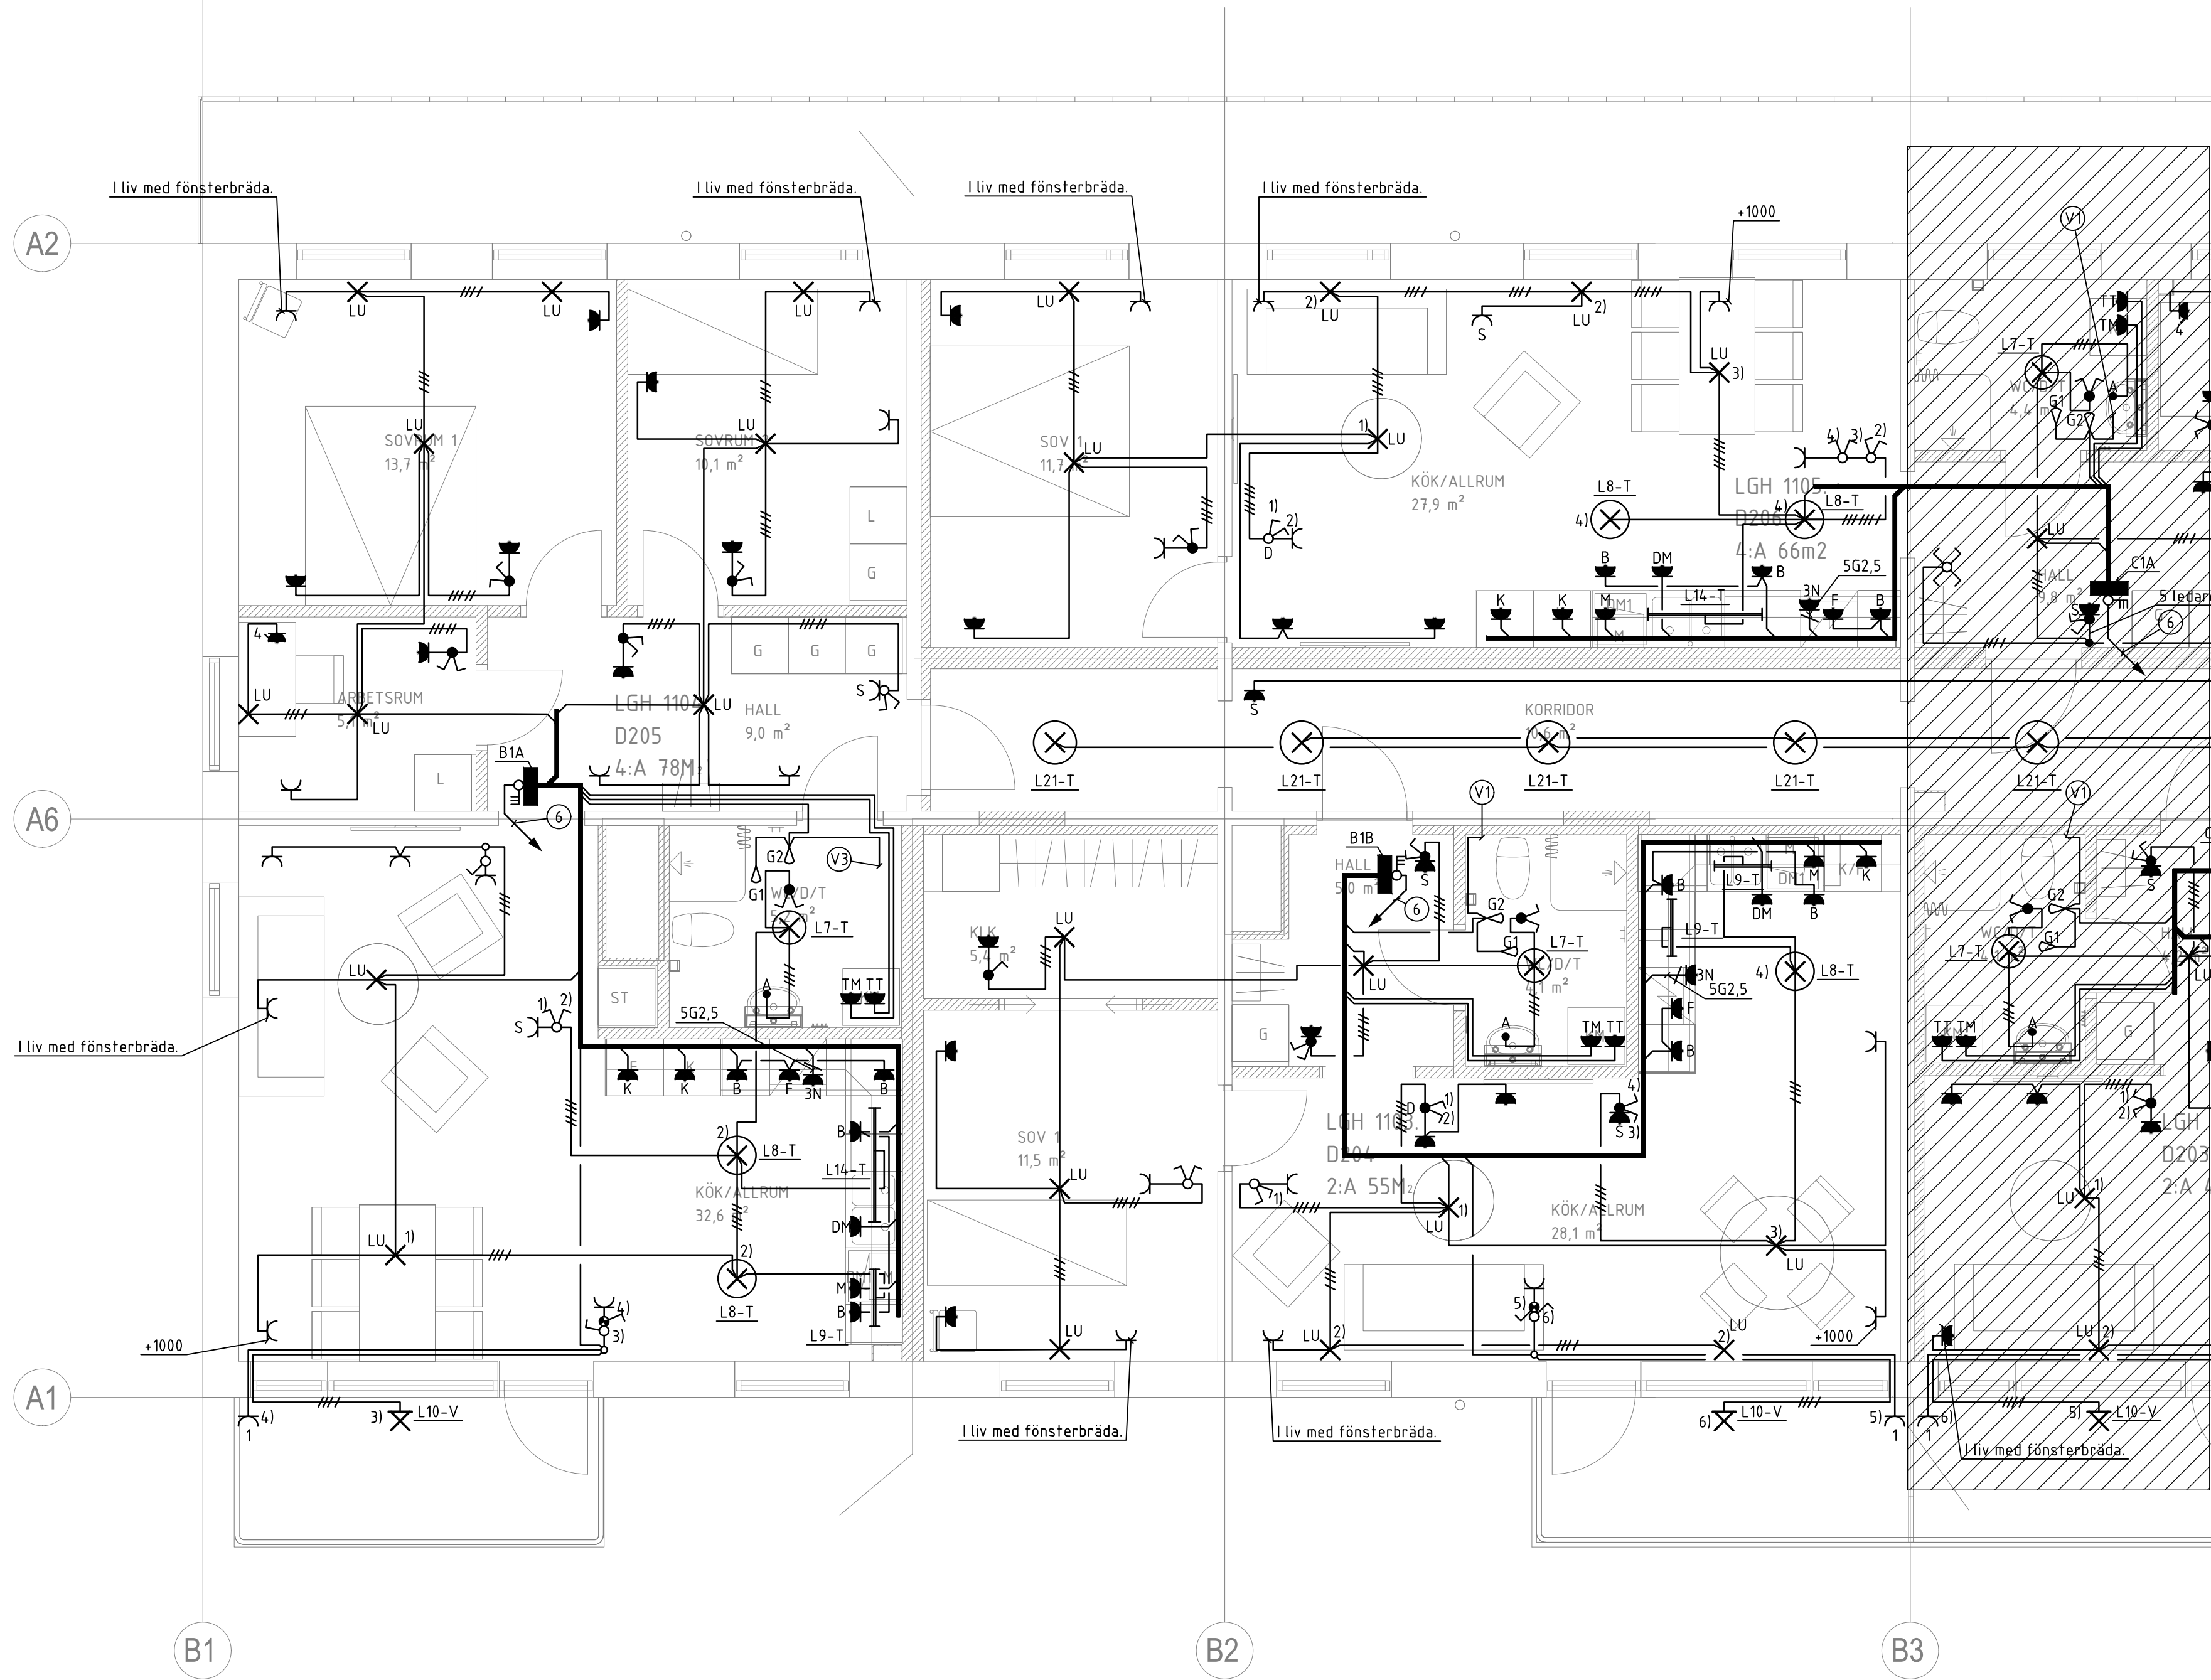


GODKÄND		STATUS
FÖRFRÅGNINGSUNDERLAG		HANDLING
DATUM 2025-02-26	ÄNDRING/PM	ÄNDRING
CENTRUMHUSET HUS D KRÅKAN 1, ROBERTSFORS		PROJEKT
ÅF-Infrastructure AB Storgatan 103 921 32 Lycksele Tel: 010-505 00 00		ANSVARIG PART
CONNY LARSSON	GABRIEL STENLUND	SKAPAD AV
CONNY LARSSON	D0191802 (210550)	UPPDRAGSSNUMMER
PLANRITNING		RITNINGSKATEGORI
OMBYGGNAD BIBLIOTEK OCH LÄGENHETER PLAN 1 TR, PLAN 2, DEL 1 BELYSNING, KRAFT		FORMAT
E-63-1-D201		SKALA 1:50
		NUMMER BET