
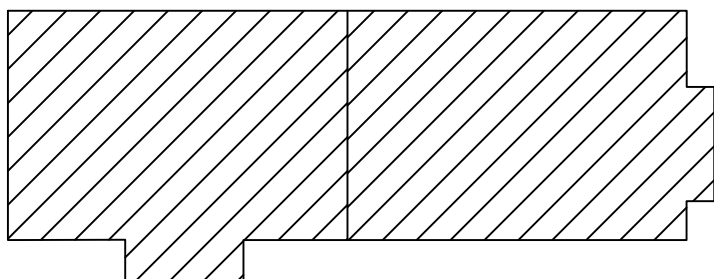


FÖRKLARINGAR

BS10 - BRAND-BRANDGASSPJÄLL
VD10 - VARIABELFLÖDESÖN

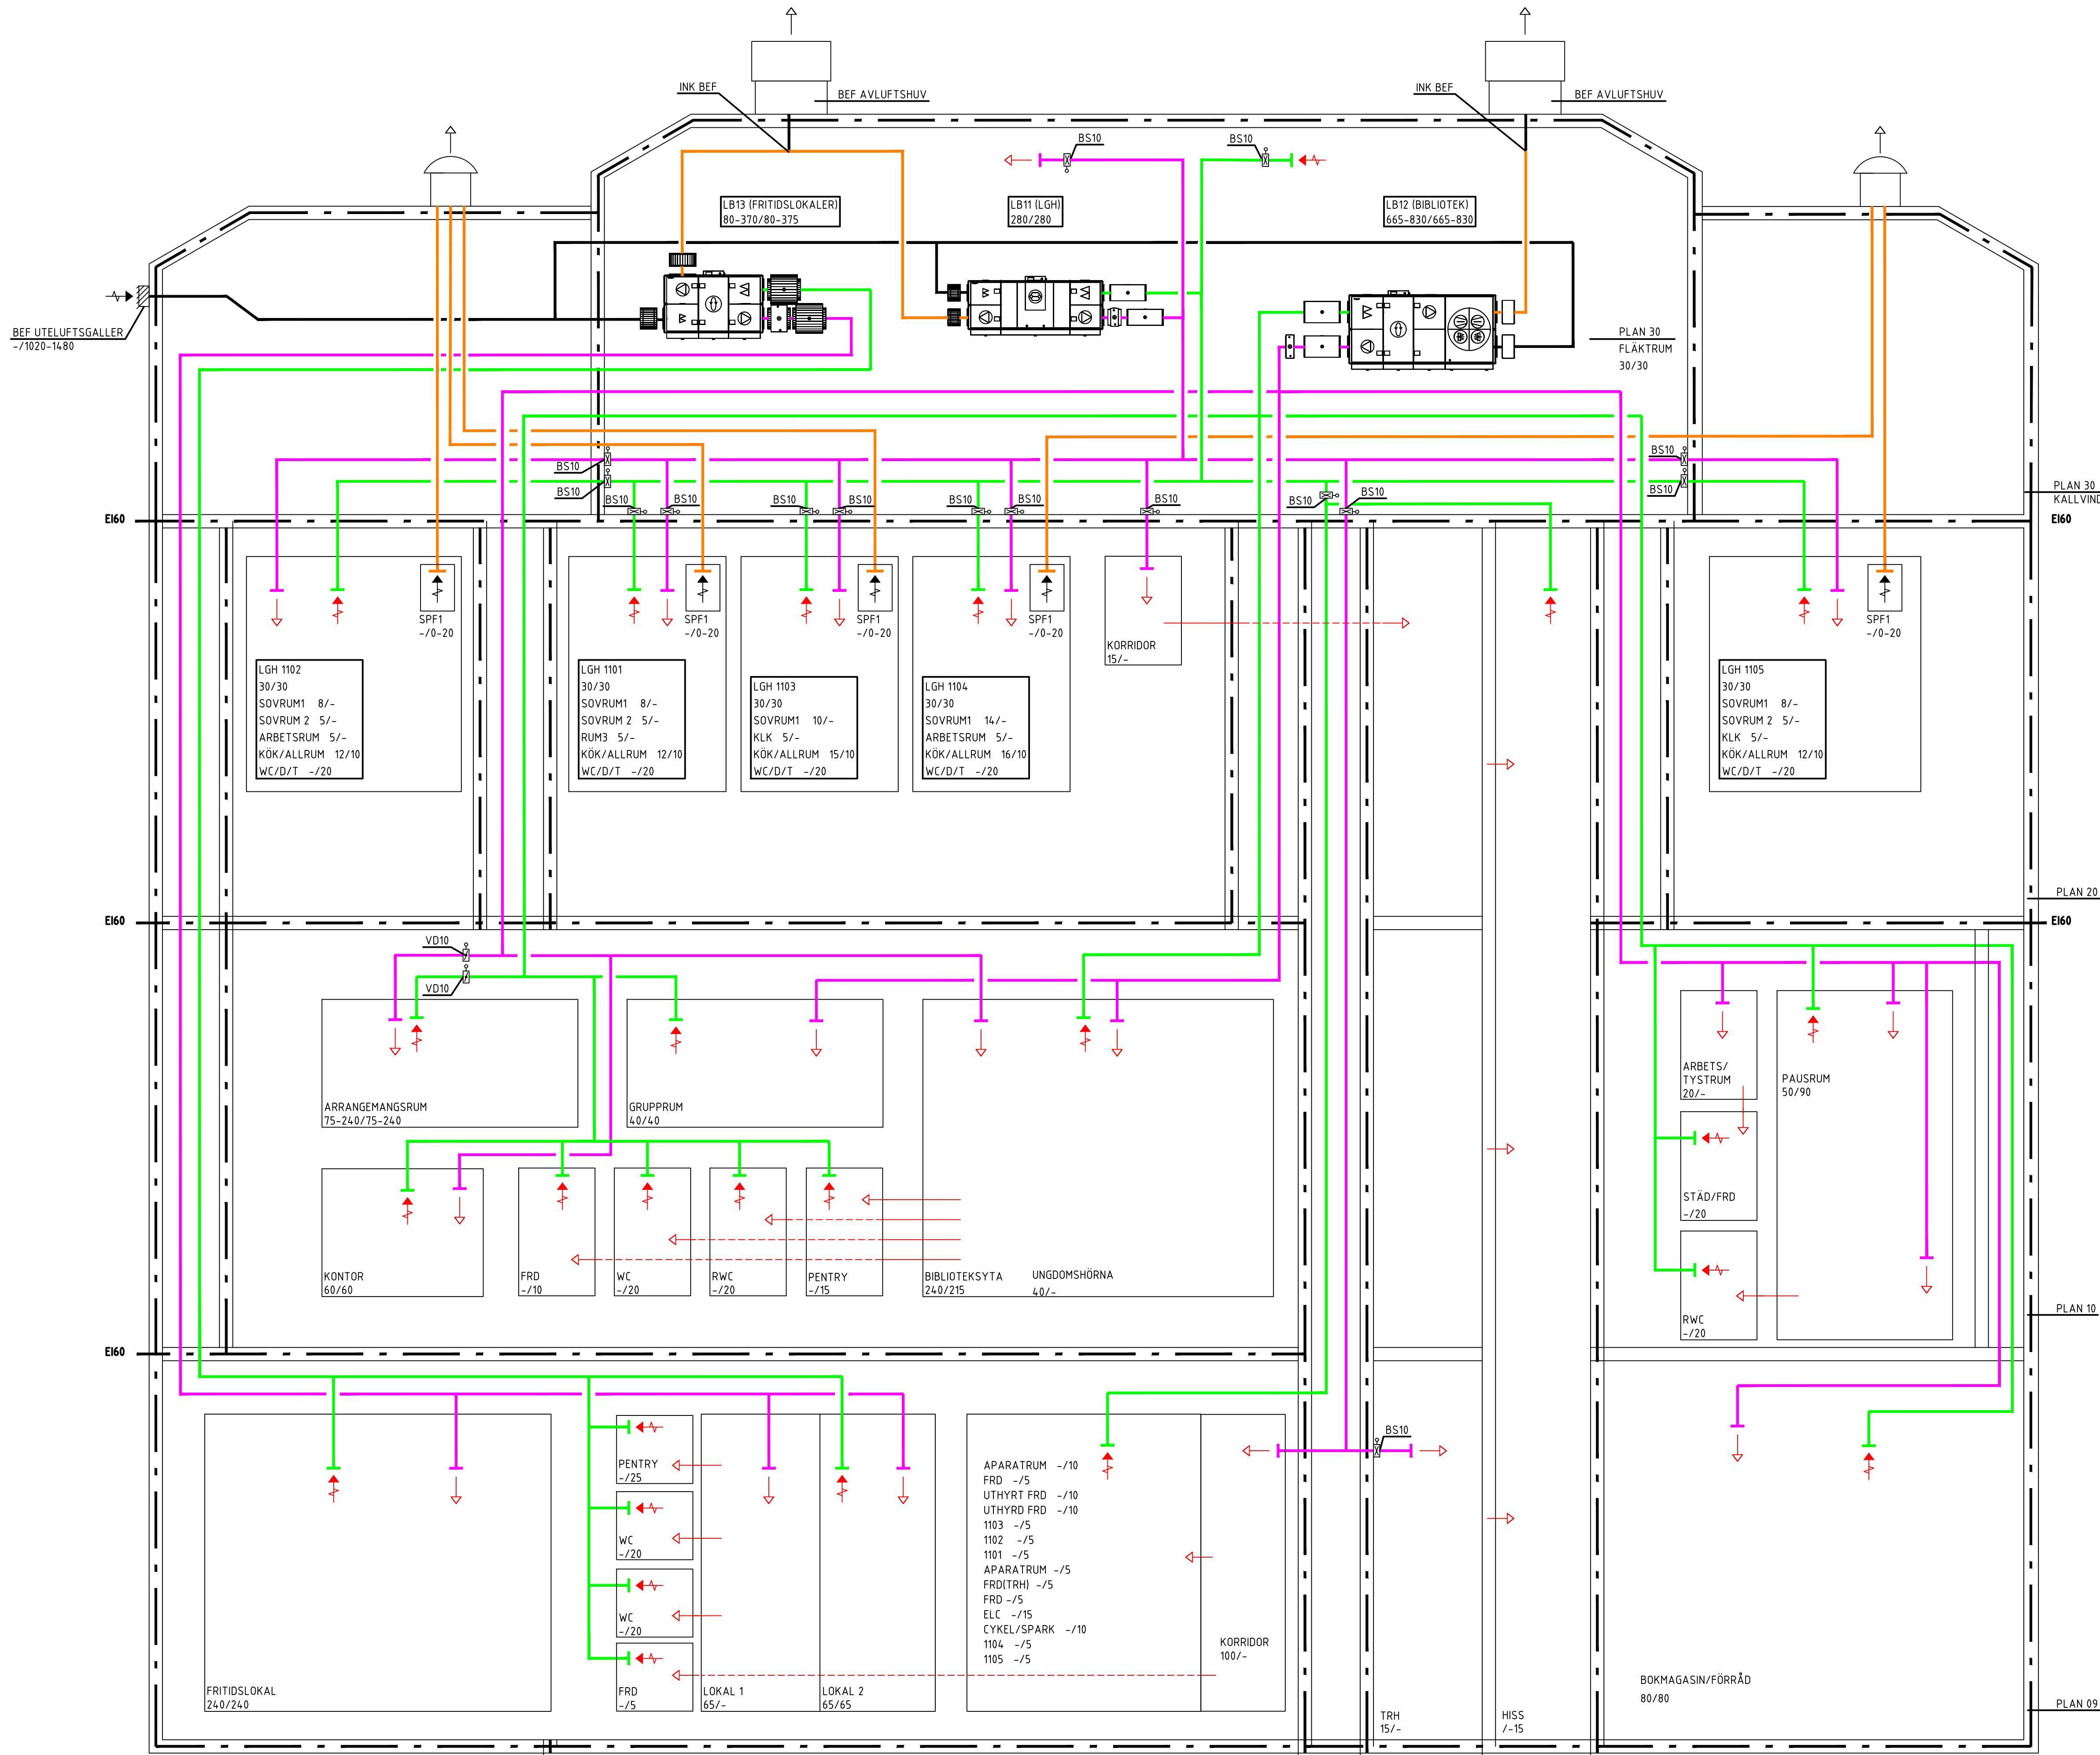

FÖRFRÅGNINGSUNDERLAG
BYGGHANDLING

DATUM	2025-02-26	STATUS	HANDLING
PROJEKT	CENTRUMHUSET HUS D KRÅKAN 1, ROBERTSFORS		
ANSVARIG PART	AFRY-Infrastructure AB		
Storgatan 103 921 32 Lycksele Tel: 010-505 00 00			
KONTAKTPERSON	Simon Rudin	KONTAKTPERSON	Marzena Januszewska-Kut
GÖRKAND AV	Simon Abrahamsson	UPPDRAGSNUMMER	D0182343 (210550)
PLANRITNING	RITNINGSKATEGORI		INNEHÅLL
OMBYGGNAD BIBLIOTEK OCH LÄGENHETER	PRINCIPSHEMA		A1
LUFTBEHANDLING	FORMAT		SKALA
V-57-8-D001	NUMMER		1:50
PLO			BET

XREF:

LAGER: SB11

PLO: 2025-02-24 14:17 X:\4-TRANSITENTITIES\TRUPPORAG\2025\0550 KRÅKAN 1 - CENTRUMHUSET\VV51 - MODELLER\1 - MODELL\1 - C-001DWG MARZENA JANUSZEWSKA-KUT