


\\.\A11 - Modeller\Export DWG\A-40-P-D090.dwg \V-50-P-D090.dwg \V-57-4 ramp.dwg \V57-4 ramp.dwg \Users\jmd53\AF-OneDrive - AFRY\Documents\A-40-P-D090-Centrumhuset Inredning - Bygglös-rv1-A-40-P-D090.dwg

LAGER: SB11

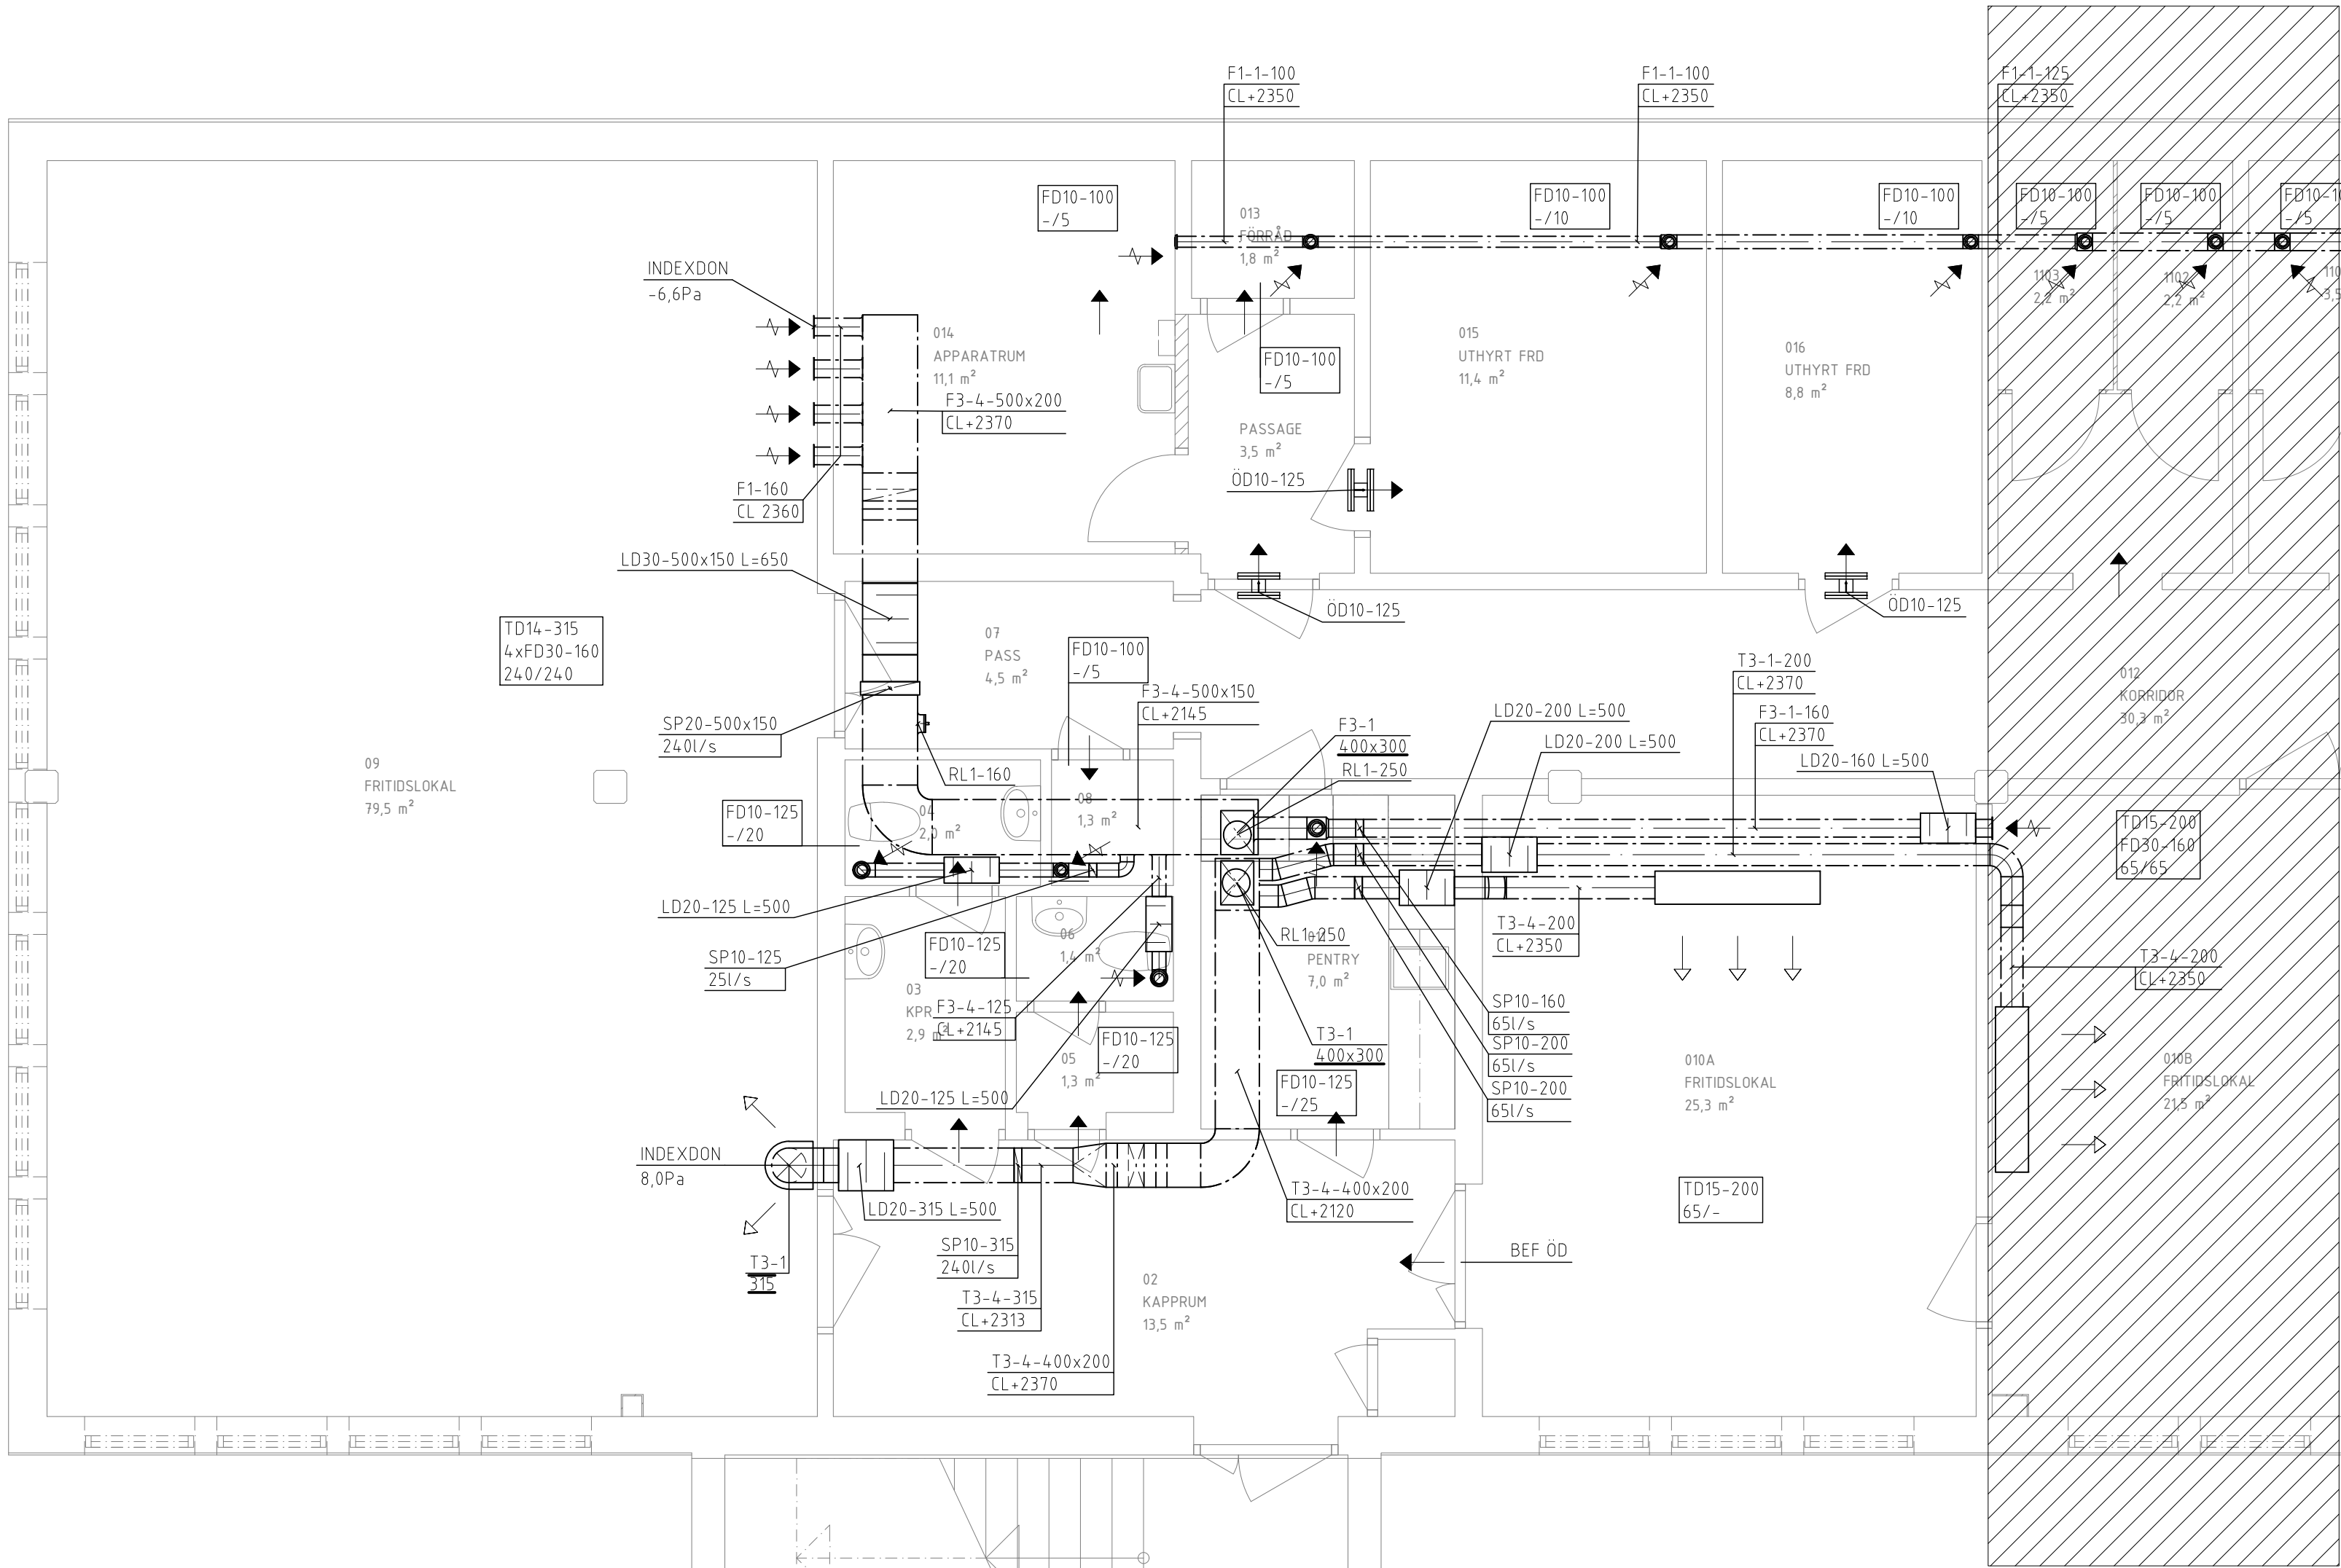

FÖRKLARINGAR

| MEDIA |          |
|-------|----------|
| A     | AVLUFT   |
| F     | FRÅNLUFT |
| T     | TILLUFT  |
| U     | UTELUFT  |
| Ö     | ÖVERLUFT |

| SYSTEM |                                     |
|--------|-------------------------------------|
| 1      | LUFTBEHANDLING LB11, LÄGENHETER     |
| 2      | LUFTBEHANDLING LB12, BIBLIOTEK      |
| 3      | LUFTBEHANDLING LB13, FRITIDSLOKALER |
| 4      | SPISFLÄKT LÄGENHETER                |
| 5      | GEMENSAMM UTELUFT                   |

| MATERIAL |                                        |
|----------|----------------------------------------|
| 1        | VARMFÖRZINKAD STÅLPLÅT                 |
| 4        | VARMFÖRZINKAD STÅLPLÅT, PULVERLACKERAD |

| DIMENSION |  |
|-----------|--|
|-----------|--|

| ISOLERING |  |
|-----------|--|
|-----------|--|

|    |                                      |
|----|--------------------------------------|
| B2 | UTV. BRANDISOLERING MINERALULL E160  |
| K3 | UTV. KONDENSISOLERING 25mm CELLGUMMI |

LUFTFLÖDEN ANGES I L/s.  
KANALDIMENSION SAMMA SOM DONANSLUTNING DÄR EJ ANNAT ANGES.  
HÖJDER PÅ KANALER ANGES MED CENTRUM KANAL I MM ÖVER FÄRDIGT GOLV..

|                                                                                      |                                     |                  |
|--------------------------------------------------------------------------------------|-------------------------------------|------------------|
| FÖRFRÅGNINGSUNDERLAG                                                                 |                                     | STATUS           |
| BYGGHANDLING                                                                         |                                     | HANDLING         |
| DATUM<br>2025-02-26                                                                  | ÄNDRING                             |                  |
| CENTRUMHUSET HUS D<br>KRÅKAN 1, ROBERTSFORS                                          |                                     | PROJEKT          |
| ANSVÄRIG PART                                                                        |                                     |                  |
| AFRY-Infrastructure AB<br>Storgatan 103<br>921 32 Lycksele<br>Tel: 010-505 00 00     |                                     |                  |
| KONTAKTPERSON<br>Simon Rudin                                                         | Ansvarig<br>Marzena Januszewska-Kut | SKAPAD AV        |
| GODKÄND AV<br>Simon Abrahamsson                                                      | Dokumentnummer<br>D0182343 (210550) | UPPDRAGSNUMMER   |
| PLANRITNING                                                                          |                                     | RITNINGSKATEGORI |
| OMBYGGNAD BIBLIOTEK OCH LÄGENHETER<br>KÄLLARPLAN - PLAN 09 - DEL 1<br>LUFTBEHANDLING | INNEHÅLL<br>A1                      | FORMAT           |
| V-57-1-D091                                                                          |                                     | SKALA<br>1:50    |
| NUMMER                                                                               |                                     | BET              |