


X:\4-Transit\Entries\TM\Uppdrag\2021\20550 Kråkan 1 - Centrumhuset\2 - Gemensamma underlag\Erhållna relationer\linjar\A11 - Modell\Export\DWG\A-40-P-D300.dwg 11.12.2025 10:00 X:\4-Transit\Entries\TM\Uppdrag\2021\20550 Kråkan 1 - Centrumhuset\2 - Gemensamma underlag\Erhållna relationer\linjar\A11 - Modell\Export\DWG\A-40-P-D300.dwg 11.12.2025 10:00

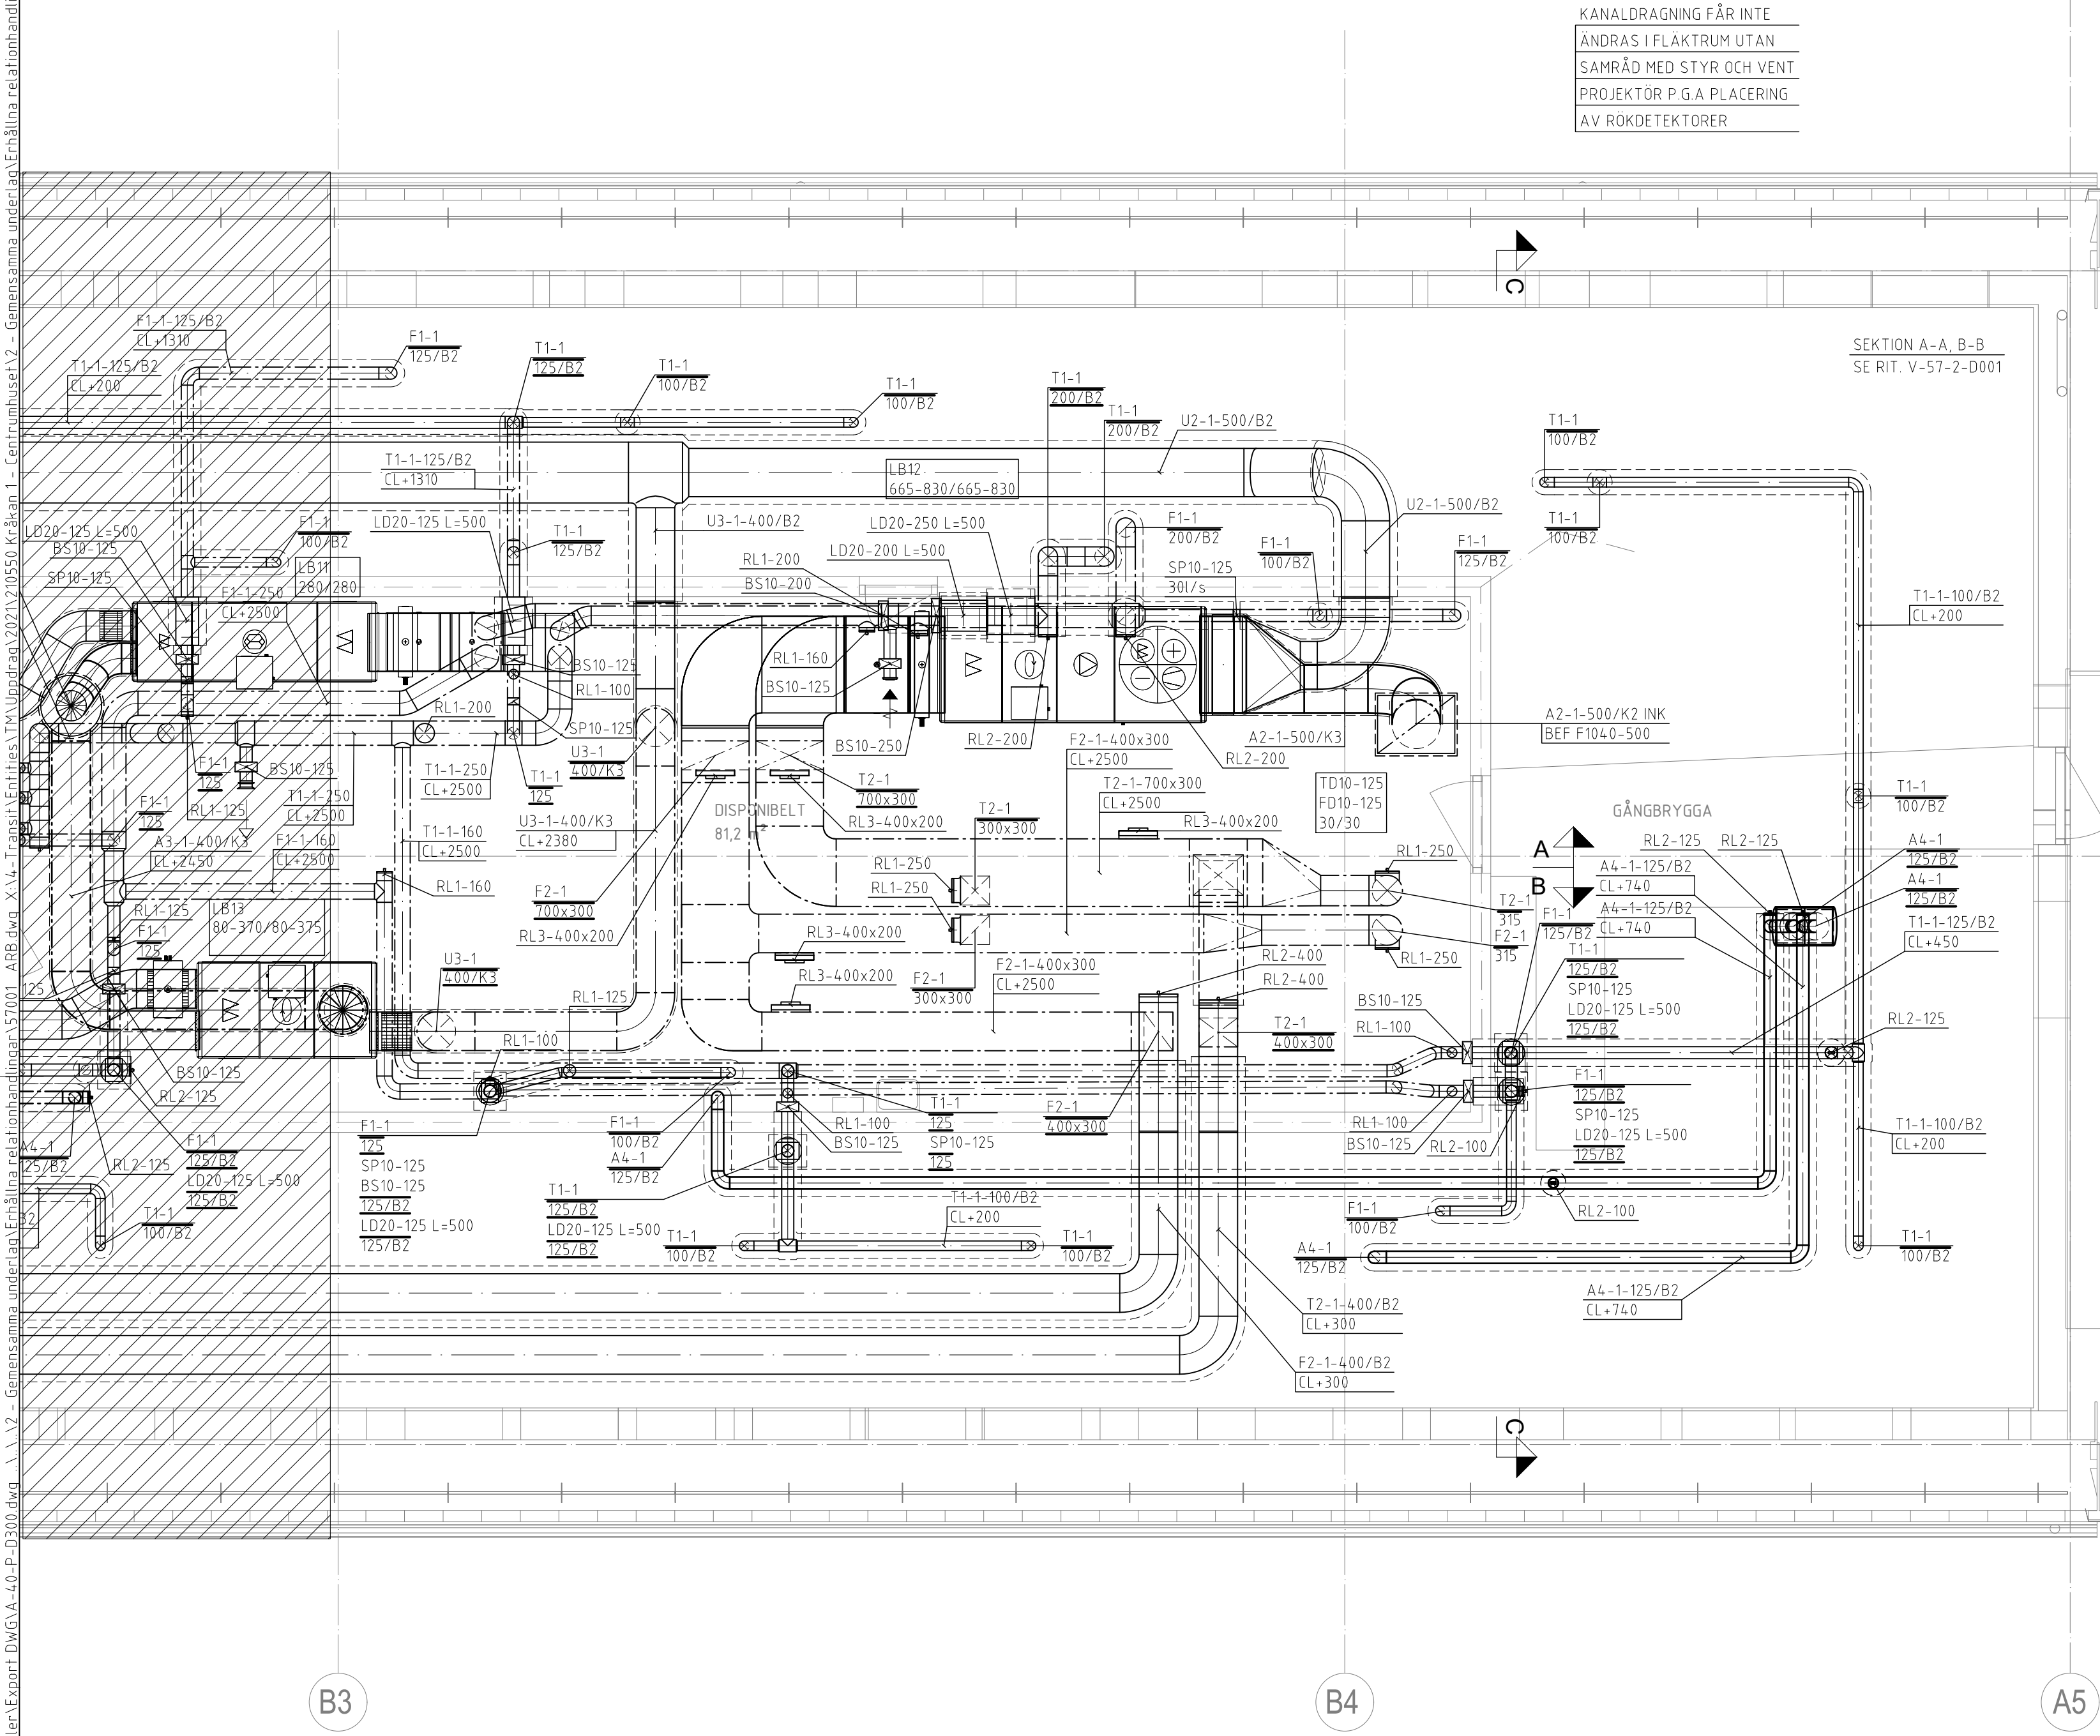

KANALDRAGNING FÅR INTE
ÄNDRAS I FLAKTRUM UTAN
SAMRÅD MED STYR OCH VENT
PROJEKTÖR P.G.A PLACERING
AV RÖKDETEKTORER

SEKTION A-A, B-B
SE RIT. V-57-2-D001

FÖRKLARINGAR

MEDIA	
A	AVLUFT
F	FRÅNLUFT
T	TILLUFT
U	UTLUFT
Ö	ÖVERLUFT

SYSTEM	
1	LUFTBEHANDLING LB11, LAGENHETER
2	LUFTBEHANDLING LB12, BIBLIOTEK
3	LUFTBEHANDLING LB13, FRITIDSKALOR
4	SPISFLÄKT LAGENHETER
5	GEMENSAMM UTELUFT

MATERIAL	
1	VARMFÖRZINKAD STÅLPLÅT
4	VARMFÖRZINKAD STÅLPLÅT, PULVERLACKERAD

DIMENSION	
-----------	--

ISOLERING	
-----------	--

B2	UTV. BRANDISOLERING MINERALULL E160
K3	UTV. KONDENSISOLERING 25mm CELLGUMMI

LUFTFLÖDEN ANGES I L/S.
KANALDIMENSION SAMMA SOM DONANSLUTNING DÄR
EJ ANNAT ANGES.
HÖJDER PÅ KANALER ANGES MED CENTRUM KANAL I MM
ÖVER FÄRDIGT GÖLV..

FÖRFRÅGNINGSUNDERLAG BYGGHANDLING

DATUM: 2025-02-26

CENTRUMHUSET HUS D KRÅKAN 1, ROBERTSFORS

AFRY-Infrastructure AB
Storgatan 103
921 32 Lycksele
Tel: 010-505 00 00

KONTAKTPERSON: Marzena Januszewska-Kut
GODKÄND AV: Simon Abrahamsson

UPPDRAGSNUMMER: D0182343 (210550)

PLANRITNING

OMBYGGNAD BIBLIOTEK OCH LÄGENHETER
VINDSVÄNING - PLAN 30 - DEL 2
LUFTBEHANDLING

V-57-1-D302