
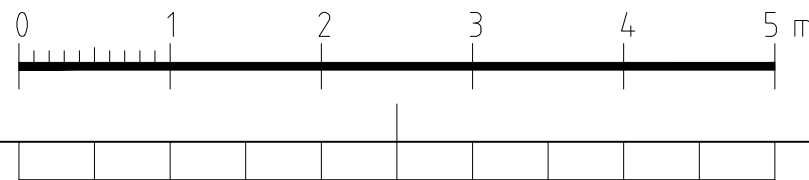
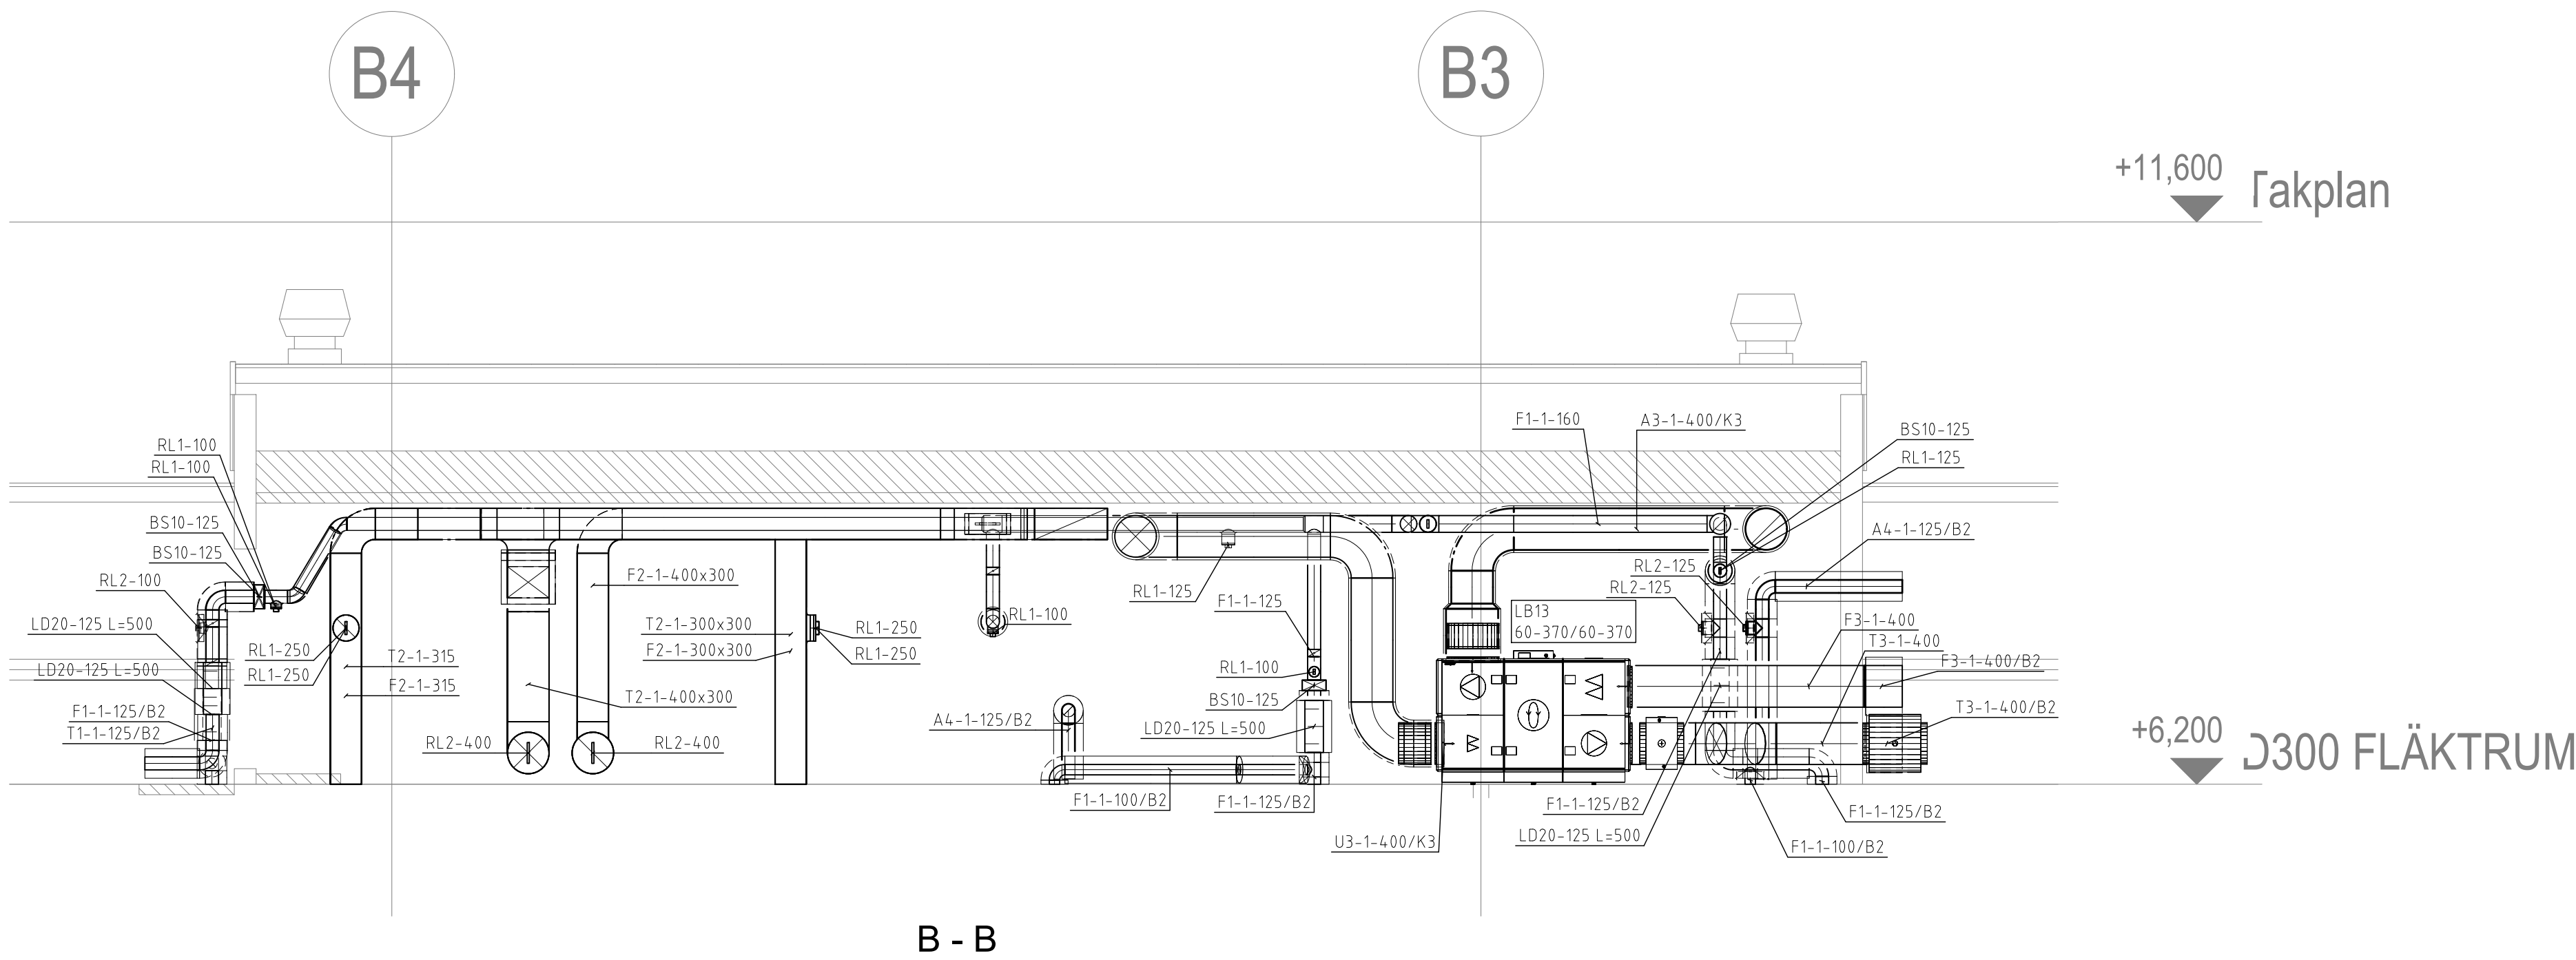


X:\4-Transit\Entries\TM\Uppdrag\2021\20550 Kråkan 1 - Centrumhuset\2 - Gemensamma underlag\Erhållna relationer\Andringsplan och sektioner\REF.dwg U:2001\2001-08-01

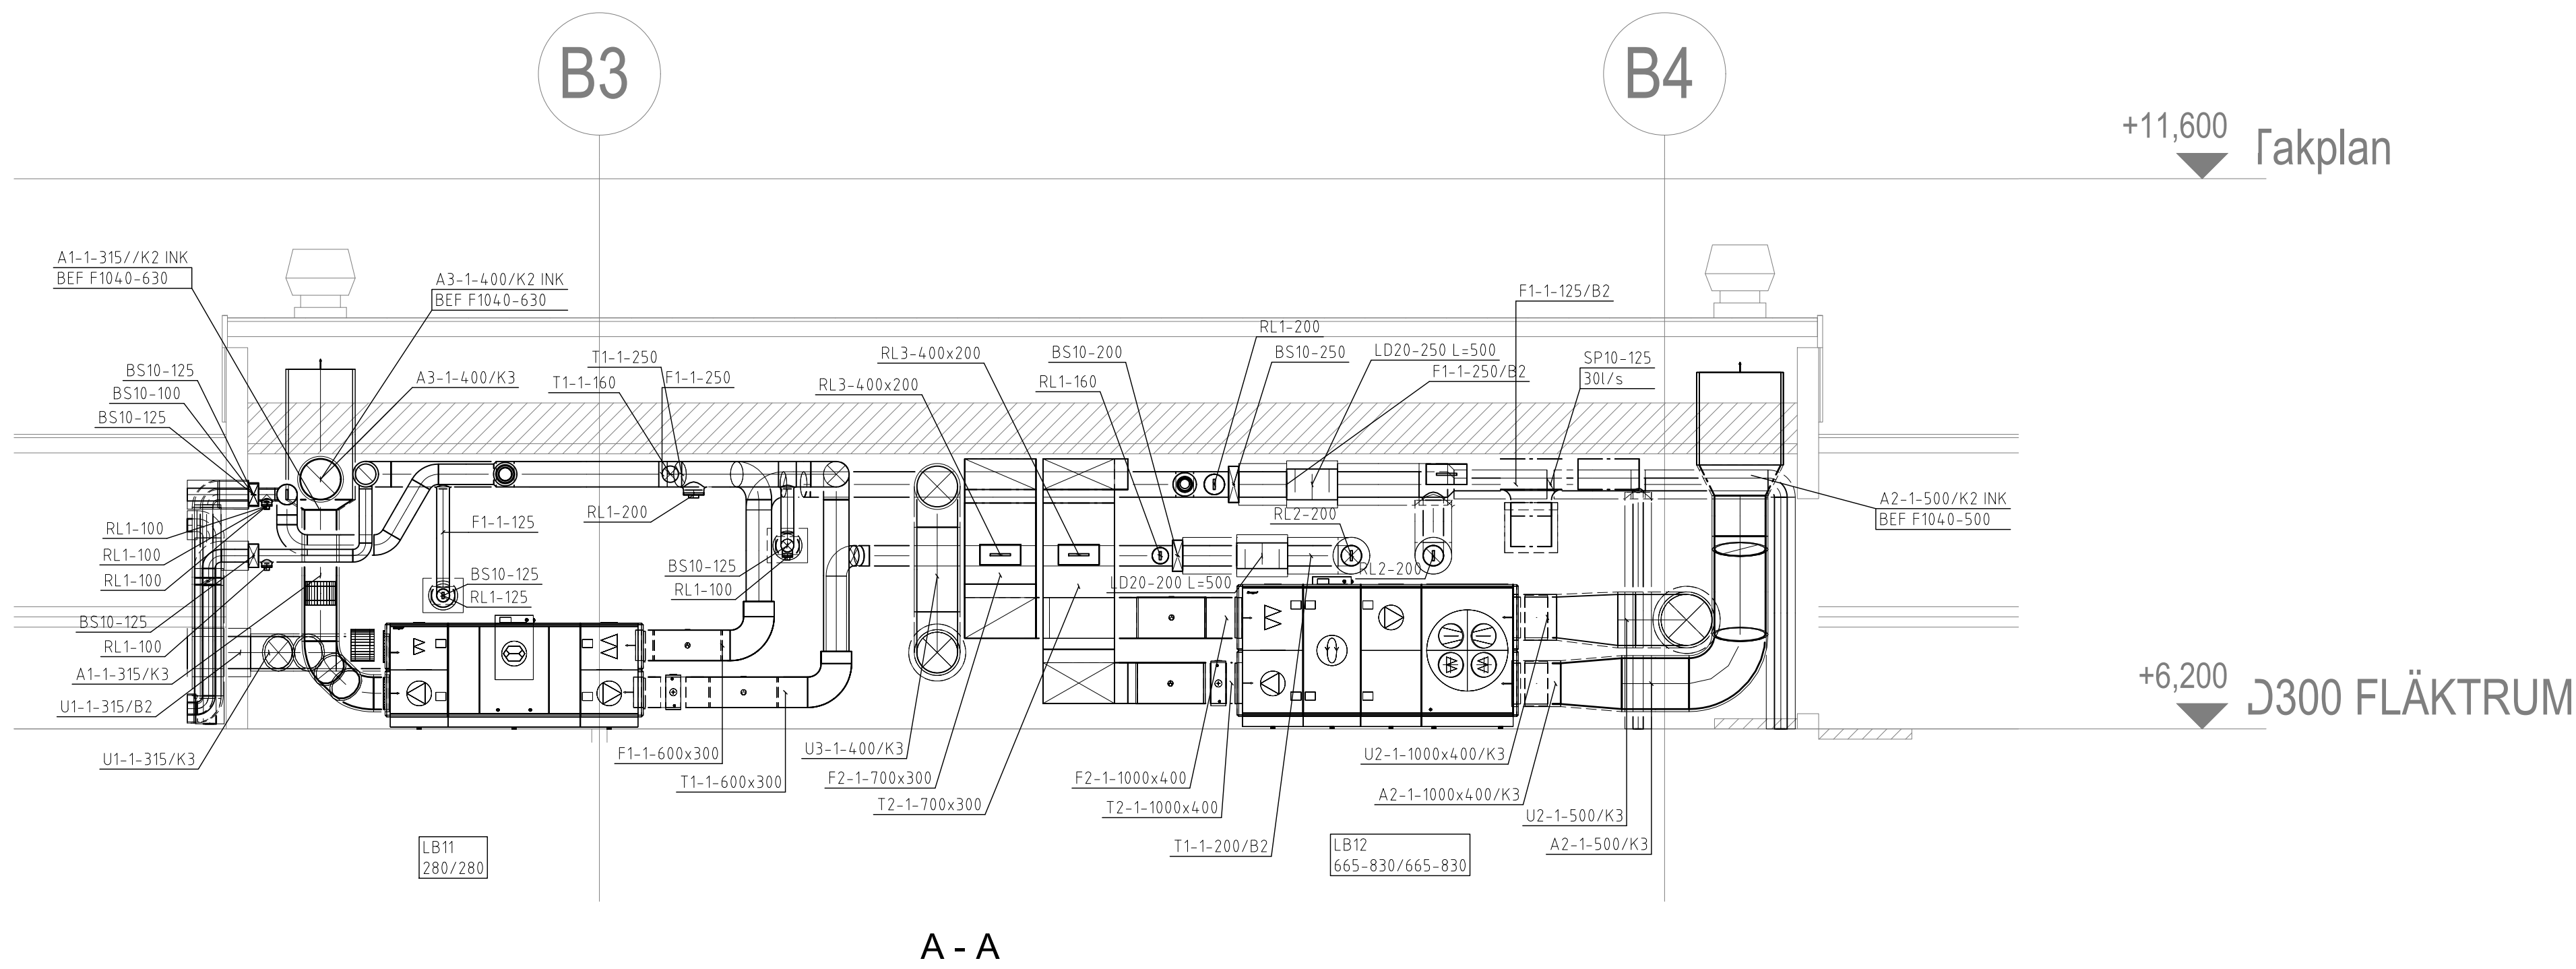

FÖRKLARINGAR

MEDIA	
A	AVLUFT
F	FRÅNLUFT
T	TILLUFT
U	UTLUFT
Ö	ÖVERLUFT

SYSTEM	
1	LUFTBEHANDLING LB11, LÄGENHETER
2	LUFTBEHANDLING LB12, BIBLIOTEK
3	LUFTBEHANDLING LB13, FRITIDSLOKALER
4	SPISFLÄKT LÄGENHETER
5	GEMENSAMM UTELUFT

MATERIAL	
1	VARMFÖRZINKAD STÅLPLÅT
4	VARMFÖRZINKAD STÅLPLÅT, PULVERLACKERAD

DIMENSION	
-----------	--

ISOLERING	
-----------	--

B2	UTV. BRANDISOLERING MINERALULL EI60
K3	UTV. KONDENSISOLERING 25mm CELLGUMMI

LUFTFLÖDEN ANGES I L/S.
KANALDIMENSION SAMMA SOM DONANSLUTNING DÄR
EJ ANNAT ANGES.
HÖJDER PÅ KANALER ANGES MED CENTRUM KANAL I MM
ÖVER FÄRDIGT GÖLV..

FÖRFRÅGNINGSUNDERLAG		STATUS
BYGGHANDLING		HANDLING
DATUM	2025-02-26	ÄNDRING
PROJEKT		
CENTRUMHUSET HUS D KRÅKAN 1, ROBERTSFORS		
ANSVÄRIG PART		
AFRY-Infrastructure AB		
Storgatan 103 921 32 Lycksele Tel: 010-505 00 00		
KONTAKTPERSON	Simon Rudin	SKAPAD AV
GODKÄND AV	Marzena Januszewska-Kut	
UPPDRAGSNUMMER	D0182343 (210550)	
PLANRITNING		RITNINGSKATEGORI
OMBYGGNAD BIBLIOTEK OCH LÄGENHETER		
PLAN30, SEKTION A-A, B-B		
LUFTBEHANDLING		
NUMMER	V-57-2-D001	BET