




X:\4-Transit\Entries\TM\Uppdrag\2021\20550 Kråkan 1 - Centrumsuset\A1 - Modeller\Export\DWG\A-40-P-D300.dwg, \, \, \2 - Gemensamma underlag\Enhållna relationer\liniar\51001_ARE.dwg, X:\4-Transit\Entries\TM\Uppdrag\2021\20550 Kråkan 1 - Centrumsuset\2 - Gemensamma underlag\Enhållna relationer\liniar\PLAN OCH SEKTION\REF.dwg, U, 2001, 200

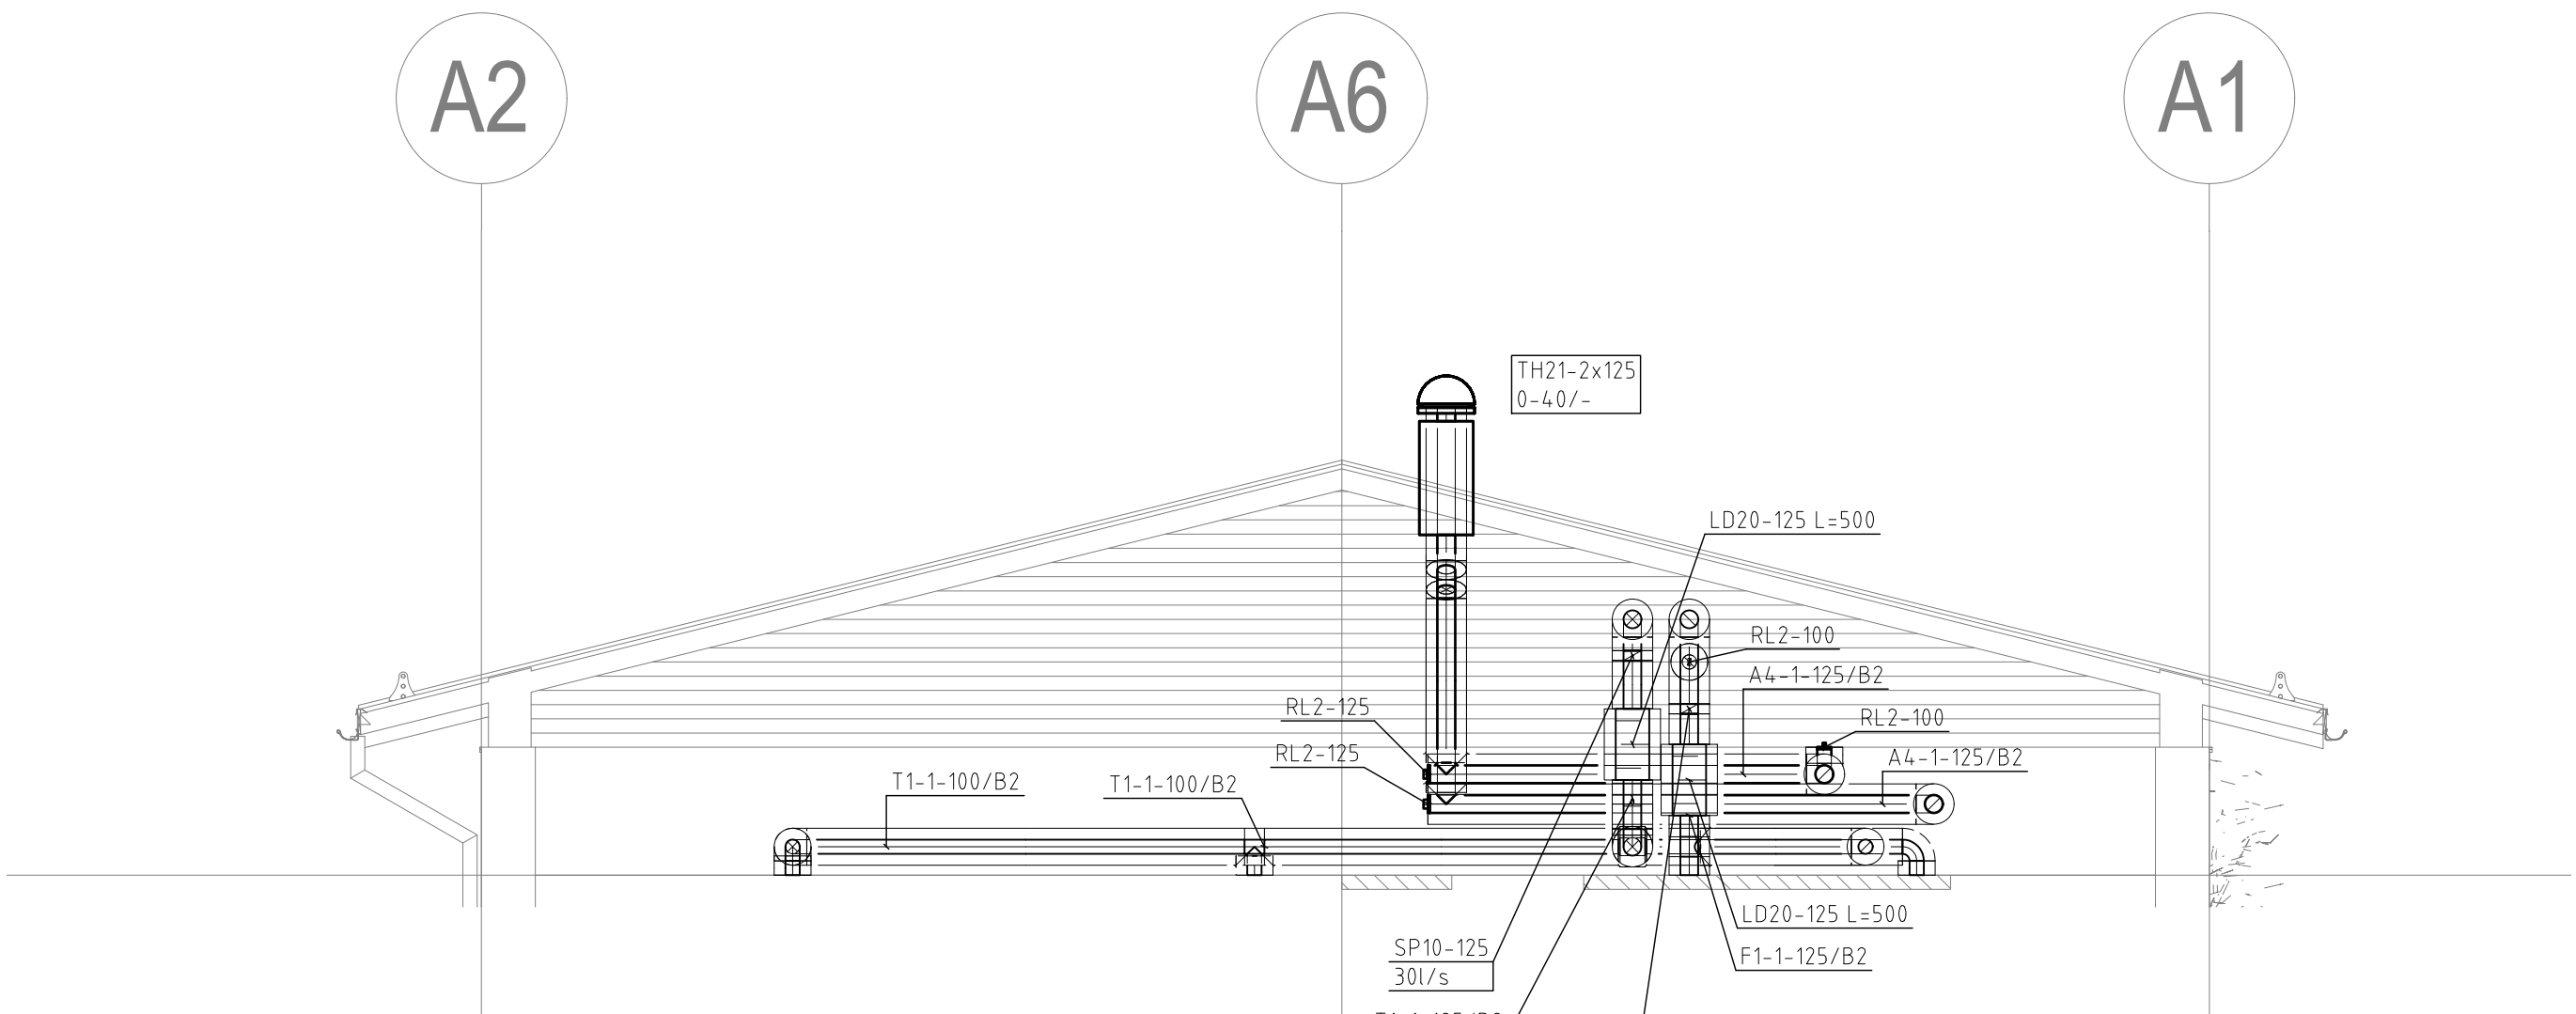


C - C

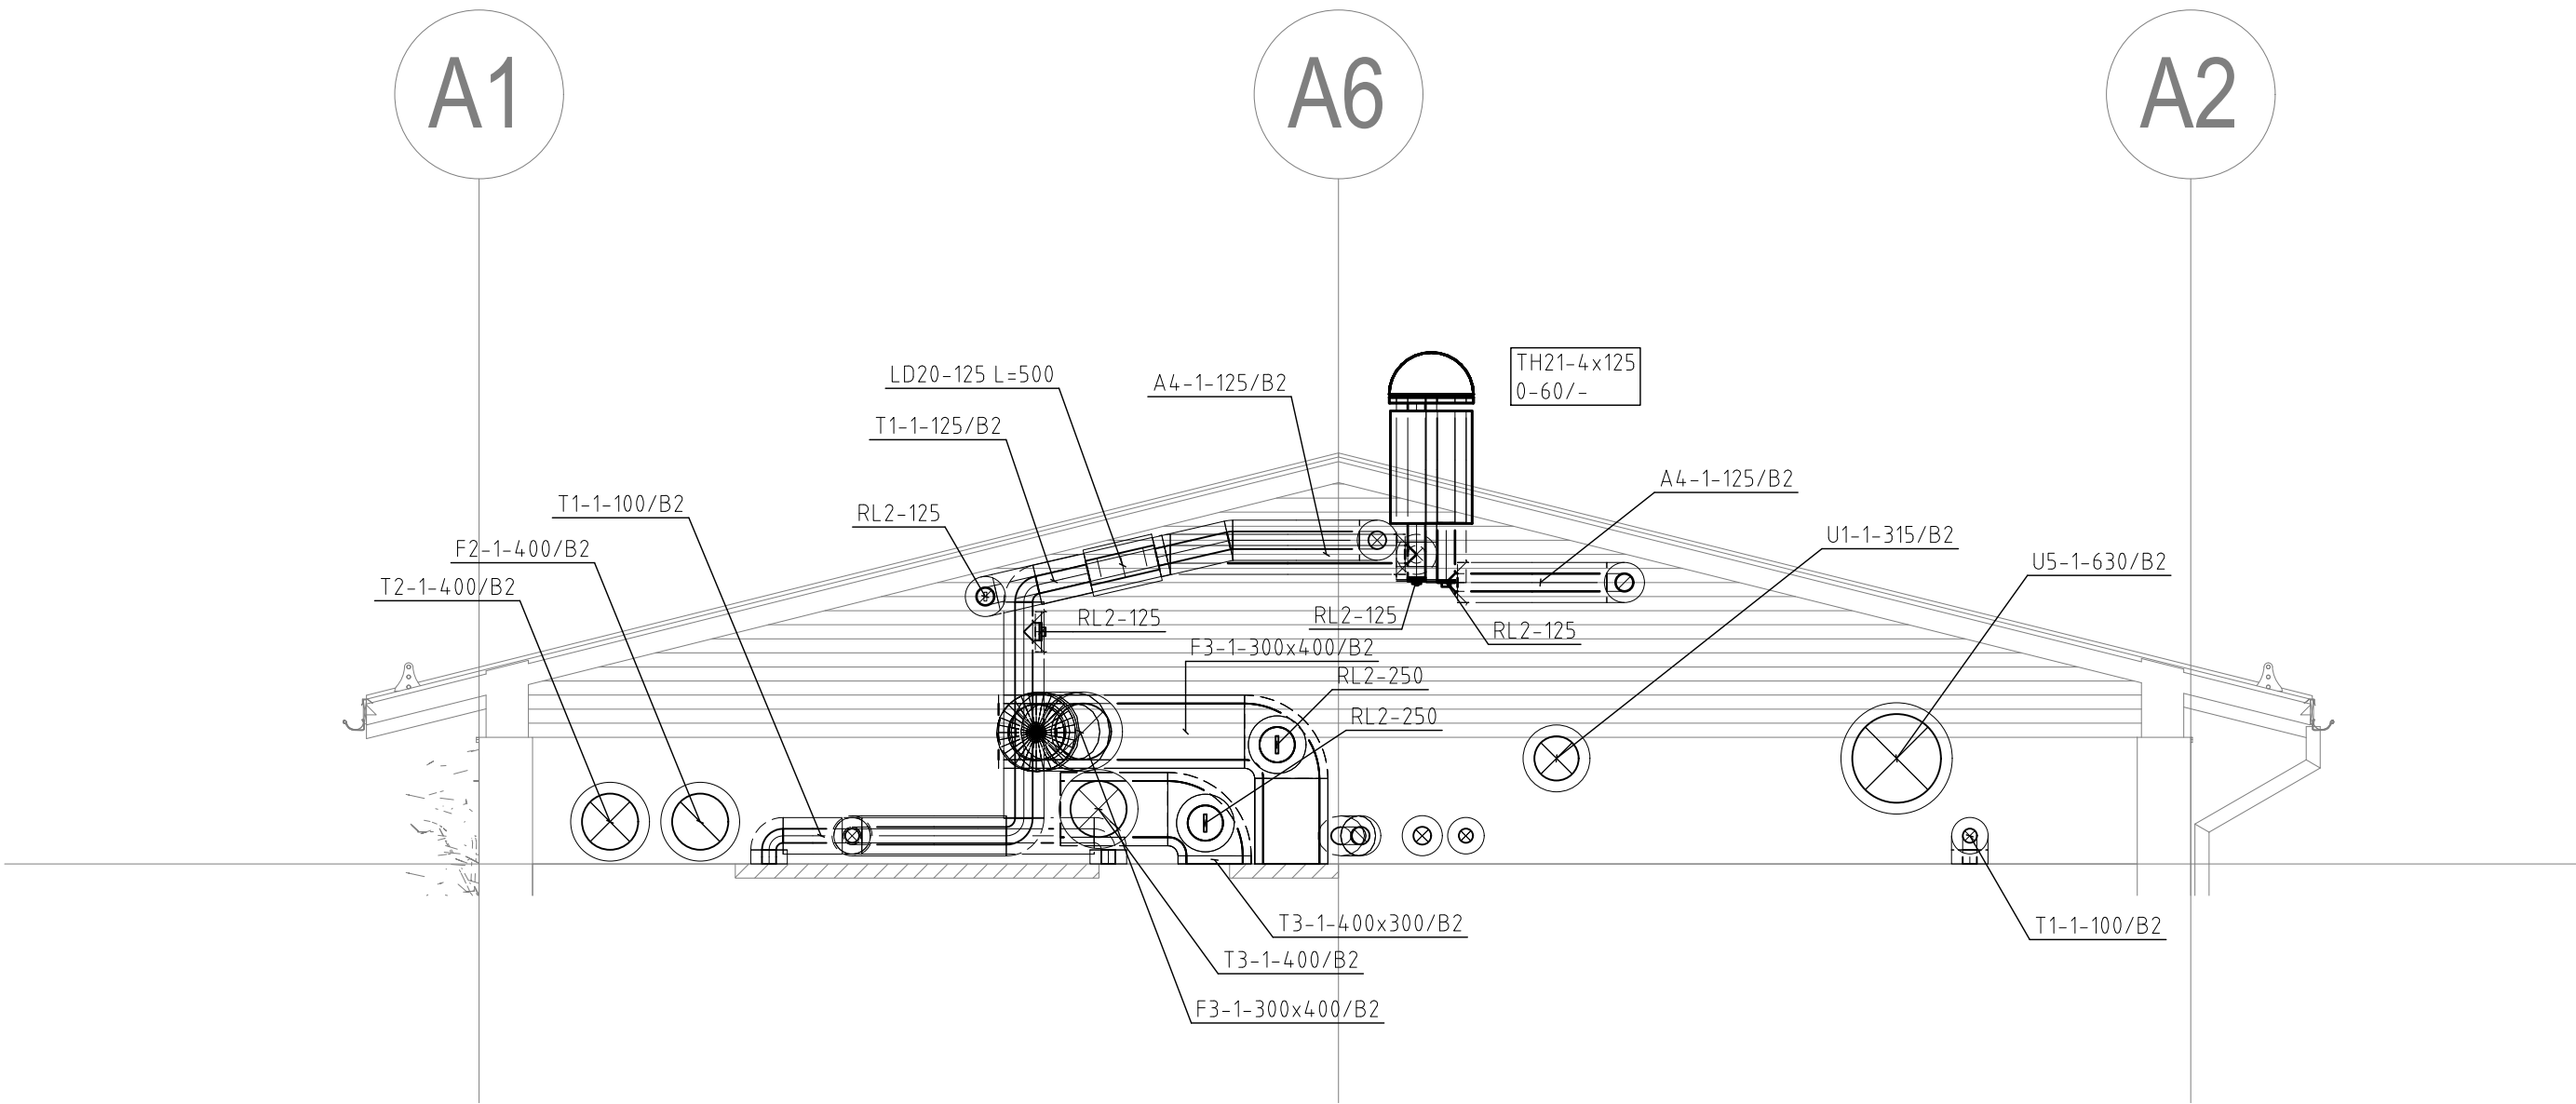

D - D

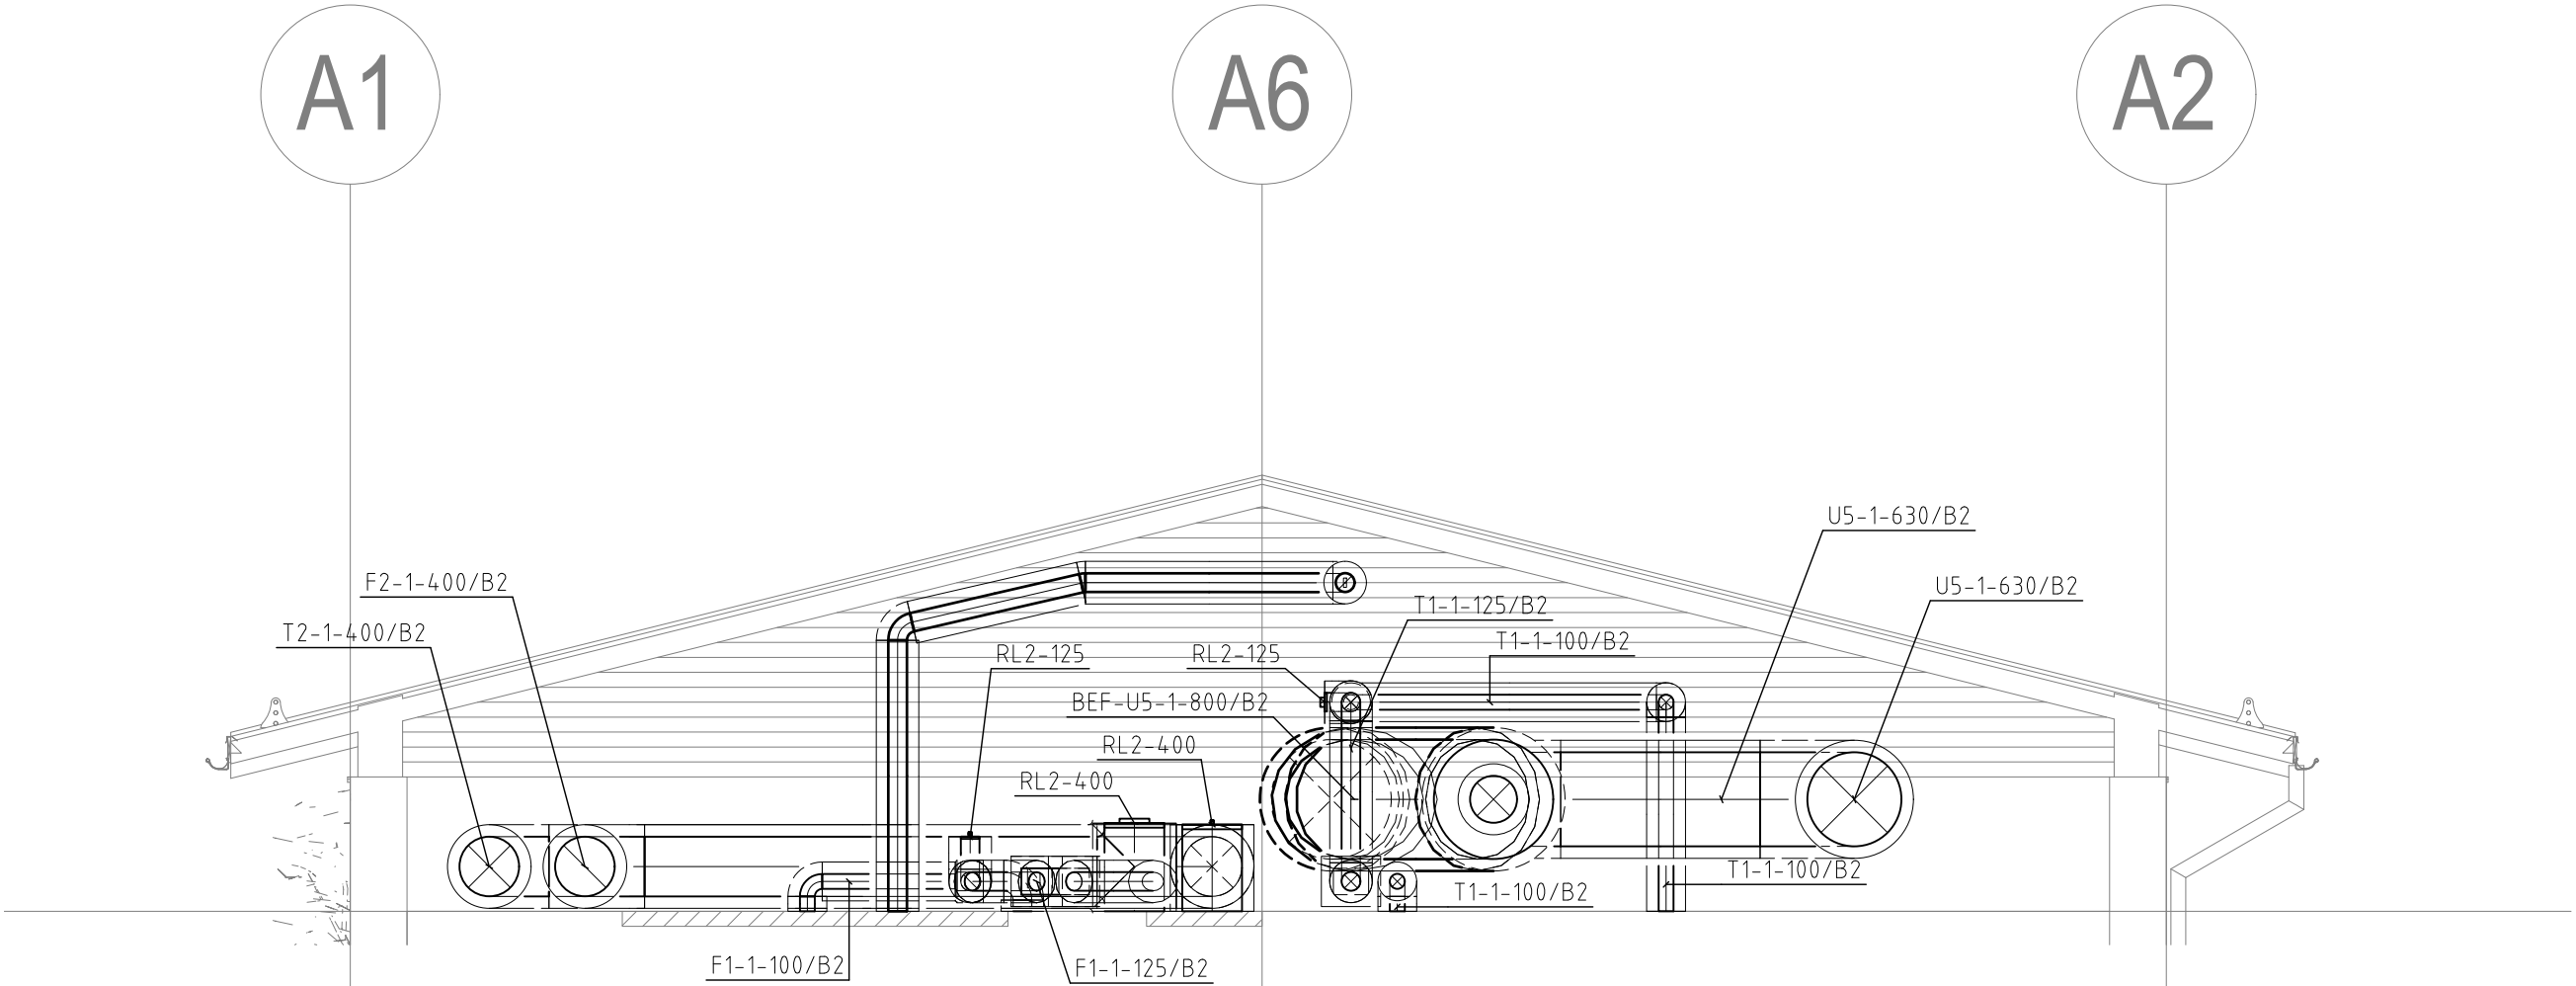


E - E

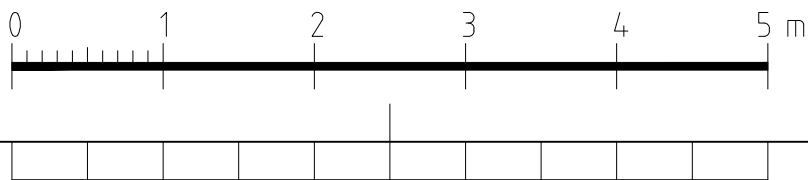

FÖRKLARINGAR

MEDIA	
A	AVLUFT
F	FRÅNLUFT
T	TILLUFT
U	UTELUFT
Ö	ÖVERLUFT
SYSTEM	
1	LUFTBEHANDLING LB11, LÄGENHETER
2	LUFTBEHANDLING LB12, BIBLIOTEK
3	LUFTBEHANDLING LB13, FRITIDSLOKALER
4	SPISFLÄKT LÄGENHETER
5	GEMENSAMM UTELUFT
MATERIAL	
1	VARMFÖRZINKAD STÅLPLÅT
4	VARMFÖRZINKAD STÅLPLÅT, PULVERLACKERAD
DIMENSION	
ISOLERING	
B2	UTV. BRANDISOLERING MINERALULL EI60
K3	UTV. KONDENSISOLERING 25mm CELLGUMMI

LUFTFLÖDEN ANGES I l/s.
KANALDIMENSION SAMMA SOM DONANSLOTNING DÄR
EJ ANNAT ANGES.
HÖJDER PÅ KANALER ANGES MED CENTRUM KANAL I MM
ÖVER FÄRDIGT GÖLV..

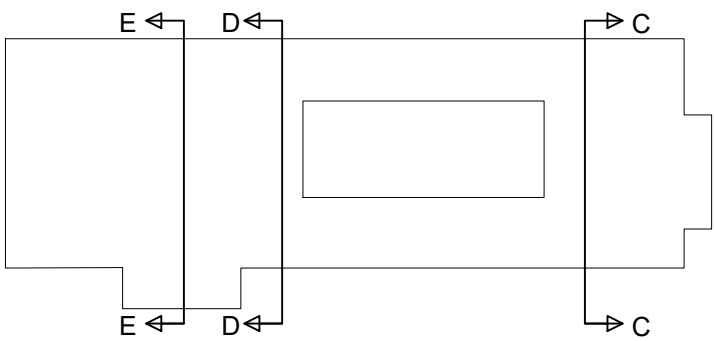

FÖRFRÅGNINGSUNDERLAG		STATUS
BYGGHANDLING		HANDLING
DATUM	2025-02-26	ÄNDRING
PROJEKT		
CENTRUMHUSET HUS D KRÅKAN 1, ROBERTSFORS		ANSVARIG PART
AFRY-Infrastructure AB Storgatan 103 921 32 Lycksele Tel: 010-505 00 00		AFRY
Simon Rudin	KONTAKTPERSON	Marzena Januszewska-Kut
Simon Abrahamsson	GODKÄND AV	D0182343 (210550)
PLANRITNING	RITNINGSKATEGORI	
OMBYGGNAD BIBLIOTEK OCH LÄGENHETER PLAN 30, SEKTION C-C, D-D, E-E LUFTBEHANDLING	INNEHÅLL	FORMAT
	A1	SKALA
	1:50	BET
V-57-2-D001		