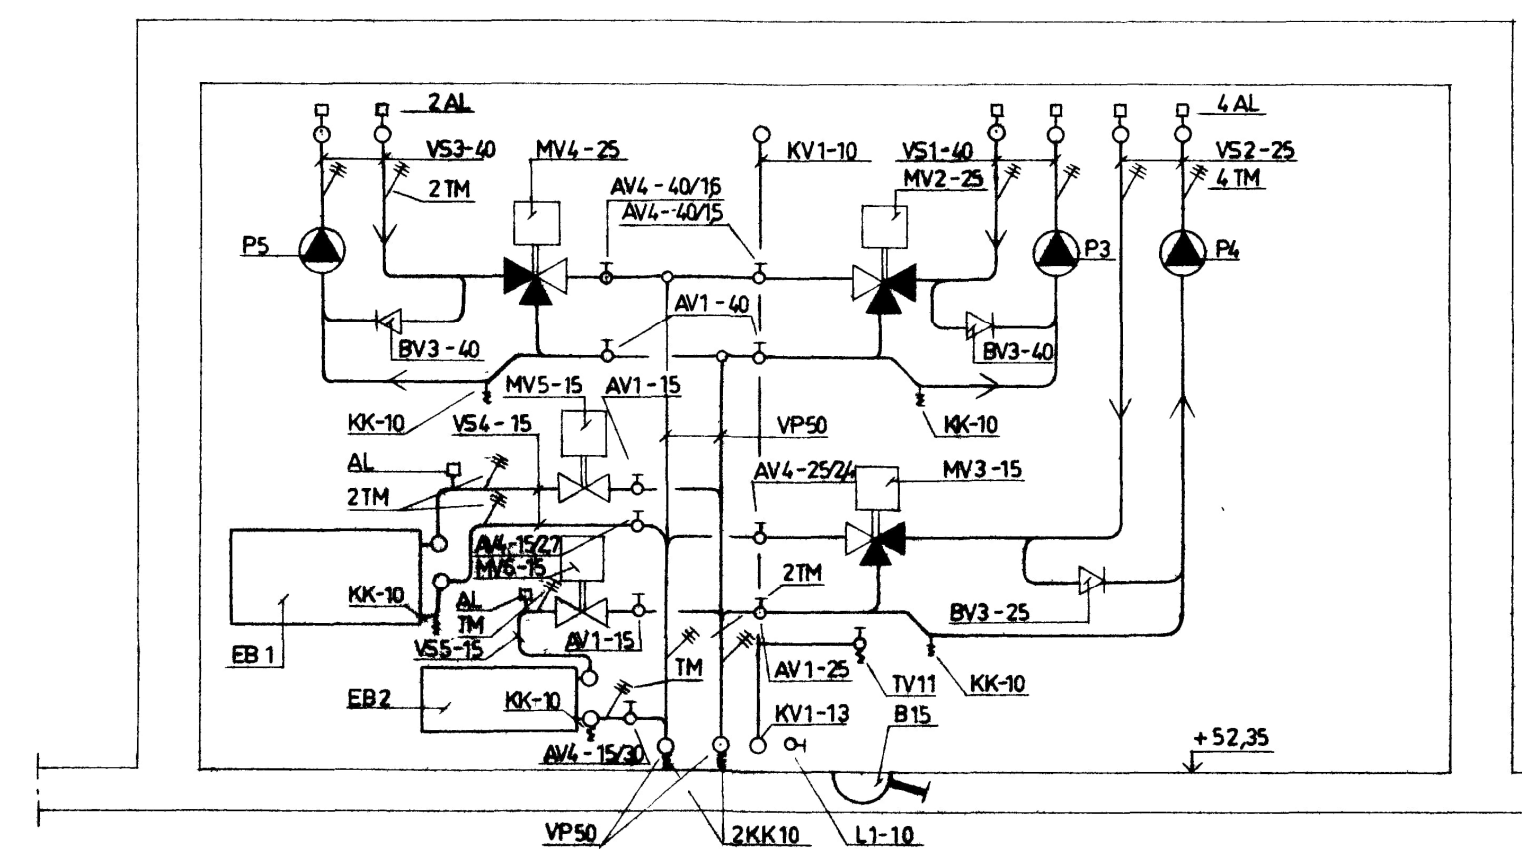
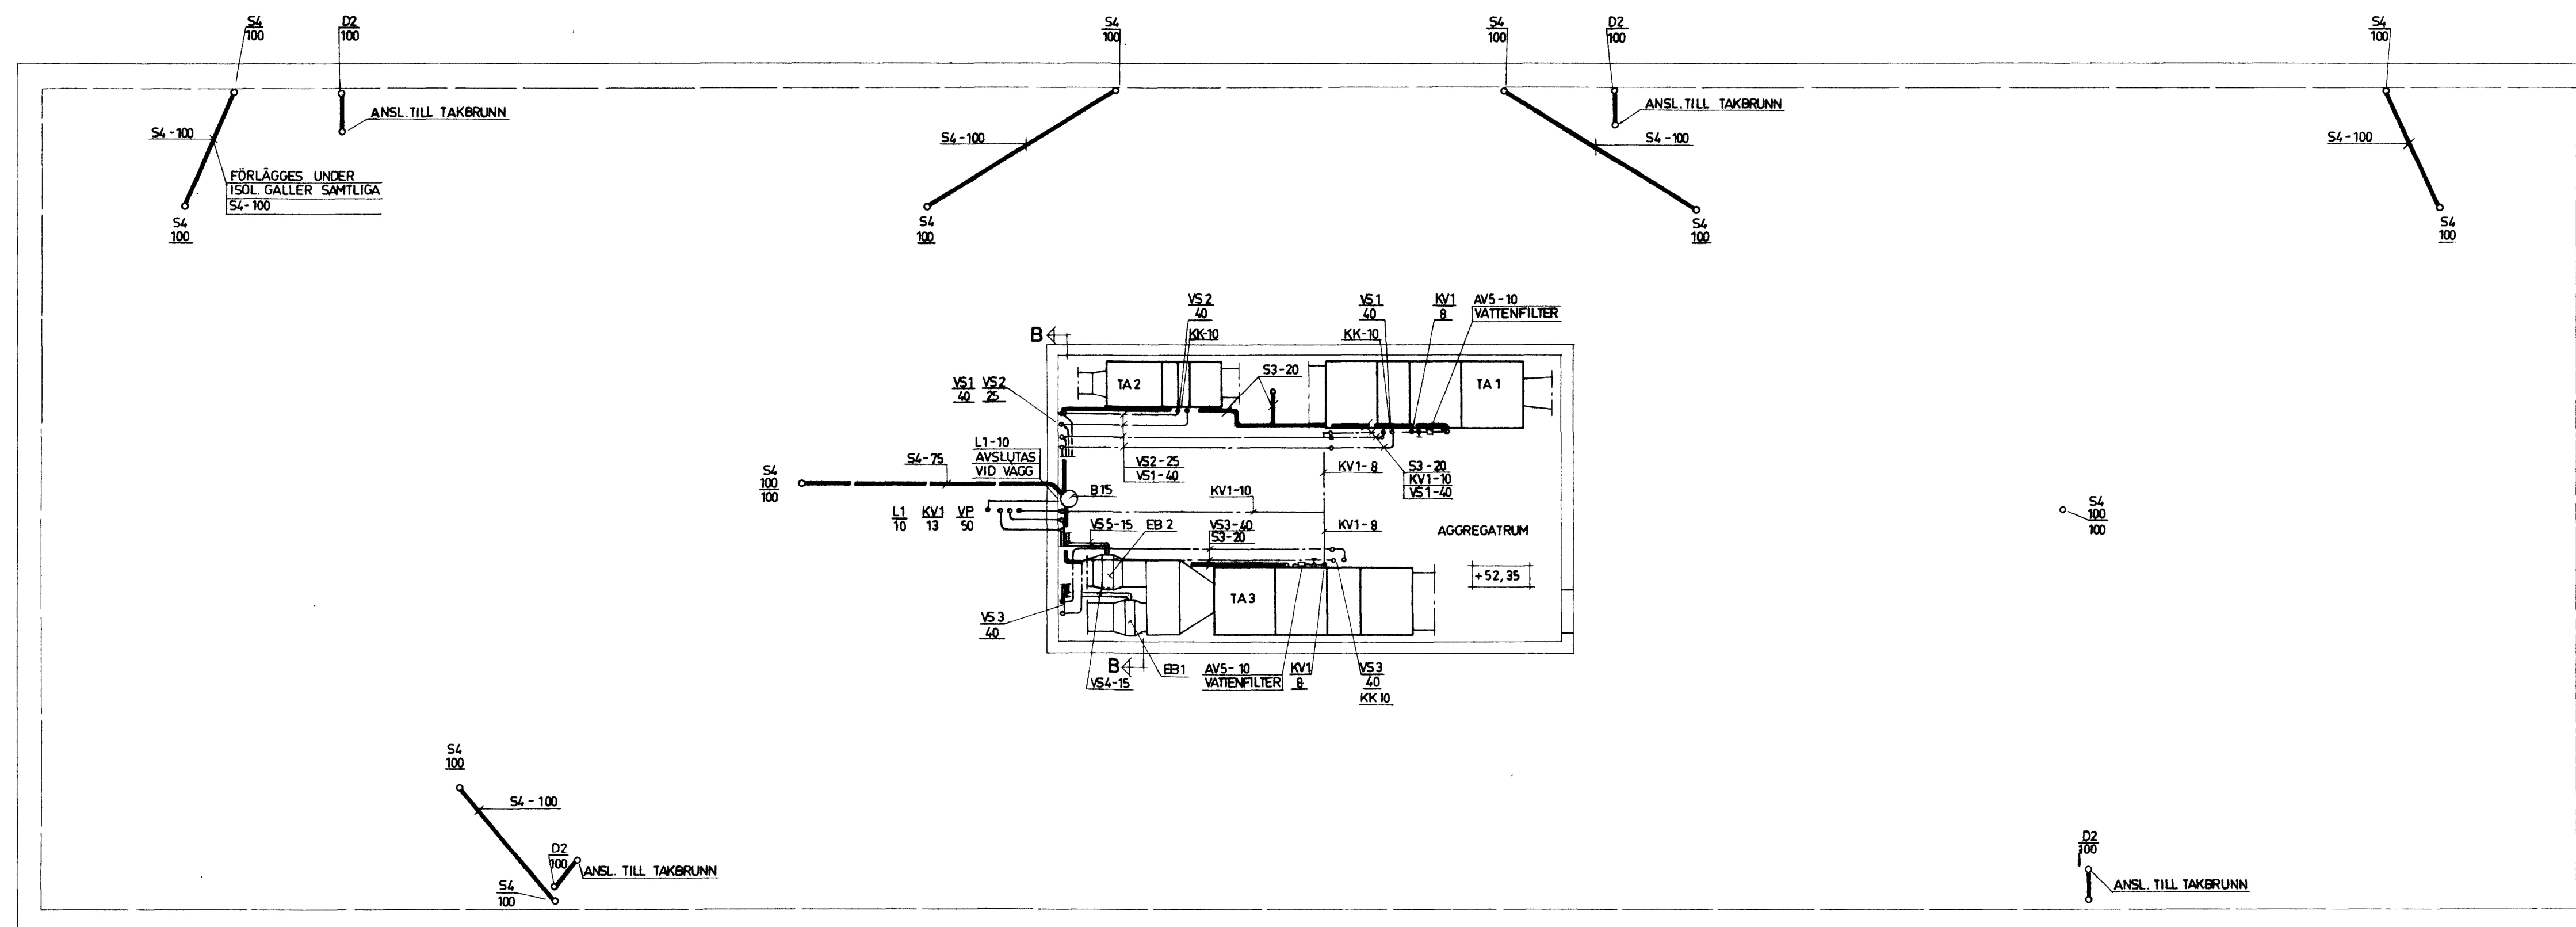


BESKRIVNING

D 15	GOLVAVRIN
AV 5	SKIVVENTIL
TV 11	SKIVVENTIL
--	VÄTTEPILDR
AV 4	STRYKVENTIL
AV 1	SKIVVENTIL
KK	KIKKOKRAN
AL	LÖPLOCKA
DV 5	BACVENTIL
TH	FÄRMÖRETER
P 3	OMMÄTLINGSPEL
P 4	- " -
P 5	- " -

B-B
SKALA 1:20

RAGNAR SANDSTRÖM INGENJÖRSBYRÅ AB UMEA SKELLEFTEA			CENTRUMHUS I ROBERTSFORS Tillbyggnad D Apotek VVS-ANLÄGGNINGAR Takplan		
KF	K	G	H-E.J.	DATUM	SKALA
HANDLAGGES AV H-E. JONSSON				26. 2. 1971	1:50
				ARBETS NR. 947	RITN. NR. 56:14