


..\\A11 - Modeller\\Export DWG\\A-40-P-D090-Centrumhuset Inredning - Bygglös-vv11-A-40-P-D090.dwg

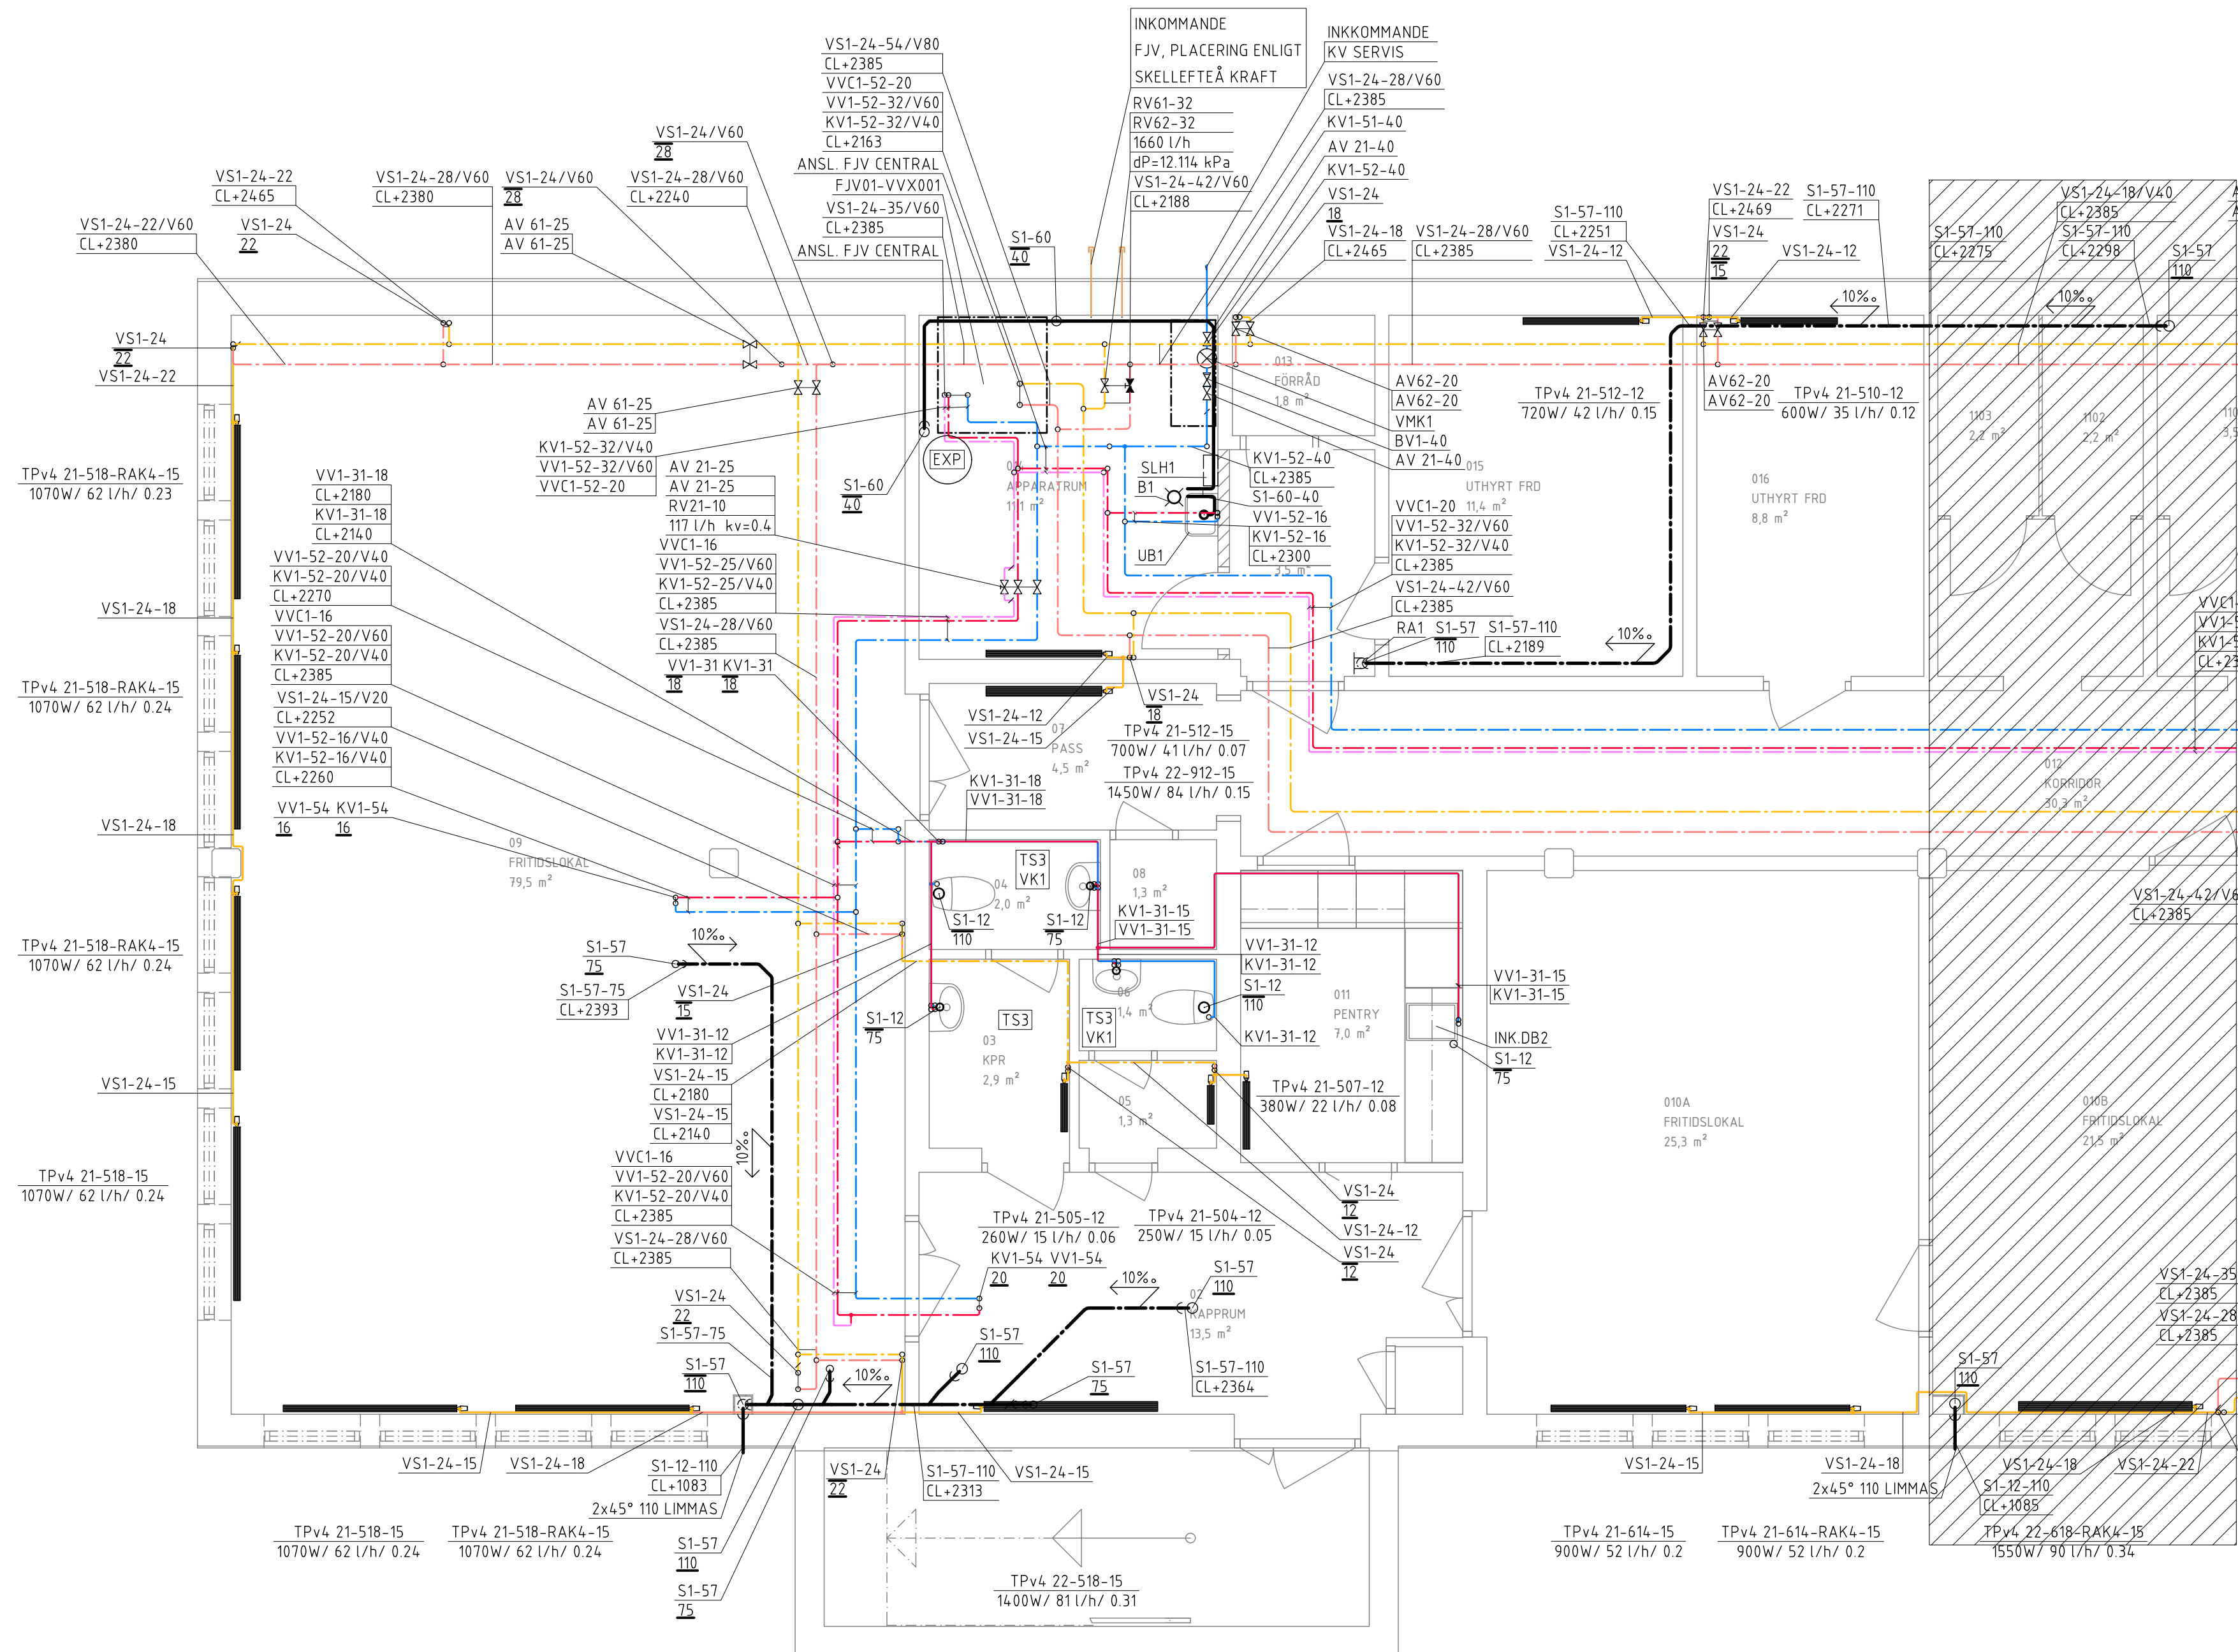

FÖRKLARINGAR

VS1-24-28/V60

SYSTEM

KV1	TAPPKALLVATTEN
VV1	TAPPVARMVATTEN
VVC1	VARMVATTENCIRKULATION
VP1	VÄRMESYSTEM, PRIMÄRSIDA
VS1	VÄRMESYSTEM, SEK. HUVUDSYSTEM
VS2	VÄRMESYSTEM, SEK. LÜFTBEHANDLING
S1	SPILLVATTEN SANITÄRT

MATERIAL

12	PP-MARKAVLOPPSRÖR
24	ELFÖRZINKADE STÅLRÖR
30	KOPPARRÖR EN 1050-290
31	FÖRKROMADE KOPPARRÖR
51	PEM SLANG PN16
52	LK PAL UNIVERSALRÖR, A, RAKA LÄNGDER
54	LK PE-X UNIVERSALRÖR, RIR EXTRA
	EXTRAISOLERADE TOMRÖR
57	WAVIN ASTO PLUS
60	ABS RÖR

DIMENSION

DIMENSION PÅ PAL, PEX, KOPPARRÖR OCH
ELFÖRZINKADE RÖR ANGES MED YTTERMÅTT I Dy I mm.

TERMISK ISOLERING

V40	VÄRMEISOLERING 40 MM (PAROC RÖRSKÅL).
V60	VÄRMEISOLERING 60 MM (PAROC RÖRSKÅL).

VVC SAMISOLERAS TILLSAMMANS MED VV.

LÜFTLEDNINGAR FÖR SPILLVATTNET I KALLVINDEN ISOLERAS
MED VÄRMEISOLERING 50 MM NÄTMATTA AV MINERALULL (V50).

YTBEKLÄDNAD

SYNLIGA ISOLERADE LEDNINGAR YTBEKLÄDES TYP
MÖNSTERPRÄGLAD ALUMINIUMPLÅT ELLER LIKVÄRDIGT.

TAPPVATTEN

SYNLIG LEDNINGSDRAGNING I RW, WC, STÅD OCH KÖK UTFÖRES
OISOLERAT OCH I FÖRKROMAT UTFÖRANDE.

TAPPVATTENRÖR DRAGNA FRÅN FS101 KLAMRAS MOT
BJÄLKLAG TILL TAPPSTALL.


VID ÖVERGÅNG FRÅN STÅENDE TILL LIGGANDE AVLOPPSSTAM
SKA ÖVERGÅNGEN UTFÖRAS MED 2x45° BÖJAR.

SAMTLIGA ÖPPNA RÖRANDAR TÄCKS MED LOCK.

HÖJDER PÅ VÄRME OCH TAPPVATTEN ANGES MED +HÖJD
CENTRUM RÖR.

HÖJDER PÅ SPILLVATTENLEDNINGAR ANGES MED
MED CL ÖFG.

ANSLUTNINGSLIDNINGAR DIM			
SAKVÄRA	KV DIM	VV DIM	S DIM
TVÄTTSTALL	12	12	75
TOALETSTÖL	12	-	110
UTSLÄGSBACK	15	15	-
DISKLÄDSBL.	15	15	75
DUSCHBL.	15	15	-
GÖLYBRUNN.	-	-	75

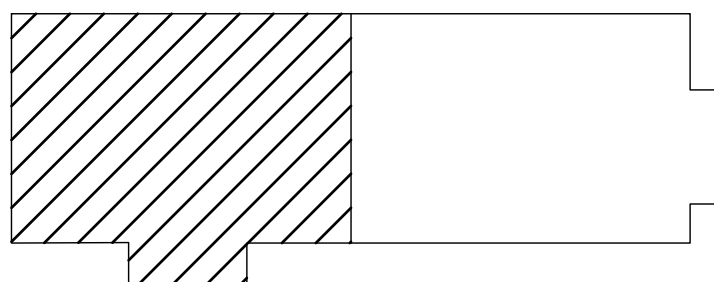

FÖRFRÅGNINGSUNDERLAG		STATUS
BYGGHANDLING		HANDLING
DATUM 2025-02-26	ÄNDRING/PM	ÄNDRING
CENTRUMHUSET HUS D KRÅKAN 1, ROBERTSFORS		PROJEKT
AFRY-Infrastructure AB Storgatan 103 921 32 Lycksele Tel: 010-505 00 00		ANSVÄRIG PART
Simon Rudin	KONTAKTPERSON Alexander Östlund	SKAPAD AV
Simon Abrahamsson	GODKÄND AV D0182343 (210550)	UPPDRAGSNUMMER
PLANRITNING		RITNINGSKATEGORI
OMBYGGNAD BIBLIOTEK OCH LÄGENHETER KÄLLARPLAN - PLAN 09 - DEL 1		INNEHÅLL
VS-INSTALLATIONER		FORMAT A1
V-50-1-D091		SKALA 1:50
		NUMMER BET