


..\\..\\A11 - Modeller\\Export DWG\\A-40-P-D090-Centrumhuset\\Inredning - Bygglav-rv\\1-A-40-P-D090.dwg - AFRY Documents\\A-40-P-D090-Centrumhuset\\Inredning - Bygglav-rv\\1-A-40-P-D090.dwg

LAGER: SB11

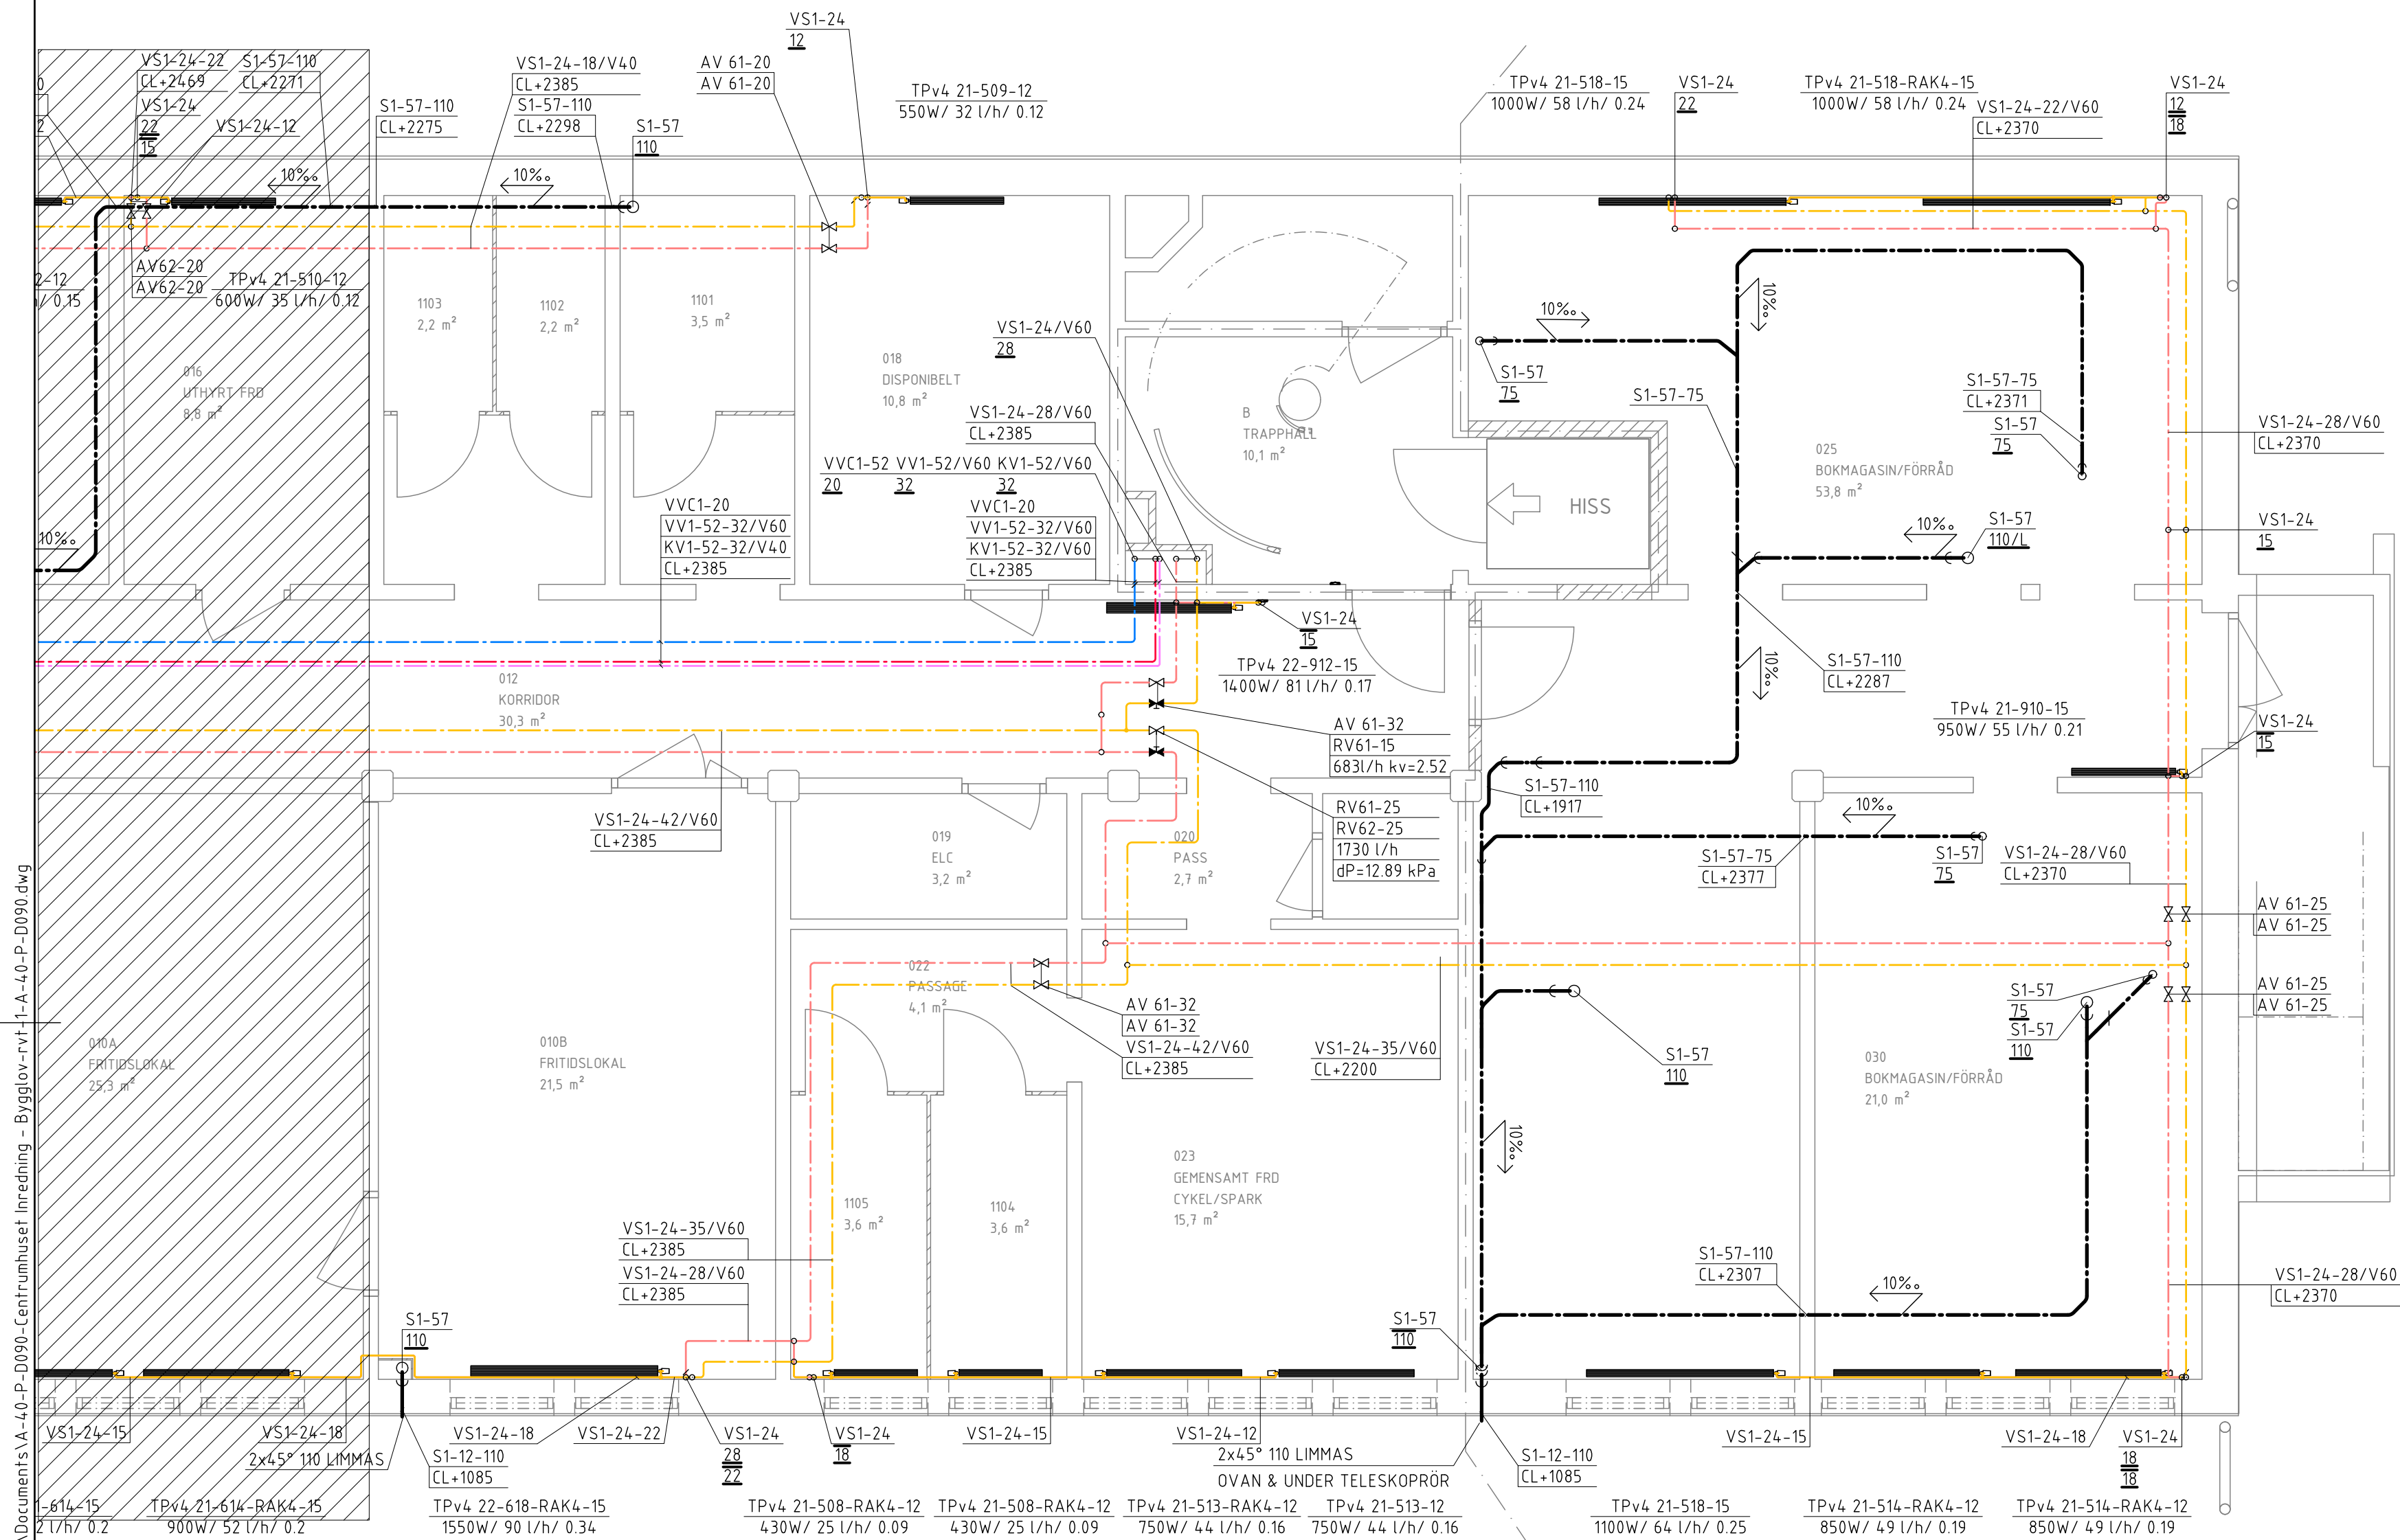

FÖRKLARINGAR

VS1-24-28/V60

SYSTEM	
KV1	TAPPKALLVATTEN
VV1	TAPPVARMVATTEN
VVC1	VARMVATTENCIRKULATION
VP1	VÄRMESYSTEM, PRIMÄRSIDA
VS1	VÄRMESYSTEM, SEK. HUVUDSYSTEM
VS2	VÄRMESYSTEM, SEK. LÜFTBEHANDLING
S1	SPILLVATTEN SANITÄRT

MATERIAL

12	PP-MARKAVLOPPSRÖR
24	ELFÖRZINKADE STÅLRÖR
30	KOPPARRÖR EN 1050-290
31	FÖRKROMADE KOPPARRÖR
51	PEM SLANG PN16
52	LK PAL UNIVERSALRÖR, A, RAKA LÄNGDER
54	LK PE-X UNIVERSALRÖR, RIR EXTRA
57	EXTRAISOLERADE TOMRÖR
60	WAVIN ASTO PLUS
60	ABS RÖR

DIMENSION

DIMENSION PÅ PAL, PEX, KOPPARRÖR OCH
ELFÖRZINKADE RÖR ANGES MED YTTERMÄTT I Dy I mm.

TERMISK ISOLERING

V40 VÄRMEISOLERING 40 MM (PAROC RÖRSKÅL).
V60 VÄRMEISOLERING 60 MM (PAROC RÖRSKÅL).

VVC SAMISOLERAS TILLSAMMANS MED VV.

LÜFTLEDNINGAR FÖR SPILLVATTNET I KALLVINDEN ISOLERAS
MED VÄRMEISOLERING 50 MM NÄTMATTA AV MINERALULL (V50).

YTBEKLÄDNAD

SYNLIGA ISOLERADE LEDNINGAR YTBEKLÄDES TYP
MÖNSTERPRÄGLAD ALUMINIUMPLÅT ELLER LIKVÄRDIGT.

TAPPVATTEN

SYNLIG LEDNINGSDRAGNING I RW, WC, STÅD OCH KÖK UTFÖRES
OISOLERAT OCH I FÖRKROMAT UTFÖRANDE.

TAPPVATTENRÖR DRAGNA FRÅN FS101 KLAMRAS MOT
BJÄLKLAG TILL TAPPSTALL.


VID ÖVERGÅNG FRÅN STÅENDE TILL LIGGANDE AVLOPPSSTAM
SKA ÖVERGÅNGEN UTFÖRAS MED 2x45° BÖJAR.

SAMTLIGA ÖPPNA RÖRANDAR TÄCKS MED LOCK.

HÖJDER PÅ VÄRME OCH TAPPVATTEN ANGES MED +HÖJD
CENTRUM RÖR.

HÖJDER PÅ SPILLVATTENLEDNINGAR ANGES MED
MED CL ÖFG.

ANSLUTNINGSLIDNINGAR DIM			
SAKVÄRA	KV DIM	VV DIM	S DIM
TVÄTTSTALL	12	12	75
TOILETTSTÖL	12	-	110
UTSLAGSBACK	15	15	-
DISKLÄDSBL.	15	15	75
DUSCHBL.	15	15	-
GÖLYVBUNN.	-	-	75

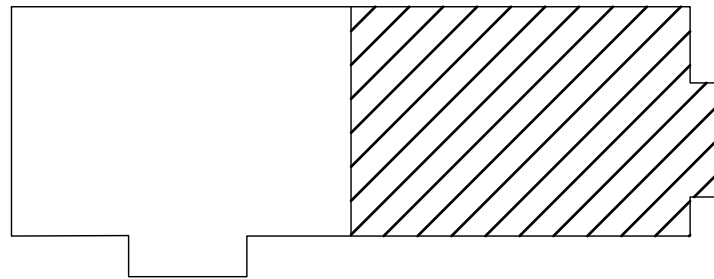

FÖRFRÅGNINGSUNDERLAG

STATUS

BYGGHANDLING

HANDLING

DATUM 2025-02-26

ÄNDRING/PM

ÄNDRING

CENTRUMHUSET HUS D KRÅKAN 1, ROBERTSFORS

PROJEKT

AFRY-Infrastructure AB

Storgatan 103
921 32 Lycksele
Tel: 010-505 00 00



KONTAKTPERSON Alexander Östlund

SKAPAD AV

Simon Rudin

GODKÄND AV D0182343 (210550)

UPPDRAGSNUMMER

Simon Abrahamsson

RITNINGSKATEGORI

PLANRITNING

OMBYGGNAD BIBLIOTEK OCH LÄGENHETER

KÄLLARPLAN - PLAN 09 - DEL 2

VS - INSTALLATIONER

V-50-1-D092

INNEHÅLL

FORMAT

A1

SKALA

1:50

NUMMER

BET