


\\V50-s1ramp.dwg \\\1\1 - Modeller\Export DWG\A-40-P-D100.dwg

LAGER: SB11

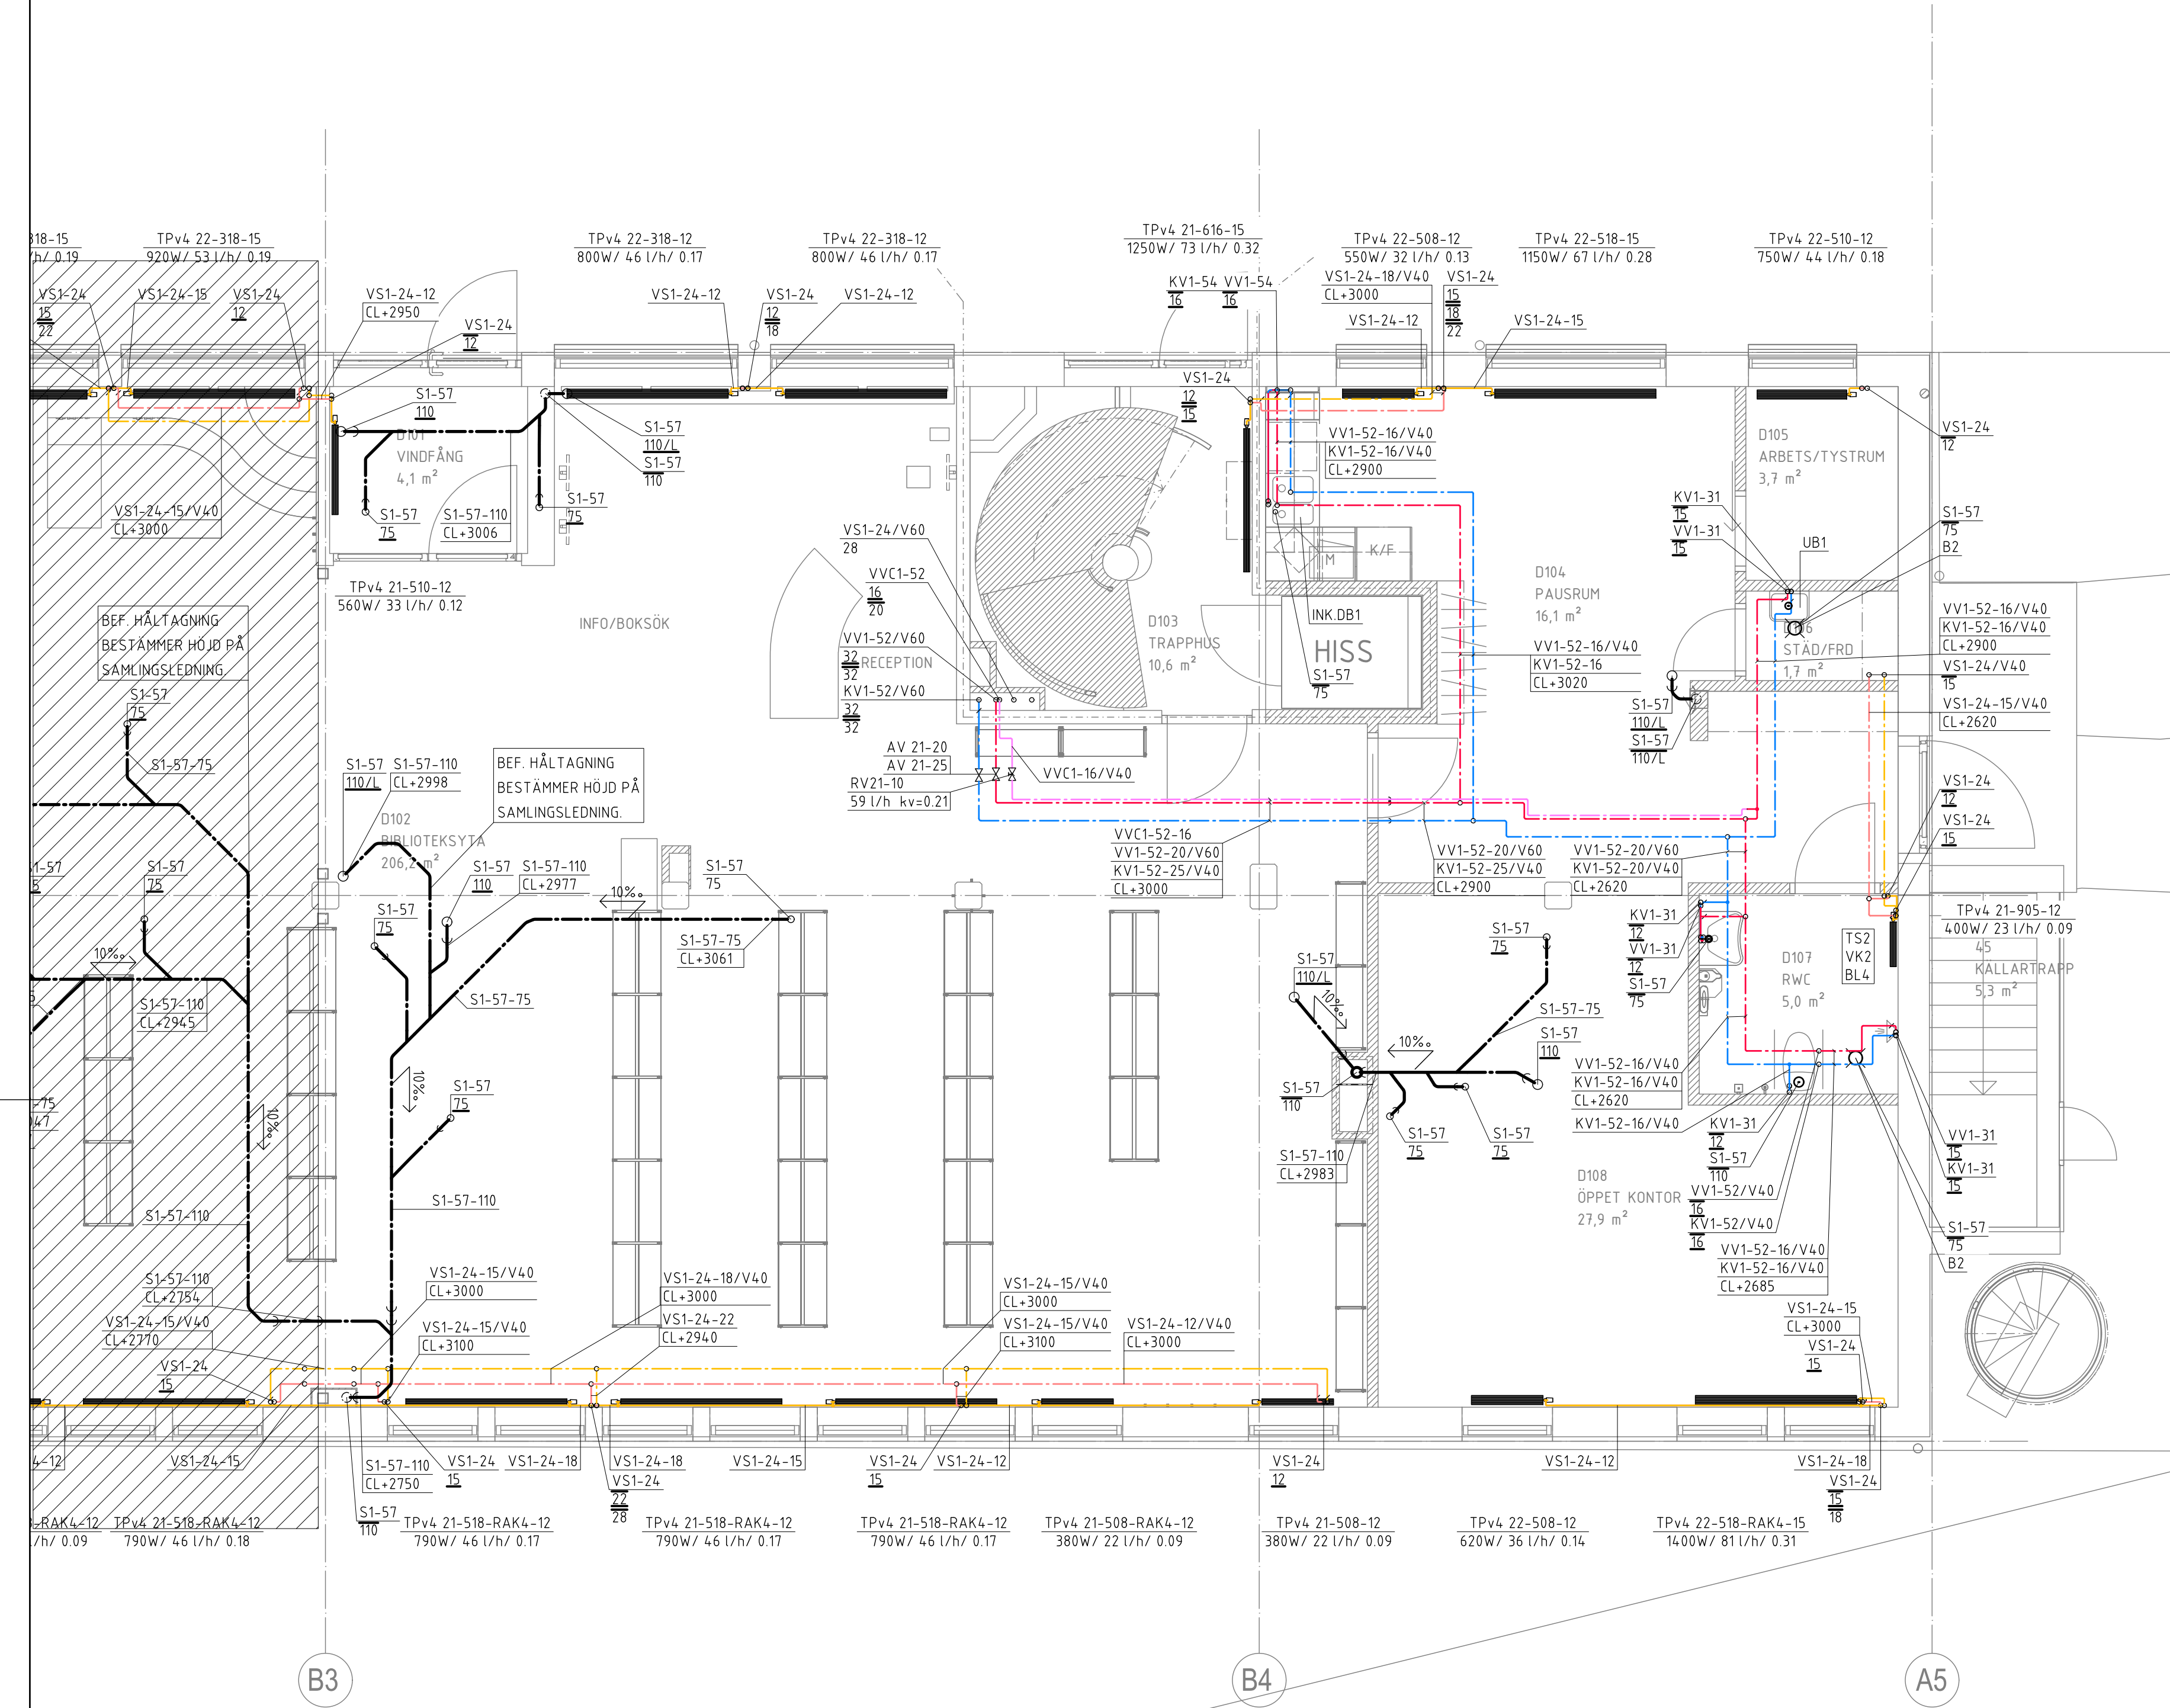

FÖRKLARINGAR

VS1-24-28/V60

SYSTEM

KV1	TAPPKALLVATTEN
VV1	TAPPVARMVATTEN
VVC1	VARMVATTENCIRKULATION
VP1	VÄRMESYSTEM, PRIMÄRSIDA
VS1	VÄRMESYSTEM, SEK. HUVUDSYSTEM
VS2	VÄRMESYSTEM, SEK. LÜFTBEHANDLING
S1	SPILLVATTEN SANITÄRT

MATERIAL

12	PP-MARKAVLOPPSRÖR
24	ELFÖRZINKADE STÅLRÖR
30	KOPPARRÖR EN 1050-290
31	FÖRKROMADE KOPPARRÖR
51	PEM SLANG PN16
52	LK PAL UNIVERSALRÖR, A, RAKA LÄNGDER
54	LK PE-X UNIVERSALRÖR, RIR EXTRA EXTRAISOLERADE TOMRÖR
57	WAVIN ASTO PLUS
60	ABS RÖR

DIMENSION

DIMENSION PÅ PAL, PEX, KOPPARRÖR OCH ELFÖRZINKADE RÖR ANGES MED YTTERMÄTT I Dy I mm.

TERMISK ISOLERING

V40	VÄRMEISOLERING 40 MM (PAROC RÖRSKÅL).
V60	VÄRMEISOLERING 60 MM (PAROC RÖRSKÅL).

VVC SAMISOLERAS TILLSAMMANS MED VV.

LÜFTLEDNINGAR FÖR SPILLVATTNET I KALLVINDEN ISOLERAS MED VÄRMEISOLERING 50 MM NÄTMATTA AV MINERALULL (V50).

YTBEKLÄDNAD
SYNLIGA ISOLERADE LEDNINGAR YTBEKLÄDES TYP MÖNSTERPRÄGLAD ALUMINIUMPLÅT ELLER LIKVÄRDIGT.

TAPPVATTEN
SYNLIG LEDNINGSDRAGNING I RWC, WC, STÅD OCH KÖK UTFÖRES OISOLERAT OCH I FÖRKROMAT UTFÖRANDE.

TAPPVATTENRÖR DRAGNA FRÅN FS101 KLAMRAS MOT BJÄLKLAG TILL TAPPSTALL.

VID ÖVERGÅNG FRÅN STÅENDE TILL LIGGANDE AVLOPPSSAMSKA ÖVERGÅNGEN UTFÖRAS MED 2x45° BÖJAR.

SAMTLIGA ÖPPNA RÖRANDAR TÄCKS MED LOCK.

HÖJDER PÅ VÄRME OCH TAPPVATTEN ANGES MED +HÖJD CENTRUM RÖR.

HÖJDER PÅ SPILLVATTENLEDNINGAR ANGES MED MED CL ÖFG.

ANSLUTNINGSLEDNINGAR DIM			
SAKVARA	KV DIM	VV DIM	S DIM
TVÄTTSTALL	12	12	75
TOILETTSTOL	12	-	110
UTSLAGSBÄCK	15	15	-
DISKLÄDSBL.	15	15	75
DUSCHBL.	15	15	-
GOLVBRUNN.	-	-	75

FÖRFRÅGNINGSUNDERLAG

STATUS

BYGGHANDLING

HANDLING

DATUM 2025-02-26

ÄNDRING/PM

ÄNDRING

CENTRUMHUSET HUS D KRÅKAN 1, ROBERTSFORS

PROJEKT

AFRY-Infrastructure AB
Storgatan 103
921 32 Lycksele
Tel: 010-505 00 00



ANSVÄRIG PART

Simon Rudin

KONTAKTPERSON

Alexander Östlund

SKAPAD AV

Simon Abrahamsson

GODKÄND AV

D0182343 (210550)

UPPDRAGSNUMMER

PLANRITNING

RITNINGSKATEGORI

OMBYGGNAD BIBLIOTEK OCH LÄGENHETER
BOTTEPLAN - PLAN 10 - DEL 2
VS - INSTALLATIONER

INNEHÅLL

FORMAT

A1

SKALA

1:50

NUMMER

BET

V-50-1-D102

