
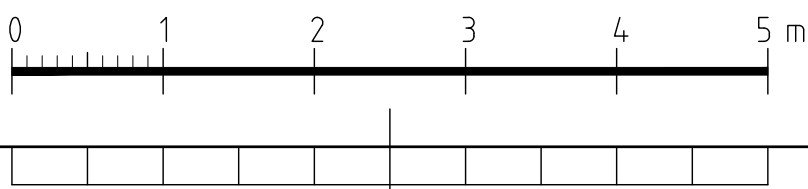


X:\L-Transit\Entries\TM\Uppdrag 2021\210550 Kråkan 1 - Modell\VS0-stamp.dwg X:\L-Transit\Entries\TM\Uppdrag 2021\210550 Kråkan 1 - Modell\VS0-stamp.dwg

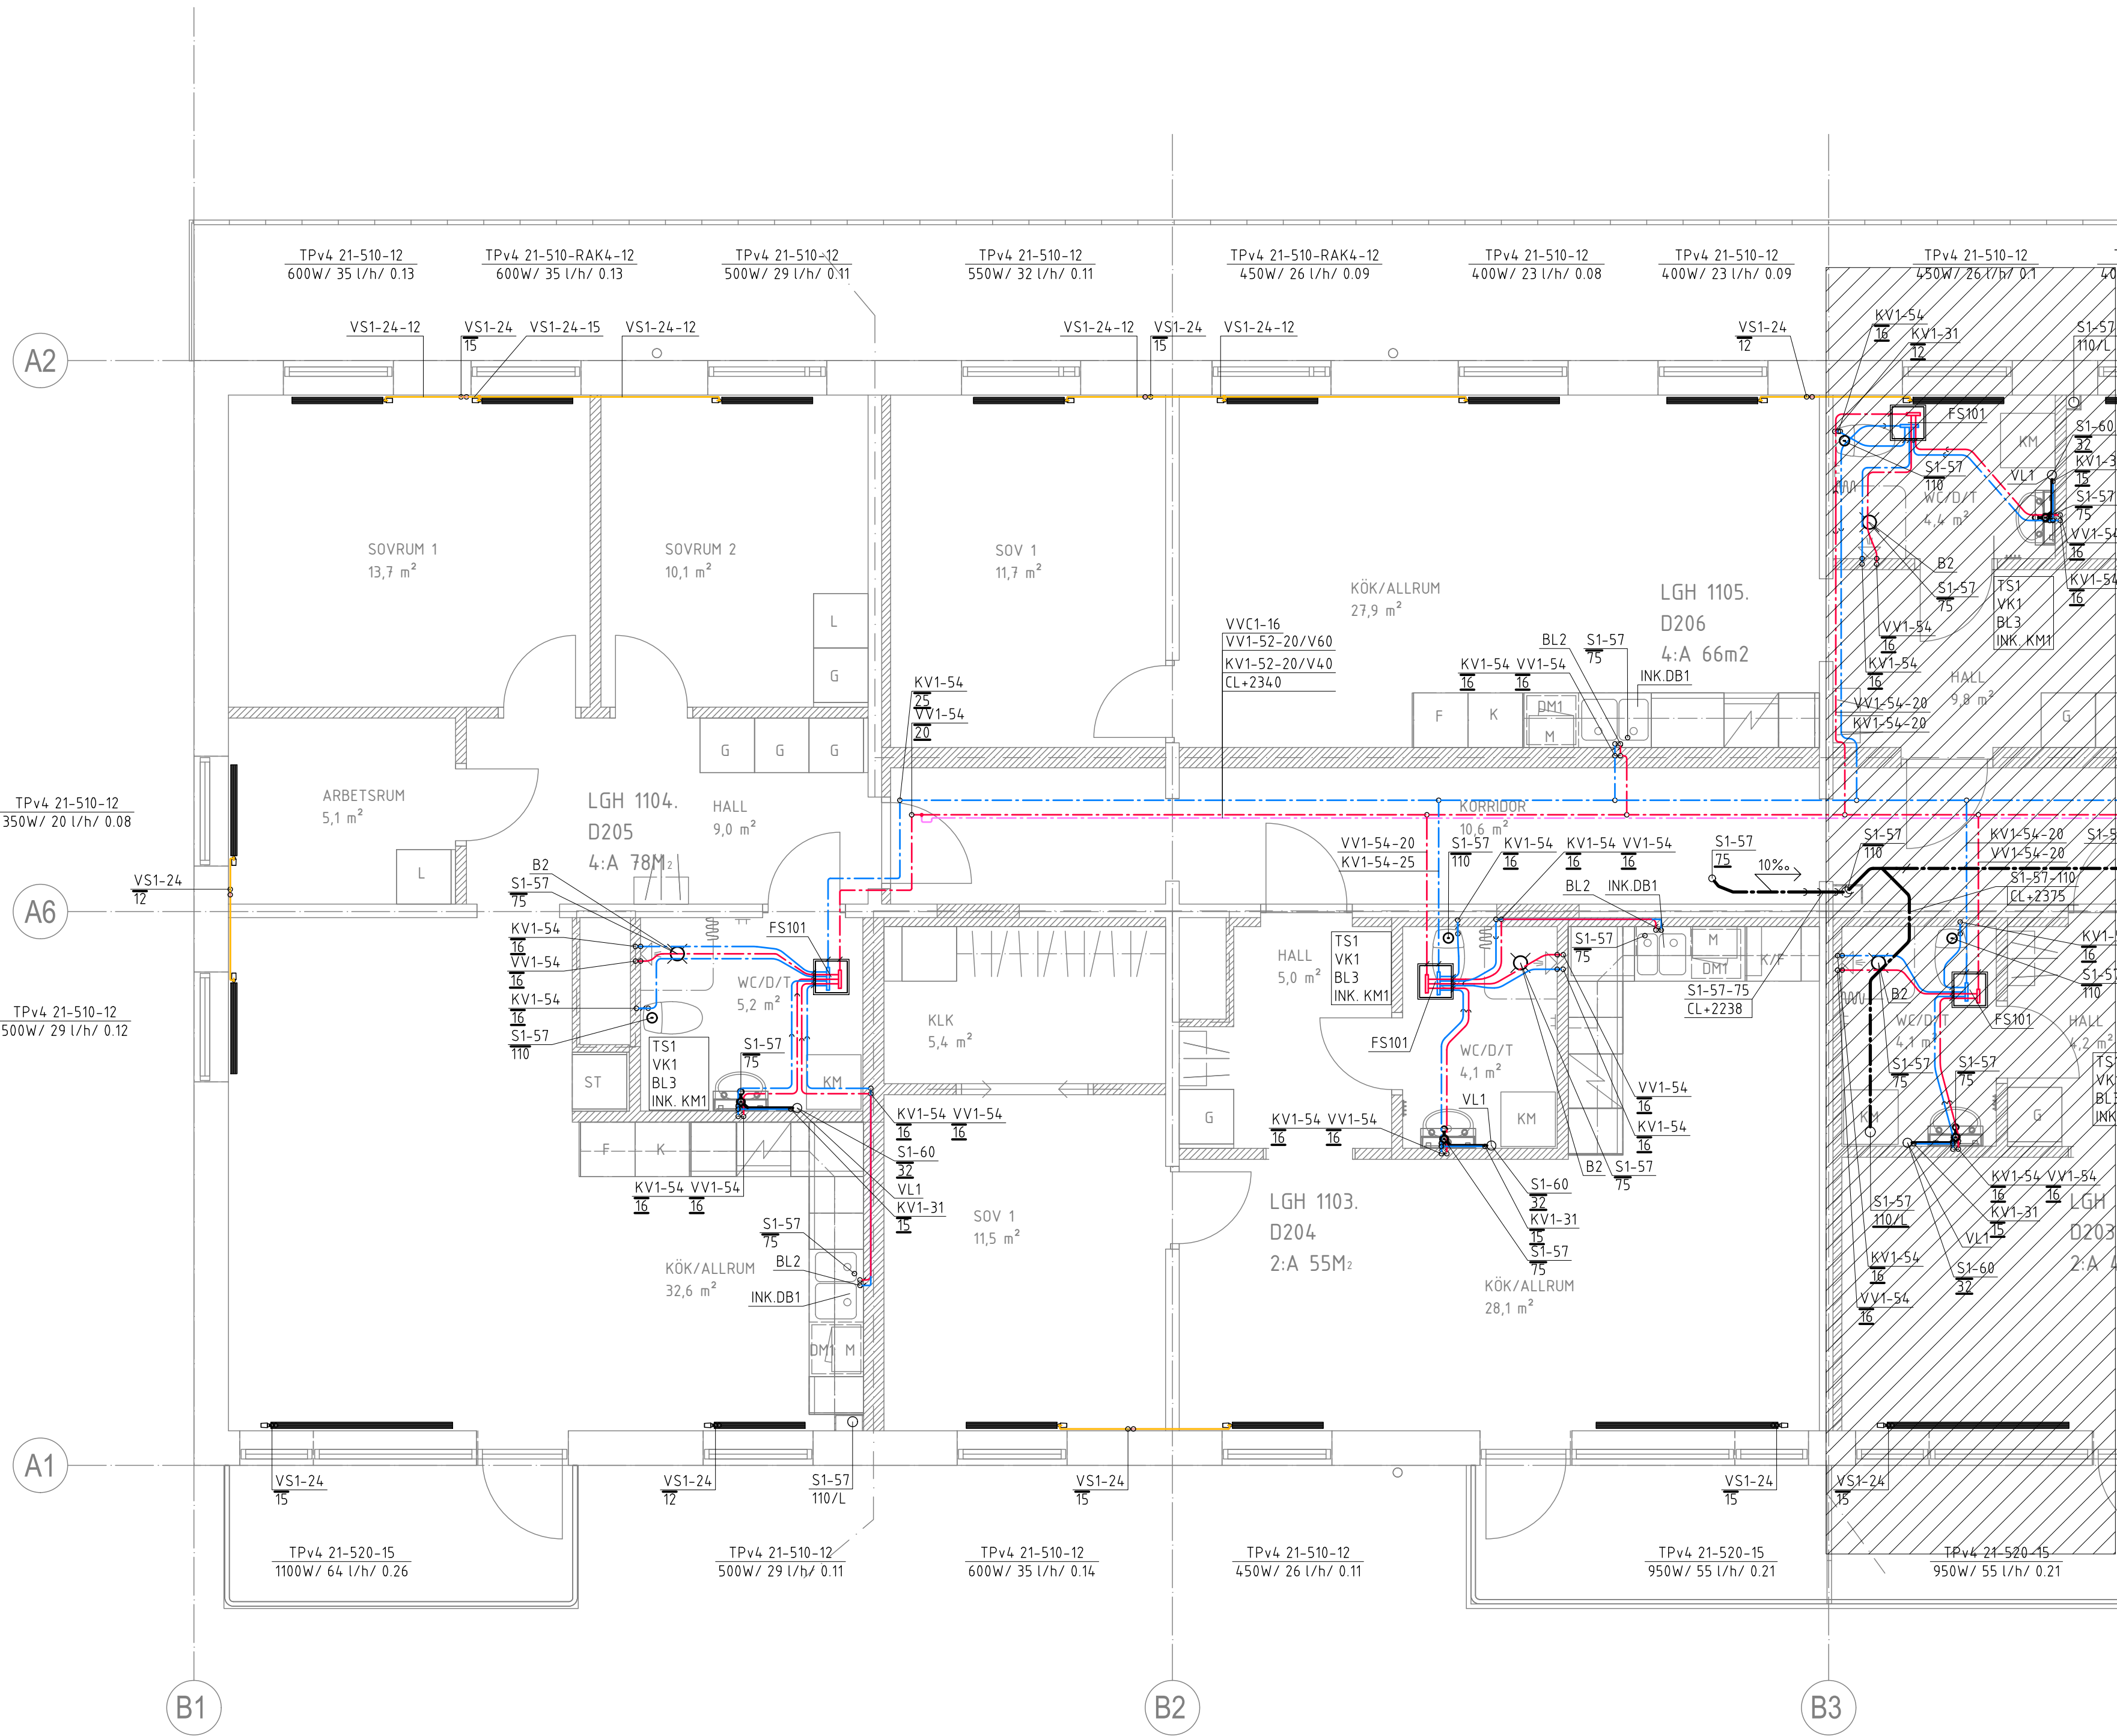

FÖRKLARINGAR

VS1-24-28/V60

SYSTEM	
KV1	TAPPKALLVATTEN
VV1	TAPPVARMVATTEN
VVC1	VARMVATTENCIRKULATION
VP1	VÄRMESYSTEM, PRIMÄRSIDA
VS1	VÄRMESYSTEM, SEK. HUVUDSYSTEM
VS2	VÄRMESYSTEM, SEK. LÜFTBEHANDLING
S1	SPILLVATTEN SANITÄRT

MATERIAL	
12	PP-MARKAVLOPPSRÖR
24	ELFÖRZINKADE STÅLRÖR
30	KOPPARRÖR EN 1050-290
31	FÖRKROMADE KOPPARRÖR
51	PEM SLANG PN16
52	LK PAL UNIVERSALRÖR, A, RAKA LÄNGDER
54	LK PE-X UNIVERSALRÖR, RIR EXTRA
	EXTRAISOLERADE TOMRÖR
57	WAVIN ASTO PLUS
60	ABS RÖR

DIMENSION
DIMENSION PÅ PAL, PEX, KOPPARRÖR OCH
ELFÖRZINKADE RÖR ANGES MED YTTERMÅTT I Dy I mm.

TERMISK ISOLERING
V40 VÄRMEISOLERING 40 MM (PAROC RÖRSKÅL).
V60 VÄRMEISOLERING 60 MM (PAROC RÖRSKÅL).

VVC SAMISOLERAS TILLSAMMANS MED VV.

LÜFTLEDNINGAR FÖR SPILLVATTNET I KALLVINDEN ISOLERAS
MED VÄRMEISOLERING 50 MM NÄTMATTA AV MINERALULL (VS0).

YTBEKLÄDNAD
SYNLIGA ISOLERADE LEDNINGAR YTBEKLÄDES TYP
MÖNSTERPRÄGLAD ALUMINIUMPLÅT ELLER LIKVÄRDIGT.

TAPPVATTEN
SYNLIG LEDNINGSDRAGNING I IRC, WC, STÅD OCH KÖK UTFÖRES
OISOLERAT OCH I FÖRKROMAT UTFÖRANDE.

TAPPVATTENRÖR DRAGNA FRÅN FS101 KLAMRAS MOT
BJÄLKLAG TILL TAPPSTALL.

VID ÖVERGÅNG FRÅN STÅENDE TILL LIGGANDE AVLOPPSSTAM
SKA ÖVERGÅNGEN UTFÖRAS MED 2x45° BÖJAR.

SAMTLIGA ÖPPNA RÖRANDAR TÄCKS MED LOCK.

HÖJDER PÅ VÄRME OCH TAPPVATTEN ANGES MED +HÖJD
CENTRUM RÖR.

HÖJDER PÅ SPILLVATTENLEDNINGAR ANGES MED
MED CL ÖFG.

ANSLUTNINGSLIEDNINGAR DIM			
SAKVARA	KV DIM	VV DIM	S DIM
TVÄTTSTALL	12	12	75
TOALETSTOL	12	-	110
UTSLÄGSBACK	15	15	-
DISKLÄDSBL.	15	15	75
DUSCHBL.	15	15	-
GÖLYBRUNN.	-	-	75

FÖRFRÅGNINGSUNDERLAG		STATUS
BYGGHANDLING		HANDLING
DATUM	ÄNDRING/PM	ÄNDRING
2025-02-26		PROJEKT
CENTRUMHUSET HUS D KRÅKAN 1, ROBERTSFORS		ANSVARIG PART
AFRY-Infrastructure AB Storgatan 103 921 32 Lycksele Tel: 010-505 00 00		AFRY
Simon Rudin	KONTAKTPERSON	Alexander Östlund
Simon Abrahamsson	GÖRKAND AV	D0182343 (210550)
PLANRITNING		RITNINGSKATEGORI
OMBYGGNAD BIBLIOTEK OCH LÄGENHETER		INNEHÅLL
PLAN 1 TR - PLAN 20 - DEL 1		FORMAT
VS - INSTALLATIONER		SKALA
V-50-1-D201		1:50
		NUMBER
		BET