


..\\A\\A1 - Modeller\\Export DWG\\A-40-P-D300.dwg - V50-stamp.dwg C:\\Users\\ind534\\OneDrive - AFRY Desktop\\Bilder\\Centrumhuset Robban\\DWG\\A-40-P-D300-Centrumhuset Inredning - Bygglösning - A-40-P-D300.dwg

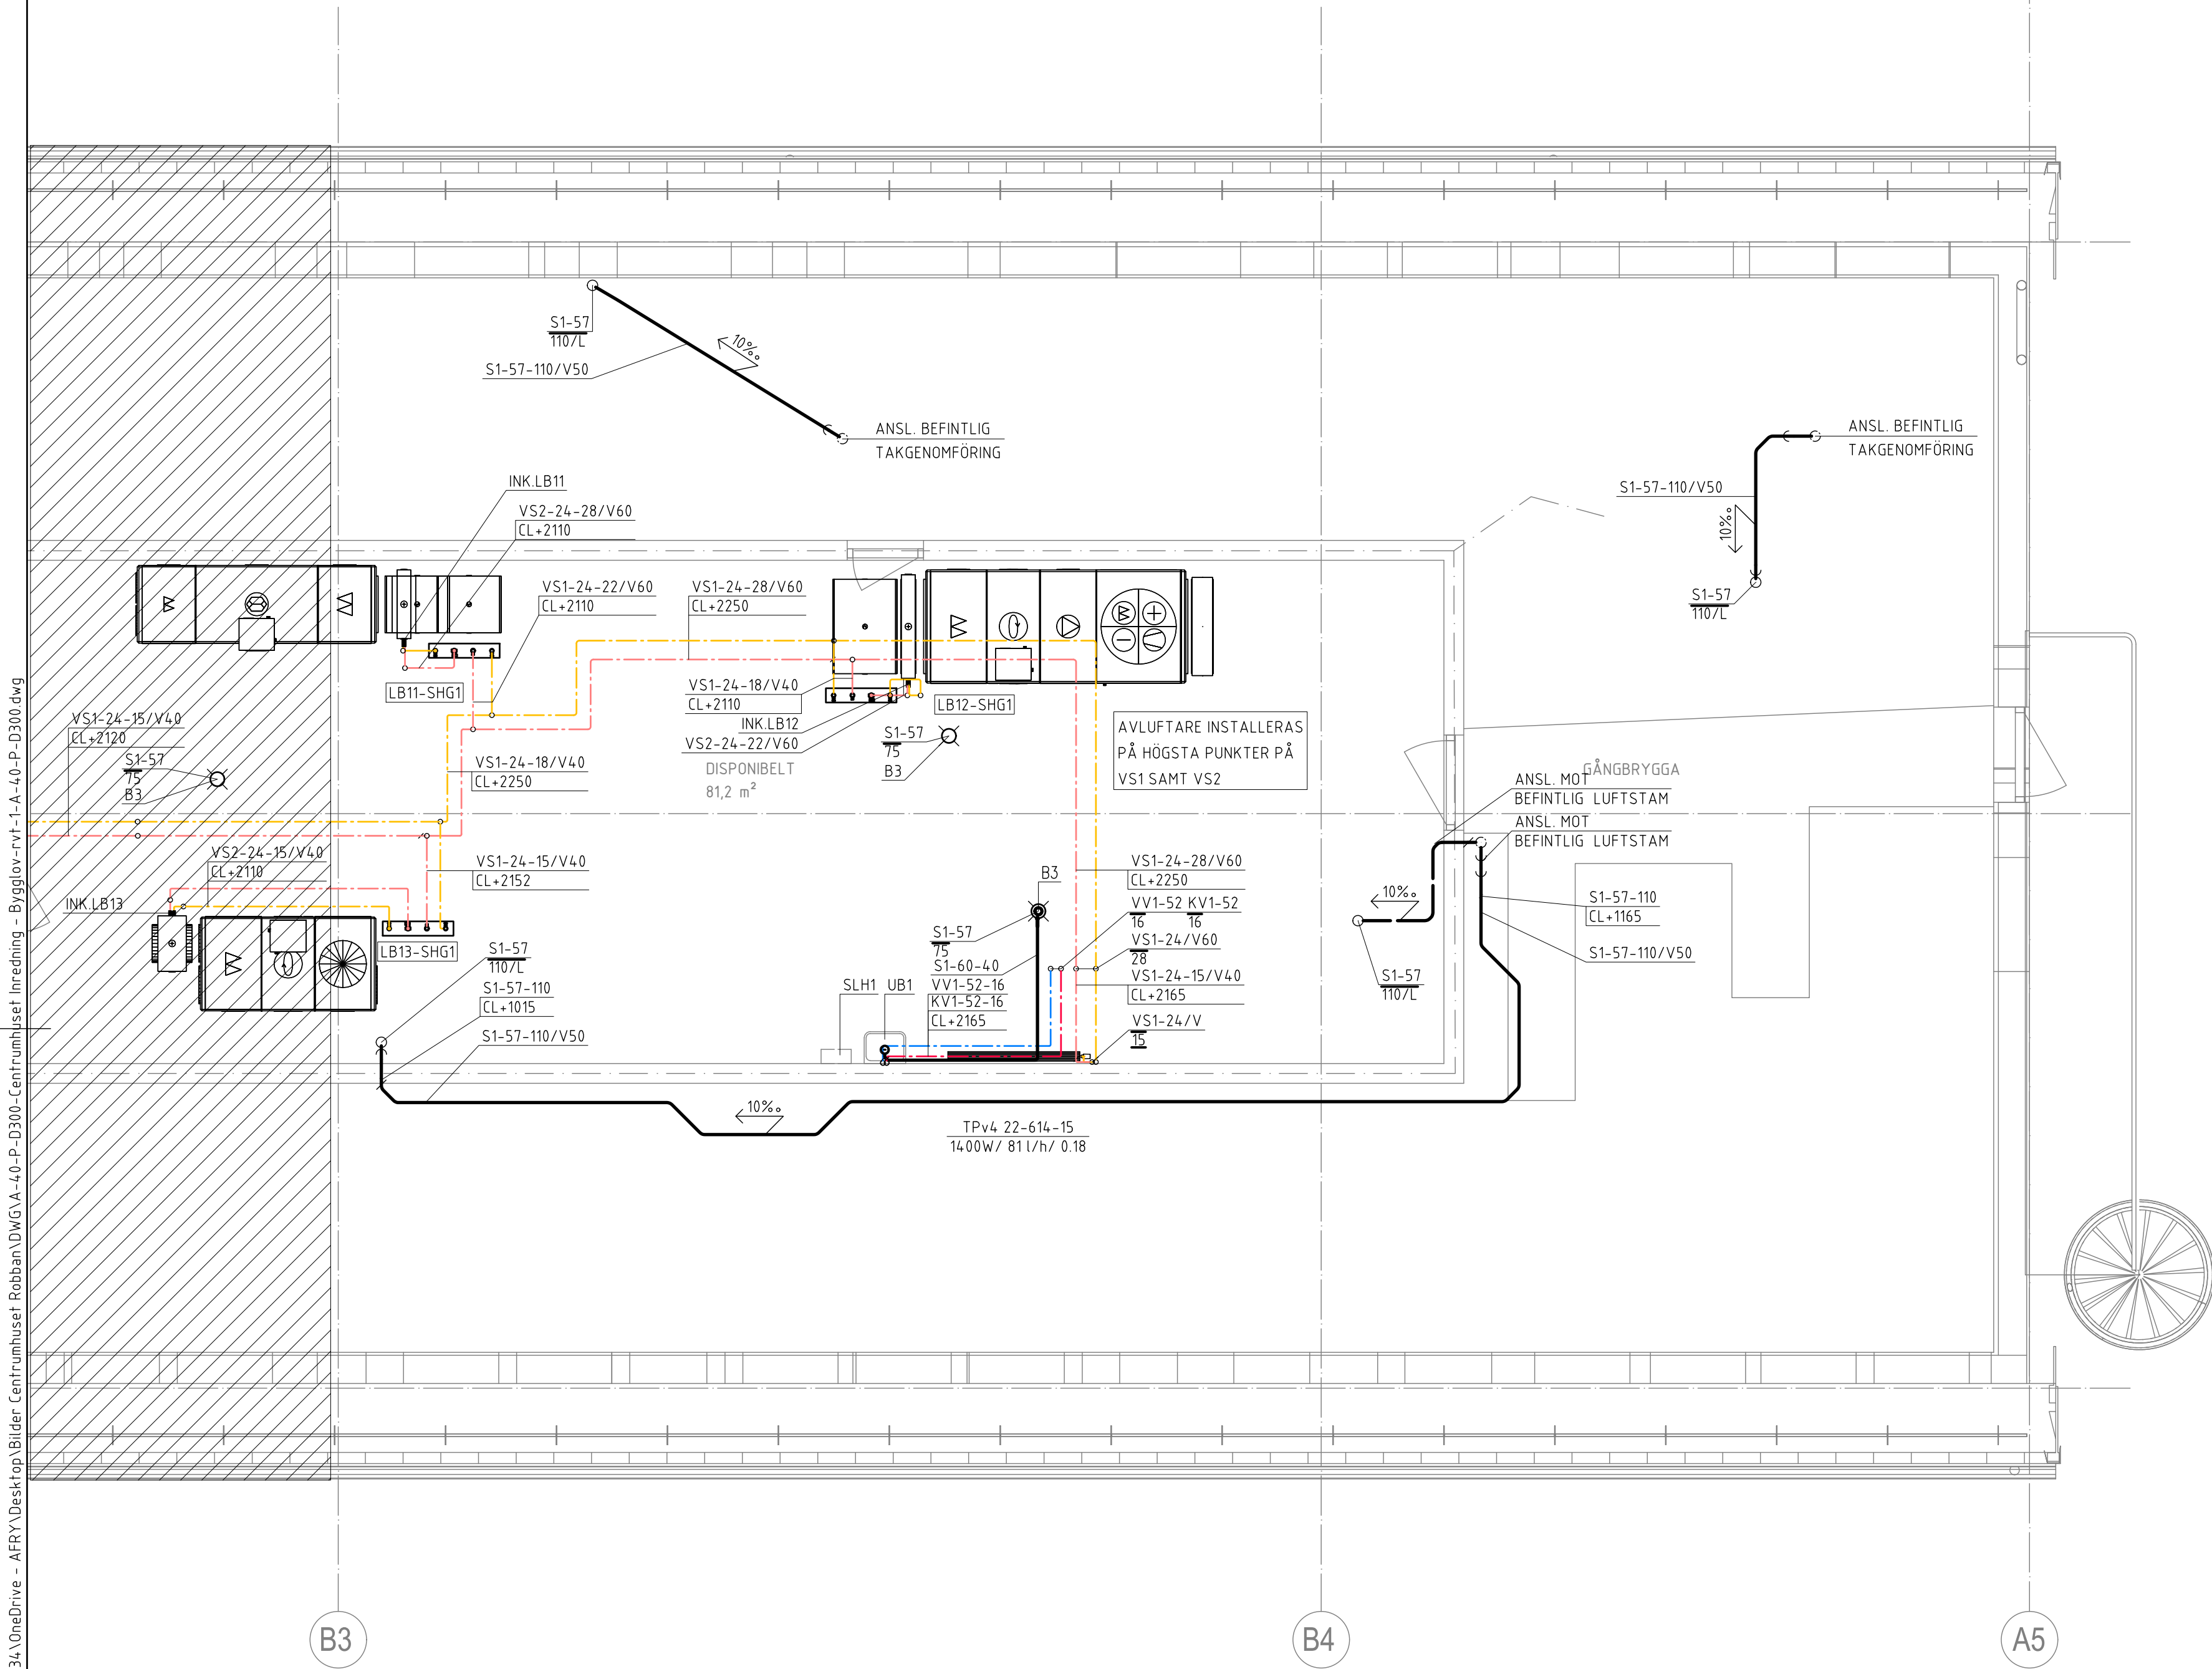

LAGER: SB11

FÖRKLARINGAR

VS1-24-28/V60

SYSTEM	
KV1	TAPPKALLVATTEN
VV1	TAPPVARMVATTEN
VVC1	VARMVATTENCIRKULATION
VP1	VÄRMESYSTEM, PRIMÄRSIDA
VS1	VÄRMESYSTEM, SEK. HUVUDSYSTEM
VS2	VÄRMESYSTEM, SEK. LÜFTBEHANDLING
S1	SPILLVATTEN SANITÄRT

MATERIAL	
12	PP-MARKAVLOPPSRÖR
24	ELFÖRZINKADE STÅLRÖR
30	KOPPARRÖR EN 1050-290
31	FÖRKROMADE KOPPARRÖR
51	PEM SLANG PN16
52	LK PAL UNIVERSALRÖR, A, RAKA LÄNGDER
54	LK PE-X UNIVERSALRÖR, RIR EXTRA EXTRAISOLERADE TOMRÖR
57	WAVIN ASTO PLUS
60	ABS RÖR

DIMENSION
DIMENSION PÅ PAL, PEX, KOPPARRÖR OCH
ELFÖRZINKADE RÖR ANGES MED YTTERMÅTT I Dy I mm.

TERMISK ISOLERING
V40 VÄRMEISOLERING 40 MM (PAROC RÖRSKÅL)
V60 VÄRMEISOLERING 60 MM (PAROC RÖRSKÅL).

VVC SAMISOLERAS TILLSAMMANS MED VV.

LÜFTLEDNINGAR FÖR SPILLVATTNET I KALLVINDEN ISOLERAS
MED VÄRMEISOLERING 50 MM NÄTMATTA AV MINERALULL (V50).

YTBEKLÄDNAD
SYNLIGA ISOLERADE LEDNINGAR YTBEKLÄDES TYP
MÖNSTERPRÄGLAD ALUMINIUMPLÅT ELLER LIKVÄRDIGT.

TAPPVATTEN
SYNLIG LEDNINGSDRAGNING I RWC, WC, STÅD OCH KÖK UTFÖRES
OISOLERAT OCH I FÖRKROMAT UTFÖRANDE.

TAPPVATTENRÖR DRAGNA FRÅN FS101 KLAMRAS MOT
BJÄLKLAG TILL TAPPSTALL.

VID ÖVERGÅNG FRÅN STÅENDE TILL LIGGANDE AVLOPPSSTAM
SKA ÖVERGÅNGEN UTFÖRAS MED 2x45° BÖJAR.

SAMTLIGA ÖPPNA RÖRANDAR TÄCKS MED LOCK.

HÖJDER PÅ VÄRME OCH TAPPVATTEN ANGES MED +HÖJD
CENTRUM RÖR.

HÖJDER PÅ SPILLVATTENLEDNINGAR ANGES MED
MED CL ÖFG.

ANSLUTNINGSLIDNINGAR DIM				
SAKVÄRA	KV DIM	VV DIM	S DIM	
TVÄTTSTALL	12	12	75	
TOALETSTÖL	12	-	110	
UTSLÄGSBACK	15	15	-	
DISKLÄDSBL.	15	15	75	
DUSCHBL.	15	15	-	
GÖLYBRUNN.	-	-	75	

GRANSKNINGSHANDLING 2025-02-26

FÖRFRÅGNINGSUNDERLAG		STATUS
BYGGHANDLING		HANDLING
DATUM 2025-02-26	ÄNDRING/PM	ÄNDRING
CENTRUMHUSET HUS D KRÅKAN 1, ROBERTSFORS		PROJEKT
AFRY-Infrastructure AB Storgatan 103 921 32 Lycksele Tel: 010-505 00 00		ANSVÄRIG PART
Simon Rudin	Alexander Ostlund	SKAPAD AV
Simon Abrahamsson	D0182343 (210650)	UPPDRAGSNUMMER
PLANRITNING		RITNINGSKATEGORI
OMBYGGNAD BIBLIOTEK OCH LÄGENHETER VINDSVÄNING - PLAN 30 - DEL 2 VS - INSTALLATIONER		INNEHÅLL A1
V-50-1-D302		FORMAT A1
		SKALA 1:50
		REVISJON 1