


X:\4-TransfEr\Entitet\TM\Uppdrag 2021\210550 Kråkan 1 - Centrumhuset\VS1 - Modeller\1 - Modell\V50-stamp.dwg

LAGER: SB11

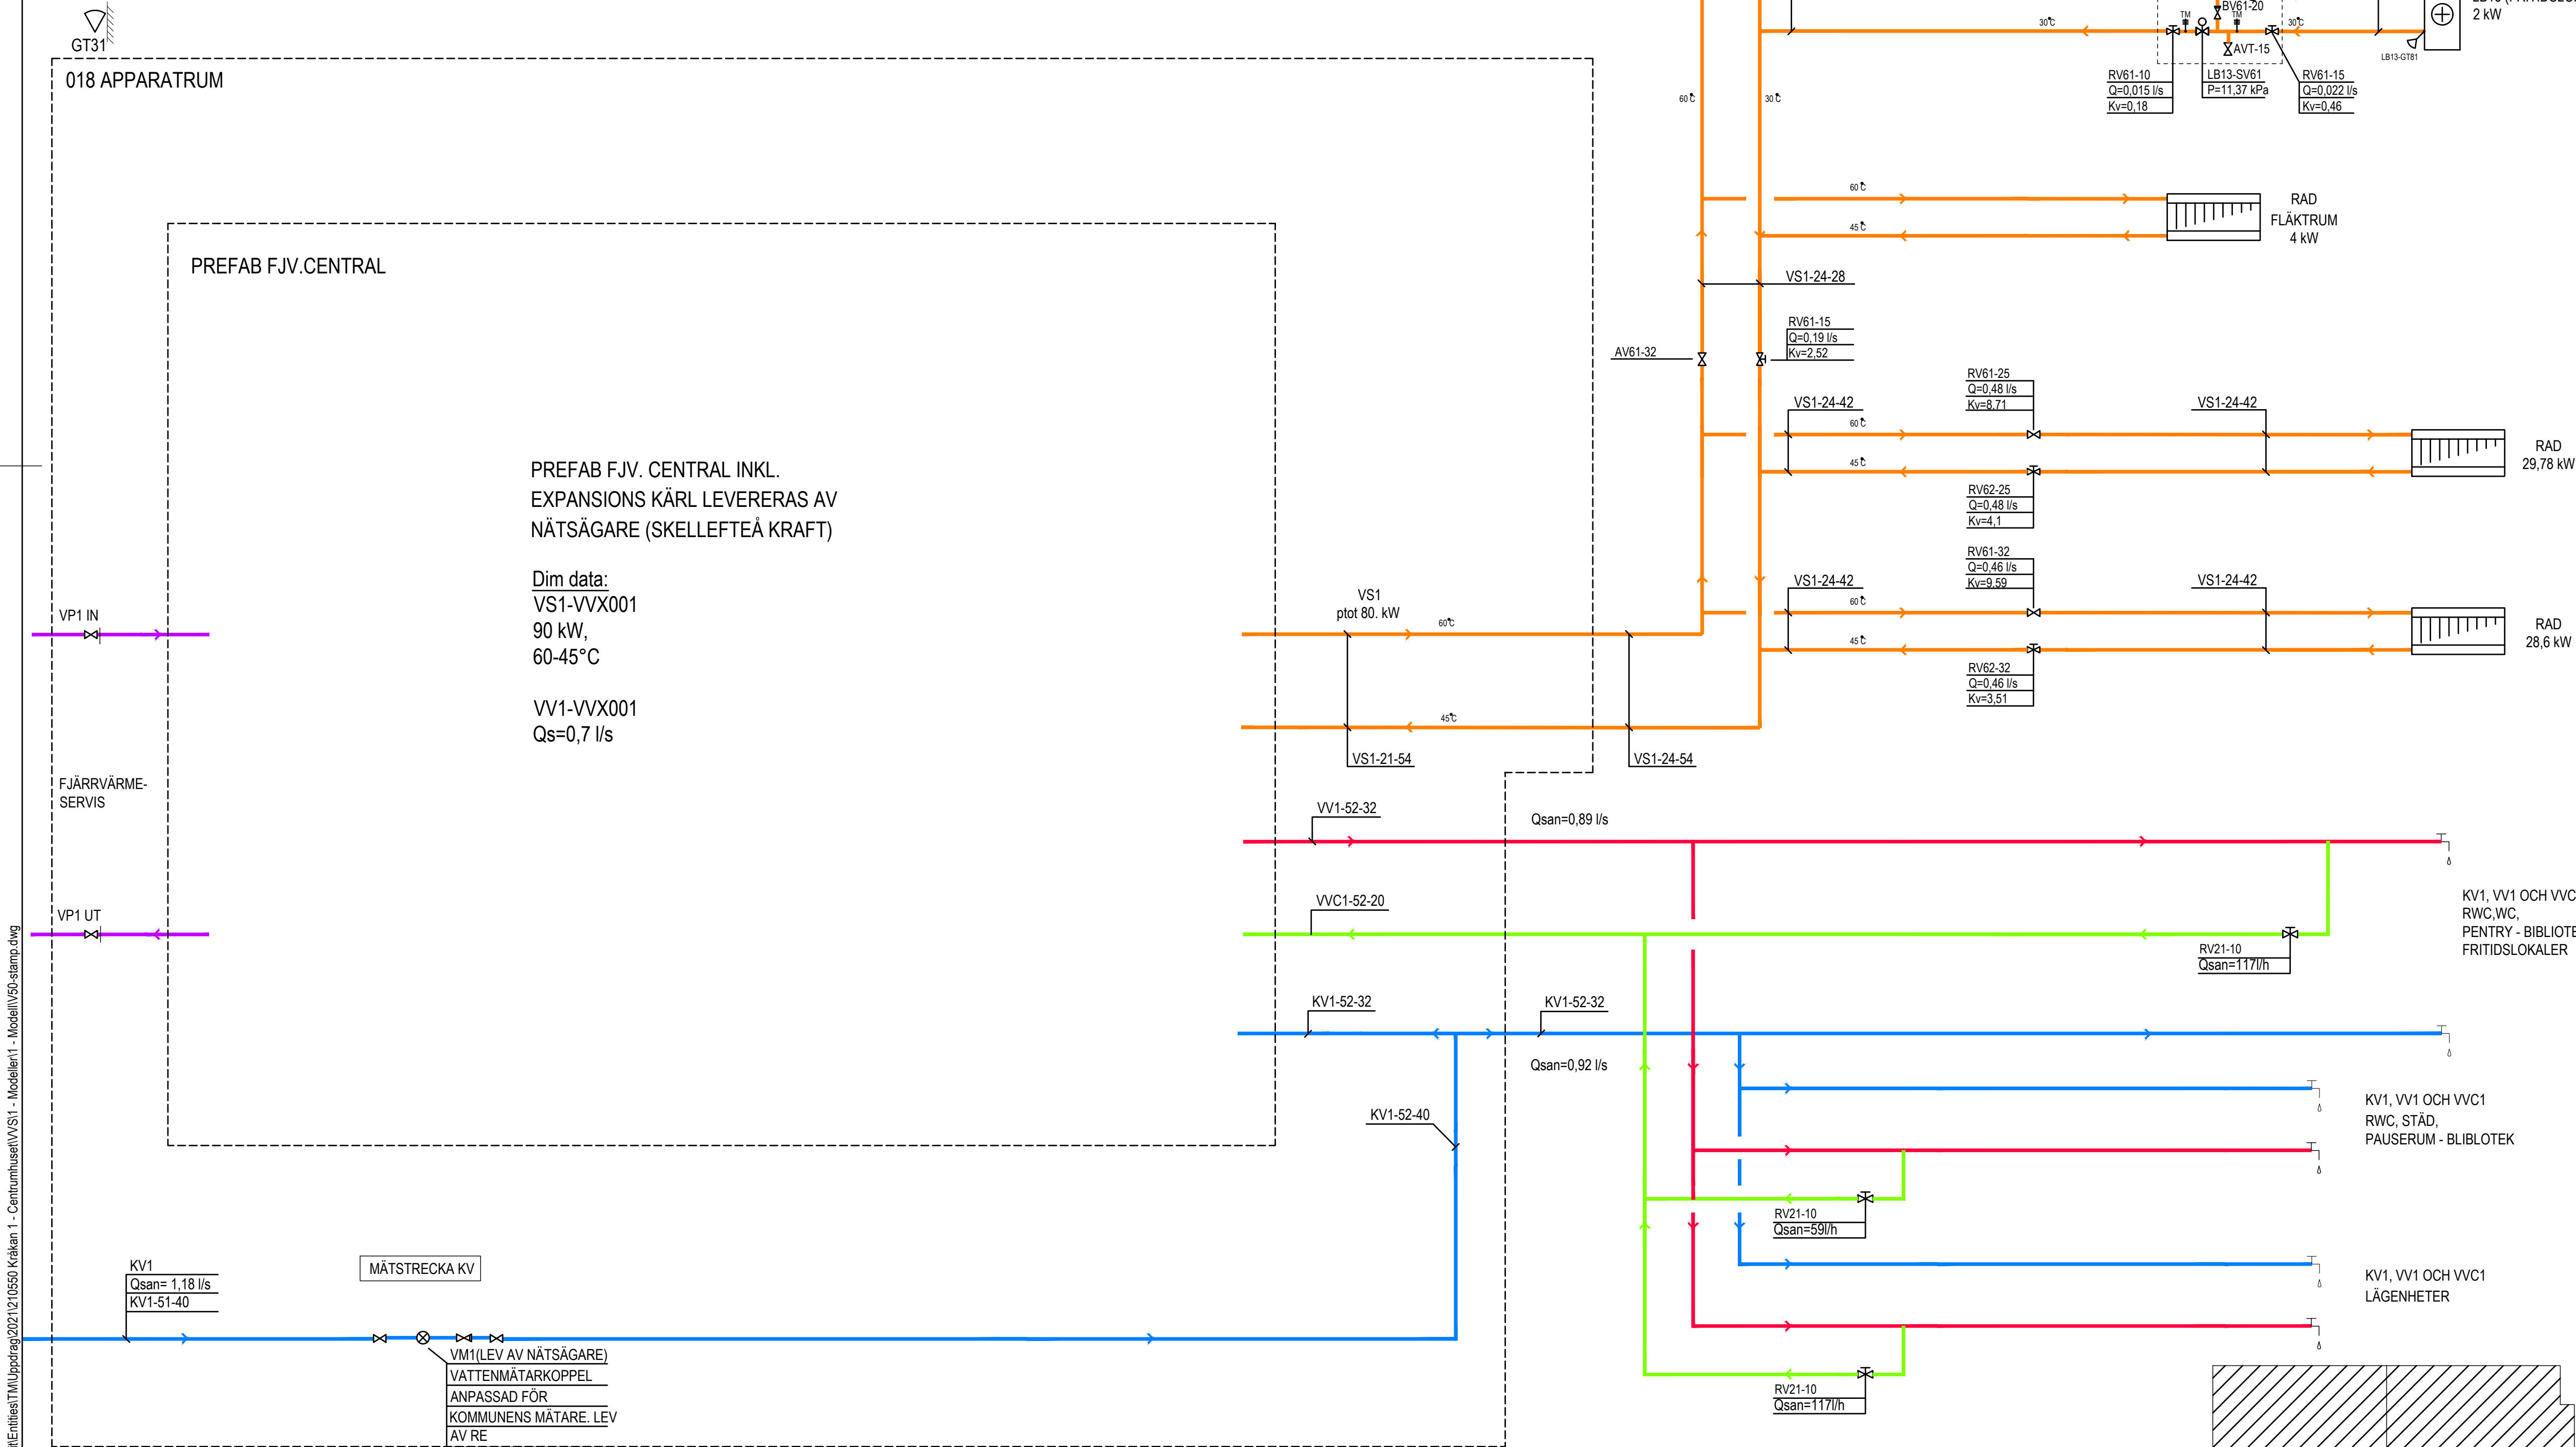

FÖRKLARINGAR

VS1-24-28/V60

SYSTEM	
KV1	TAPPKALLVATTEN
VV1	TAPPVARMVATTEN
VVC1	VARMVATTENCIRKULATION
VP1	VÄRMESYSTEM, PRIMÄRSIDA
VS1	VÄRMESYSTEM, SEK. HUVUDSYSTEM
VS2	VÄRMESYSTEM, SEK. LÜFTBEHANDLING
S1	SPILLVATTEN SANITÄRT

MATERIAL	
12	PP-MARKAVLOPPSRÖR
24	ELFÖRZINKADE STÅLRÖR
30	KOPPARRÖR EN 1050-290
31	FÖRKROMADE KOPPARRÖR
51	PEM SLANG PN16
52	LK PAL UNIVERSALRÖR, A, RAKA LÄNGDER
54	LK PE-X UNIVERSALRÖR, RIR EXTRA EXTRAISOLERADE TOMRÖR
57	WAVIN ASTO PLUS
60	ABS RÖR

DIMENSION
DIMENSION PÅ PAL, PEX, KOPPARRÖR OCH ELFÖRZINKADE RÖR ANGES MED YTERMÅTT I Dy I mm.

TERMISK ISOLERING
V40 VÄRMEISOLERING 40 MM (PAROC RÖRSKÅL).
V60 VÄRMEISOLERING 60 MM (PAROC RÖRSKÅL).

VVC SAMISOLERAS TILLSAMMANS MED VV.

LÜFTLEDNINGAR FÖR SPILLVATTNET I KÄLLVINDEN ISOLERAS MED VÄRMEISOLERING 50 MM NÄTMATTA AV MINERALULL (V50).

YTBEKLÄDNAD
SYNLIGA ISOLERADE LEDNINGAR YTBEKLÄDES TYP MÖNSTERPRÄGLAD ALUMINIUMPLÅT ELLER LIKVÄRDIGT.

TAPPVATTEN
SYNLIG LEDNINGSDRAGNING I RWC, WC, STÅD OCH KÖK UTFÖRES OISOLERAT OCH I FÖRKROMAT UTFÖRANDE.

TAPPVATTENRÖR DRAGNA FRÅN FS101 KLAMRAS MOT BJÄLKLAG TILL TAPPSTÄLL.

VID ÖVERGÅNG FRÅN STÅENDE TILL LIGGANDE AVLOPPSSTAM SKA ÖVERGÅNGEN UTFÖRAS MED 2x45° BÖJAR.

SAMTLIGA ÖPPNA RÖRANDAR TÄCKS MED LOCK.

HÖJDER PÅ VÄRME OCH TAPPVATTEN ANGES MED +HÖJD CENTRUM RÖR.

HÖJDER PÅ SPILLVATTENLEDNINGAR ANGES MED MED CL ÖFG.

ANSLUTNINGSLIEDNINGAR DIM				
SAKVARA	KV DIM	VV DIM	S DIM	
TVÄTTSTALL	12	12	75	
TOALETSTÖL	12	-	110	
UTSLAGSBÄCK	15	15	-	
DISKLÄDSBL.	15	15	75	
DUSCHBL.	15	15	-	
GÖLYVBÄNN.	-	-	75	

FÖRFRÅGNINGSUNDERLAG		STATUS	
BYGGHANDLING		HANDLING	
DATUM 2025-02-26	ÄNDRING/PM	ÄNDRING	
CENTRUMHUSET HUS D KRÅKAN 1, ROBERTSFORS		PROJEKT	
AFRY-Infrastructure AB Storgatan 103 921 32 Lycksele Tel: 010-505 00 00		ANSVARIG PART	
Simon Rudin	KONTAKTPERSON	Alexander Östlund	SKAPAD AV
Simon Abrahamsson	GODKÄND AV	D0182343 (210550)	UPPDRAGSNUMMER
PLANRITNING		RITNINGSKATEGORI	
OMBYGGNAD BIBLIOTEK OCH LÄGENHETER		INNEHÅLL	FORMAT A1
FLOODESSCHEMA		SKALA	
VS - INSTALLATIONER		NUMMER	BET
V-50-8-D001			