

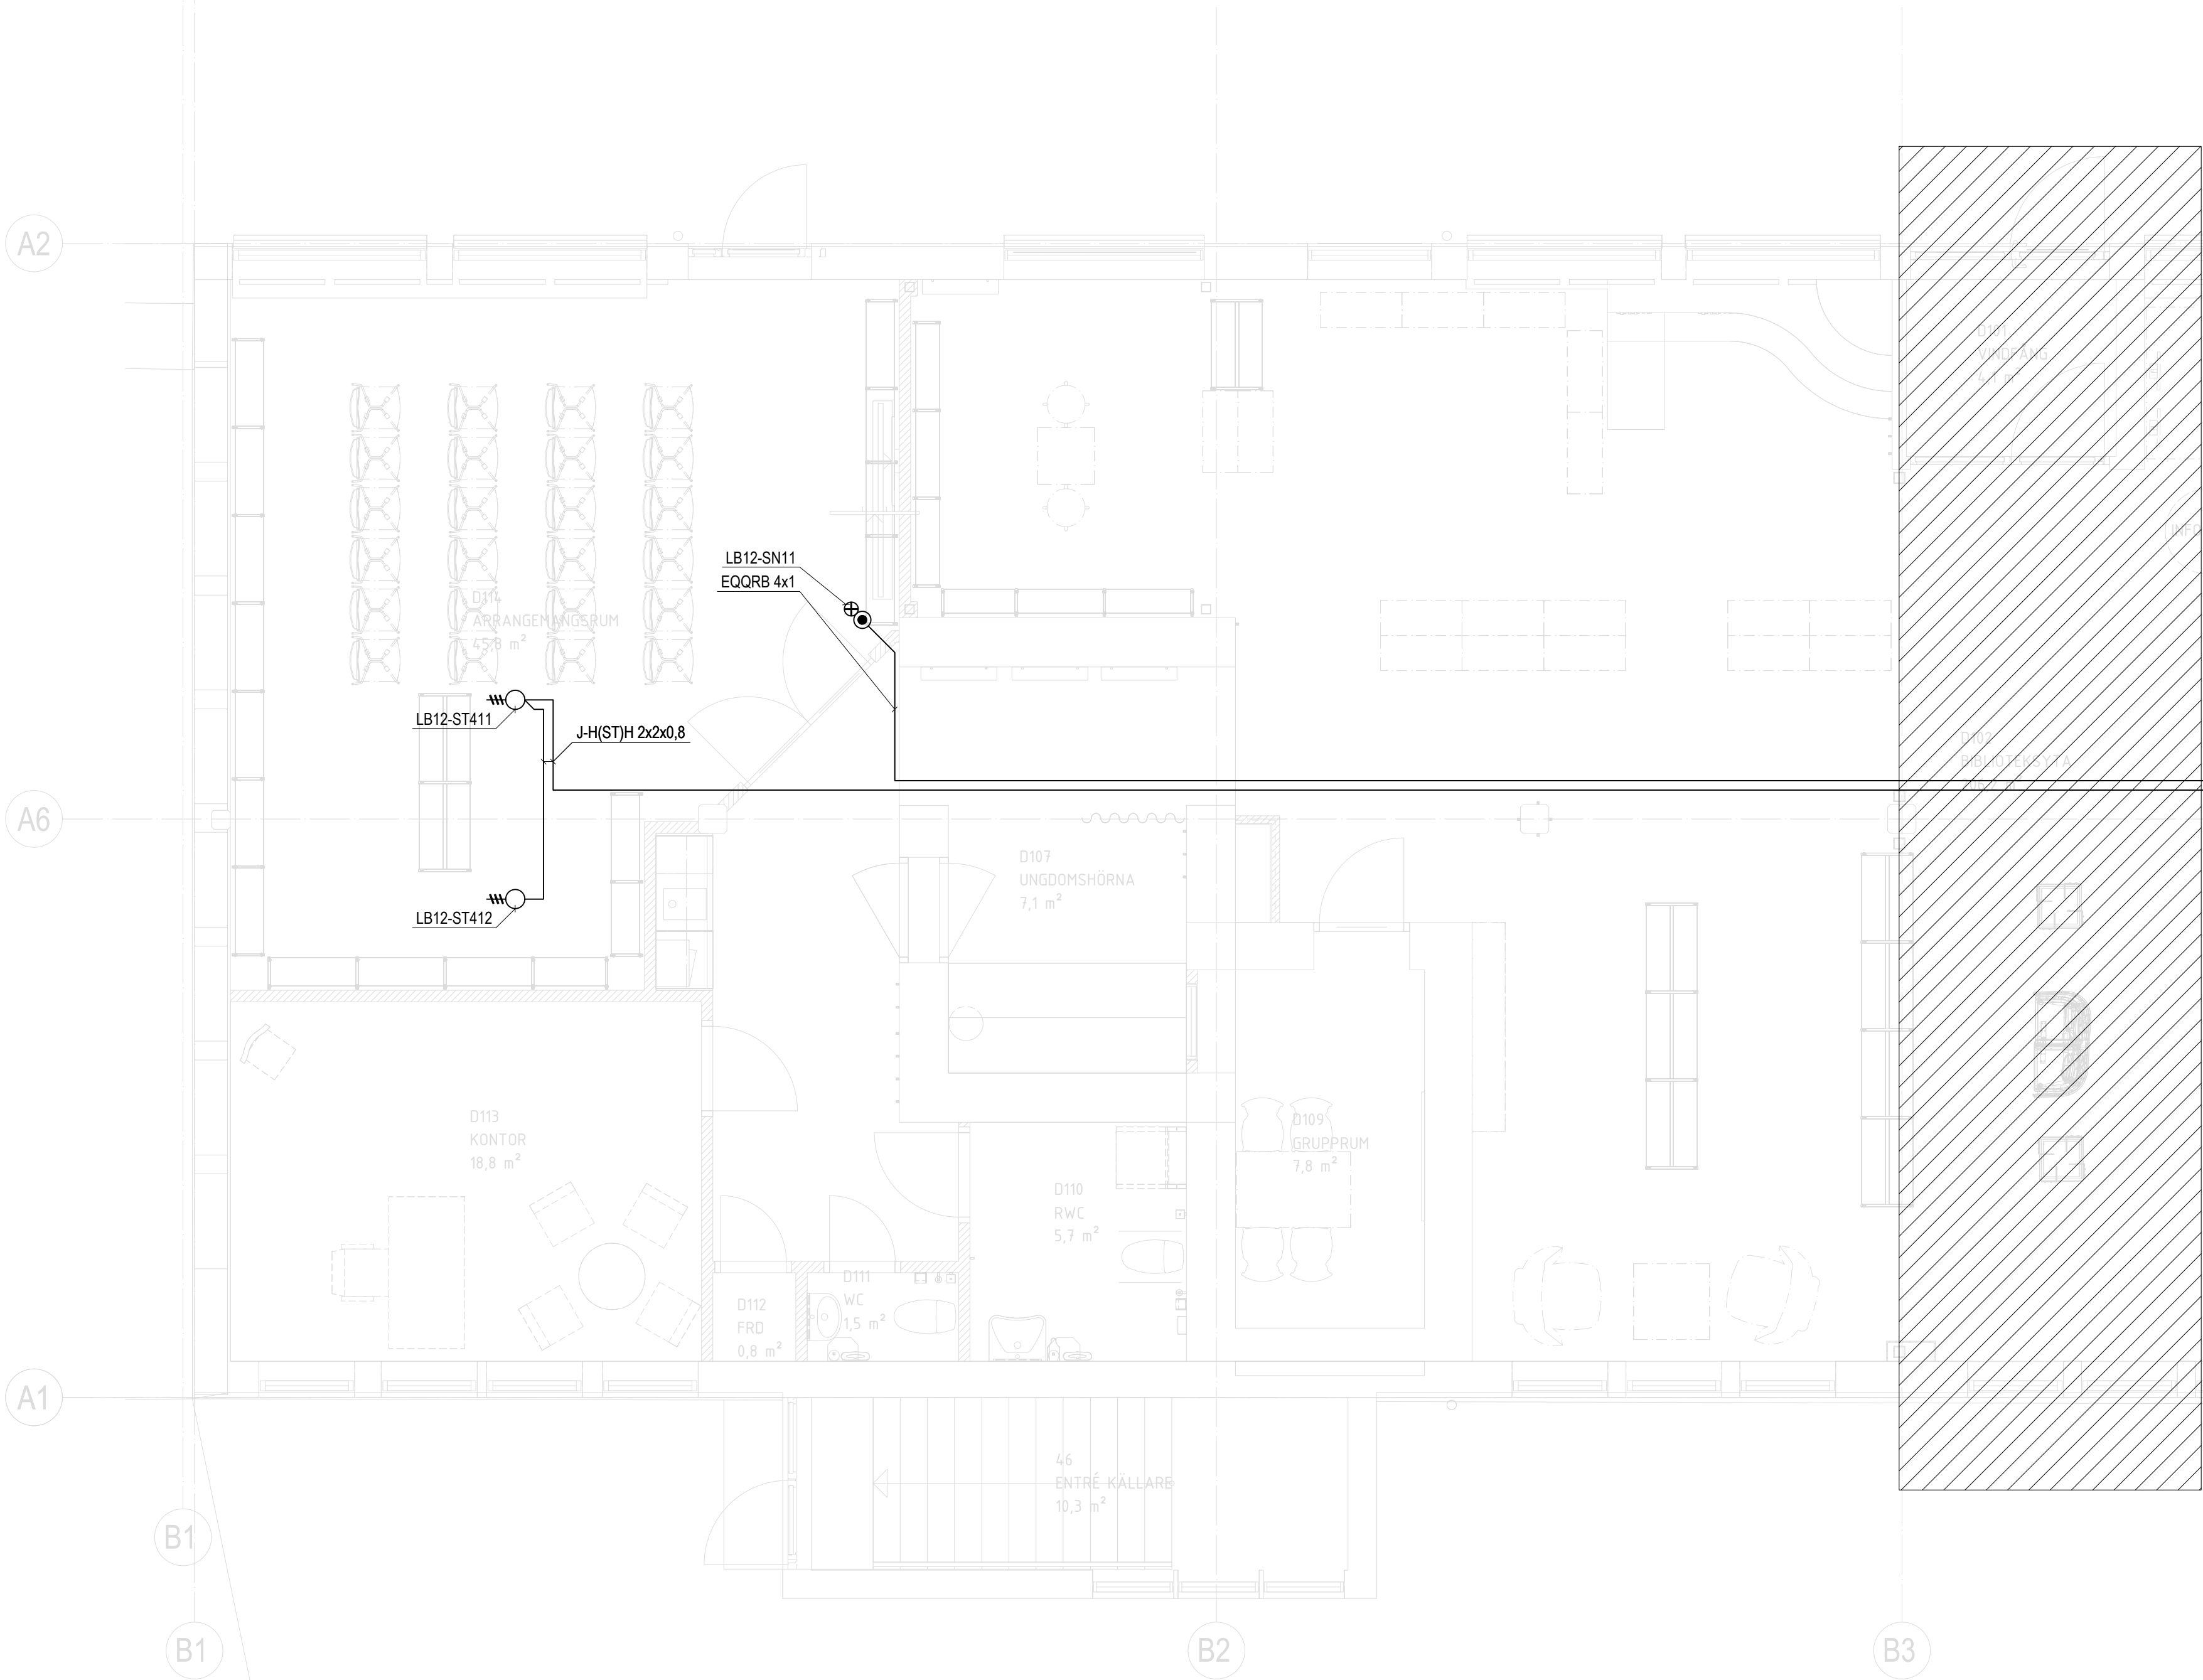


\\...\\A1 - Modeller\\Export DWG\\A-40-P-D100.dwg X:\\...\\Transit\\Entities\\TM\\Uppdrag\\2021\\210550 Kråkan 1 - Centrumhuset\\Sjyrv1 - Modeller\\Modell\\Fsyst.dwg ...\\EL1 - Modeller\\E-61-P-D100.dwg

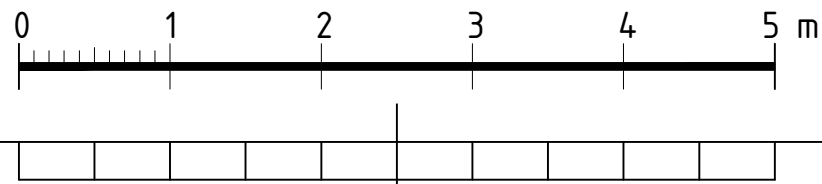

FÖRESKRIFTER
STYRKABEL 3X1,5 MÅNGTRÄDIG HALOGENFRI
ANVÄNDS DÄR ANNAT EJ ÄNGES

LEDNING MELLAN SÄKERHETSBRYTARE OCH MOTOR
SKALL VARA AV SAMMA TYP SOM MATANDE KABEL
TILL SÄKERHETSBRYTARE

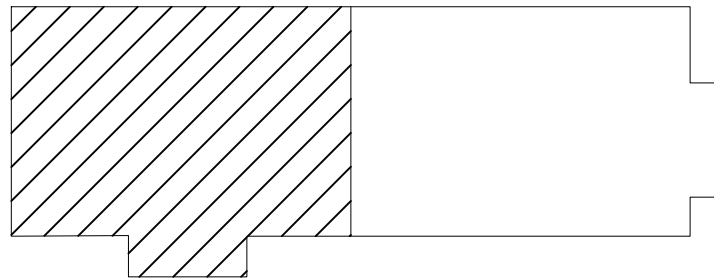

FÖRFRÅGNINGSUNDERLAG		STATUS	
BYGGHANDLING		HANDLING	
DATUM	ÄNDRING/PM	ÄNDRING	
2025-02-26		PROJEKT	
CENTRUMHUSET HUS D KRÅKAN 1, ROBERTSFORS			
ÅF-Infrastructure AB		ANSVÄRIG PART	
Storgatan 103 921 32 Lycksele Tel: 010-505 00 00		 AFRY	
KONTAKTPERSON	André Sjölander	SKAPAD AV	
Simon Rudin		UPPDRAGSNUMMER	
Simon Abrahamsson	D0182343 (210550)	RITNINGSKATEGORI	
PLANRITNING			
OMBYGGNAD BIBLIOTEK OCH LÄGENHETER		INNEHÅLL	
BOTTENPLAN - PLAN 10 - DEL 1		A1	
STYR- OCH ÖVERVAKNINGSSYSTEM		1:50	
S-81-1-D101		NUMMER	
		BET	