



..\\..\\A1 - Modeller\\Export DWG\\A-40-P-D100.dwg X:\\..\\Transit\\Entities\\TM\\Uppdrag\\2021\\210550 Kråkan 1 - Centrumhuset\\Styr\\1 - Modeller\\Modell\\Fstyr.dwg \\..\\..\\EL1 - Modeller\\E-61-P-D100.dwg

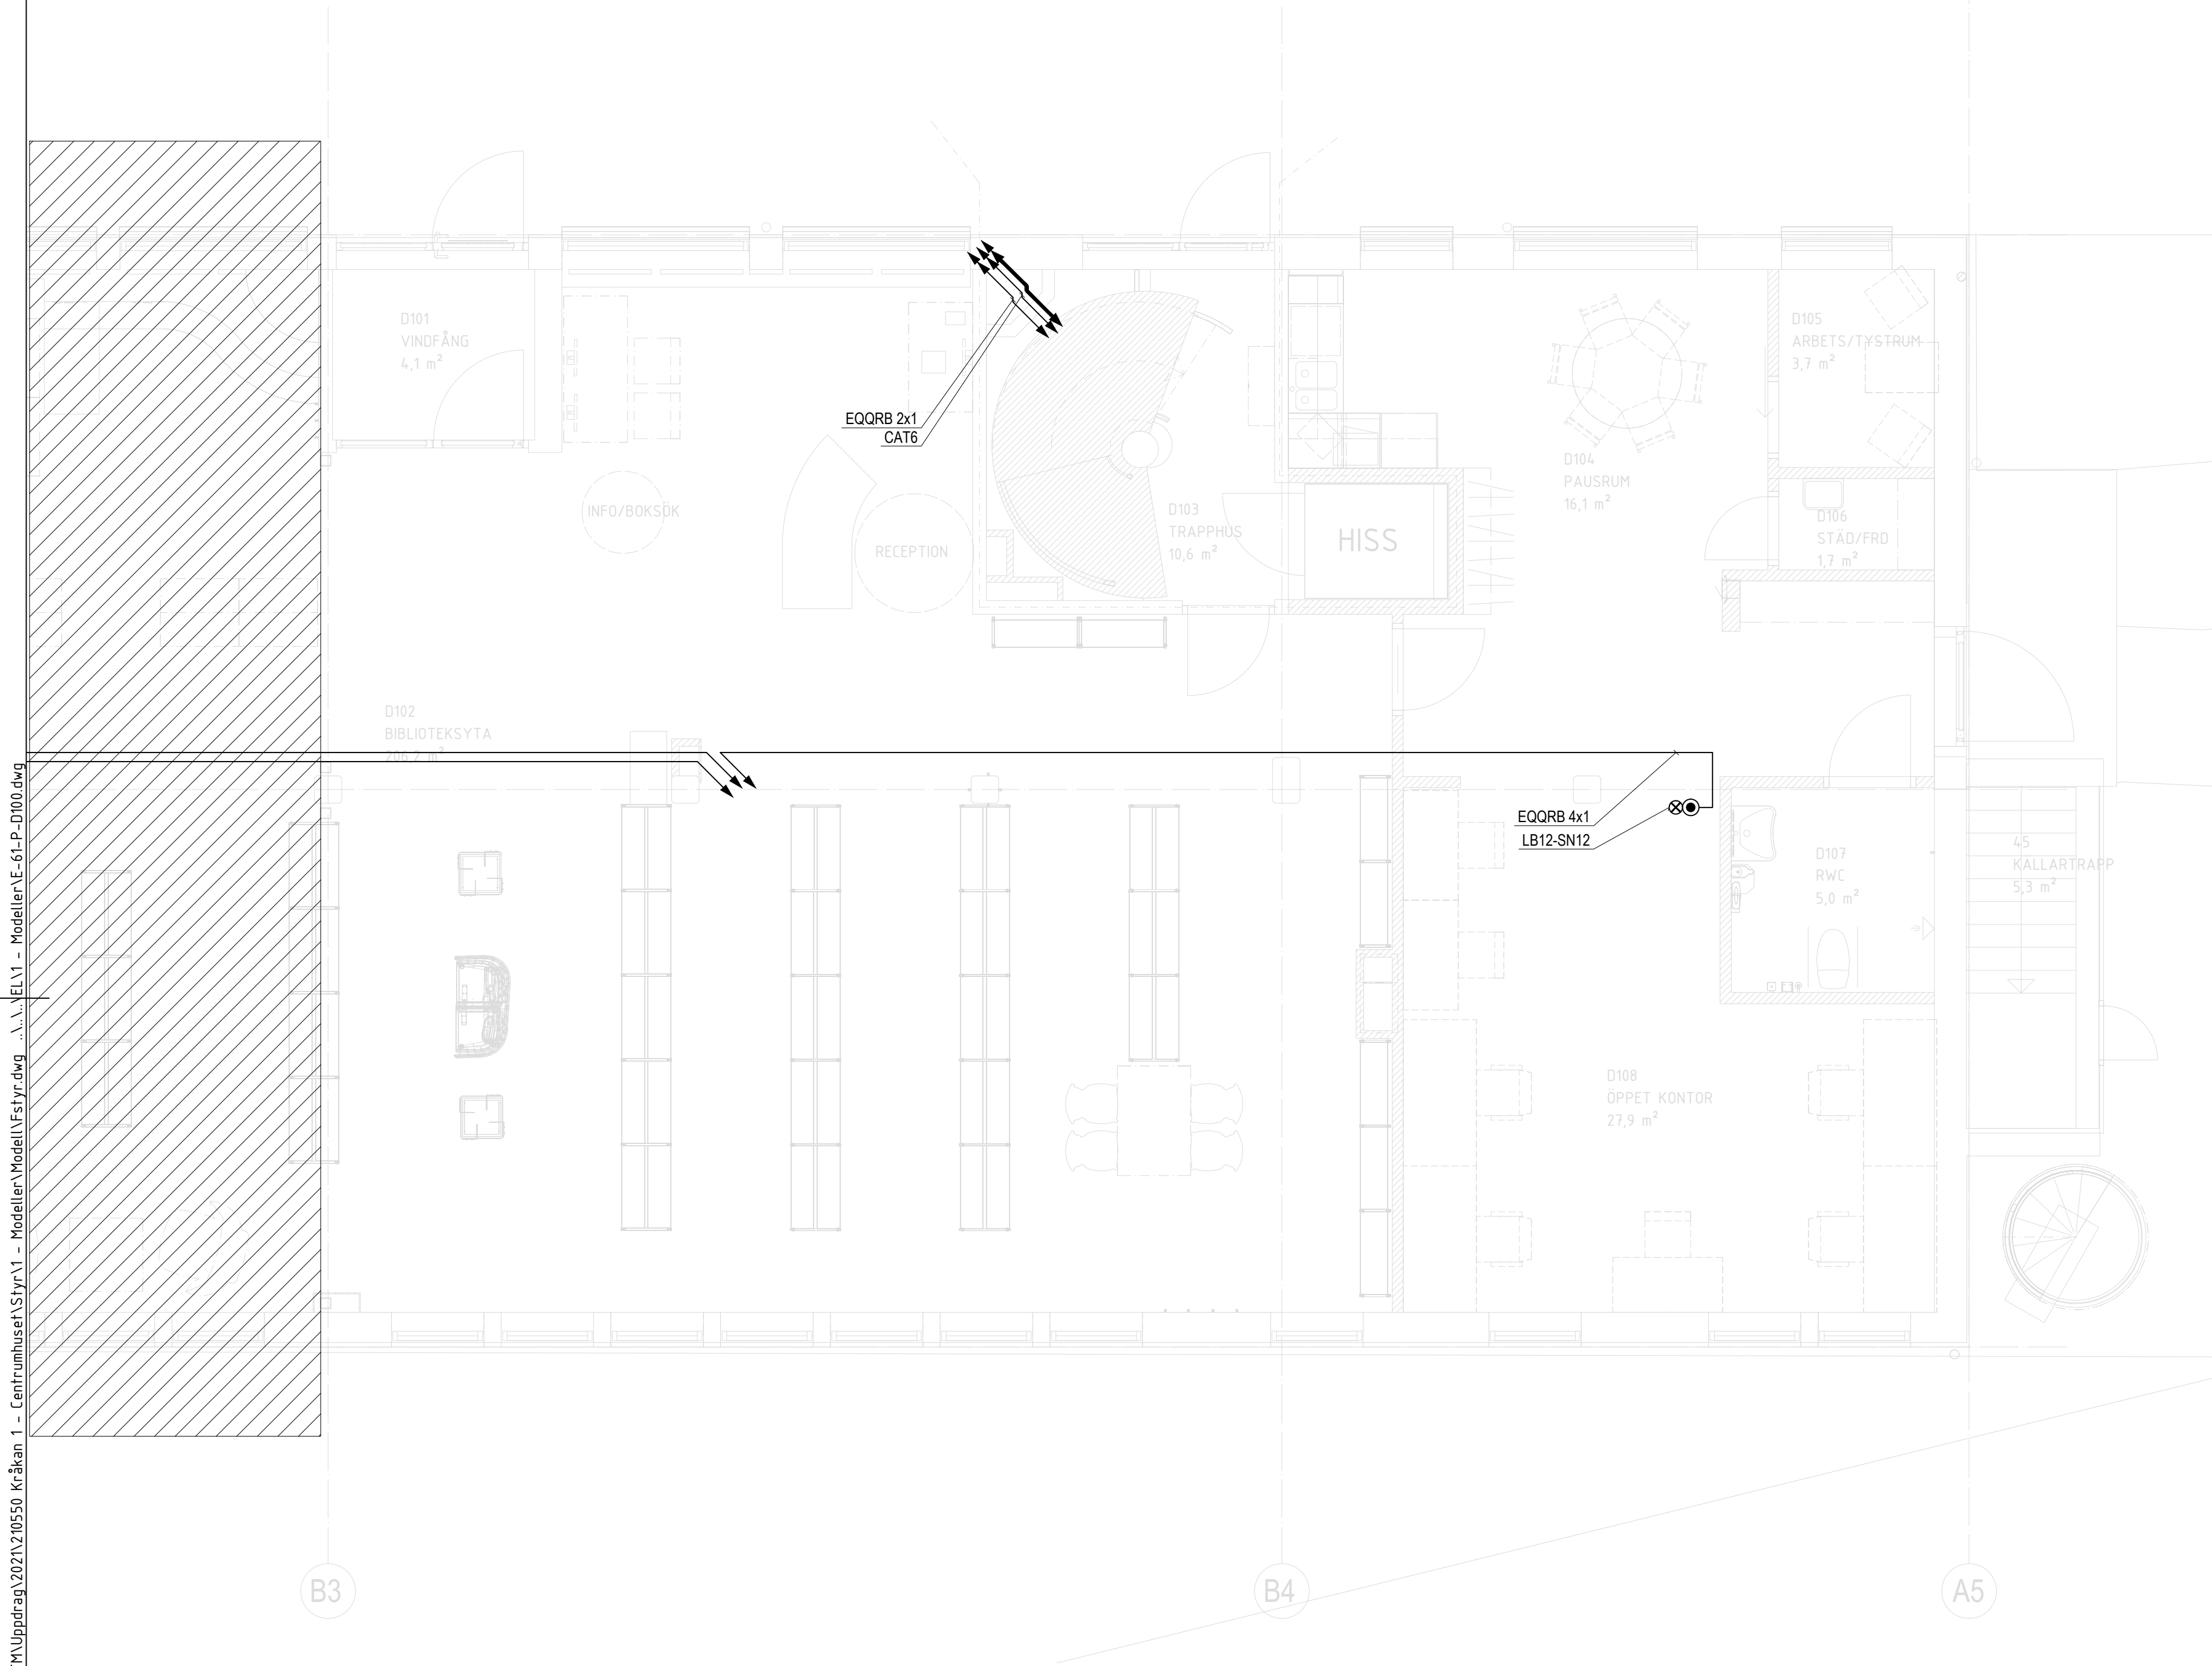

LAGER: SB11

FÖRESKRIFTER
STYRKABEL 3X1,5 MÅNGTRÄDIG HALOGENFRI
ANVÄNDS DÄR ANNAT EJ ÄNGES

LEDNING MELLAN SÄKERHETSBRYTARE OCH MOTOR
SKALL VARA AV SAMMA TYP SOM MATANDE KABEL
TILL SÄKERHETSBRYTARE

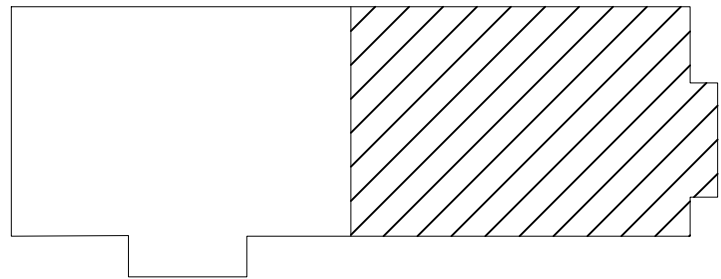

FÖRFRÅGNINGSUNDERLAG		STATUS	
BYGGHANDLING		HANDLING	
DATUM	ÄNDRING/PM	ÄNDRING	
2025-02-26		PROJEKT	
CENTRUMHUSET HUS D KRÅKAN 1, ROBERTSFORS			
ÅF-Infrastructure AB		ANSVARIG PART	
Storgatan 103 921 32 Lycksele Tel: 010-505 00 00		 AFRY	
KONTAKTPERSON	André Sjölander	SKAPAD AV	
Simon Rudin			
GODKÄND AV	D0182343 (210550)	UPPRAGSNUMMER	
Simon Abrahamsson			
PLANRITNING		RITNINGSKATEGORI	
OMBYGGNAD BIBLIOTEK OCH LÄGENHETER		INNEHÅLL	
BOTTENPLAN - PLAN 10 - DEL 2		A1	
STYR- OCH ÖVERVAKNINGSSYSTEM		SKALA	
S-81-1-D102		1:50	
		NUMMER	
		BET	