



..\\..\\A1 - Modeller\\Export DWG\\A-4.0-P-D202.dwg X:\\..\\Transit\\Entities\\TM\\Uppdrag\\2021\\210550 Kråkan 1 - Centrumhuset\\Fstyr.dwg

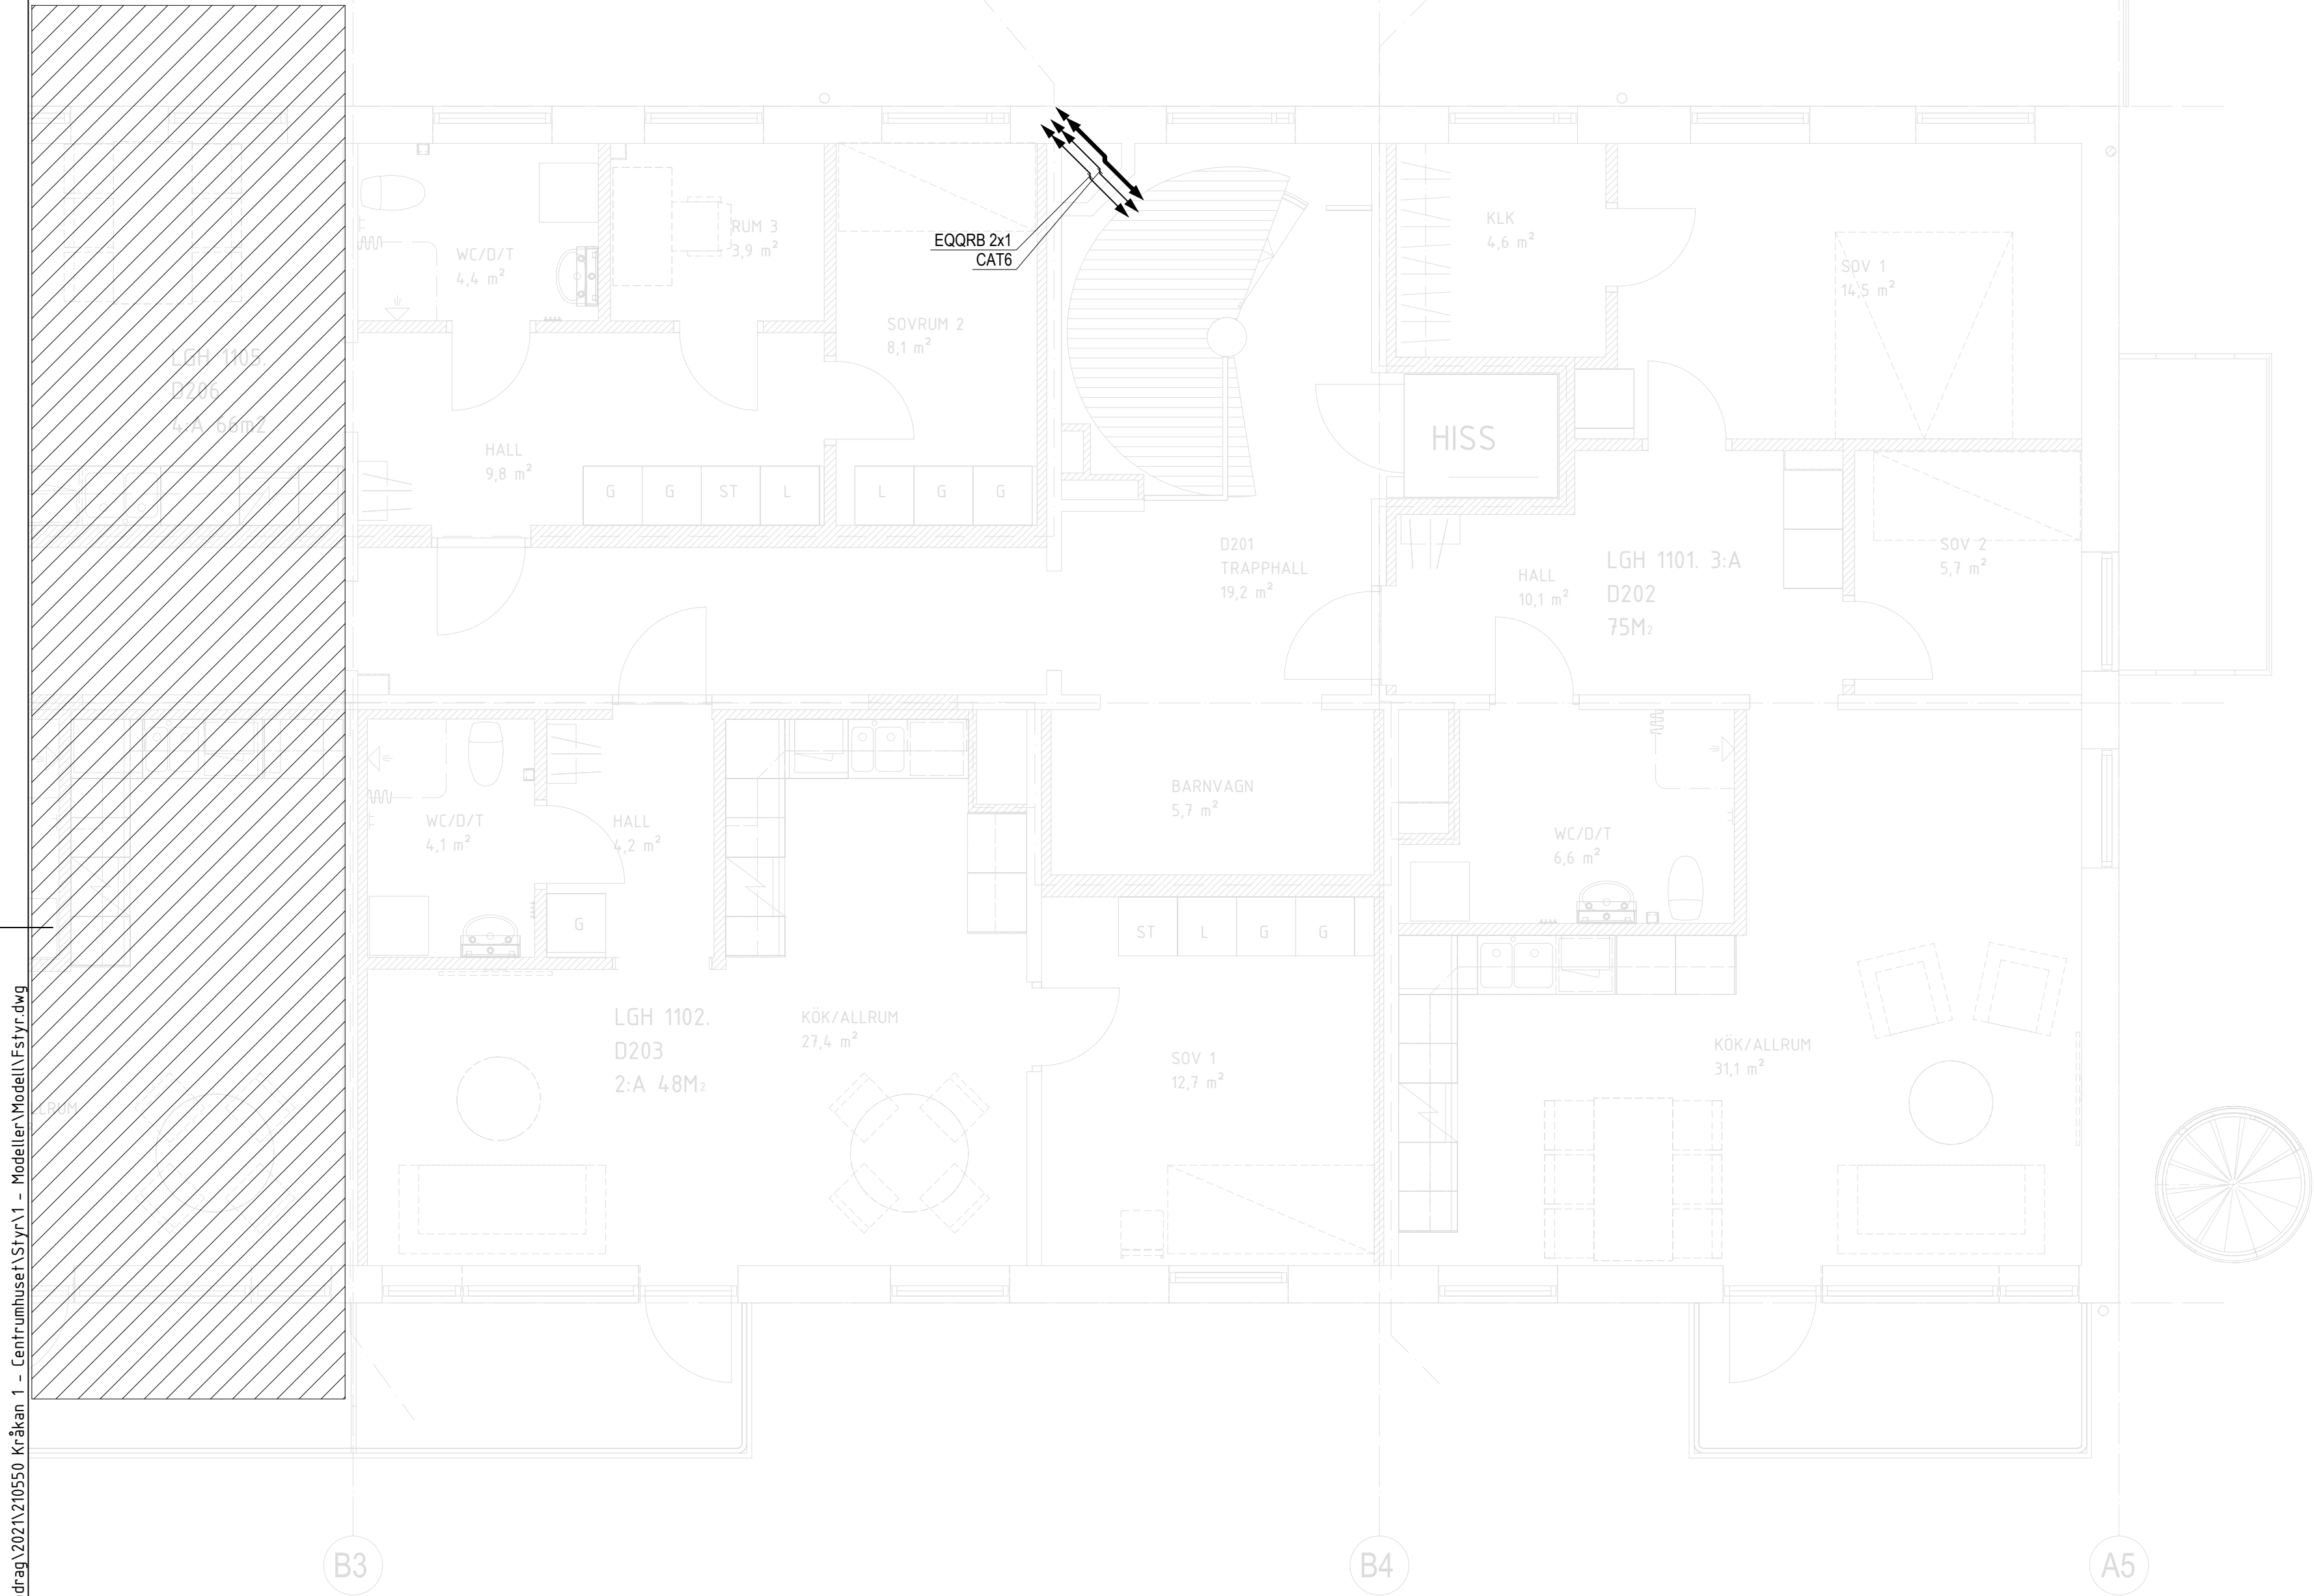


LAGER: SB11

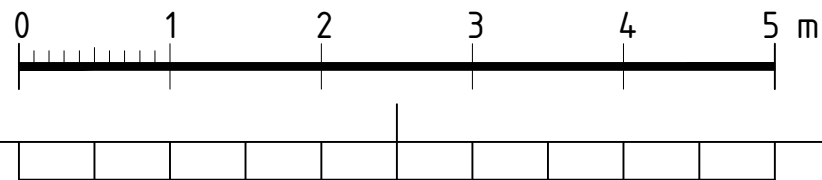

FÖRESKRIFTER

STYRKABEL 3X1,5 MÅNGTRÄDIG HALOGENFRI
ANVÄNDS DÄR ANNAT EJ ANGES

LEDNING MELLAN SÄKERHETSBRYTARE OCH MOTOR
SKALL VARA AV SAMMA TYP SOM MATANDE KABEL
TILL SÄKERHETSBRYTARE

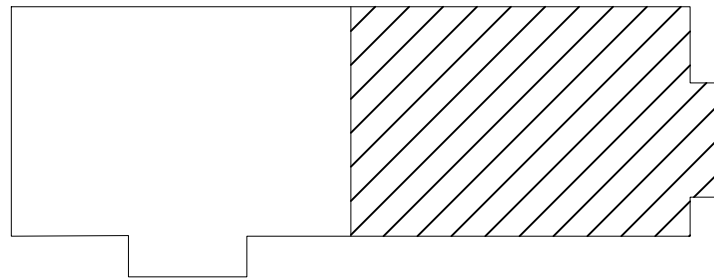

FÖRFRÅGNINGSUNDERLAG		STATUS
BYGGHANDLING		HANDLING
DATUM 2025-02-26	ÄNDRING/PM	ÄNDRING
CENTRUMHUSET HUS D KRÅKAN 1, ROBERTSFORS		PROJEKT
ÅF-Infrastructure AB Storgatan 103 921 32 Lycksele Tel: 010-505 00 00		ANSVARIG PART
KONTAKTPERSON Simon Rudin	André Sjölander	SKAPAD AV
GODKÄND AV Simon Abrahamsson	D0182343 (210550)	UPPDRAGSNUMMER
PLANRITNING		RITNINGSKATEGORI
OMBYGGNAD BIBLIOTEK OCH LÄGENHETER PLAN 1 TR - PLAN 20 - DEL 2 STYR- OCH ÖVERVAKNINGSSYSTEM		INNEHÅLL A1 FORMAT 1:50 SKALA BET
S-81-1-D202		NUMMER