
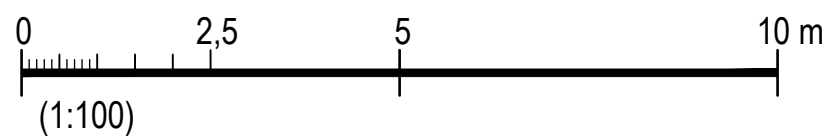


TECKENFÖRKLARING

KOORDINATSYSTEM: SWEREF 99 20 15
HÖJDSYSTEM: RH 2000
HÖJD- OCH MÄTTANGIVELSER ANGES I METER.

- + 45.71 BEFINTLIGA HÖJDER
- FASTIGHETSGRÄNS
- ARBETSOMRÅDE
- FASAD MED ENTRÉPIL
- BELÄGGNINGSKANT
- SKÄRM TAK, 3M ÖVER MARK
- STÖDMUR GRUNDLÄGGNING CARPORT
- MURKRÖN
- TRÄDGÅRDSKANTSTEN
- HÄCK
- SKRAPGALLER
- DAGVATTENBRUNN
- DRÄNERINGSBRUNN
- SPILLVATTENBRUNN
- BELYSNINGSSTOLPE
- BUSKAR/TRÄD
- DRÄNERINGSLEDNING
- VATTENLEDNING
- SPILLVATTENLEDNING
- DAGVATTENLEDNING
- KULVERT BETONG DIM: 300mm
- FJÄRRVÄRME
- SIGNALKABEL FJÄRRVÄRME
- OPT-LEDNING
- TELE-LEDNING
- EL-LEDNING
- BELYSNINGSKABEL

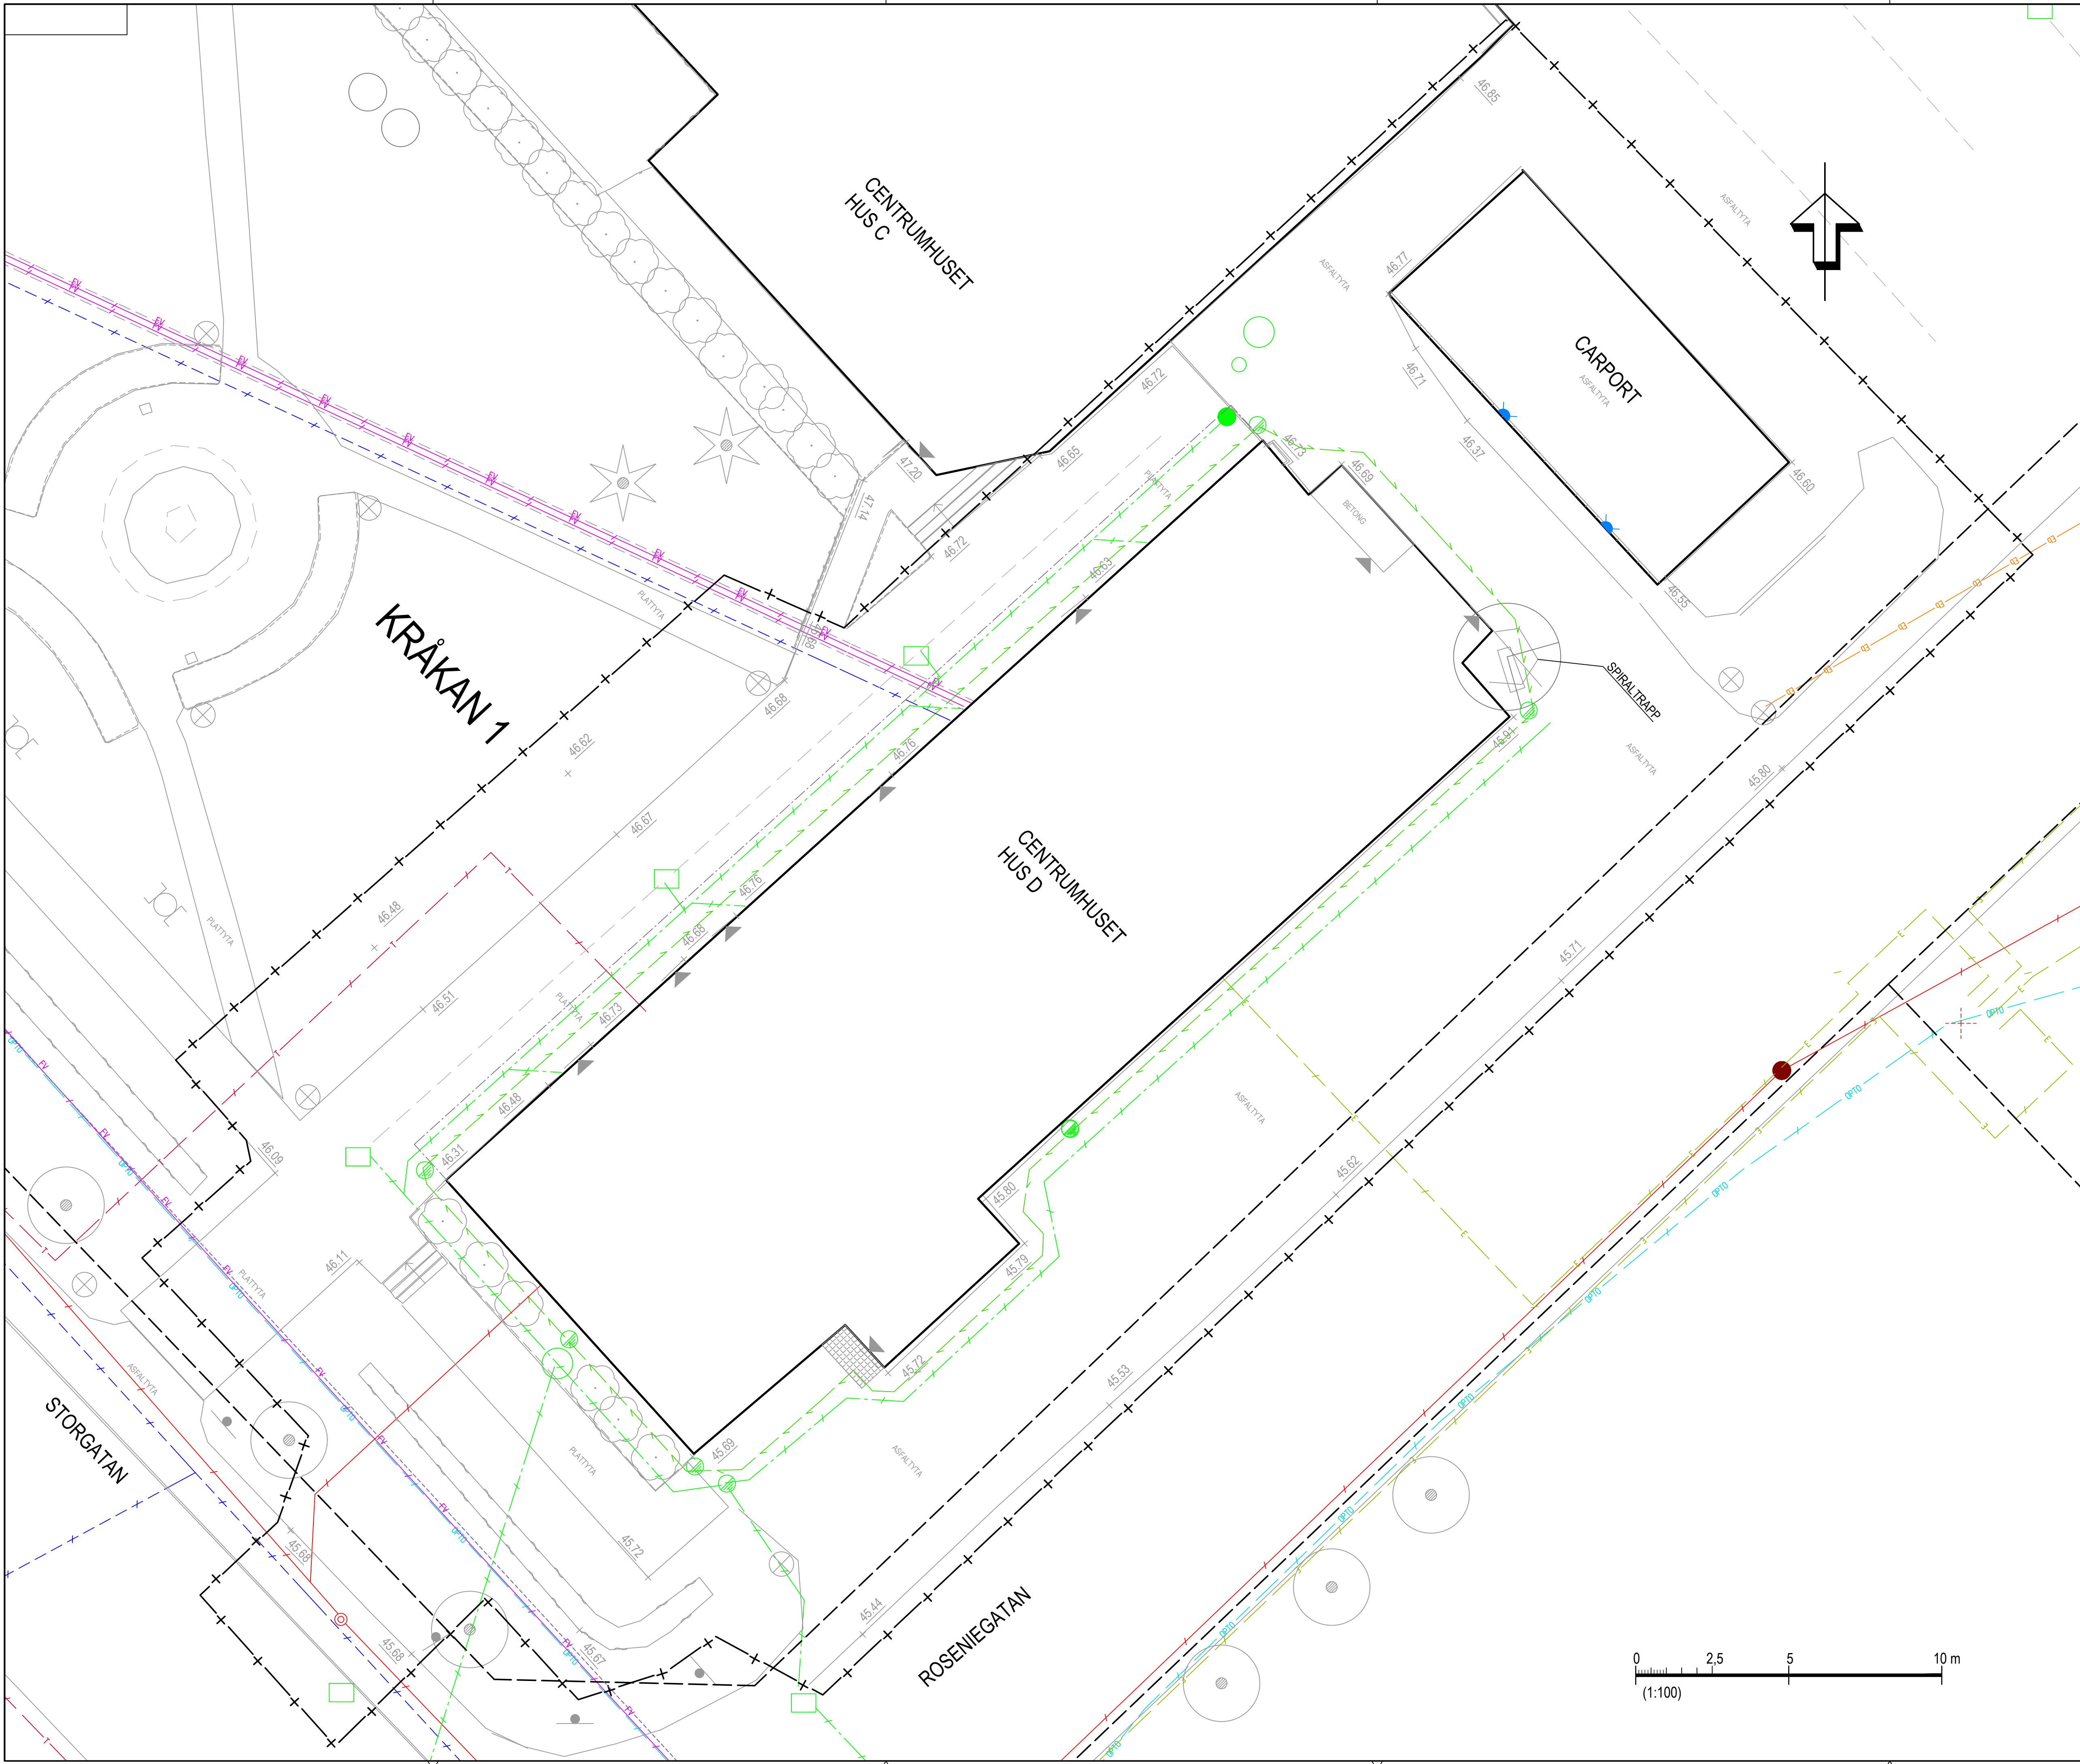

BET	ÄNDRINGEN ÄVSKER	DATUM	SIGN
FÖRFRÅGNINGSUNDERLAG		DATUM	ÄNDRING
2025-02-26		PROJEKT	ANSVARIG PART
CENTRUMHUSET HUS D KRÅKAN 1, ROBERTSFORS		AFRY	
E.PALAGE	KONTAKTPERSON	E.PALAGE	SKAPAD AV
E.PALAGE	GRÄNSÄR	210550	UPPERÄSSNUMMER
PLANRITNING		RITNINGSKATEGORI	
OMBYGGNAD BIBLIOTEK OCH LÄGENHETER		INNEHÅLL	FORMÅT
BEFINTLIGHETSPLAN		A1	SKALA
C-01-1-D000		NUMMER	BET