


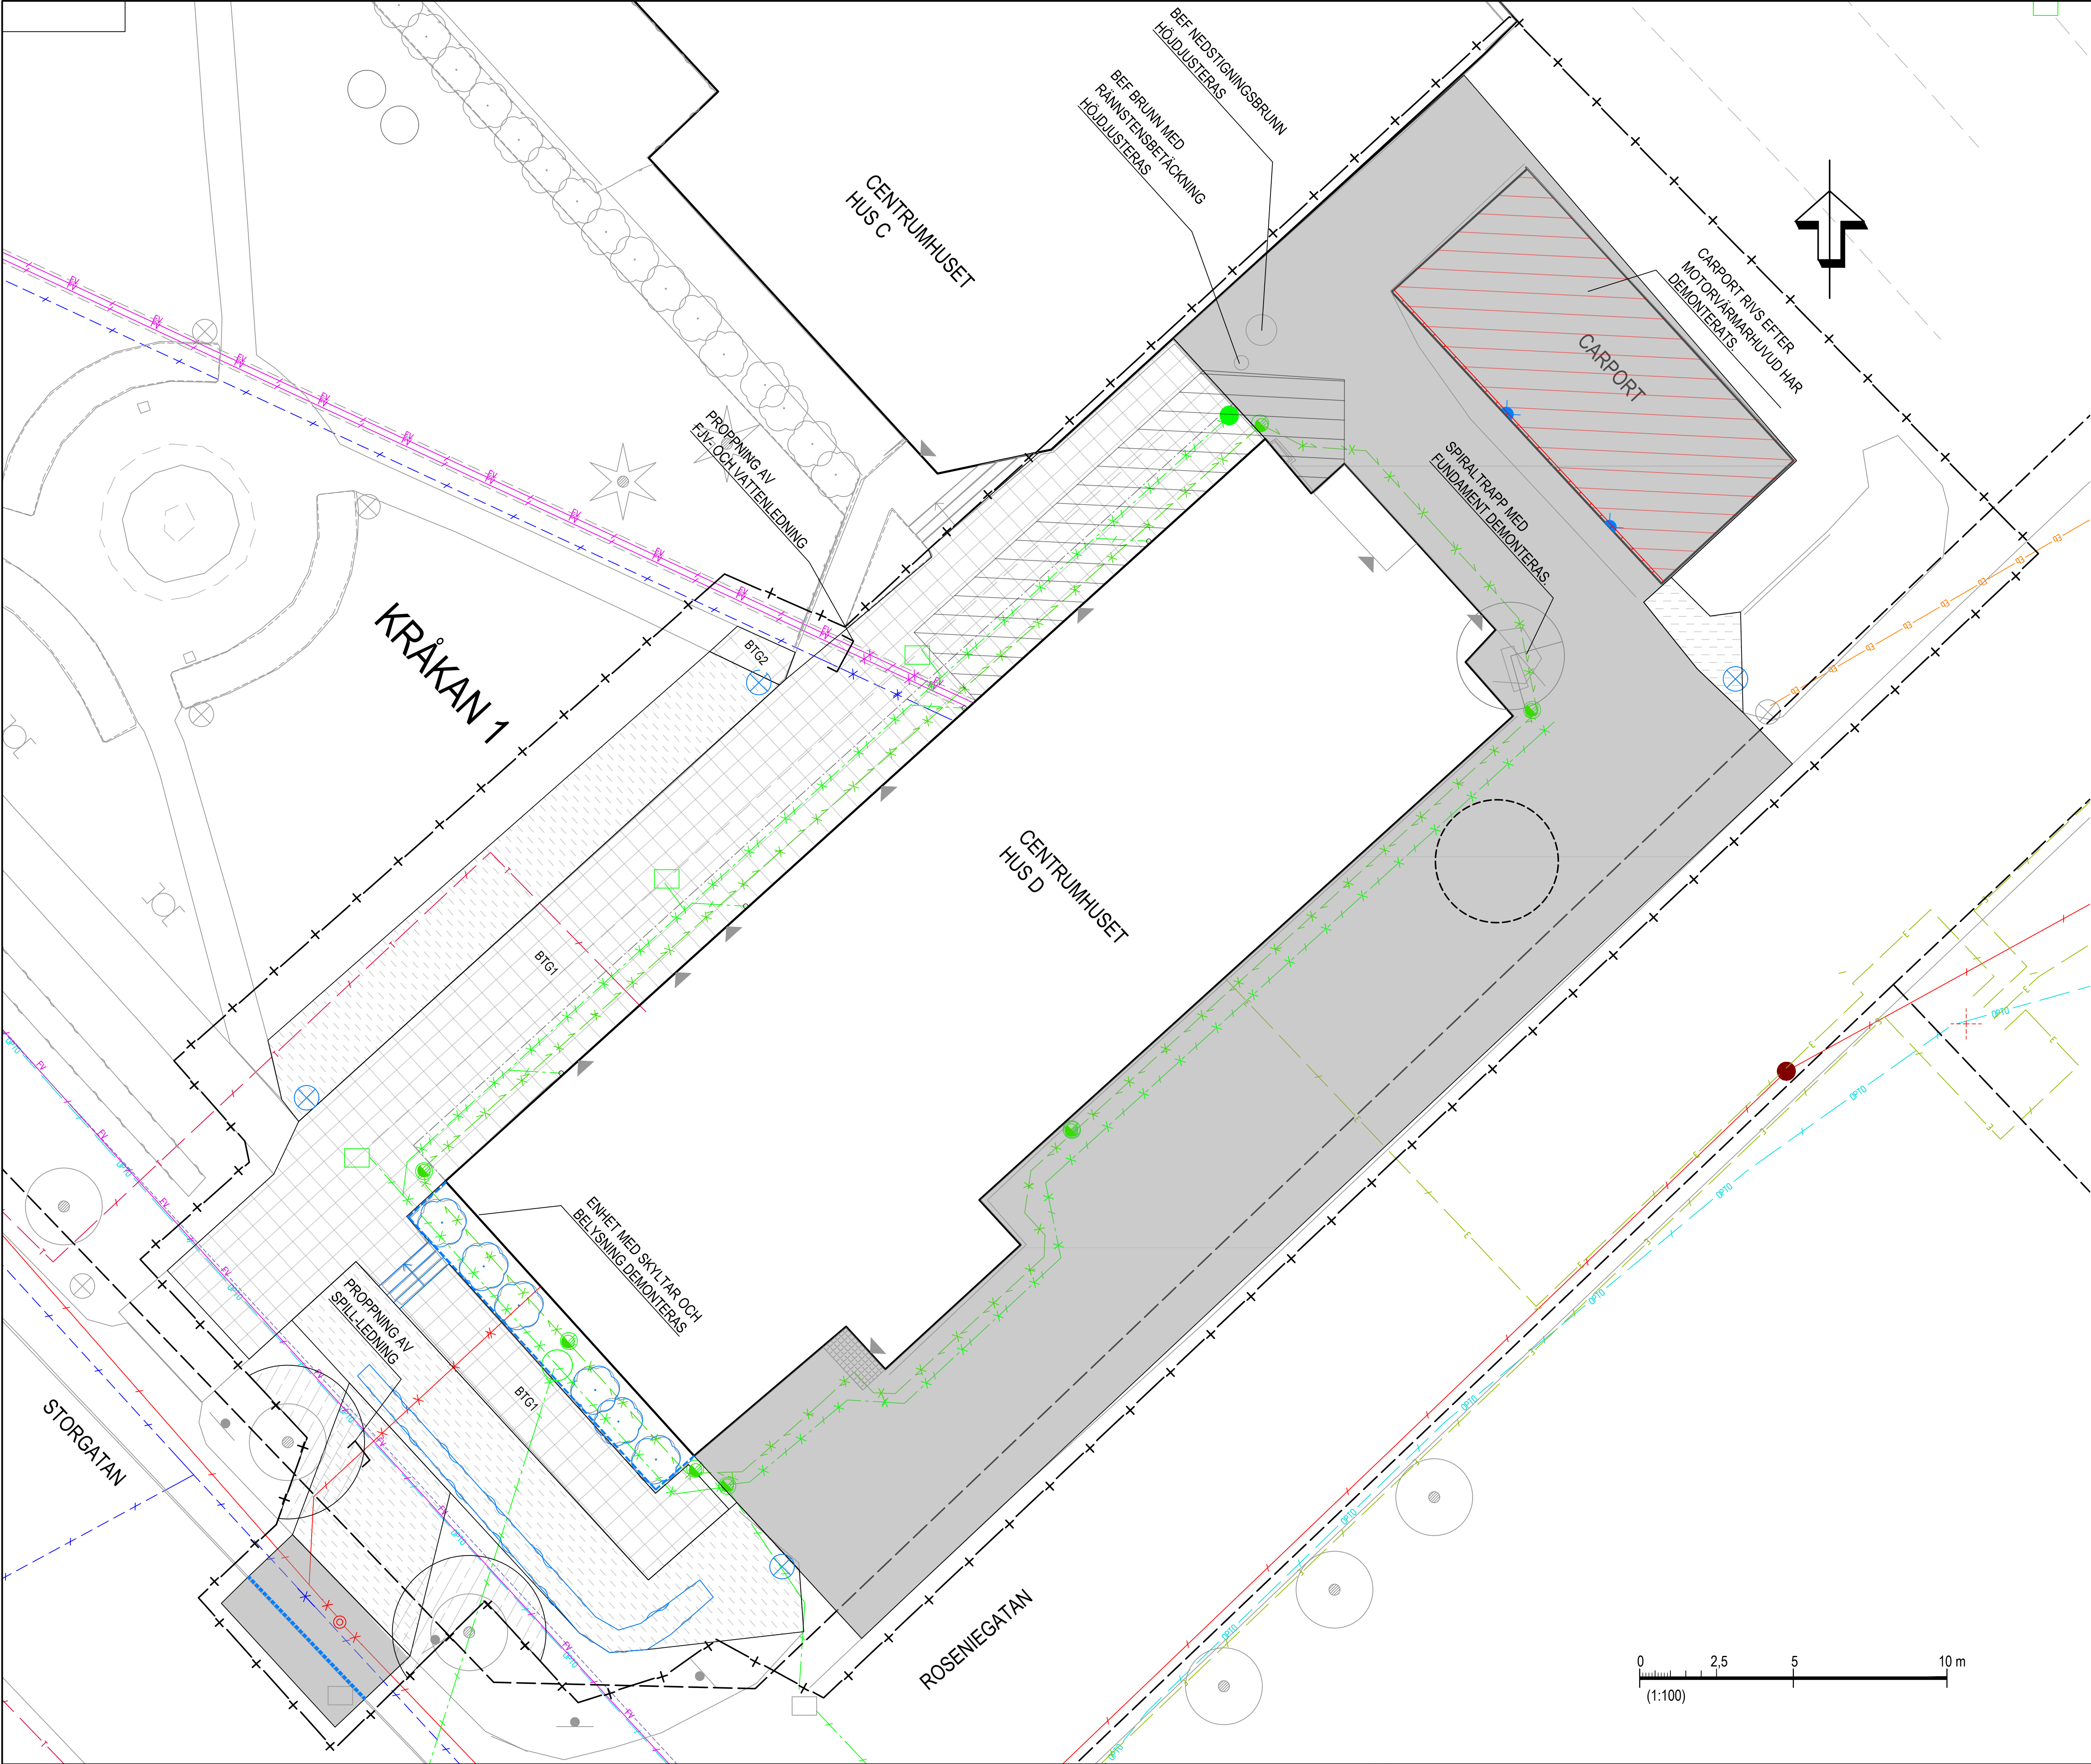

TECKENFÖRKLARING

KOORDINATSYSTEM: SWEREF 99 20 15
HÖJDSYSTEM: RH 2000
HÖJD- OCH MÄTTANGIVELSER ANGES I METER.

- ARBETSSOMRÅDE
- OMRÅDE FÖR PROVGROP
- FÖRSIKTIG SCHAFTSKYDD AV ROTZON
- STRÄCKA FÖR SPONT
- RIVNING
- STÖDMUR GRUNDLÄGGNING CARPORT
- DRÄNERINGSLEDNING
- VATTENLEDNING
- SPILLVATTENLEDNING
- DAGVATTENLEDNING
- KULVERT BETONG DIM: 300mm
- FJÄRRVÄRME
- DAGVATTENBRUNN
- DRÄNERINGSBRUNN
- SPILLVATTENBRUNN
- ASFALT

- DEMONTERING
- BETONGKANTSTÖD
- TRÄDGÅRDSKANTSTEN
- HÄCK
- PLATTYTTA, BTG 1 & BTG 2
- VEGETATIONSAVTAGNING
- MOTORVÄRMARHUVD*
- BELYSNINGSSTOLPE
- BLOCKSTEGSTRAPP
- BUSKAR

ANM:
LEDNINGAR I KULVERT SKA RIVAS DÄR DE FRAMKOMMER I SCHAFT.
*MOTORVÄRMARHUVD DEMONTERAS AV EL-ENTREPRENÖR.

BET	ÄNDRINGEN ÄVSR	DATUM	SIGN
FÖRFRÅGNINGSUNDERLAG			
2025-02-26			
CENTRUMHUSET HUS D KRÅKAN 1, ROBERTSFORS			
AFRY			
E.PALAGE	KONTAKTPERSON	E.PALAGE	SKAPAD AV
E.PALAGE	GRAND AV	210550	UPPERANSNUMMER
PLANRITNING			
OMBYGGNAD BIBLIOTEK OCH LÄGENHETER			
RIVNINGSPÅN			
C-93-1-D000			