

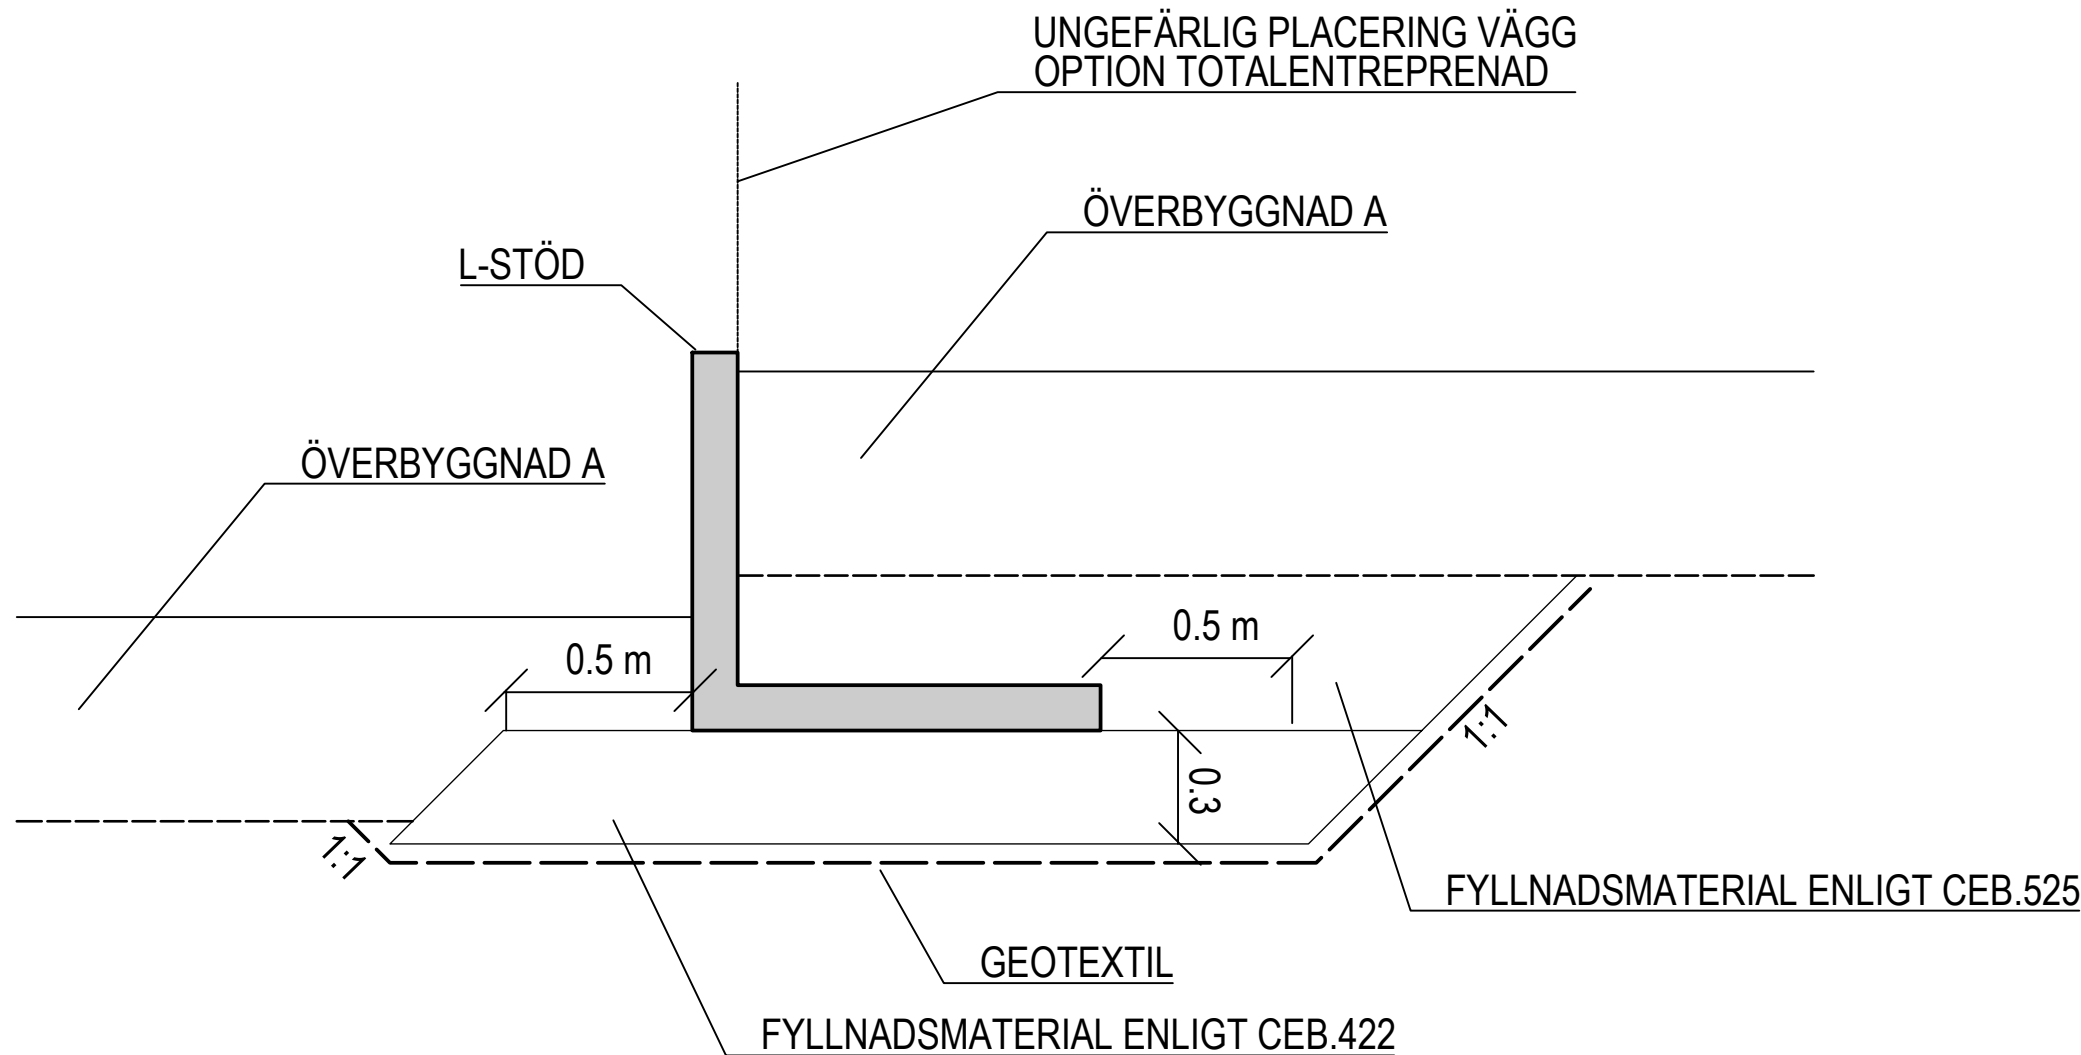


TYPSEKTION NY STÖDMUR

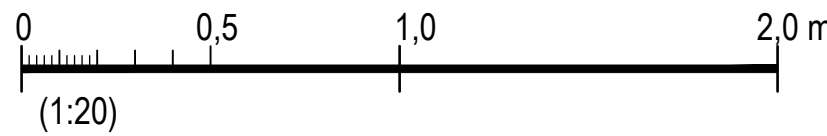

ELEVATION NY STÖDMUR

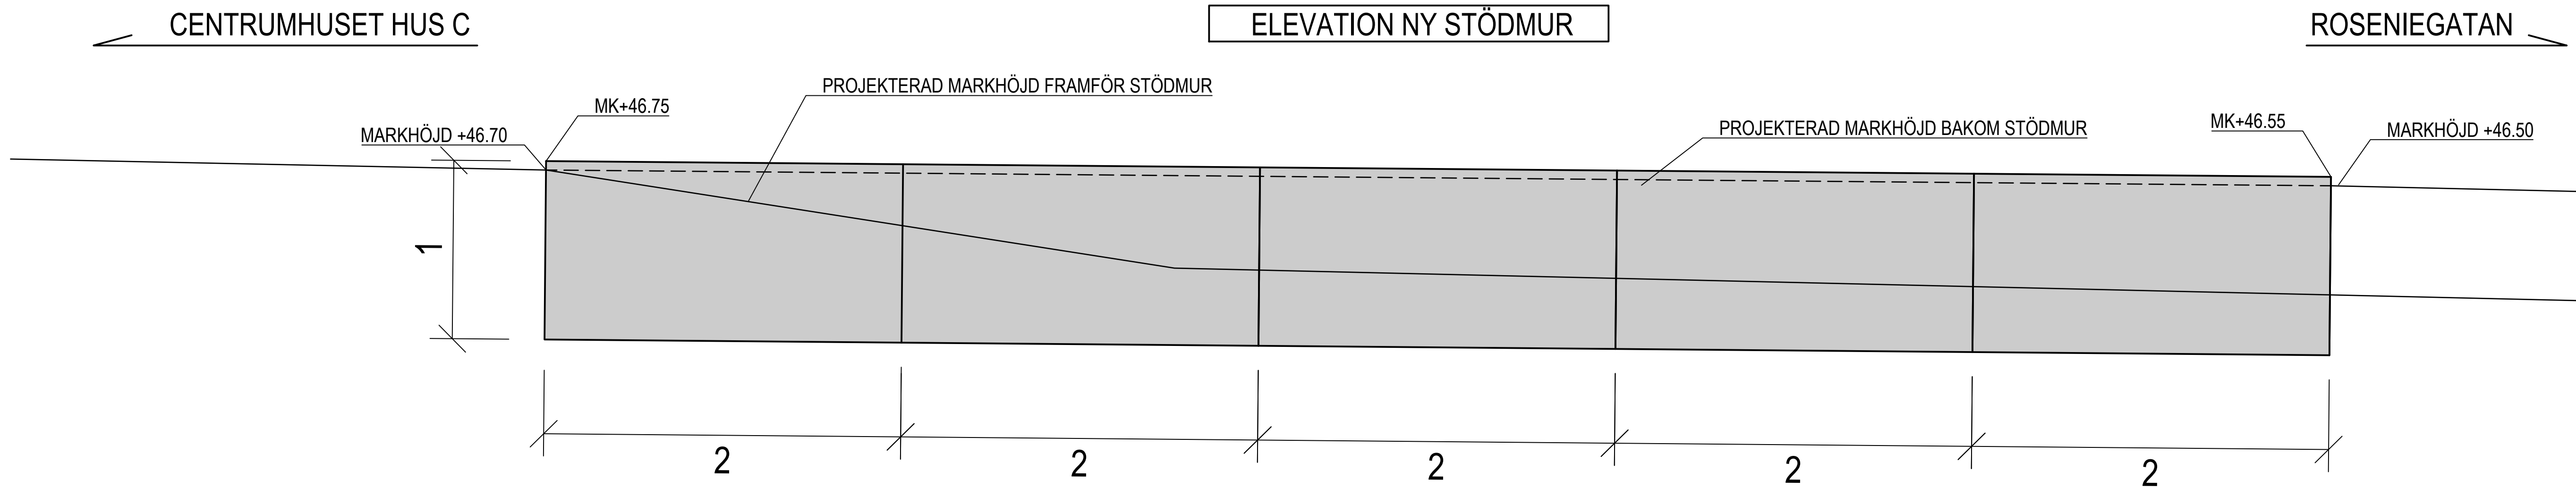

BET	ÄNDRINGEN AVSER	DATUM	SIGN
STATUS			
FÖRFRÅGNINGSUNDERLAG			
DATUM	ÄNDRING	PROJEKT	ANSVARIG PART
2025-02-26	-		
CENTRUMHUSET HUS D KRÅKAN 1, ROBERTSFORS			
AFRY			
E.PALAGE	KONTAKTPERSON	E.PALAGE	SKAPAD AV
E.PALAGE	GRÄND AV	210550	UPPERINGSNUMMER
DETALJRITNING		RITNINGSKATEGORI	
OMBYGGNAD BIBLIOTEK OCH LÄGENHETER NY STÖDMUR		INNEHÅLL	FORMAT
		A1	SKALA
		1:20	BET
M-30-6-D000		NUMMER	