


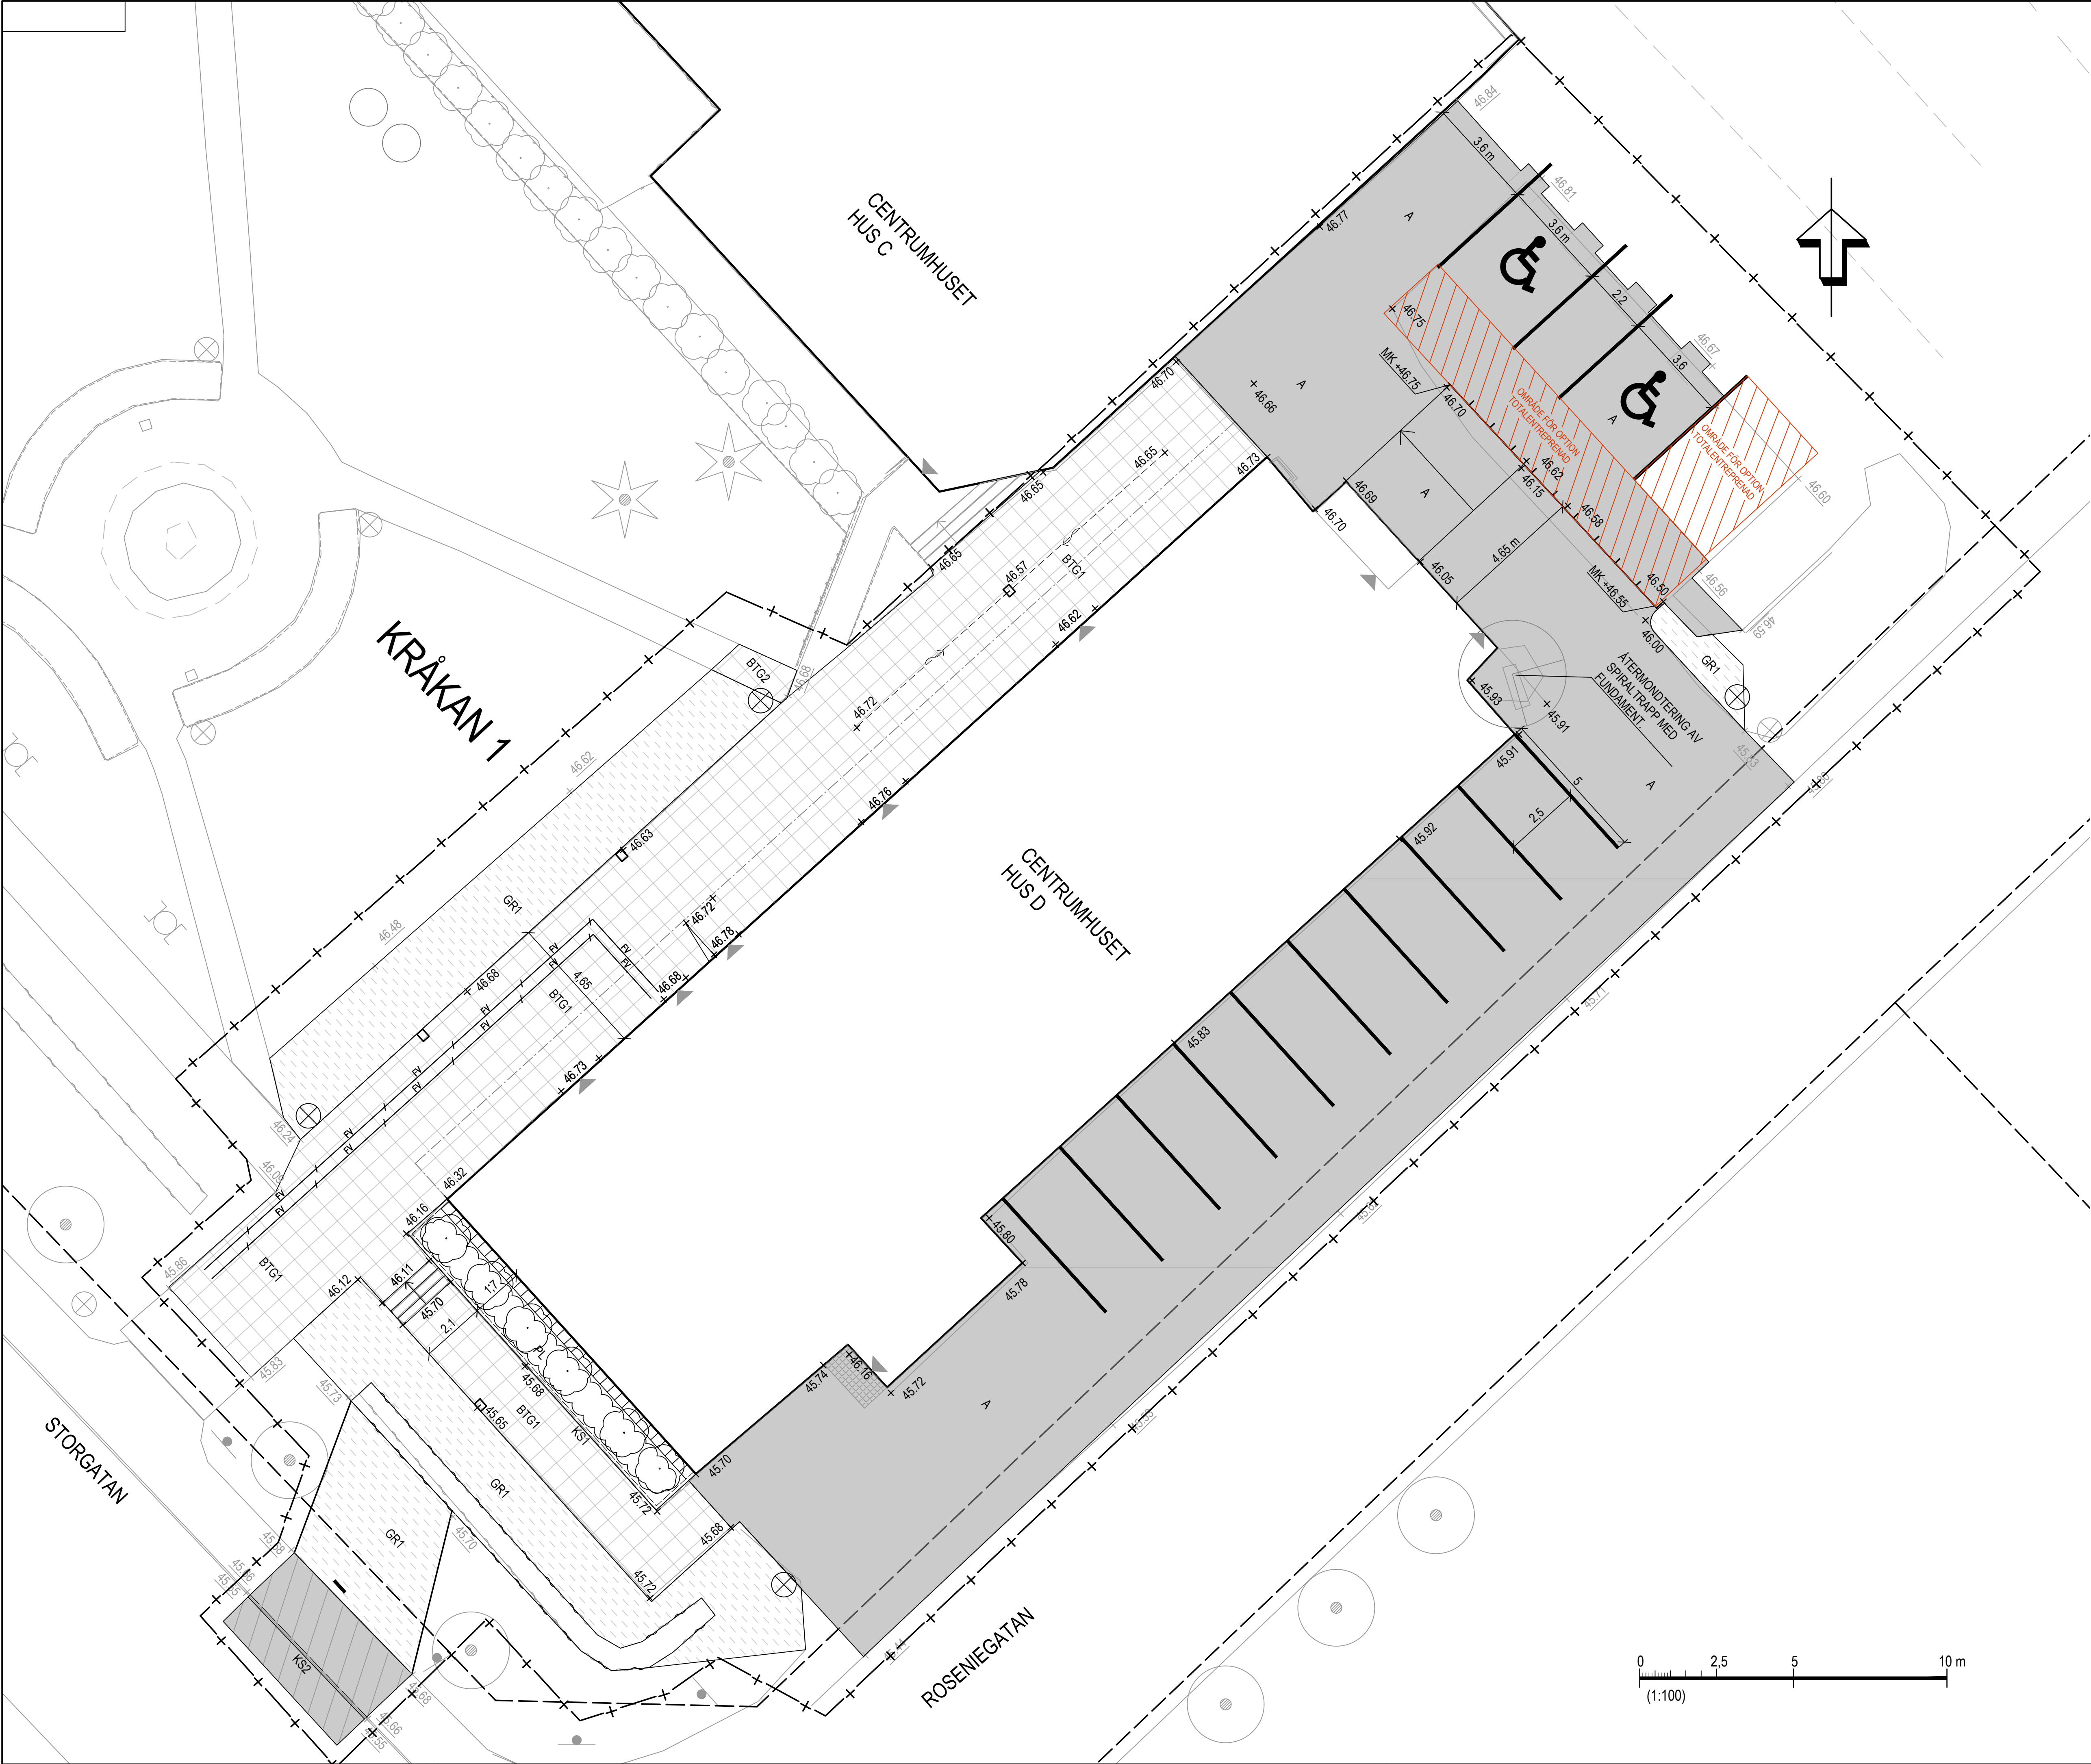


TECKENFÖRKLARING

KOORDINATSYSTEM: SWEREF 99 20 15
HÖJDSYSTEM: RH 2000
HÖJD- OCH MÄTTANGIVELSER ANGES I METER.

- ARBETSOMRÅDE
- FASTIGHETSGRÄNS
- + 45.71 BEFINTLIG HÖJD
- + 45.92 FÖRESLAGEN MARKHÖJD
- BELÄGGNINGSKANT
- LÄNGPUNKTSLINJE MED RIKTNINGSPIL
- STÖDMUR L-STÖD
- HÖJDANGIVELSE MURKRÖN
- MÄLNING
- FRIS AV BETONGPLATTOR
- A ASFALTYTA - ABT16
- GR1 GRÄSYTA
- PL PLANTERINGSYTA
- DAGVATTENBRUNN

- ÅTERSTÄLLNING/ÅTERMONTERING
- KS1 TRÄDGÅRDSKANTSTEN VISNING:100mm
- KS2 BETONGKANTSTEN VISNING:100mm
- HÄCK
- BTG1 PLATTYTA - 350X350
- BTG2 PLATTYTA - 210X105
- ASFALTYTA
- BUSKAR
- BELYSNINGSSTOLPE
- BLOCKSTEGSTRAPP

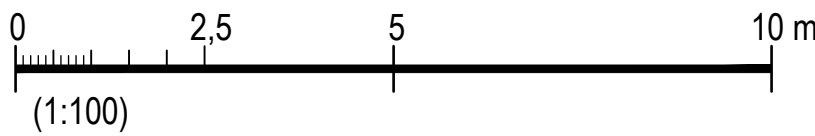

BET	ÄNDRINGEN AVSEER	DATUM	SIGN
FÖRFRÅGNINGSUNDERLAG			
2025-02-26	ÄNDRING	PROJEKT	ANSVARIG PART
CENTRUMHUSET HUS D KRÅKAN 1, ROBERTSFORS			
AFRY			
E.PALAGE	KONTAKTPERSON	E.PALAGE	SKAPAD AV
E.PALAGE	GRAND AV	210550	UPPERHÄLLSNUMMER
PLANRITNING		INNEHÅLL	FORMAT
OMBYGGNAD BIBLIOTEK OCH LÄGENHETER MARKPLANERINGSSPLAN		A1	SKALA
M-31-1-D000		NUMMER	BET