



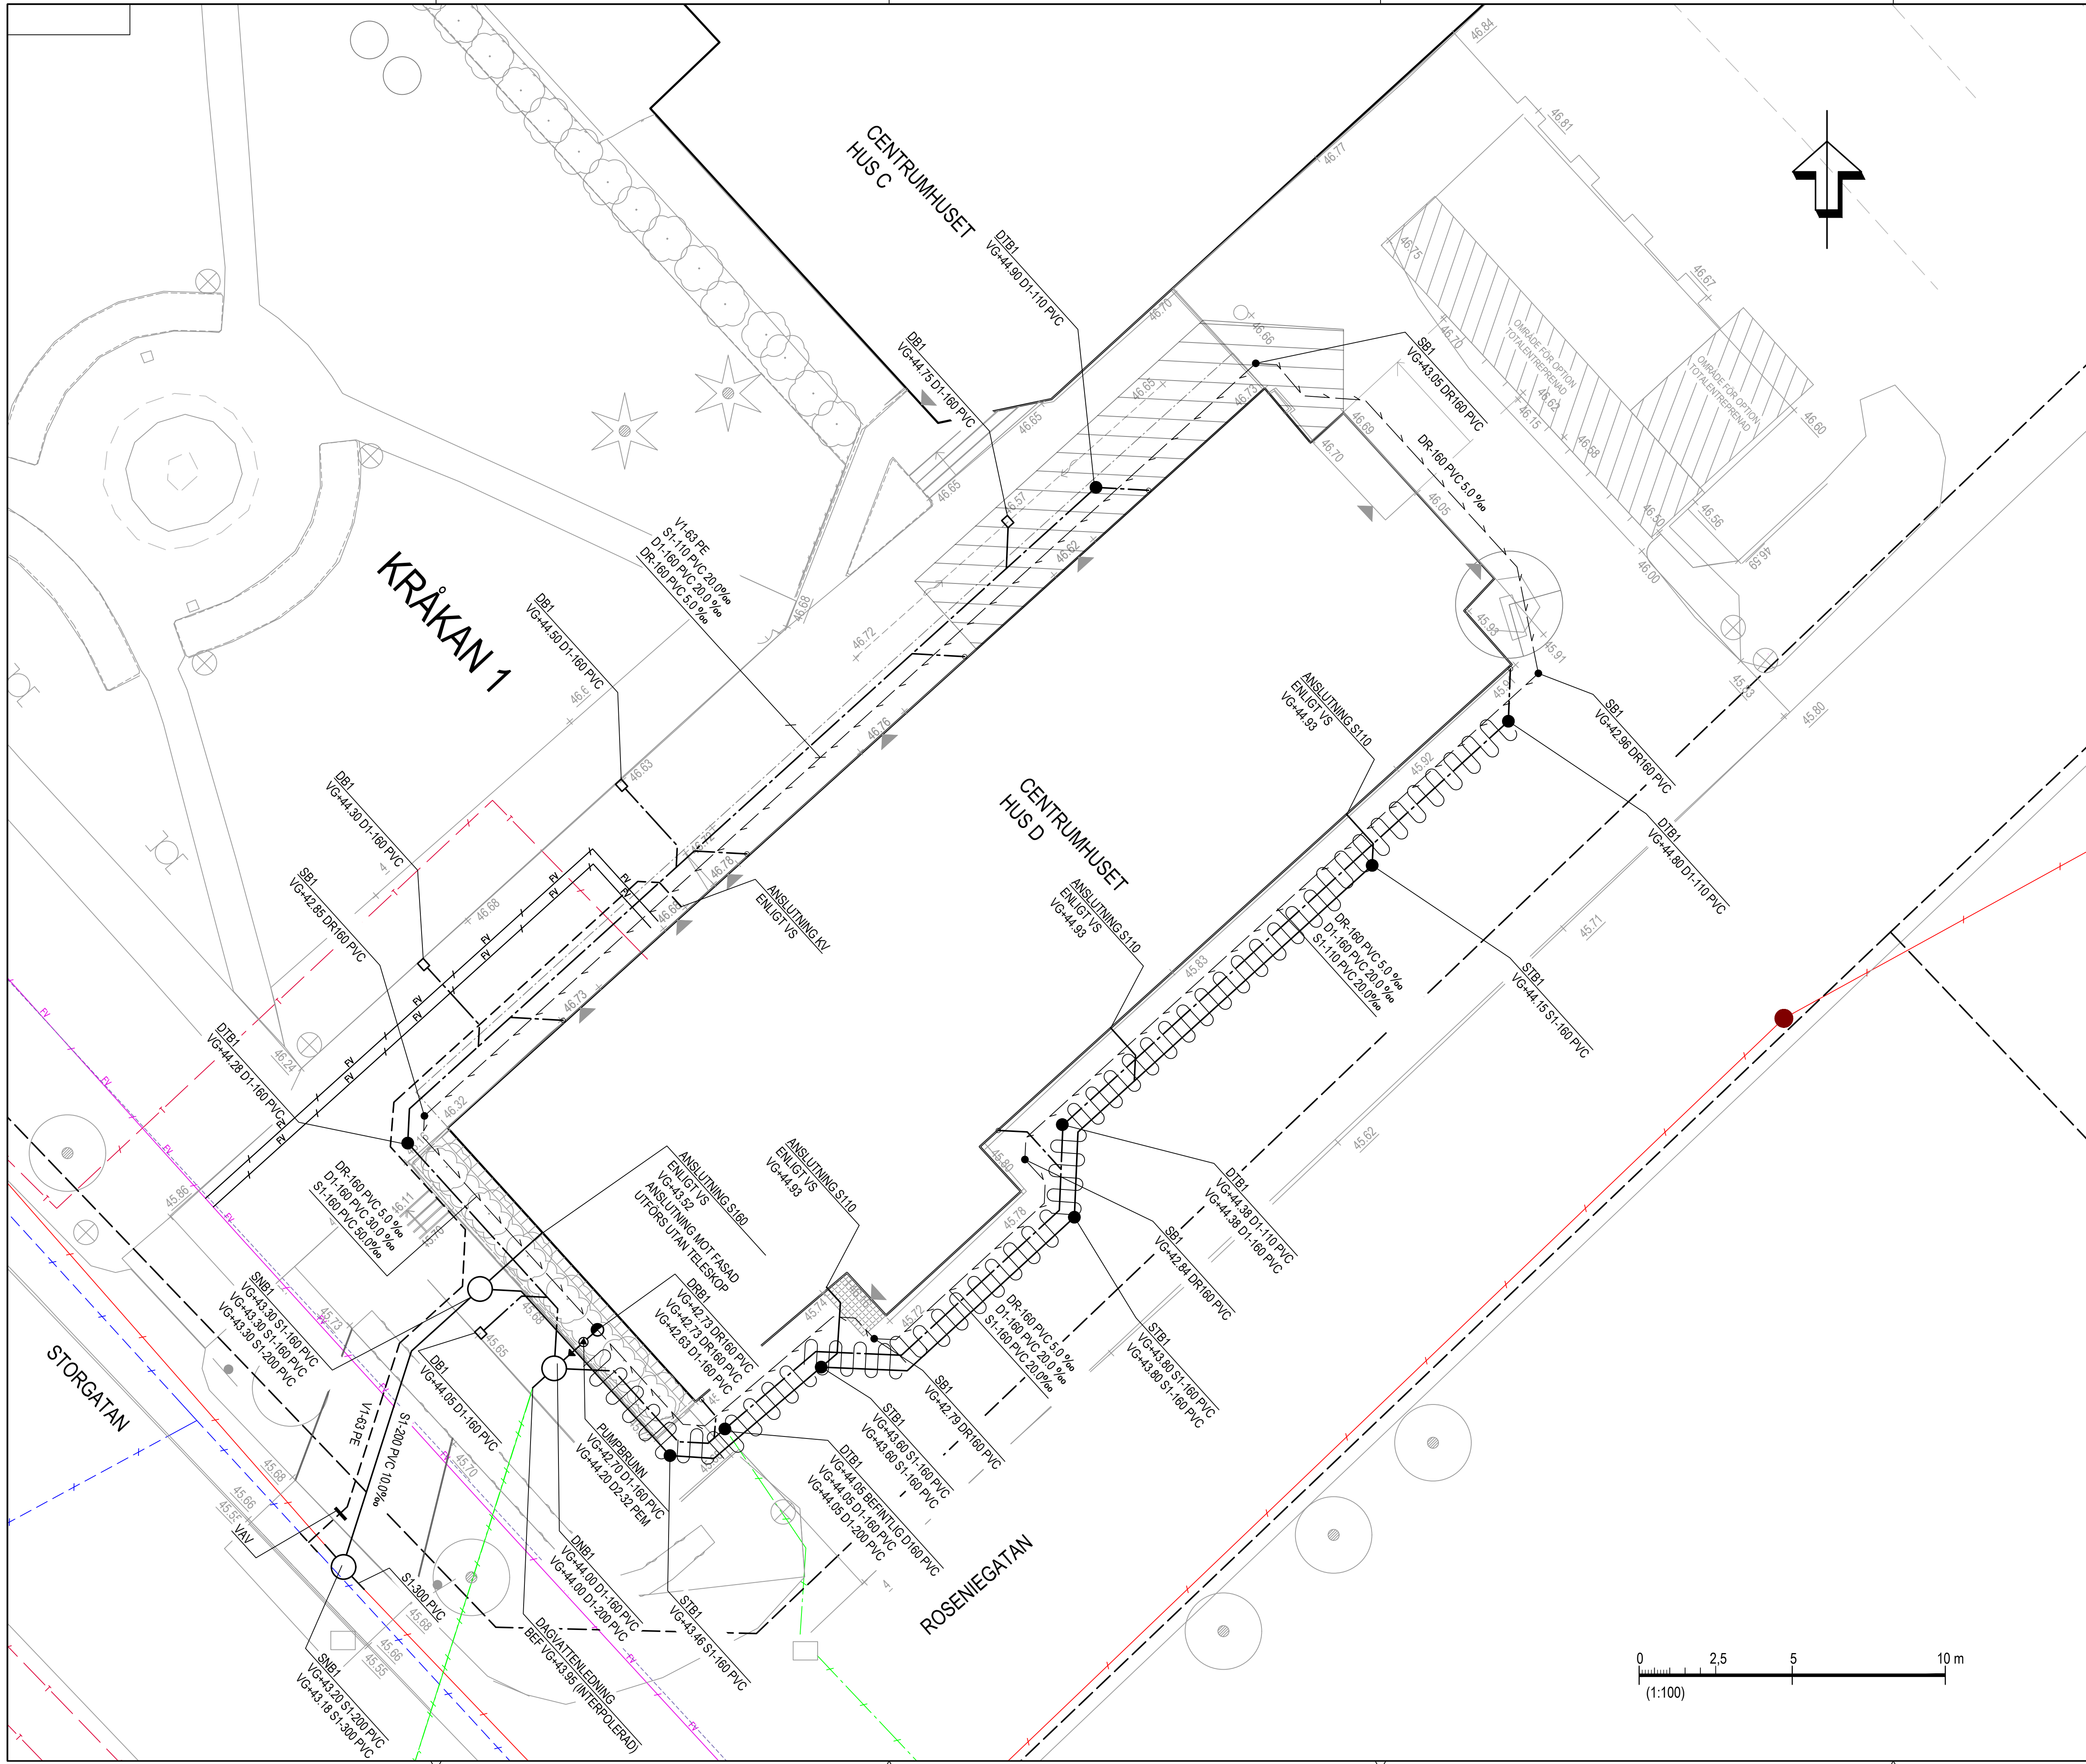

## TECKENFÖRKLARING

KOORDINATSYSTEM: SWEREF 99 20 15  
HÖJDSYSTEM: RH 2000  
HÖJD- OCH MÄTTANGIVELSER ANGES I METER.

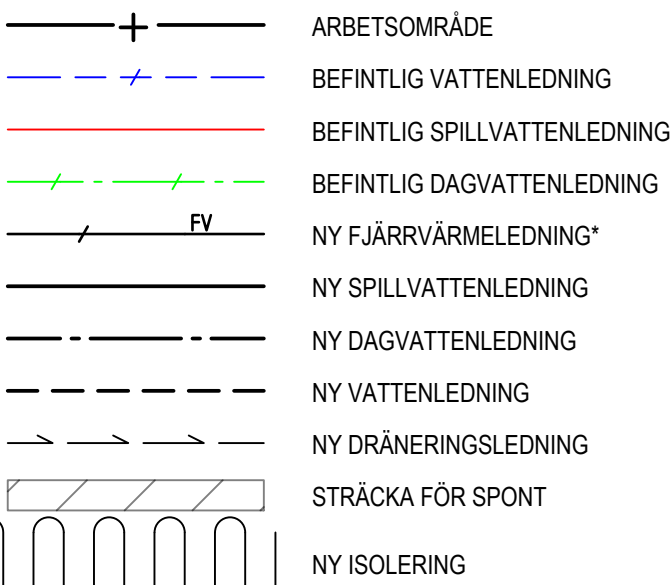

-  KILSLUDSVENTIL (VAV)
-  DAGVATTENBRUNN 400 PP MED (DB1)
-  GALLERBÄCK OCH SANDFÄNG
-  DAGVATTENBRUNN 400 PP MED
-  TÄTT LOCK OCH SANDFÄNG (DB2)
-  NEDSTIGNINGSBRUNN PÅ DAGVATTENLEDNING (DNB1)
-  NEDSTIGNINGSBRUNN PÅ SPILLVATTENLEDNING (SNB1)
-  TILLSYNSBRUNN 400 PP, SPILLVATTENLEDNING (STB1)
-  TILLSYNSBRUNN 400 PP, DAGVATTENLEDNING (DTB1)
-  DRÄNBRUNN, DRÄNLEDNING (DBR1)
-  SPOLBRUNN, DRÄNLEDNING (SB1)
-  STUPRÖR
-  PUMPBRUNN

ANM:  
JTGÄNDE LEDNING PUMPBRUNN 32 PEM.  
NY FJV-LEDNING REDOVISAR UNGEFÄRLIGT LÅGE FÖR NY FJV.  
SAMORDNING SKA SKE MED SKELLFTEÅ KRAFT FÖR EXAKT PLACERING  
DRÄNERING SKA I HÖGPUNKT ANLÄGGAS MED HJÄSSAN 150 MM  
UNDER KANTBALK.

|                                                                                       |                 |               |           |
|---------------------------------------------------------------------------------------|-----------------|---------------|-----------|
| BET                                                                                   | ÄNDRINGEN AVSER | DATUM         | SIGN      |
|                                                                                       |                 | STATUS        |           |
| FÖRFRÅGNINGSUNDERLAG                                                                  |                 | HANDLING      |           |
| 2025-02-20                                                                            | DATUM           | ÄNDRING       |           |
| -                                                                                     |                 | PROJEKT       |           |
| CENTRUMHUSET HUS D<br>KRÅKAN 1, ROBERTSFORS                                           |                 |               |           |
|                                                                                       |                 | ANSVARIG PART |           |
|  |                 |               |           |
| E.PALAGE                                                                              | KONTAKTPERSON   | E.PALAGE      | SKAPAD AV |
| E.PALAGE                                                                              | GODKÄND AV      | UPPLAGGNUMMER |           |
|                                                                                       | 210550          |               |           |
| PLANRITNING                                                                           |                 | RITNINGSSKALA |           |
| OMBYGGNAD BIBLIOTEK OCH LÅGENHETER<br>VA-PLAN                                         |                 | INNEHÅLL      | FORMAT    |
|                                                                                       |                 | A1            | SKALA     |
|                                                                                       |                 | 1:100         | BET       |
| R-51-1-D000                                                                           |                 | NUMMER        |           |