




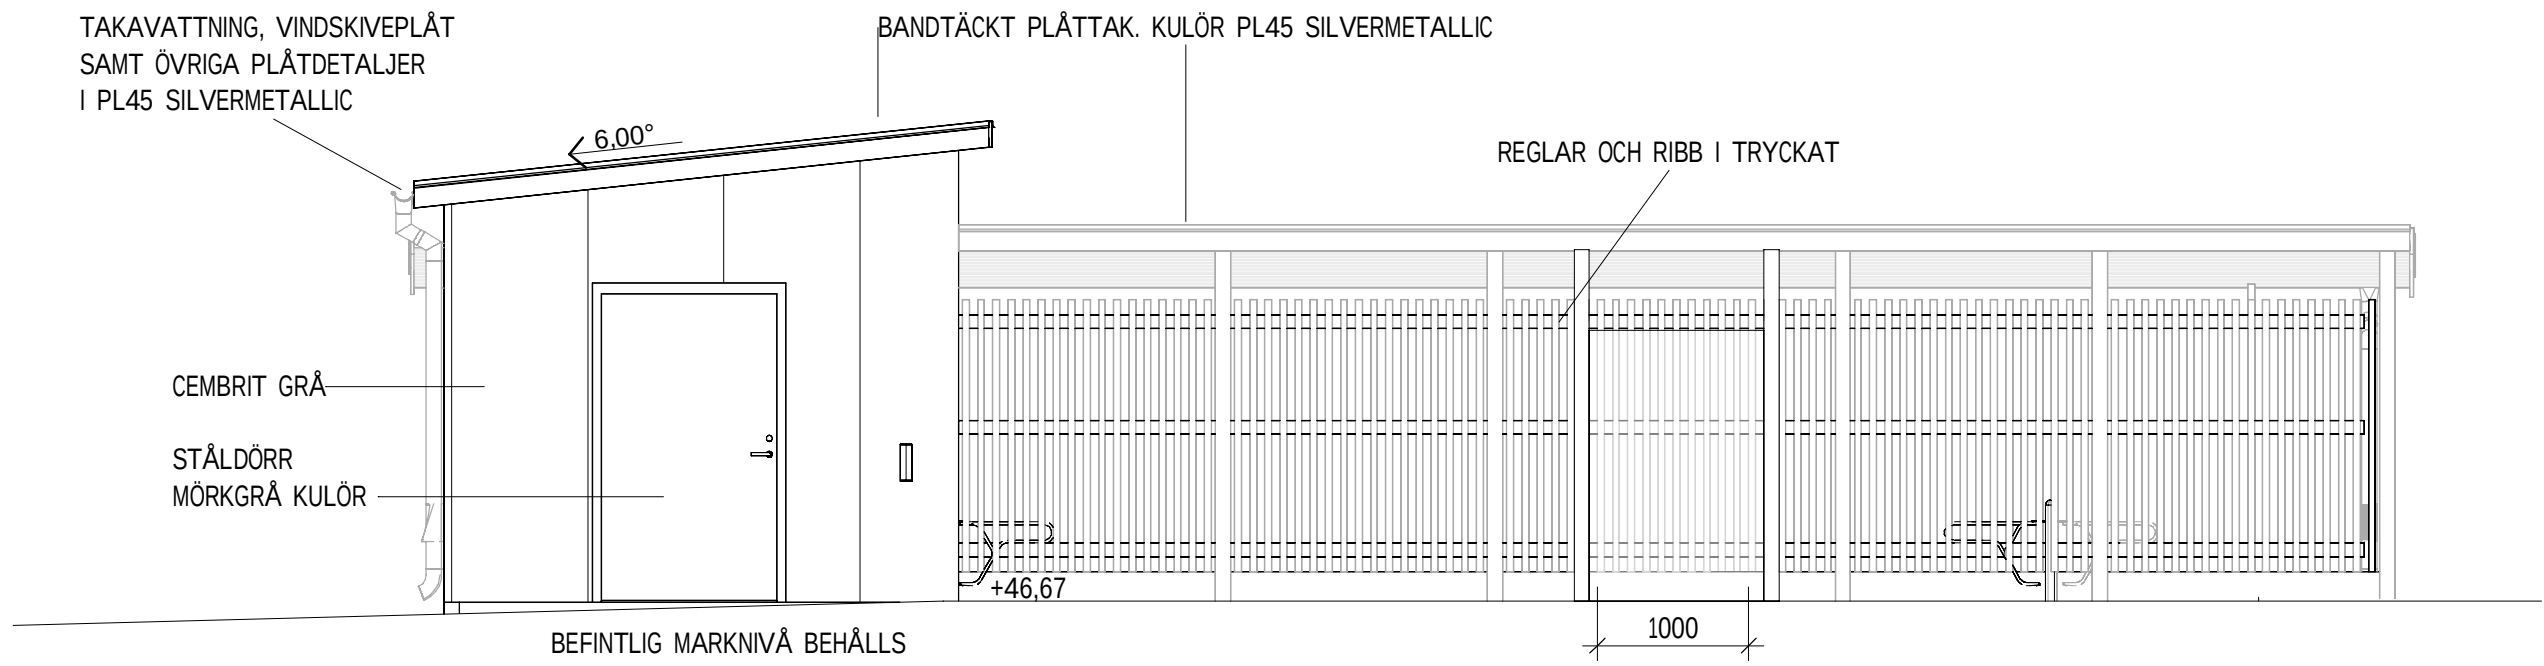


AVFALLSRUM - FASAD MOT NORDOST, PARKERING

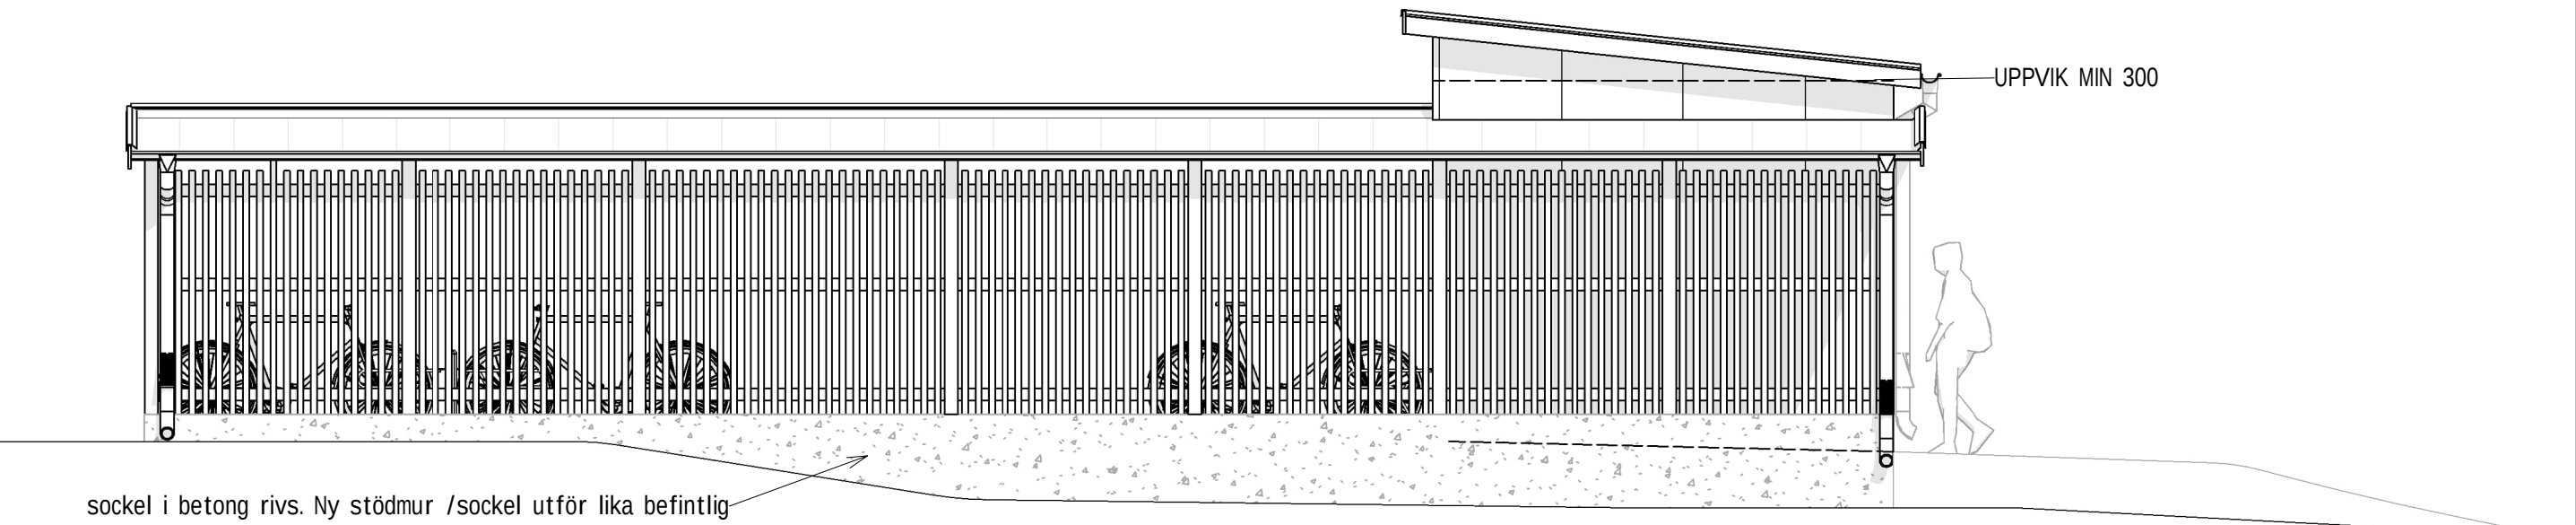


AVFALLSRUM - FASAD MOT SYDVÄST, STORGATAN

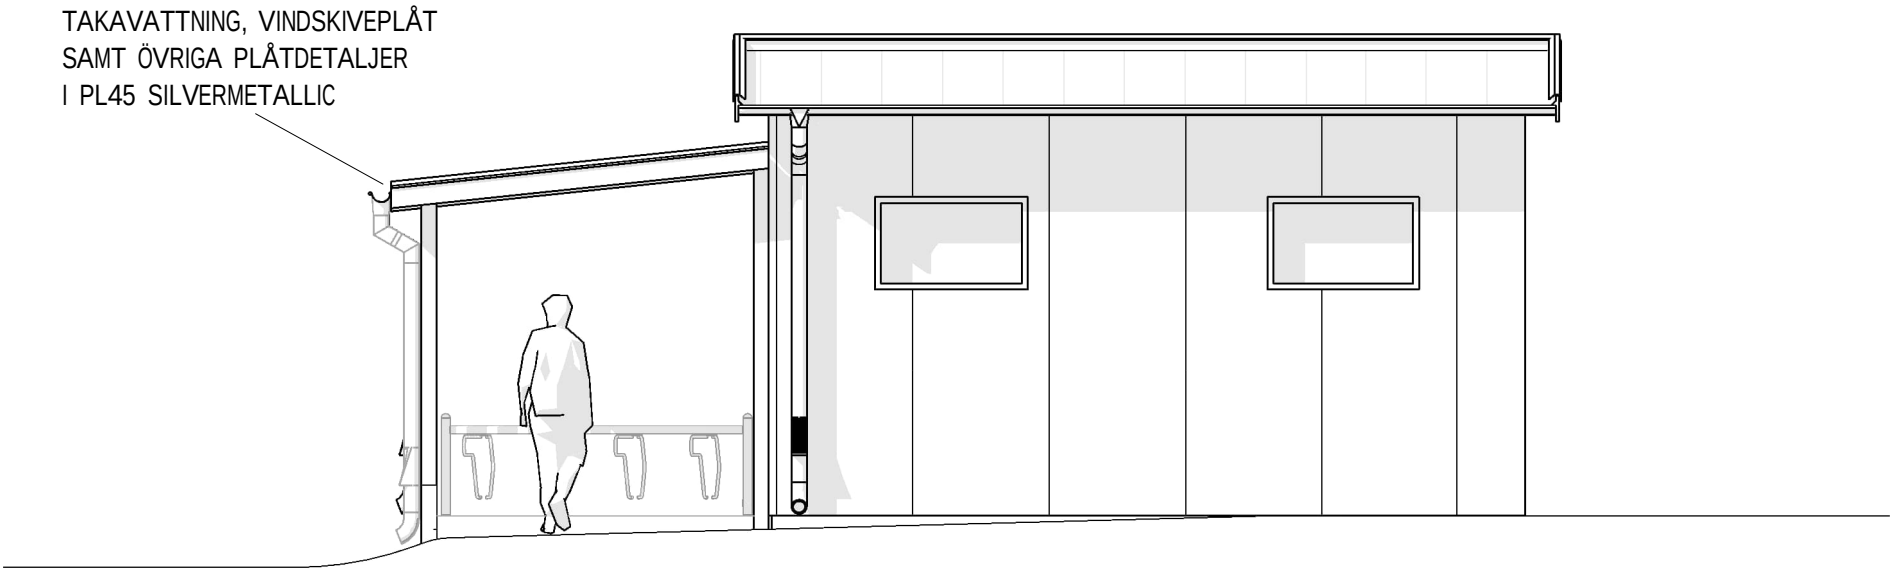


AVFALLSRUM - FASAD MOT SYDOST, ROSENIEGATAN

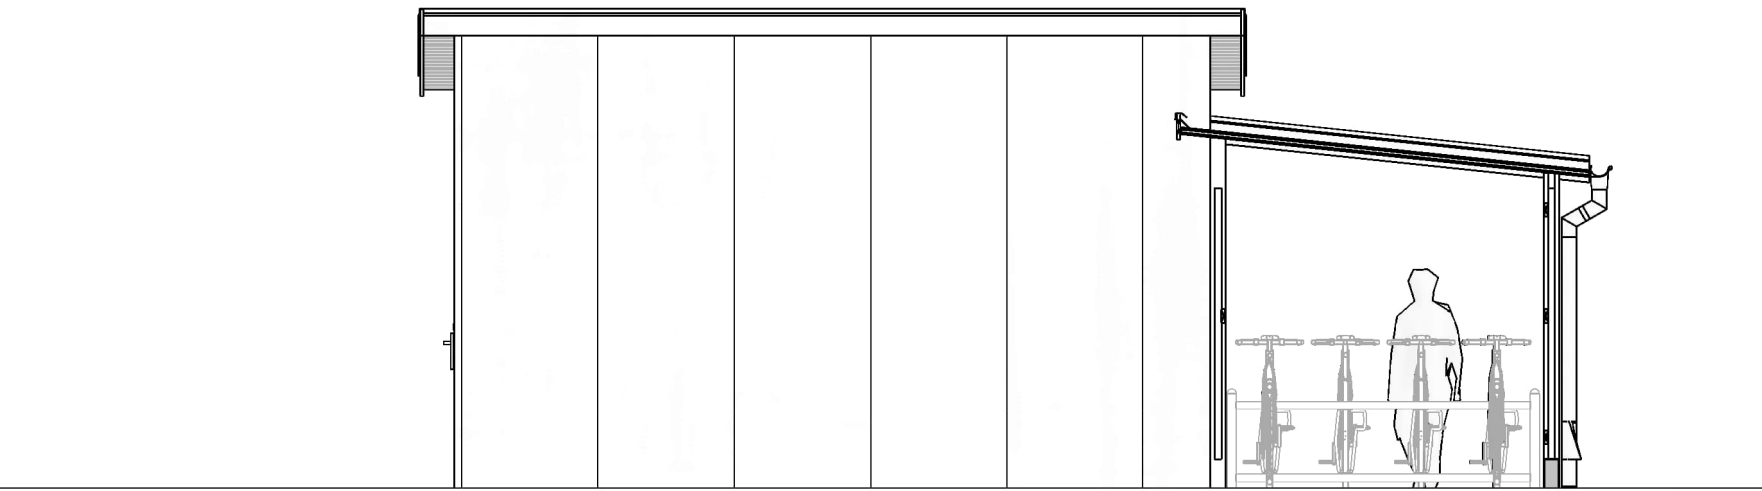


AVFALLSRUM - FASAD MOT NORDVÄST

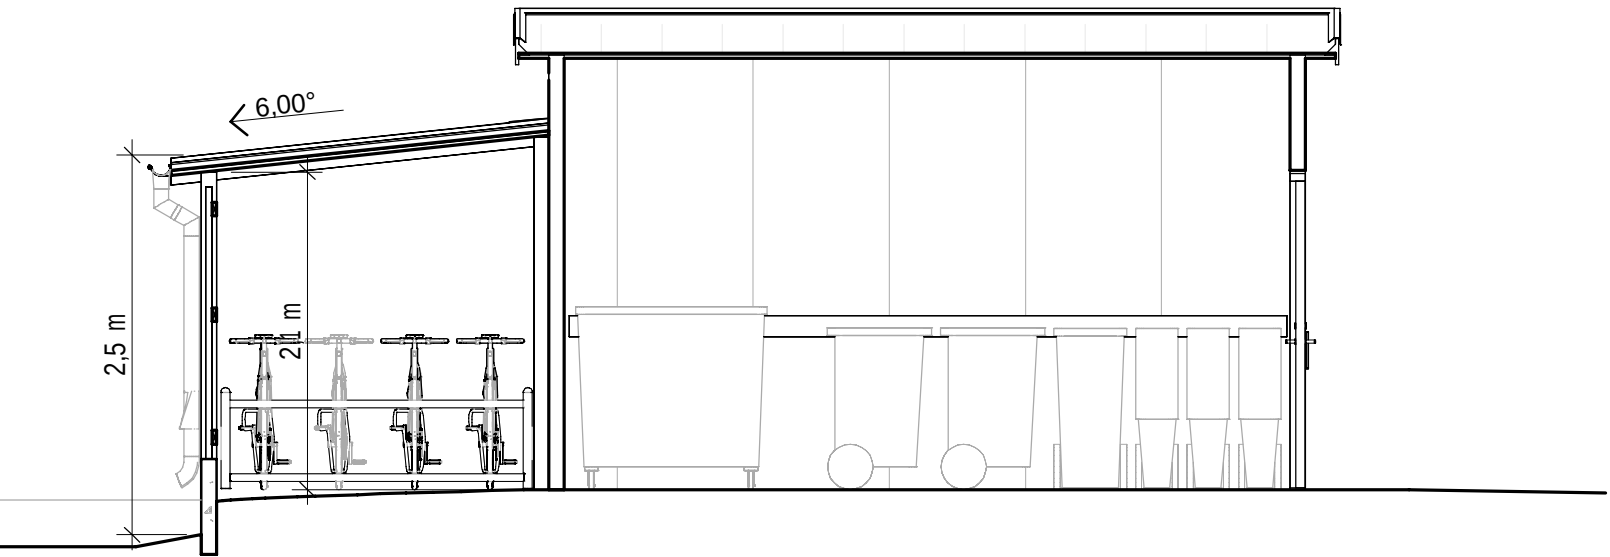

SEKTION 1

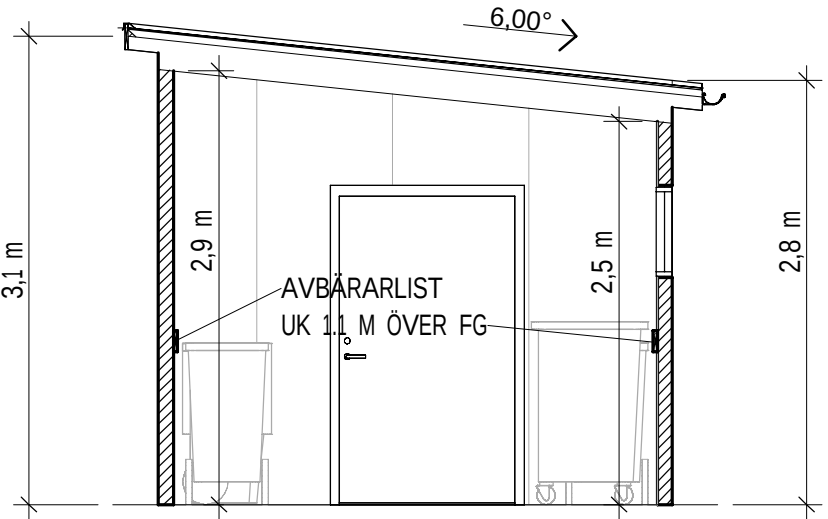

SEKTION 2

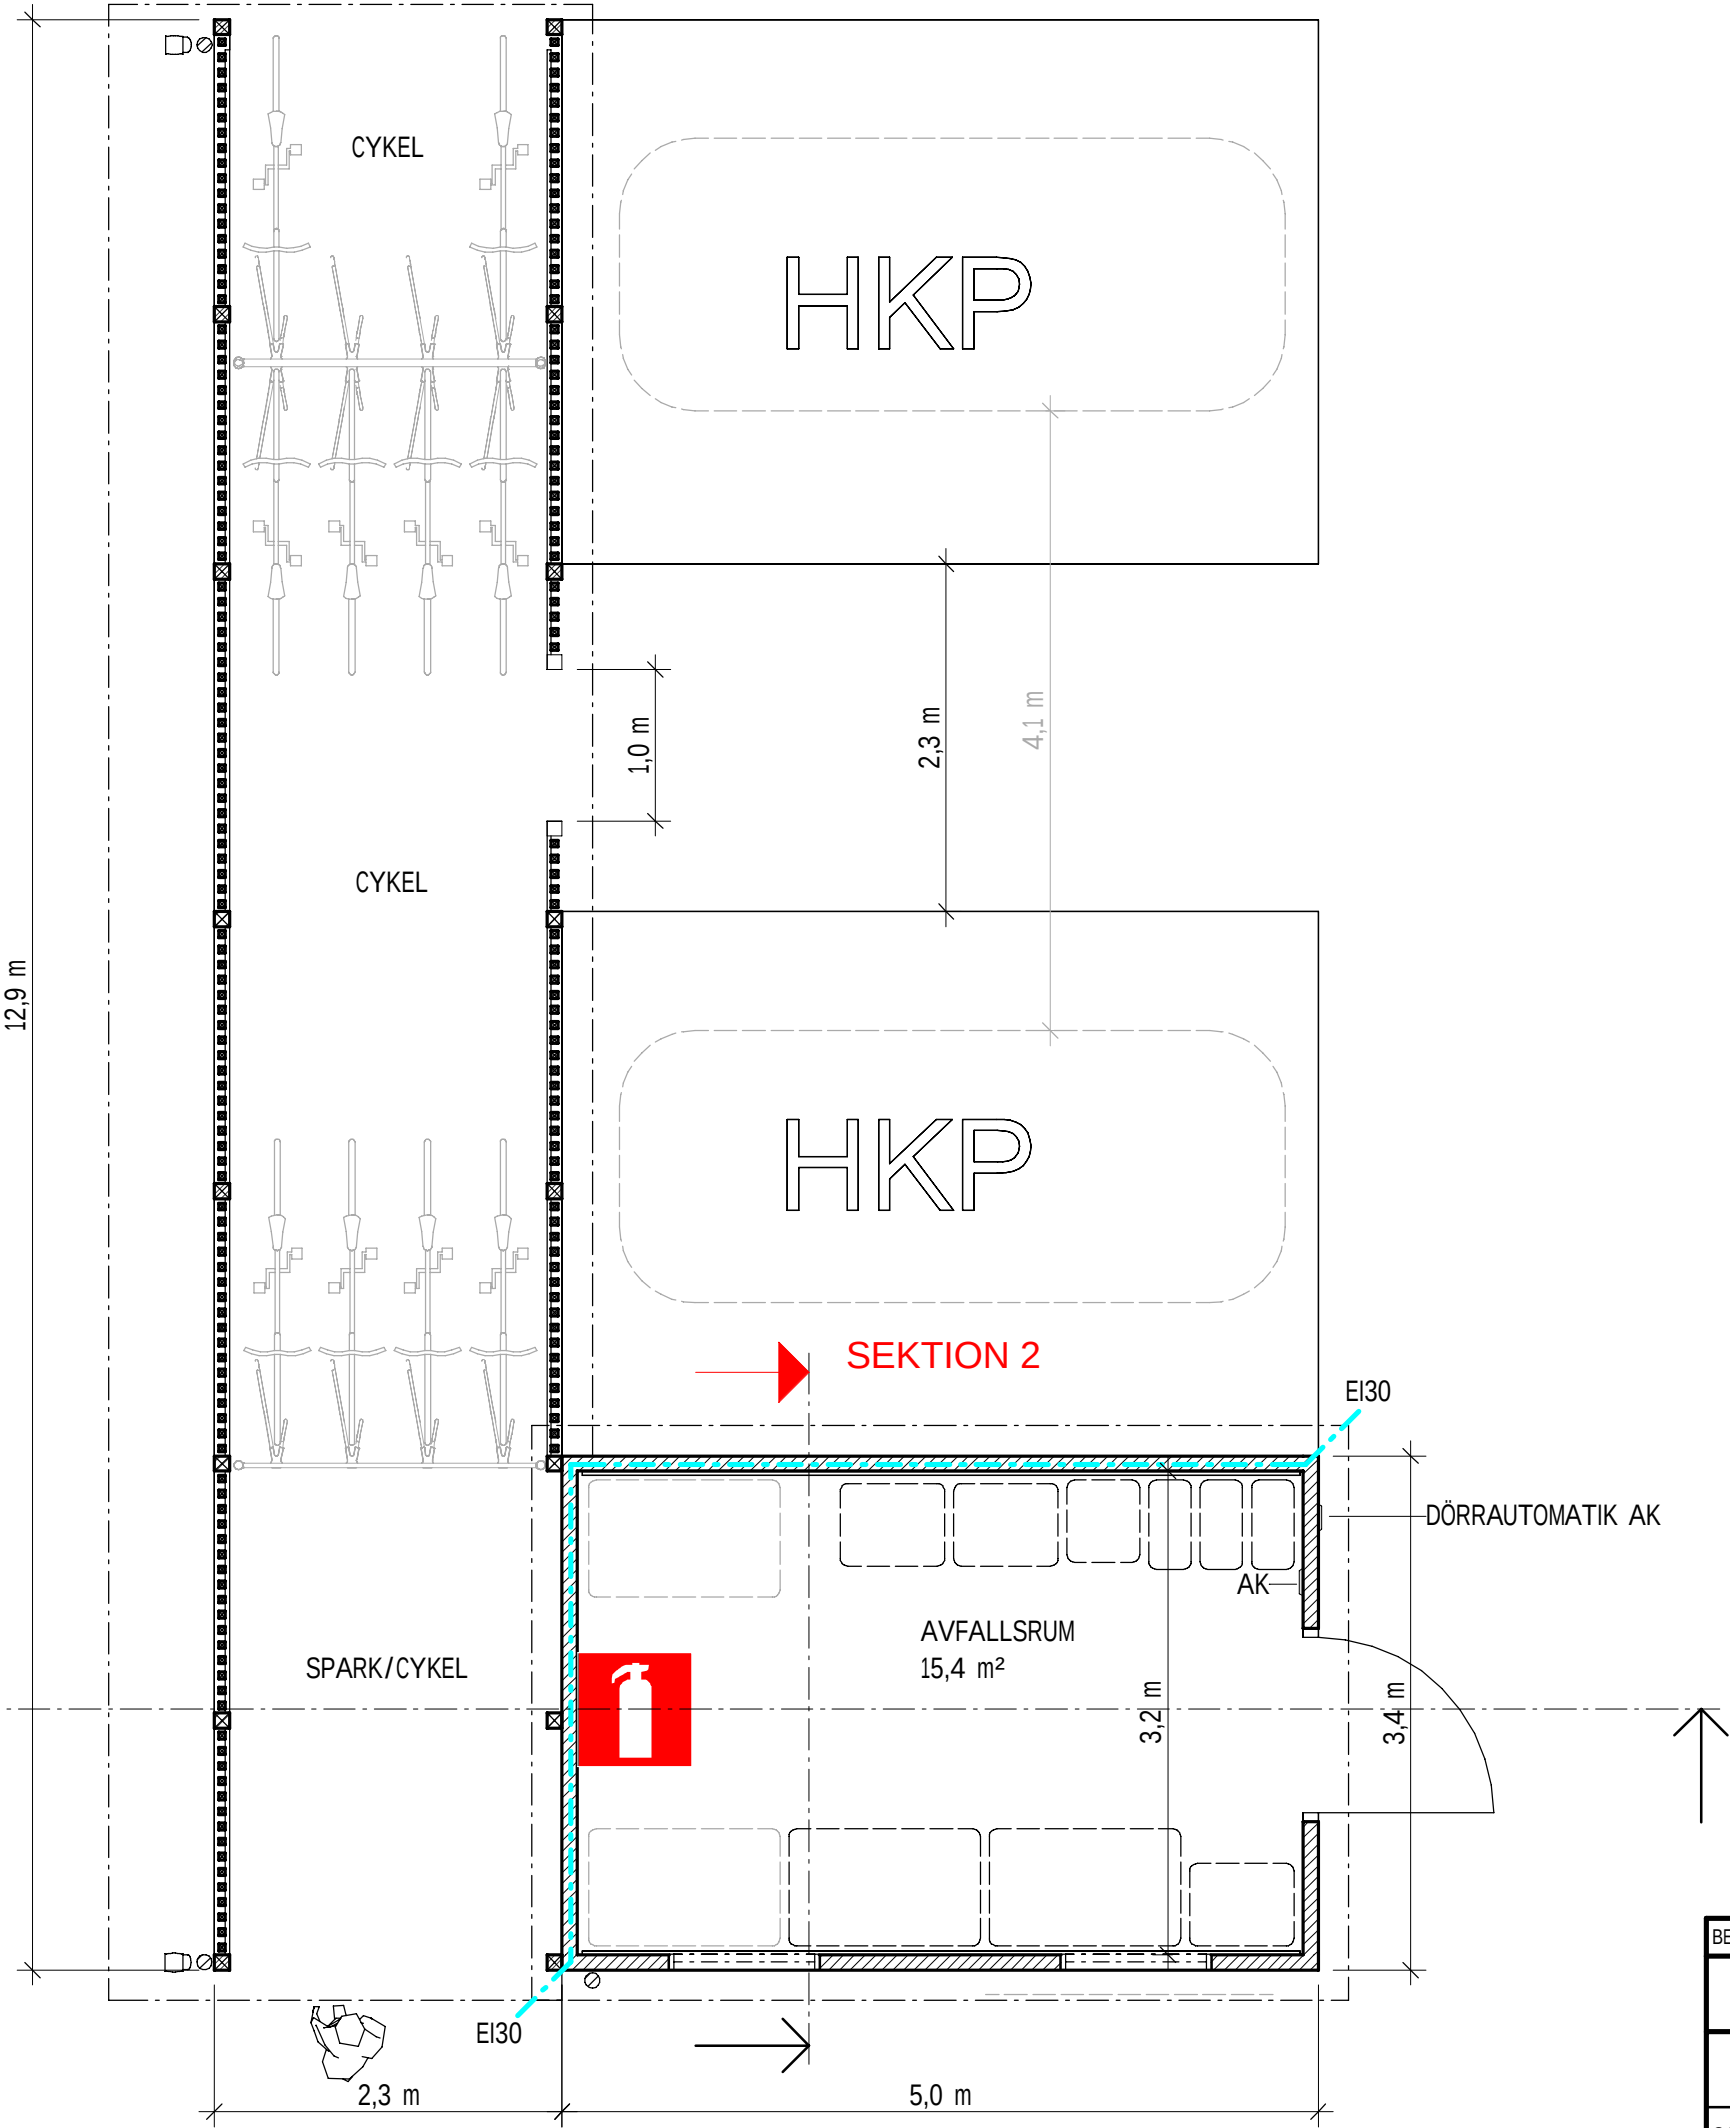

AVFALLSRUM - PLAN

SKALA 1:50
0 1 2 5
METER

BET	ÄNDRING	AVSER	DATUM	SIGN	STATUS
För granskning					
BYGGLOVSHANDLING					
2025-01-27	DATUM	J. SJÖGREN	KONTAKTPERSON	J. SJÖGREN	SKAPAD AV
CENTRUMHUSET HUS D					
KRÅKAN 1, ROBERTSFORS					
ANSVARIG PART					
AFRY AFRY Ark Studio					
J. SJÖGREN	GODKÄND AV	J. SJÖGREN	UPPERAGSNUMMER	210550	SKAPAD AV
RITNINGSKATEGORI					
OMBYGGNAD BIBLIOTEK OCH LÄGENHETER					
AVFALLSRUM					
FASADER, PLAN, SEKTION					
BL AVFALLSRUM					