


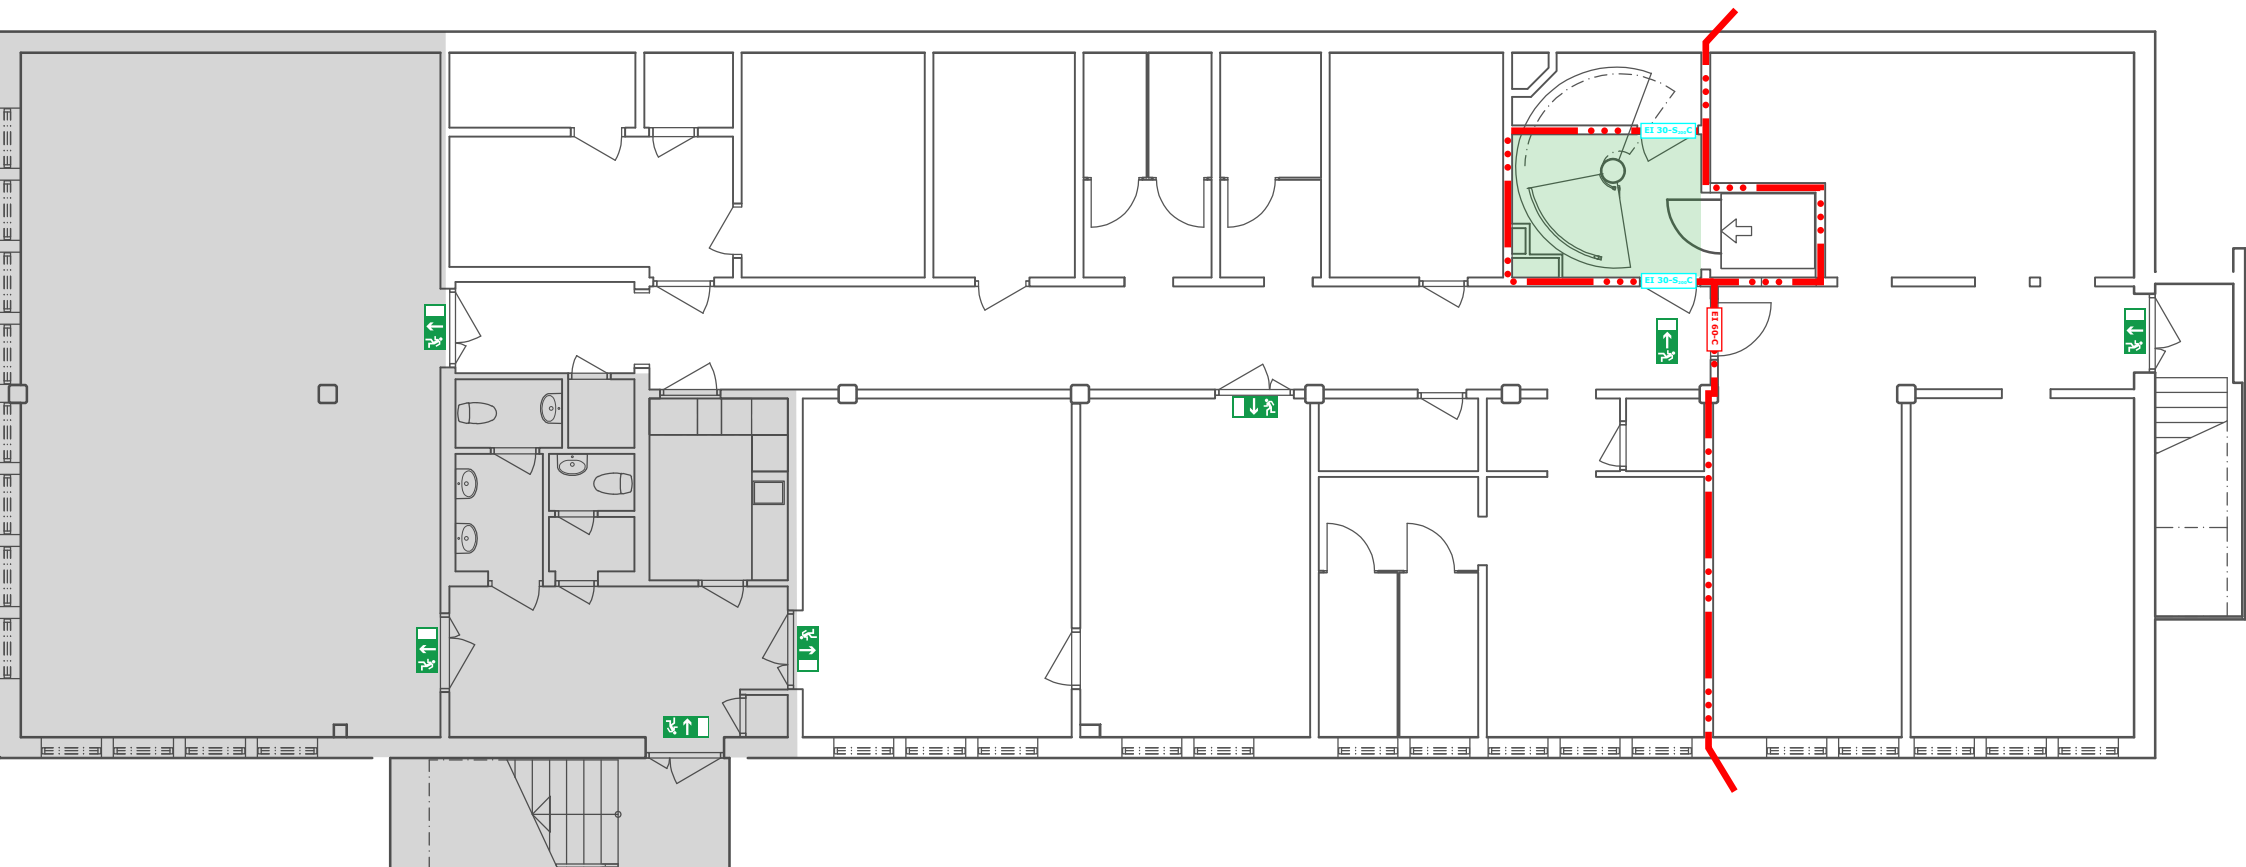

Brandskyddsskiss

Centrumhuset, Robertsfors

Upprättad av: AFRY, MA Safety

Datum: 2025-02-26

Uppdragsnummer: D0192413



Teckenförklaring Brandskiss

Brandcellgräns EI 60

EI 30-S...C



EI 60-C


Dörrklass EI 30-S200C

Område utgör utrymningsväg

Område berörs ej

Genomlyst vägledande markering

Dörrklass EI 60-C

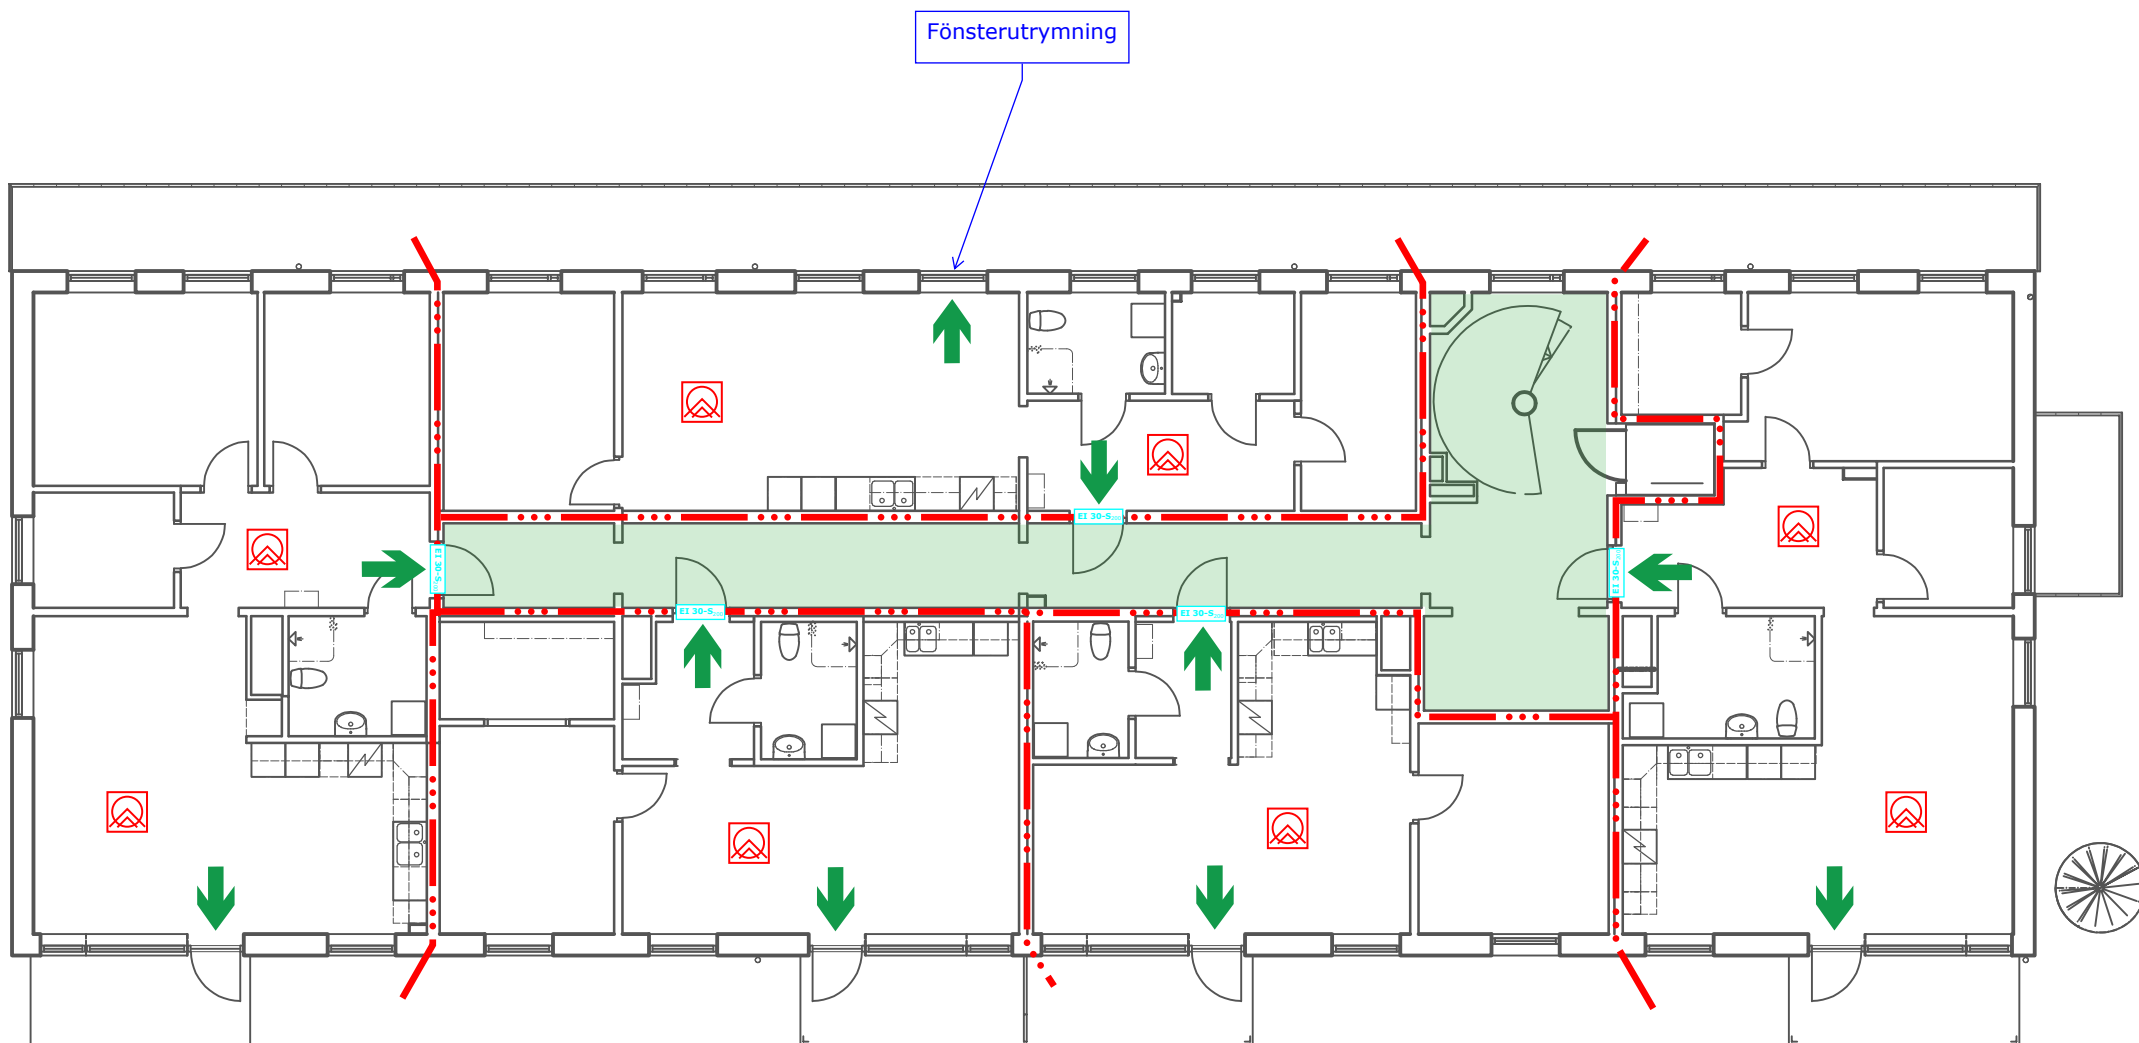


Brandskyddsskiss
Centrumhuset, Robertslors

Upprättad av: AFRY, MA Safety
Datum: 2025-02-26
Uppdragsnummer: D0192413

Teckenförklaring Brandskiss

	Brandcellsgräns EI 60
	Dörrklass EI 30-S200
	Område utgör utrymningsväg
	Utrymningsriktning
	Rökdetektor

AFRY
AF PÖRVY

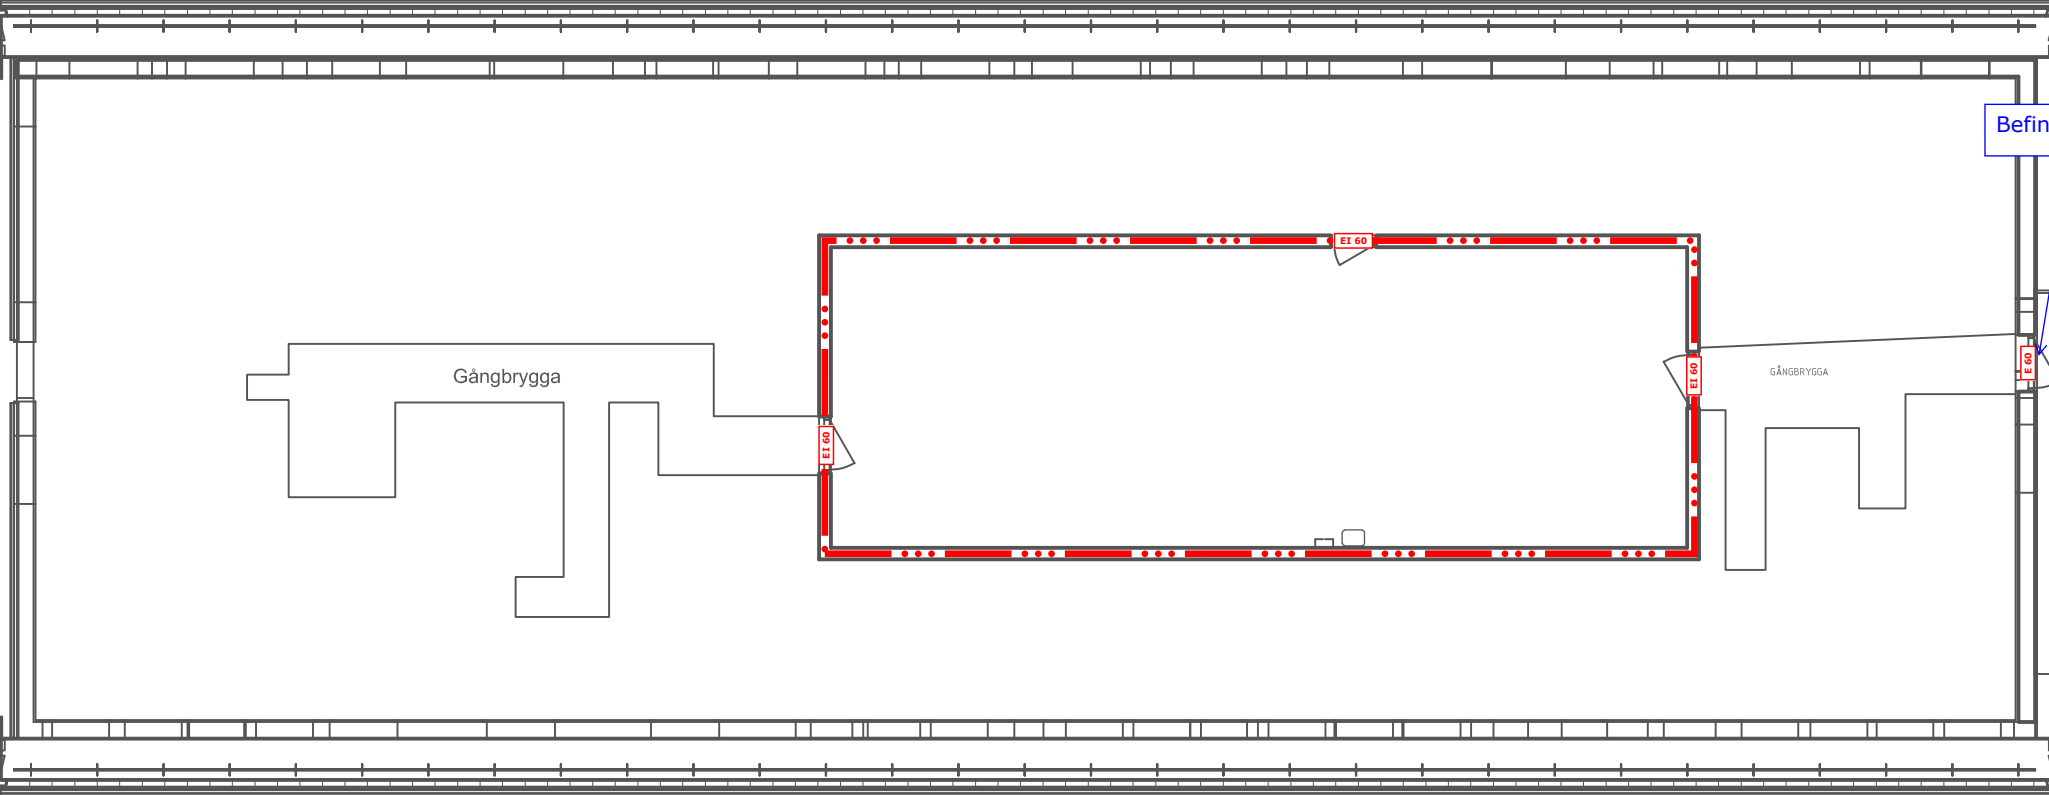

Brandskyddsskiss

Centrumhuset, Robertsfors

Upprättad av: AFRY, MA Safety

Datum: 2025-02-26

Uppdragsnummer: D0192413




Teckenförklaring Brandskiss


Brandcellsgräns EI 60

EI 60


Dörklass EI 60

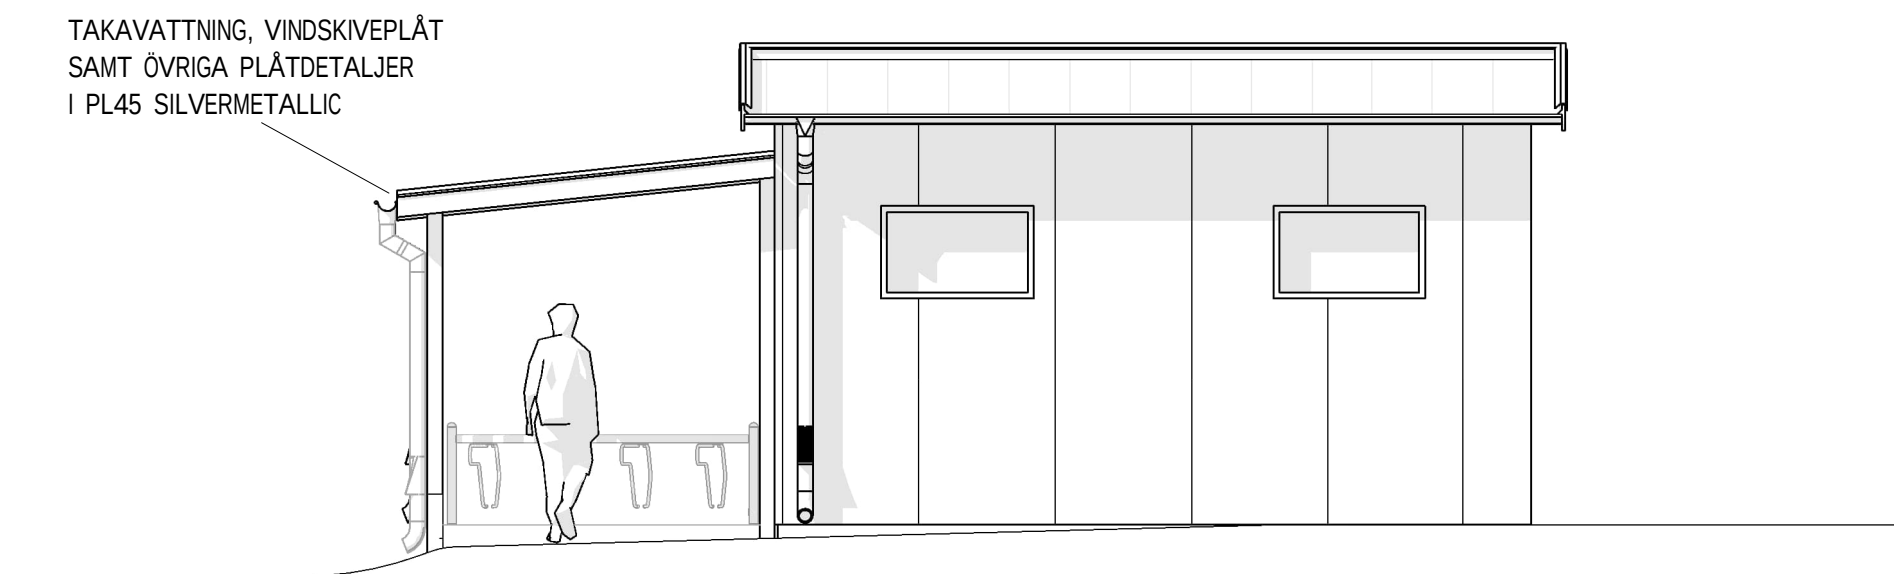


AVFALLSRUM - FASAD MOT SYDOST, ROSENIEGATAN

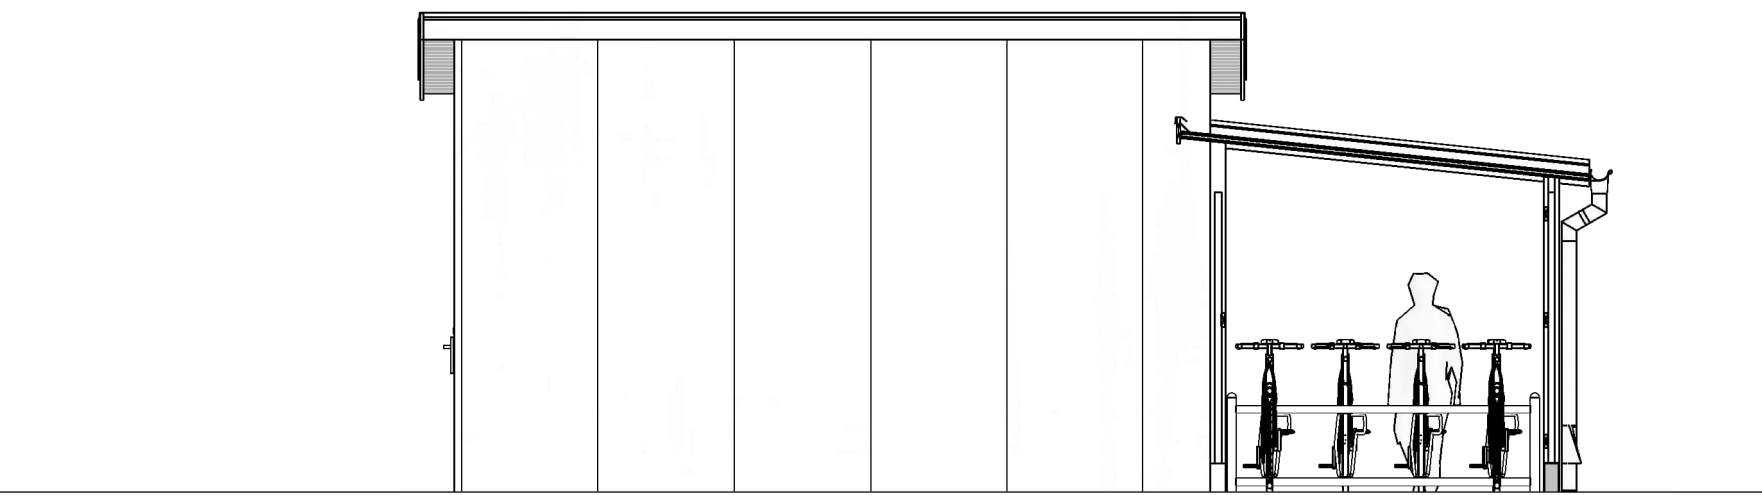


AVFALLSRUM - FASAD MOT NORDVÄST

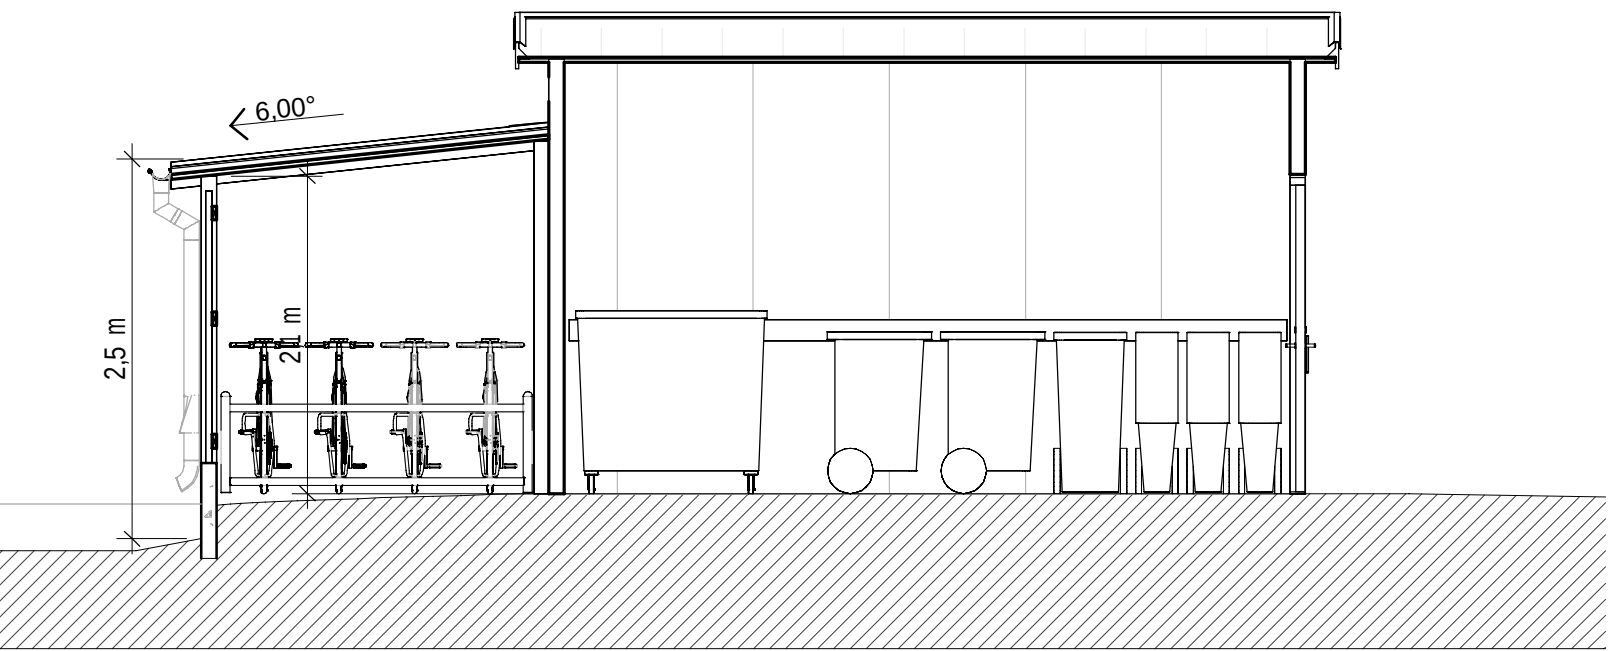

SEKTION 1

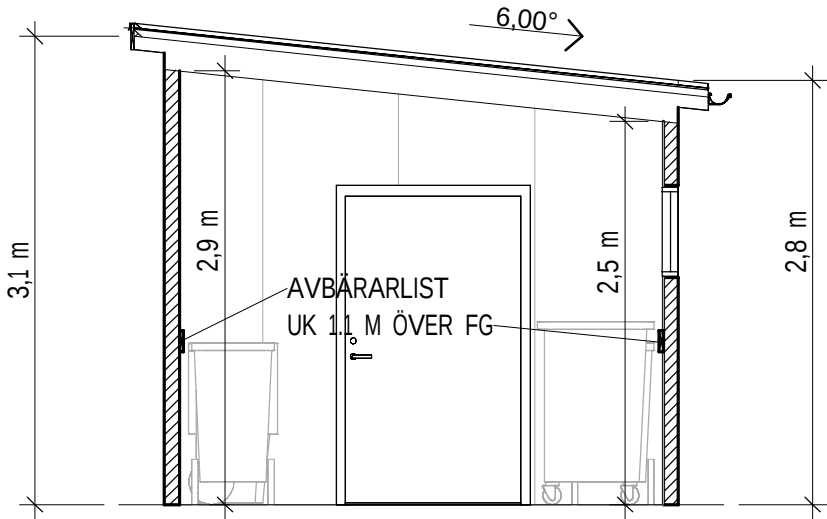

SEKTION 1

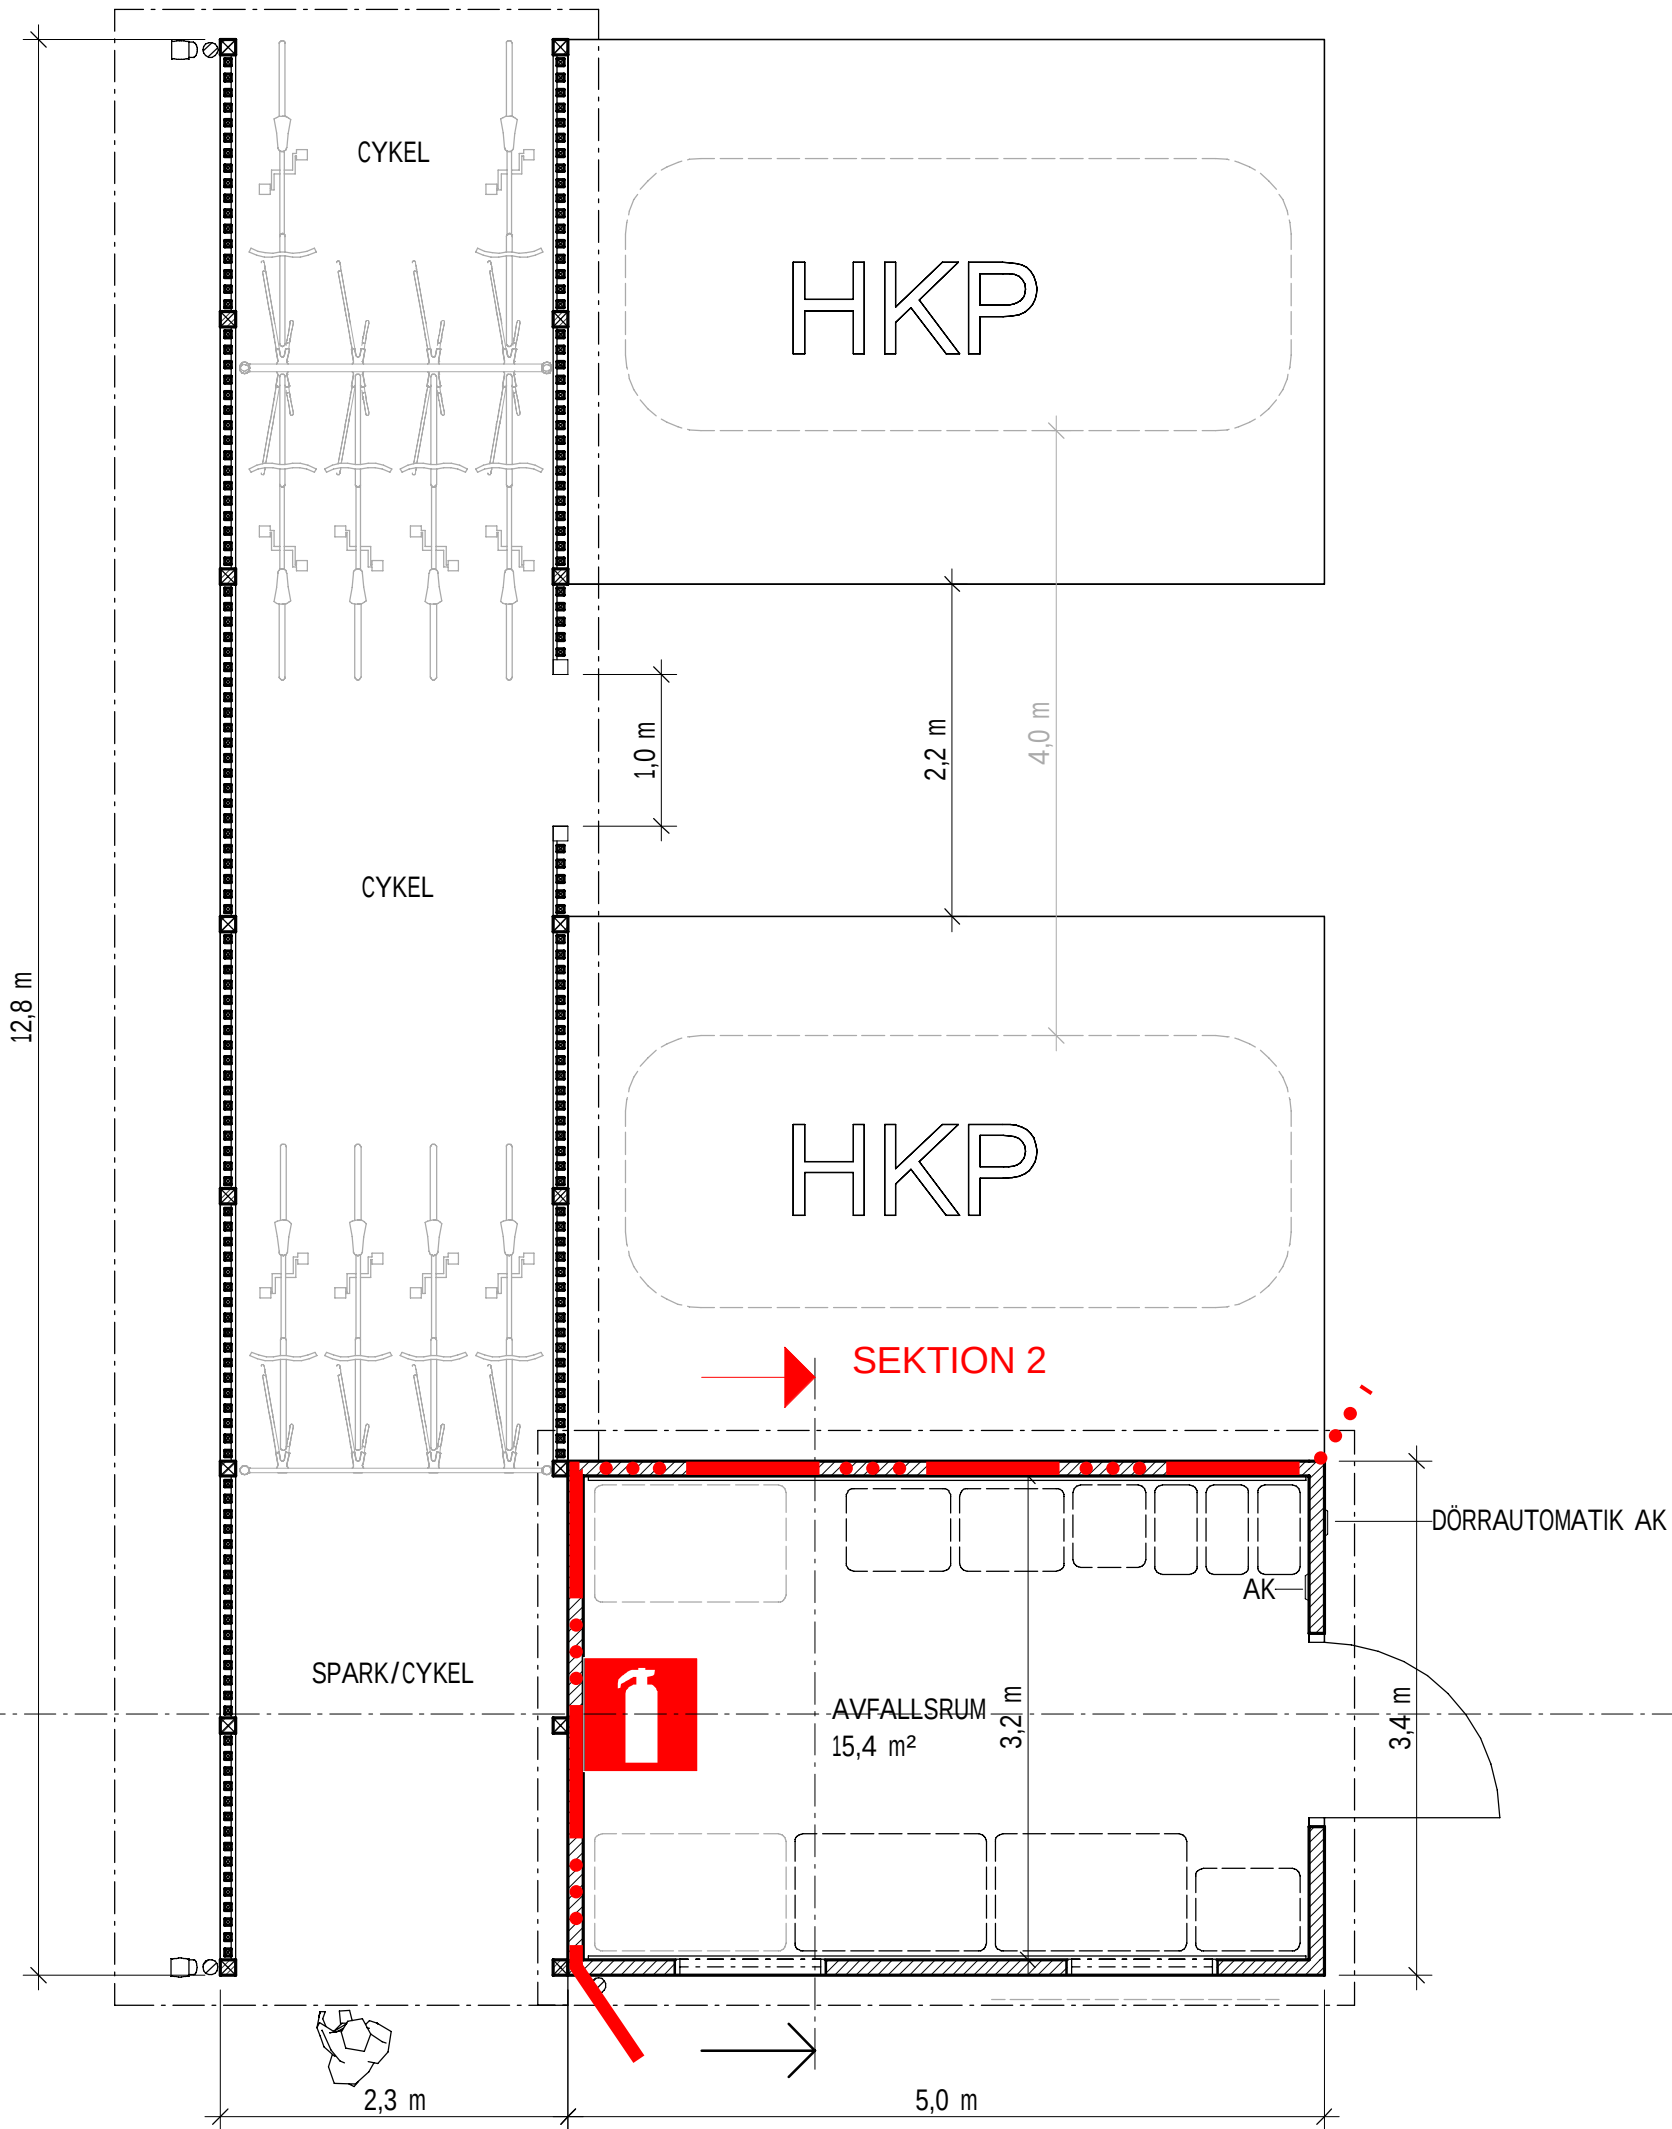

AVFALLSRUM - PLAN

Brandskyddsskiss Centrumhuset, Robertsfors			
Upprättad av: AFRY, MA Safety Datum: 2025-02-26 Uppdragsnummer: D0192413			
AFRY Ark Ark			
Teckenförklaring Brandskiss Brandcellsgräns EI 60			
SET	ÄNDRING AVSER	DATUM	SIGN
För granskning			
BYGGLOVSHANDLING			
DATUM	ÄNDRING	PROJEKT	ANSVARIG PART
2024-12-02			
CENTRUMHUSET HUS D KRÅKAN 1, ROBERTSFORS			
AFRY AFRY Ark Studio			
Handläggare	KONTAKTPERSON	J. Sjögren	SKAPAD AV
Checker	GODKÄND AV	210550	UPPRAGSNUMMER
OMBYGGNAD BIBLIOTEK OCH LÄGENHETER			RITNINGSKATEGORI
AVFALLSRUM			FORMAT
FASADER, PLAN, SEKTION			SKALA
A-40-3-2			1:50
			RETT