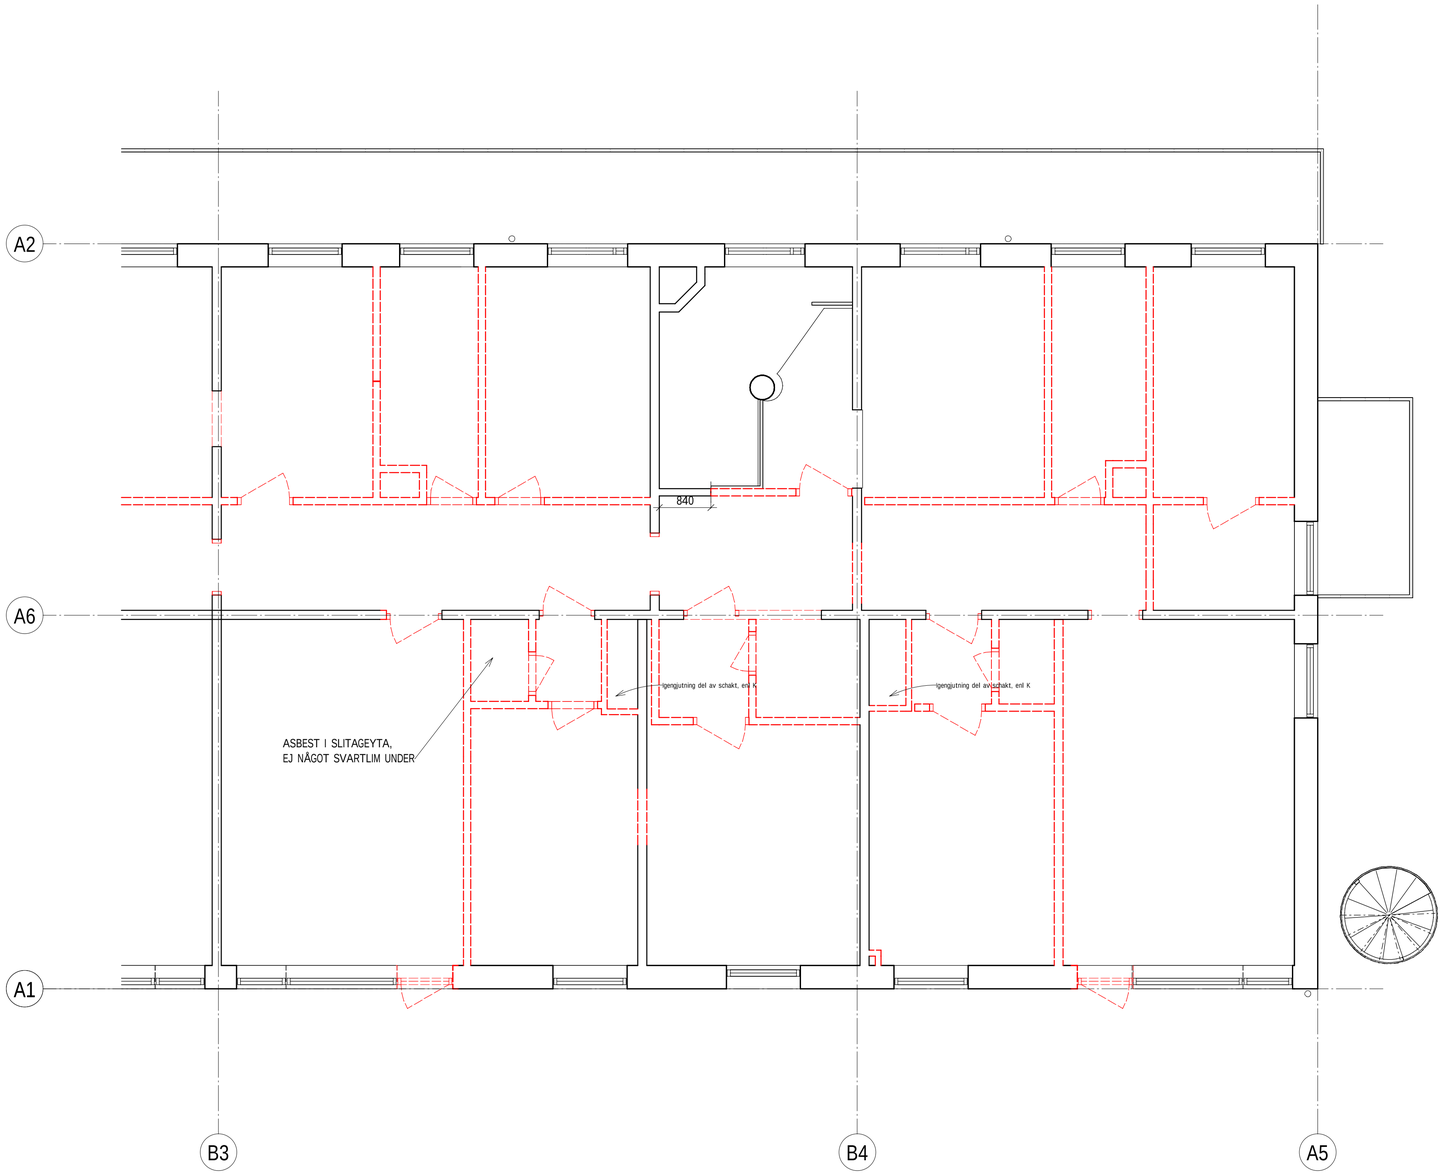


FÖRKLARINGAR

BEFINTLIGA BYGGDELAR

RIVNA BYGGDELAR

KONNEKTIONSLINJE

BRANDCELLSGRÄNSER:
EI15
E30
EI30
EI60

FÖRESKRIFTER

SANERING:
Sanering enl miljöinventering utförd av konsultera 22-12-2023

SKALA 1:50 0 1 2 5
METER

BET	ÄNDRING AVSER	DATUM	SIGN

STATUS: GRANSKNINGSHANDLING

HANDLING: BYGGHANDLING

DATUM: 2025-02-26

ÄNDRING:

PROJEKT:
CENTRUMHUSET HUS D
KRÅKAN 1, ROBERTSFORS

ANSVARIG PART:
AFRY
AFRY Ark Studio

KONTAKTPERSON	SKAPAD AV
J. Sjögren	L.Grubbström
GODKÄND AV	UPPDRAGSNUMMER
J. Sjögren	210550

RITNINGSKATEGORI:

INNEHÅLL	FORMAT
OMBYGGNAD BIBLIOTEK OCH LÄGENHETER	A1
RIVNING PLAN 200 - DEL 2	SKALA 1:50
NUMMER: A-49-1-D202	BET

Filen C:\Users\jind534\OneDrive - AFRY\Documents\A-40-V-01_ludviggrubbstrom.rvt