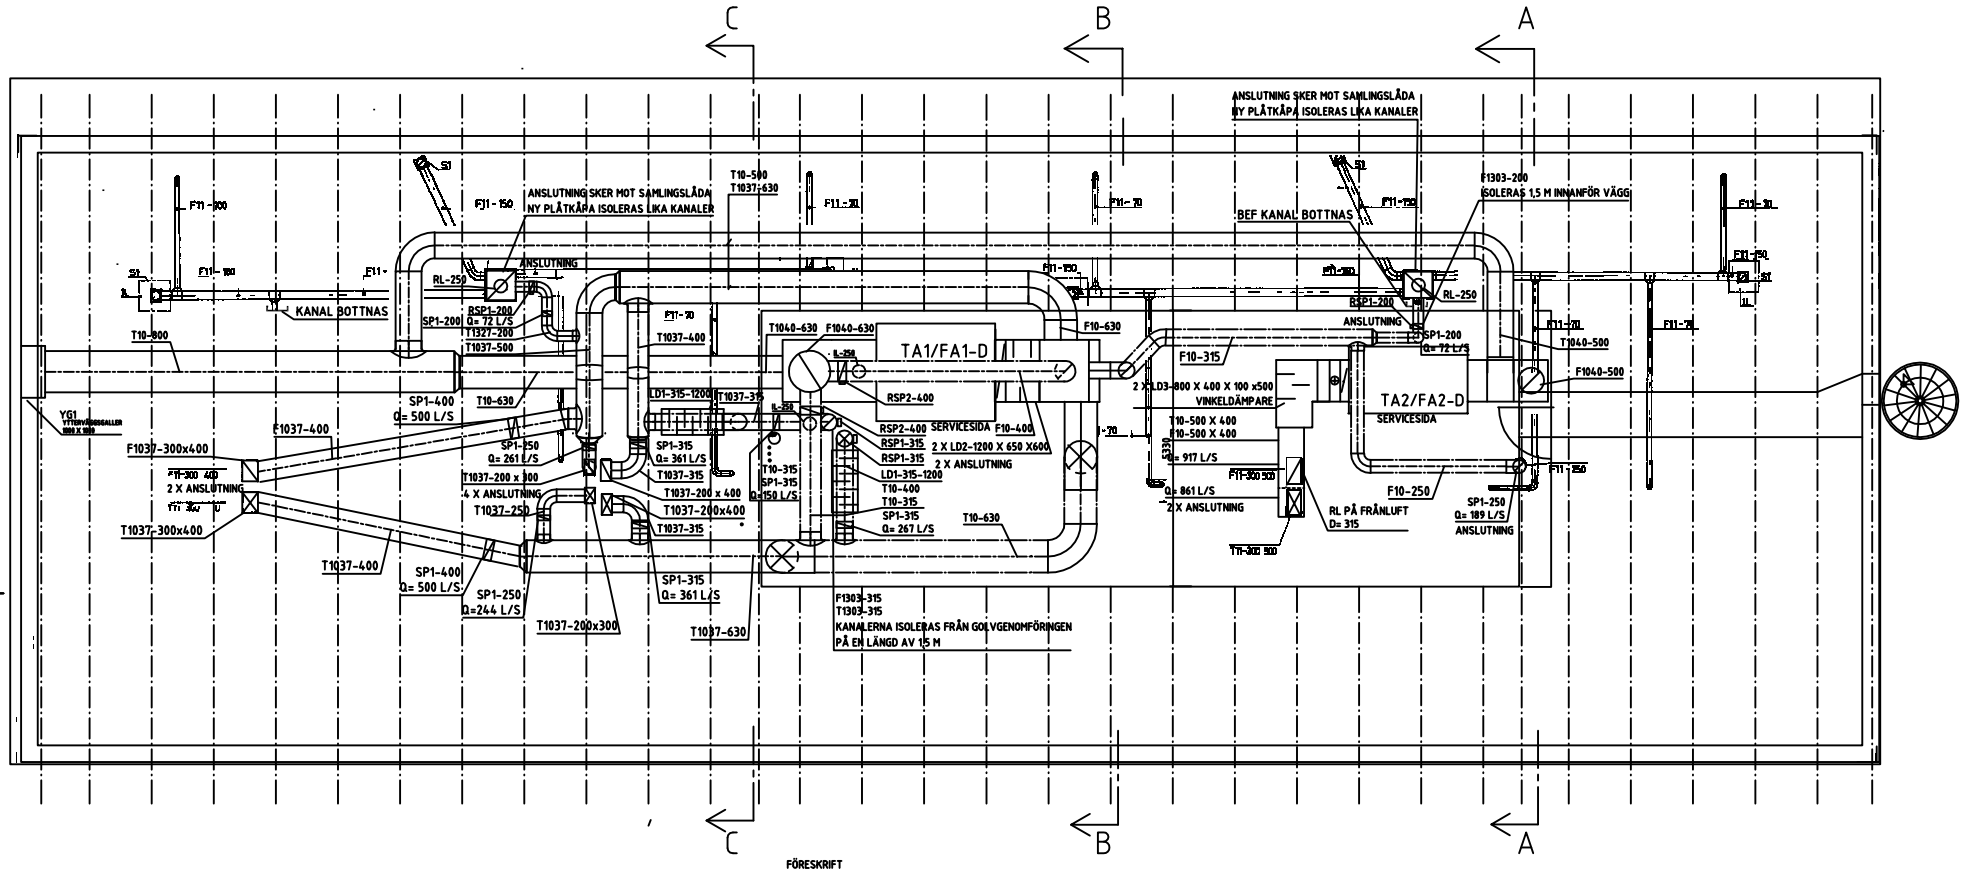


FÖRESKRIFT

REKTANGULÄRA KANALAVSNITT I ANSLUTNING TILL AGGREGATEN
ISOLERAS LIKA ANSLUTANDE KANALER.

LED 1 Funktion T = Tilluft F = Frånluft Ö = Överluft	LED 2 Kanaltyp 1 = Varmförz. stålplåt 2 = Kallvalsad stålplåt 3 = Rostfri Stålplåt 4 = Flexibel kanal	LED 3 Brandklass 0 = Utan brandklass 1 = Utv isol A15 2 = Utv isol A30 3 = Utv isol A60	LED 4 Isolering utöver brandisolering 0 = Oisolerad 1 = Utv isol 30 mm 2 = Utv isol 100 mm 3 = Utv isol 200 mm 4 = Utv isolerad Cellplast 13 mm. Diff tät.	LED 5 Ytskikt 0 = Utan ytskikt 1 = Nätmatta förz. stålplåt. 2 = Al-folie 3 = Al-folie + nät-matta 4 = Al-folie diff tät 5 = Plan Al-plåt 6 = Plastplåt 7 = Papp 8 = Diffusionstät plast

BET	ANT	ÄNDRINGEN AVSER	DATUM	SIGN

Förfrågningsunderlag

ROBERTSFORS KOMMUN
CENTRUMHUSET BYGGNAD D

ITN
Nydalavägen 6
903 38 Umeå
Tel 090-128830

UPPDRAG NR	RITAD/KONSTR AV	HANDLÄGGARE
02004	LEB	LEB
DATUM	ANSVARIG	
2002-05-12	LEB	

OMBYGGNAD VENTILATION
TAKPLAN
-
-

SKALA	NUMMER	BET
1:50	57:001	-

57:001.dwg

Xref C:\itn\0PROJEKT\0_02004C-husetRob\Ventritning\test\x_plan2.dwg