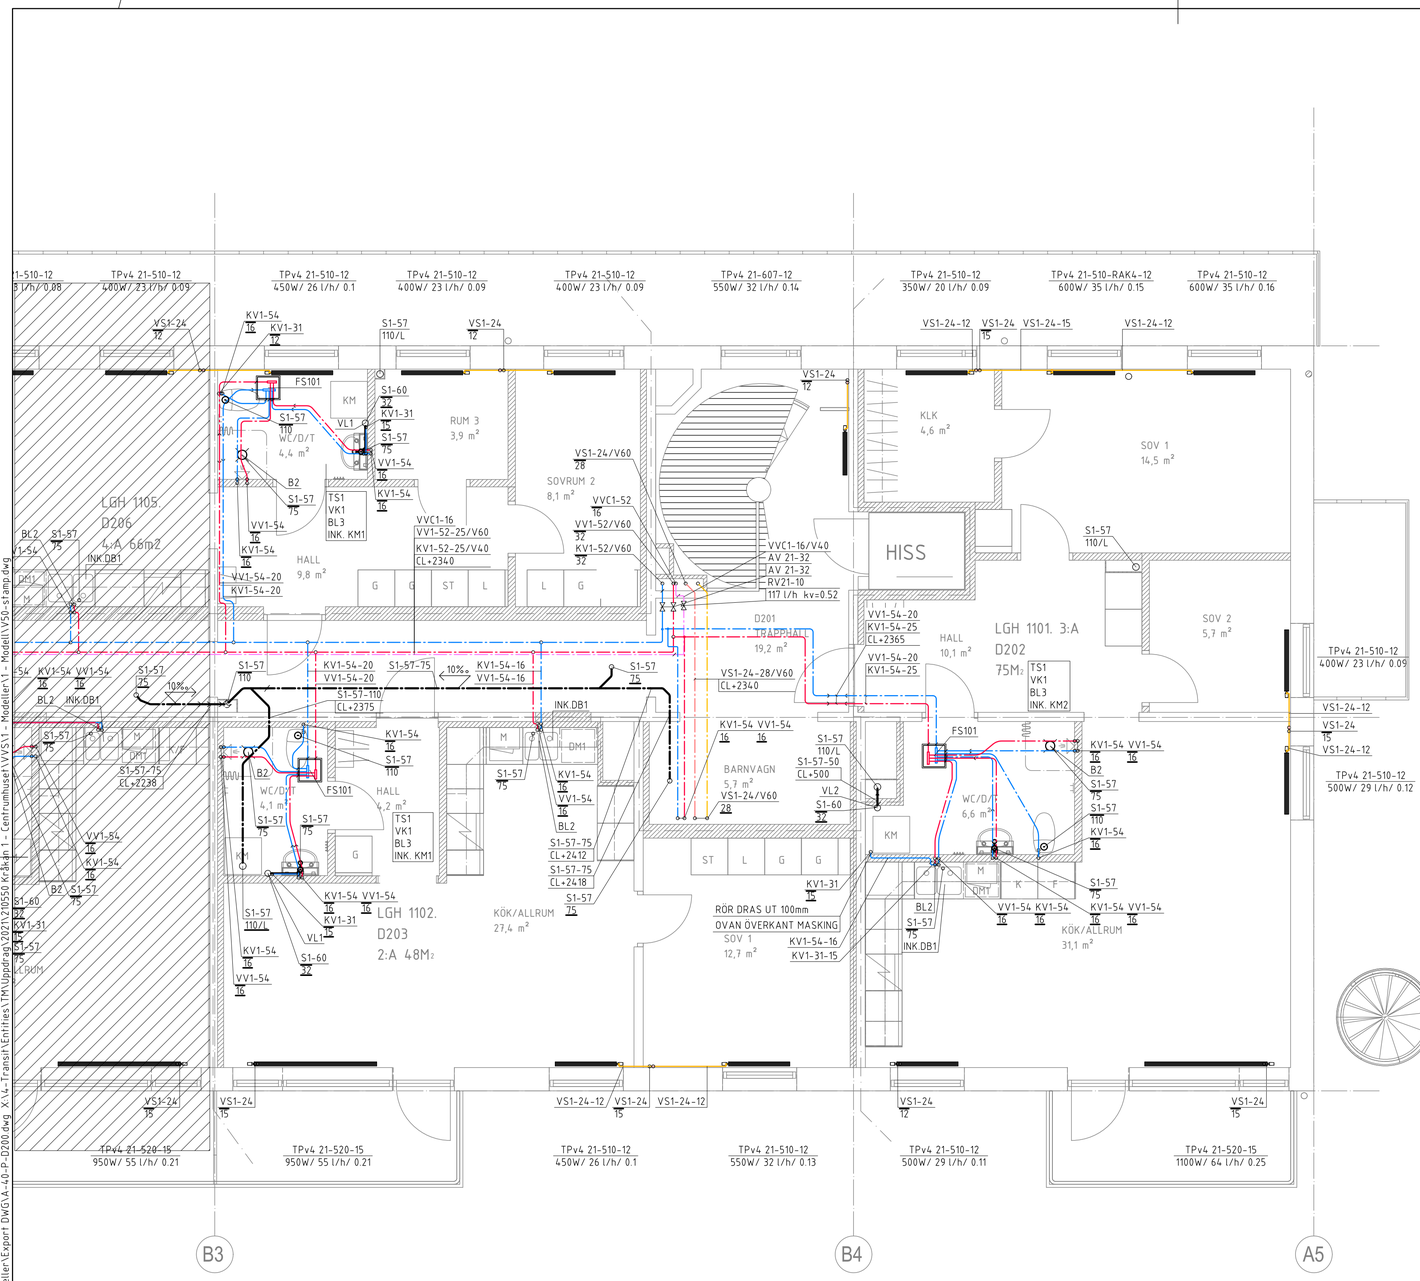


FÖRKLARINGAR

VS1-24-28/V60

SYSTEM

KV1	TAPPKALLVATTEN
VV1	TAPPVARMVATTEN
VVC1	VARMVATTENCIRKULATION
VP1	VÄRMESYSTEM, PRIMÄRSIDA
VS1	VÄRMESYSTEM, SEK. HUVUDSYSTEM
VS2	VÄRMESYSTEM, SEK. LUFTBEHANDLING
S1	SPILLVATTEN SANITÄRT

MATERIAL

12	PP-MARKAVLOPPSRÖR
24	ELFÖRZINKADE STÅLRÖR
30	KOPPARRÖR EN 1050-290
31	FÖRKROMADE KOPPARRÖR
51	PEM SLANG PN16
52	LK PAL UNIVERSALRÖR, A, RAKA LÄNGDER
54	LK PE-X UNIVERSALRÖR, RIR EXTRA EXTRAISOLERADE TOMRÖR
57	WAVIN ASTO PLUS
60	ABS RÖR

DIMENSION

DIMENSION PÅ PAL, PEX, KOPPARRÖR OCH ELFÖRZINKADE RÖR ANGES MED YTTERMÅTT I Dy I mm.

TERMISK ISOLERING

V40	VÄRMEISOLERING 40 MM (PAROC RÖRSKÅL).
V60	VÄRMEISOLERING 60 MM (PAROC RÖRSKÅL).

VVC SAMISOLERAS TILLSAMMANS MED VV.

LUFTLEDNINGAR FÖR SPILLVATTNET I KALLVINDEN ISOLERAS MED VÄRMEISOLERING 50 MM NÄTMATTA AV MINERALULL (V50).

YTBEKLÄDNAD
SYNLIGA ISOLERERADE LEDNINGAR YTBEKLÄDES TYP MÖNSTERPRÄGLAD ALUMINIUMPLÅT ELLER LIKVÄRDIGT.

TAPPVATTEN
SYNLIG LEDNINGSDRAGNING I RWC, WC, STÄD OCH KÖK UTFÖRES OISOLERAT OCH I FÖRKROMAT UTFÖRANDE.

TAPPVATTENRÖR DRAGNA FRÅN FS101 KLAMRAS MOT BJÄLKLAG TILL TAPPSTÄLL.

VID ÖVERGÅNG FRÅN STÅENDE TILL LIGGANDE AVLOPPSSTAM SKA ÖVERGÅNGEN UTFÖRAS MED 2x45° BÖJAR.

SAMTLIGA ÖPPNA RÖRÄNDAR TÄCKS MED LOCK.

HÖJDER PÅ VÄRME OCH TAPPVATTEN ANGES MED +HÖJD CENTRUM RÖR.

HÖJDER PÅ SPILLVATTENLEDNINGAR ANGES MED MED CL ÖFG.

ANSLUTNINGSLEDNINGAR DIM			
SAKVARA	KV DIM	VV DIM	S DIM
TVÄTTSTALL	12	12	75
TOALETTSTOL	12	–	110
UTSLAGSBACK	15	15	–
DISKLÄDSBL.	15	15	75
DUSCHBL.	15	15	–
GOLVBRUNN.	–	–	75

FÖRFRÅGNINGSUNDERLAG

STATUS

BYGGHANDLING

HANDLING

DATUM 2025-02-26 | ÄNDRING/PM

ÄNDRING

PROJEKT

CENTRUMHUSET HUS D
KRÅKAN 1, ROBERTSFORS

ANSVARIG PART

AFRY-Infrastructure AB
Storgatan 103
921 32 Lycksele
Tel: 010-505 00 00

AFRY

KONTAKTPERSON: Simon Rudin | SKAPAD AV: Alexander Östlund

GODKÄND AV: Simon Abrahamsson | UPPDRAGSNUMMER: D0182343 (210550)

RITNINGSKATEGORI

PLANRITNING

INNEHÅLL

OMBYGGNAD BIBLIOTEK OCH LÄGENHETER
PLAN 1 TR - PLAN 20 - DEL 2
VS - INSTALLATIONER

FORMAT A1

SKALA 1:50

NUMMER V-50-1-D202

BET

X:\4-Transit\Entities\TM\Uppdrag\2021\210550 Kråkan 1 - Centrumhuset\VVS\1 - Modeller\1 - Modell\VS0-stamp.dwg
X:\4-Transit\Entities\TM\Uppdrag\2021\210550 Kråkan 1 - Centrumhuset\A\1 - Modeller\Export DWG\A-40-P-D200.dwg

LAGER: SB11