

PLANBESTÄMMELSER

Följande gäller inom områden med nedanstående beteckningar. Endast angiven användning och utformning är tillåten. Där beteckning saknas gäller bestämmelsen inom hela planområdet.

GRÄNSBETECKNINGAR

- Planområdesgräns
- Användningsgräns
- Egenskapsgräns

ANVÄNDNING AV MARK OCH VATTEN

Allmän plats. 4 kap. 5 § 1 st 2 p.

- GATA
- Gata
- Kvartersmark. 4 kap. 5 § 1 st 3 p.
- B
- Bostäder
- E
- Teknisk anläggning - Transformatorstation
- S
- Förskolegård

EGENSKAPSBESTÄMMELSER FÖR

KVARTERSMARK

Bebyggandets omfattning

- e₁ Största byggnadsarea är 50 m². 4 kap. 11 § 1 st 1 p.
- e₂ Största bruttoarea är 2150 m² per byggnad, inklusive inglasade balkonger och 1920 m² exklusive inglasade balkonger. 4 kap. 11 § 1 st 1 p.
- e₃ Största bruttoarea är 1970 m² per byggnad, inklusive inglasade balkonger och 1780 m² exklusive inglasade balkonger. 4 kap. 11 § 1 st 1 p.
- e₄ Största byggnadsarea är 70 m² per enskild byggnad, största totala byggnadsarea är 150 m². 4 kap. 11 § 1 st 1 p.

- Marken får inte föras med byggnad. 4 kap. 11 § 1 st 1 p.
- Endast komplementbyggnad får placeras. 4 kap. 11 § 1 st 1 p.

- Minsta takvinkel i grader. 4 kap. 11 § 1 st 1 p.

Utformning

- f₁ Fasad ska utformas i puts utan synliga elementskarvar. Sockelväning ska vara tydligt markerad, genom att utföras med avvikande fasadmateriäl, i enlighet med planbeskrivning, sidan 39. 4 kap. 16 § 1 st 1 p.
- f₂ Balkong får skjuta ut högst 2,2 meter från fasad. Balkong som krägar ut över kvartersmark ska ha en fri höjd om minst 2,5 meter ovan underliggande mark. Balkonger får utgöra max. 35% av fasadernas sammanlagda längd. 4 kap. 16 § 1 st 1 p.
- f₃ Balkong får skjuta ut högst 2,2 meter från fasad. Balkong som krägar ut över innergård ska ha en fri höjd om minst 2,5 meter ovan underliggande mark. Balkonger får utgöra max. 35% av fasadernas sammanlagda längd. 4 kap. 16 § 1 st 1 p.

Entréer till trapphus, cykelrum och miljöstuga ska vara tydligt markerade och utformas med uppglasade partier. 4 kap. 16 § 1 st 1 p.

- Högsta totalhöjd i meter över angivet nolplan. 4 kap. 16 § 1 st 1 p.

- Högsta byggnadshöjd i meter. 4 kap. 16 § 1 st 1 p.

Utförande

- b₁ Marken får inte hårdgräsa. 4 kap. 16 § 1 st 1 p.
- b₂ Dagvatten ska avledas till dagvattenfördröjande anläggning inom fastigheten, med lämplig lagringsvolym specifikt beräknad utifrån takytornas storlek. 4 kap. 16 § 1 st 1 p.
- b₃ Fastläggning av föröreningar från parkering ska ske i infiltrationsyta. 4 kap. 16 § 1 st 1 p.
- b₄ Dagvatten ska avledas till dagvattenfördröjande anläggning inom fastigheten, med lämplig lagringsvolym specifikt beräknad utifrån den hårdgjorda ytans storlek. 4 kap. 16 § 1 st 1 p.
- b₅ Byggnads fasad ska utformas så att Folkhälsomyndighetens allmänna råd (2014:13) för lågfrekvent buller från bussar på tomgång inte överskrider inomhus i bostadsrum. 4 kap. 16 § 1 st 1 p.

Markens anordnande och vegetation

- n₁ Trädet får inte fallas. Om trädet fallis ska återplantering ske med samma art och stammen ska tas om hand för att gynna fauna i enlighet med planbeskrivning, sidan 18. 4 kap. 10 §
- n₂ Marken ska föras med växtlighet och vara nedsänkt gentemot omgivande ytor i enlighet med planbeskrivning, sidan 18. 4 kap. 10 §
- n₃ Marken ska föras med växtlighet i enlighet med planbeskrivning, sidan 18. 4 kap. 10 §
- n₄ Marken ska föras med växtlighet och vara nedsänkt gentemot parkering i enlighet med planbeskrivning, sidan 18. 4 kap. 10 §

Stängsel och utfart

- Utfartsförbud. 4 kap. 9 §

ADMINISTRATIVA BESTÄMMELSER

Huvudmannaskap

Huvudmannaskapet är kommunalt för allmän plats. 4 kap. 7 §

Genomförandetid

Genomförandetiden är 10 år för kvartersmark och allmän plats. 4 kap. 21 §

Ändrad lovplikt

Marklov krävs även för fällning av med n1 markerade träd. Marklov för trädffällning får endast ges om trädet utgör risk att skada människor eller egendom. 4 kap. 15 § 1 st 3 p.

Marklov krävs även för schaktning, fyllning och sprängning som påverkar tomtens höjdläge med mer än 0,5 meter. Stödmurar högre än 0,5 meter ska terraseras eller släntas mot omgivande mark. Stödmur i fastighetsgräns är inte tillåtet. Vid ändring av marknivå ska marken ansluta foljsamt mot omgivande fastigheter. Vid marklov skall hänsyn tas till dagvattenhantering och naturvården. 4 kap. 15 § 1 st 3 p.

Övrigt

Dagvatten ska omhändertats lokalt (LOD) på egen fastighet i enlighet med planbeskrivning, sidan 32. 4 kap. §

ILLUSTRATION

- Illustrationslinje
- Illustrationstext

Teckenförklaring

- Traktgräns
- Fastighetsgräns
- Bostadshus
- Övrig byggnad
- Väg
- Stiget
- Staket
- Stödmur
- Häck
- Dike
- Nivåkurvor

- Fastighetsbeteckning
- Koordinatangivelse


- Berg i dagen
- Barrskog
- Brunnslock
- Flaggstång
- Belysningsstolpe

Kartbeteckningar enligt HMK-KA 2.2.6.1
Koordinat- och projektionssystem:
SWEREF 99 18 00
Höjdsystem RH 2000


Ledningar från ledningskollen ej redovisade
Detaljinformation, datum för inmätning/fältkontroll:
2021-09-06 av Värmdö kommun
Fastighetsinformation och aktualitetsdatum
i fastighetsregister: 2021-09-02
Grundkartan senast reviderad:
2021-09-06

Grundkartan upprättad av:
Metria AB, Katrineholm
katrineholm@metria.se
Telefon: 010-121 87 80

Skala 1:1000

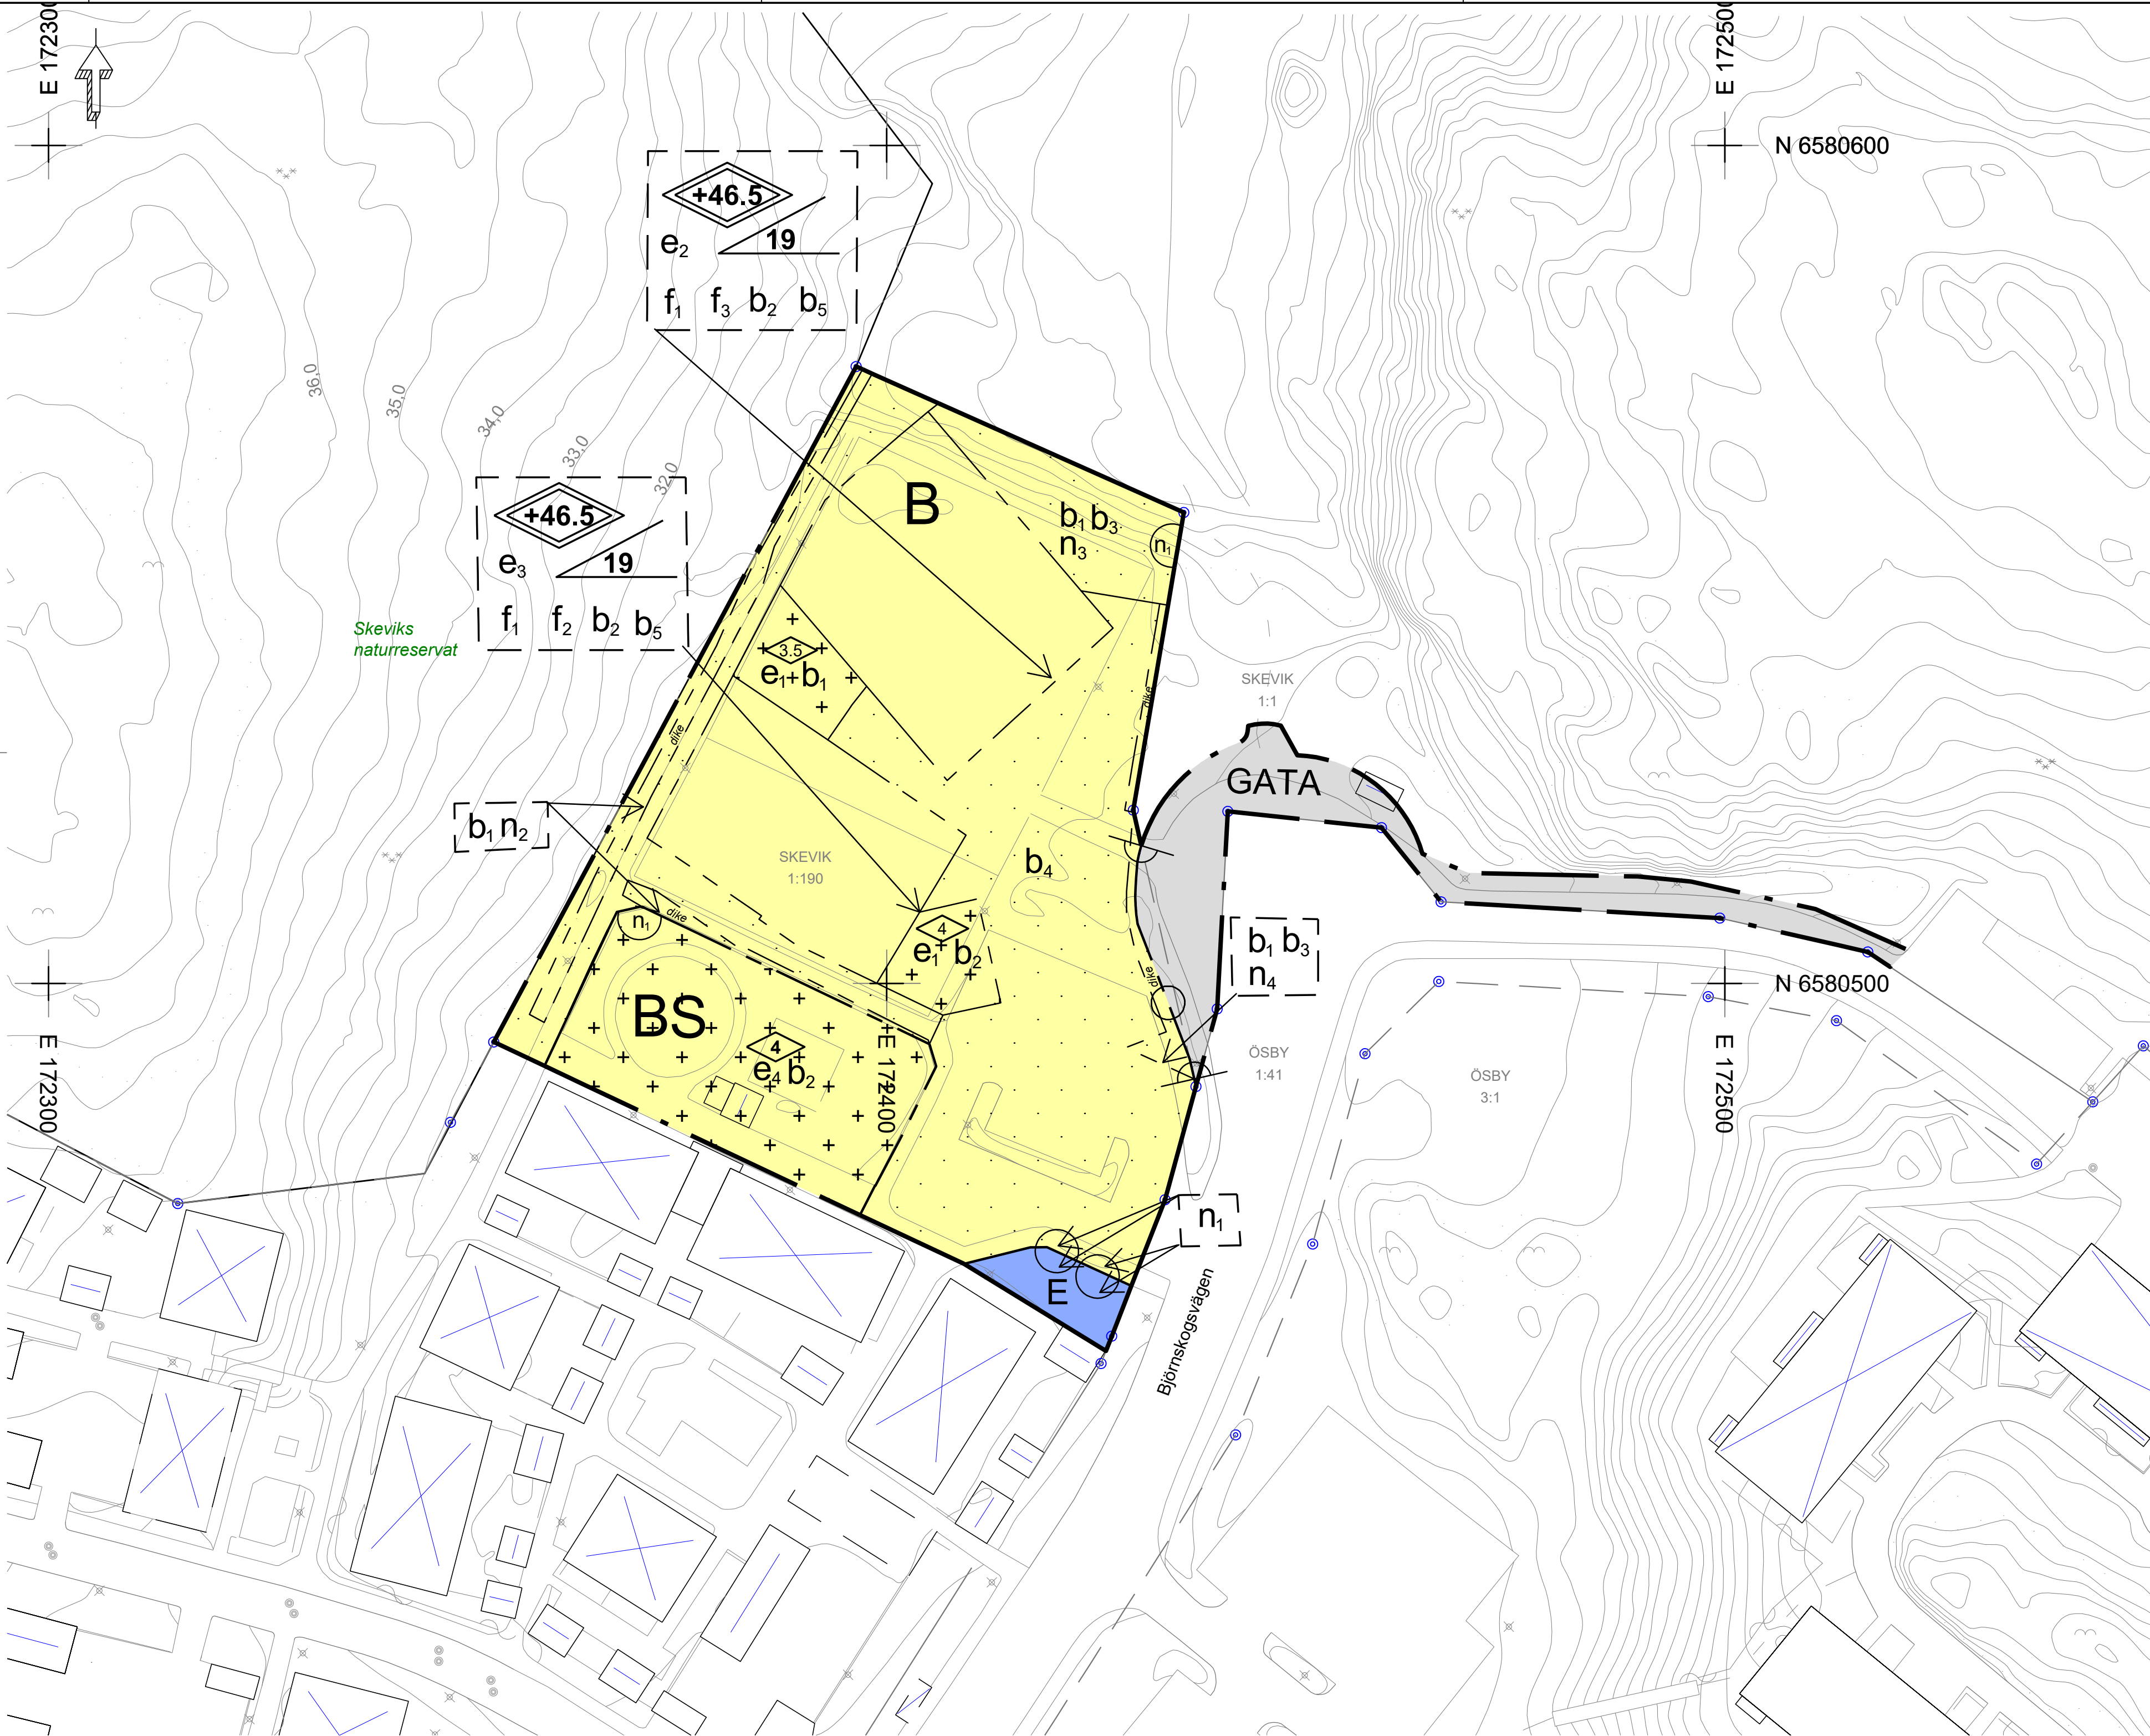

Översiktskarta

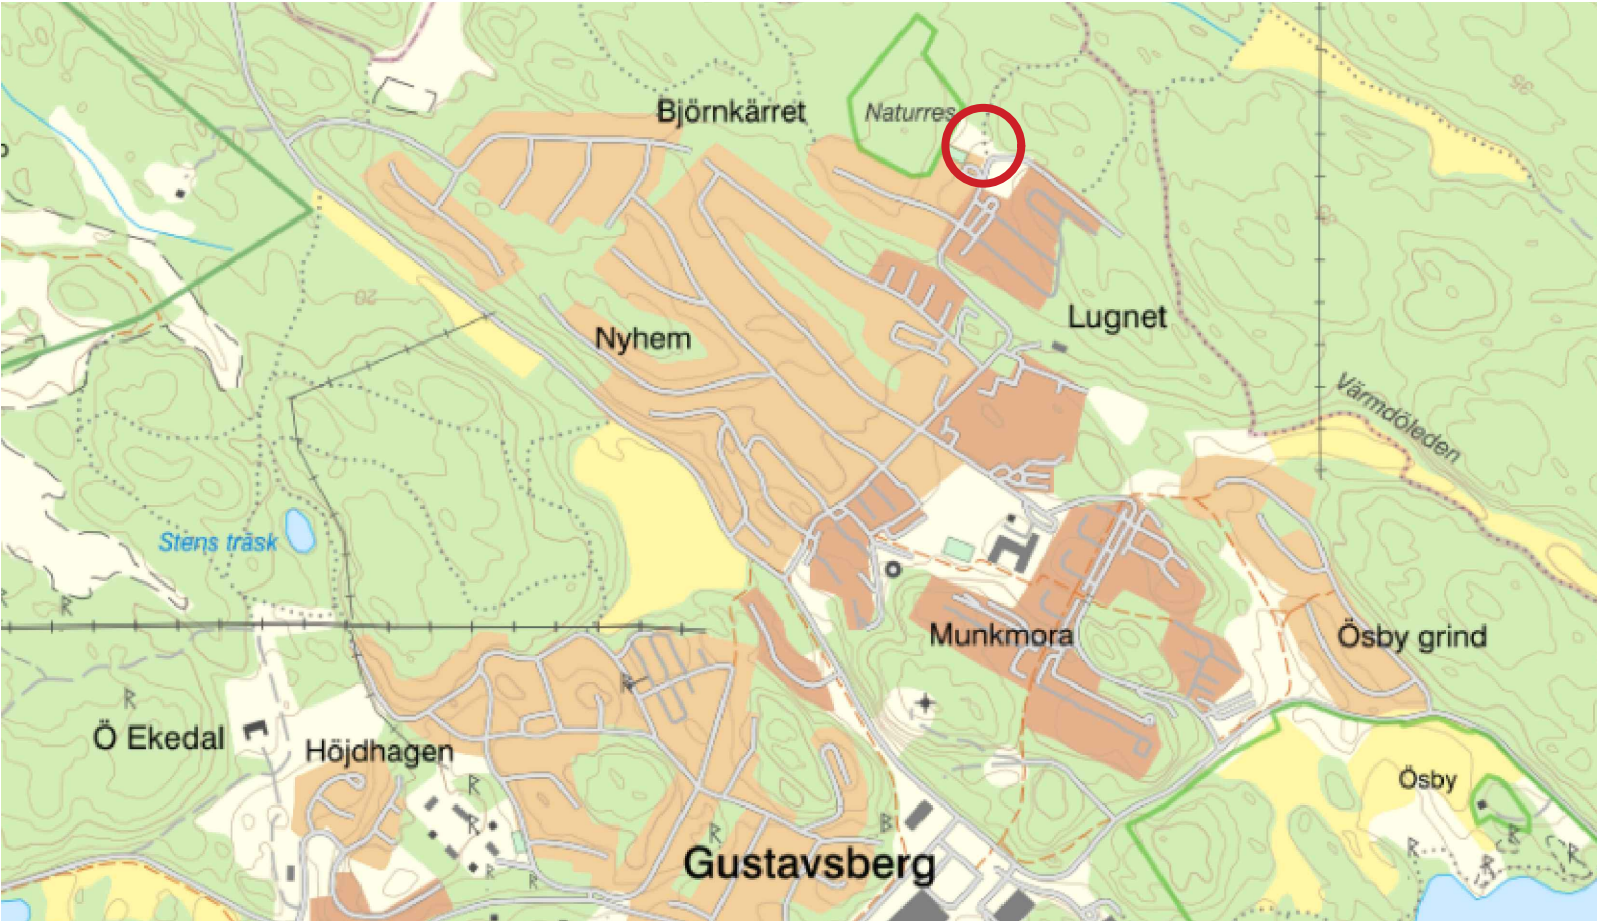

Till planen hör: ☐ Planprogram ☐ Samrådsredogörelse program ☐ Samrådsredogörelse		☒ Planbeskrivning ☐ Miljökonsekvensbeskrivning ☒ Fastighetsförteckning ☐ Samrådsredogörelse	☒ Granskningsutlåtande ☒ Geskäftsprogram ☐ Kvalitetsprogram ☐ Illustration
Detaljplan för Skevik 1:190 och del av Skevik 1:1			
VÄRMDÖ KOMMUN		Stockholms Län	Beslutsdatum
Antagandehandling			Godkännande
Upprättad i enlighet med PBL 2010:900		2021-11-10	KF
Upprättad 2021-09-20		Reviderad	2021-12-16
Raad Alwajid planchef		Anna Fredriksson planarkitekt/projektledare	DP245