


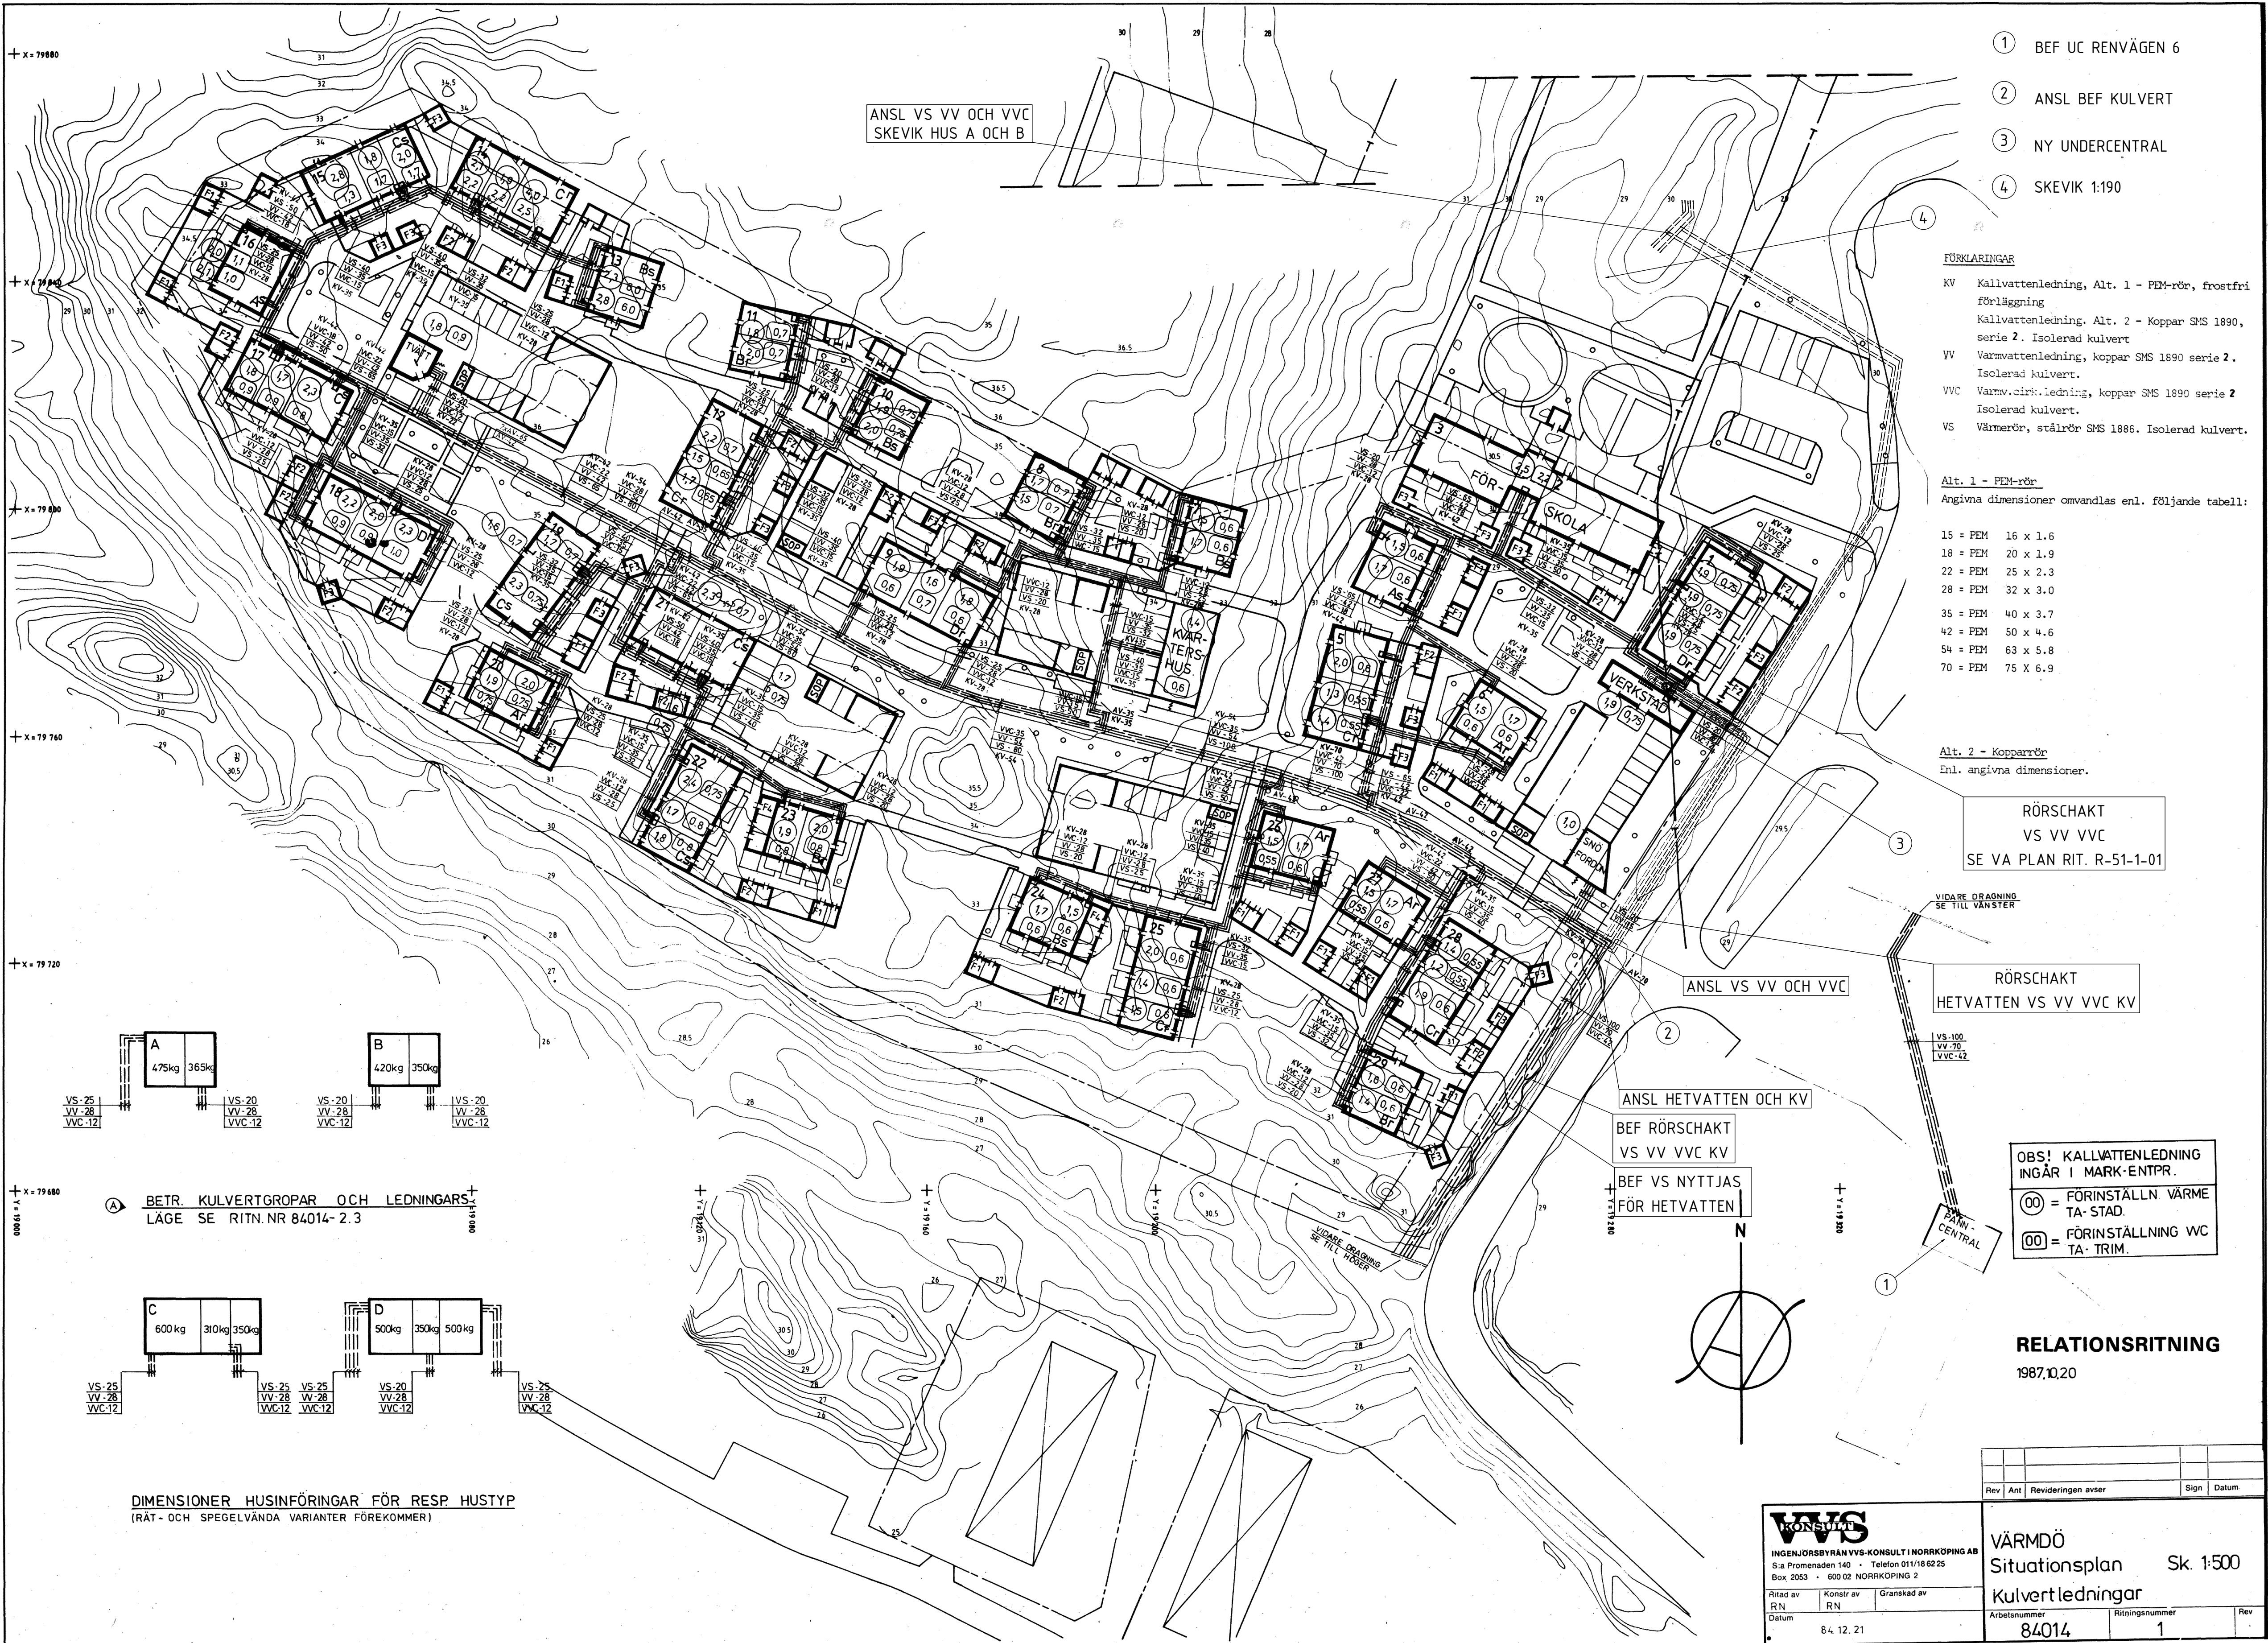

- ① BEF UC RENVÄGEN 6
- ② ANSL BEF KULVERT
- ③ NY UNDERCENTRAL
- ④ SKEVIK 1:190

FÖRKLARINGAR

KV Kallvattenledning, Alt. 1 - PEM-rör, frostfri
Förläggning
Kallvattenledning, Alt. 2 - Koppar SMS 1890,
serie 2. Isolerad kulvert
VV Varmvattenledning, koppar SMS 1890 serie 2.
Isolerad kulvert.
VVC Varmv.cirk.ledning, koppar SMS 1890 serie 2
Isolerad kulvert.
VS Värmerör, stålör SMS 1886. Isolerad kulvert.

Alt. 1 - PEM-rör
Angivna dimensioner omvandlas enl. följande tabell:

15 = PEM	16 x 1.6
18 = PEM	20 x 1.9
22 = PEM	25 x 2.3
28 = PEM	32 x 3.0
35 = PEM	40 x 3.7
42 = PEM	50 x 4.6
54 = PEM	63 x 5.8
70 = PEM	75 x 6.9


Alt. 2 - Kopparrör
Enl. angivna dimensioner.

RÖRSCHAKT
VS VV VVC
SE VA PLAN RIT. R-51-1-01


RÖRSCHAKT
HETVATTEN VS VV VVC KV

OBS! KALLVATTENLEDNING
INGÅR I MARK-ENTPR.
⊙ = FÖRINSTÄLLN VÄRME
TA- STAD.
⊙ = FÖRINSTÄLLNING VVC
TA- TRIM.

RELATIONSRTNING
1987.02.20

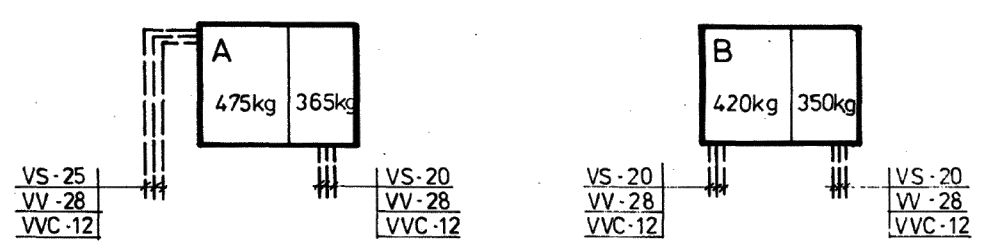

BETR. KULVERTGRÖPAR OCH LEDNINGAR
LÄGE SE RITN. NR 84014- 2.3

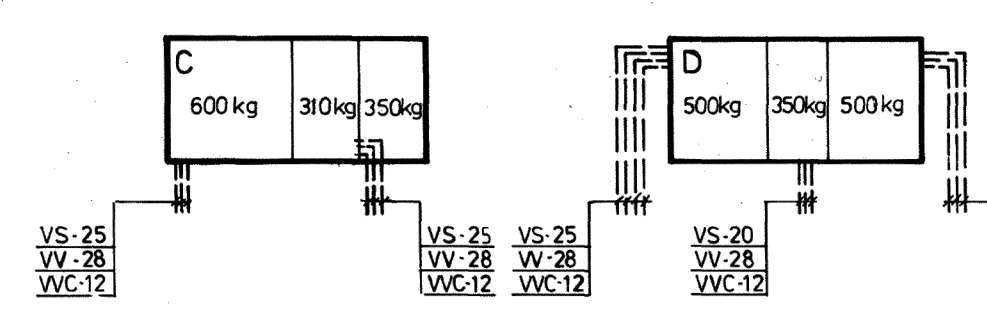

DIMENSIONER HUSINFÖRNINGAR FÖR RESP. HUSTYP
(RÄT- OCH SPEGELVÄNDA VARIANTER FÖREKOMMER)

VVS
INGENJÖRSBYRÅN VVS-KONSULT I NORRKÖPING AB
S:a Promenaden 140 • Telefon 011/18 62 25
Box 2053 • 600 02 NORRKÖPING 2

VÄRMDÖ
Situationsplan
Kulvert ledningar
Sk. 1:500

Ritad av R.N.	Konstr av R.N.	Granskad av
Datum 8.4.12.21	Arbetsnummer 84014	Ritningsnummer 1

BET	ANT	ÄNDRINGEN AVSER	SIGN	DATUM
-----	-----	-----------------	------	-------

BILAGA 1

FACIL CONSULT AB
VVS-PROJEKTERING
TEL: 08-500 240 50 FAX: 08-504 401 47

UPPDRAG NR 24049	RITAD AV HJN	HANDLÄGARE HJN
DATUM 2024-11-29	ANSVARIG PHS	

SKEVIK 1:190
FISKGJUSEVÄGEN
OMRÅDESOVERSIKT

UNDERCENTRALER OCH RÖRSTRÄCKNING

SKALA 1:20/A1 1:40/A3	RITNING NR V-56	BET
-----------------------------	--------------------	-----