


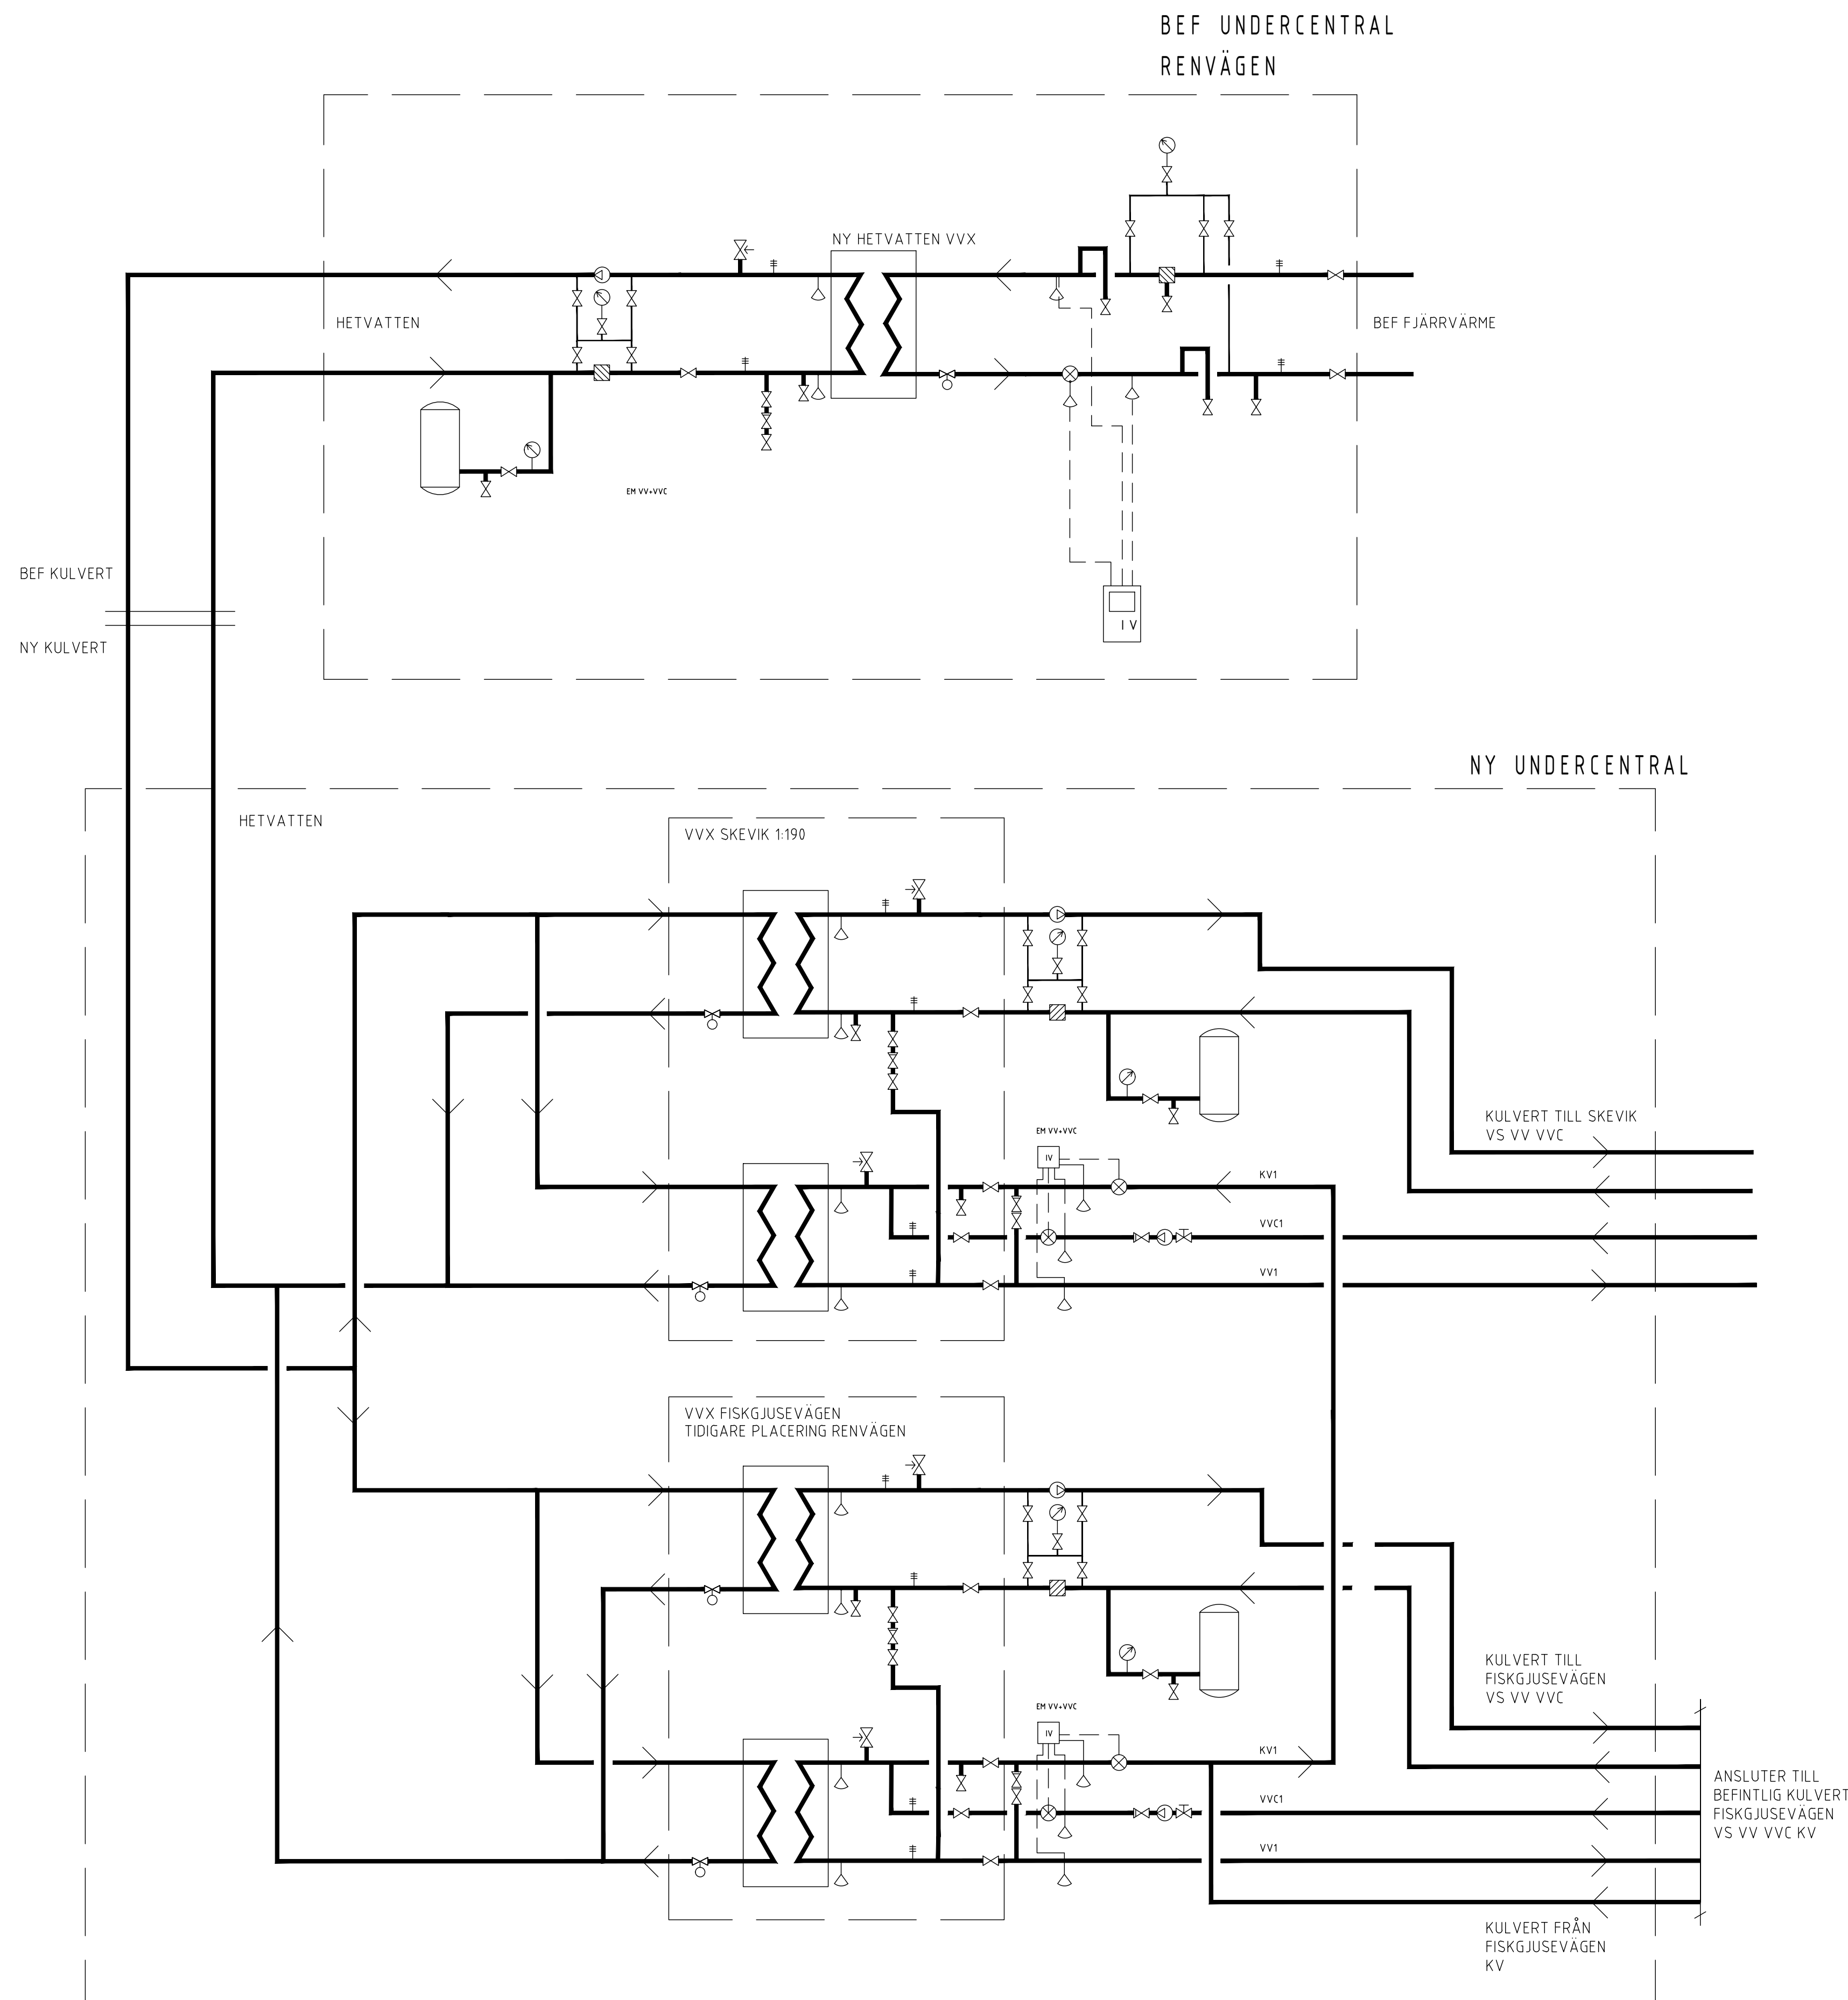

FÖRKLARINGAR

- EXPANSIONSKÄRL
- VÄXLARE
- GIVARE
- TERMOMETER
- PUMP
- INJUSTERINGSVENTIL
- AVSTÄNGNINGSVENTIL
- STYRVENTIL
- BACKVENTIL
- MÄTARE
- SÄKERHETSVENTIL
- FILTER
- MANOMETER
- DIFFERENSTRYCKVENTIL

BET	ANT	ÄNDRINGEN AVSER		SIGN	DATUM
BILAGA 2					
 FACIL CONSULT AB VVS-PROJEKTERING TEL: 08-500 240 50 FAX: 08-504 401 47					
UPPDRAG NR: 2049		RITAD AV HJN		HANDLÄGGARE HJN	
DATUM 2024-11-29		ANSVARIG PHS			
SKEVIK 1:190					
PRINCIP FLÖDESSCHEMA					
VS-INSTALLATIONER					
SKALA	- / A1 - / A3	RITNING NR			BET
V50.8-100					