
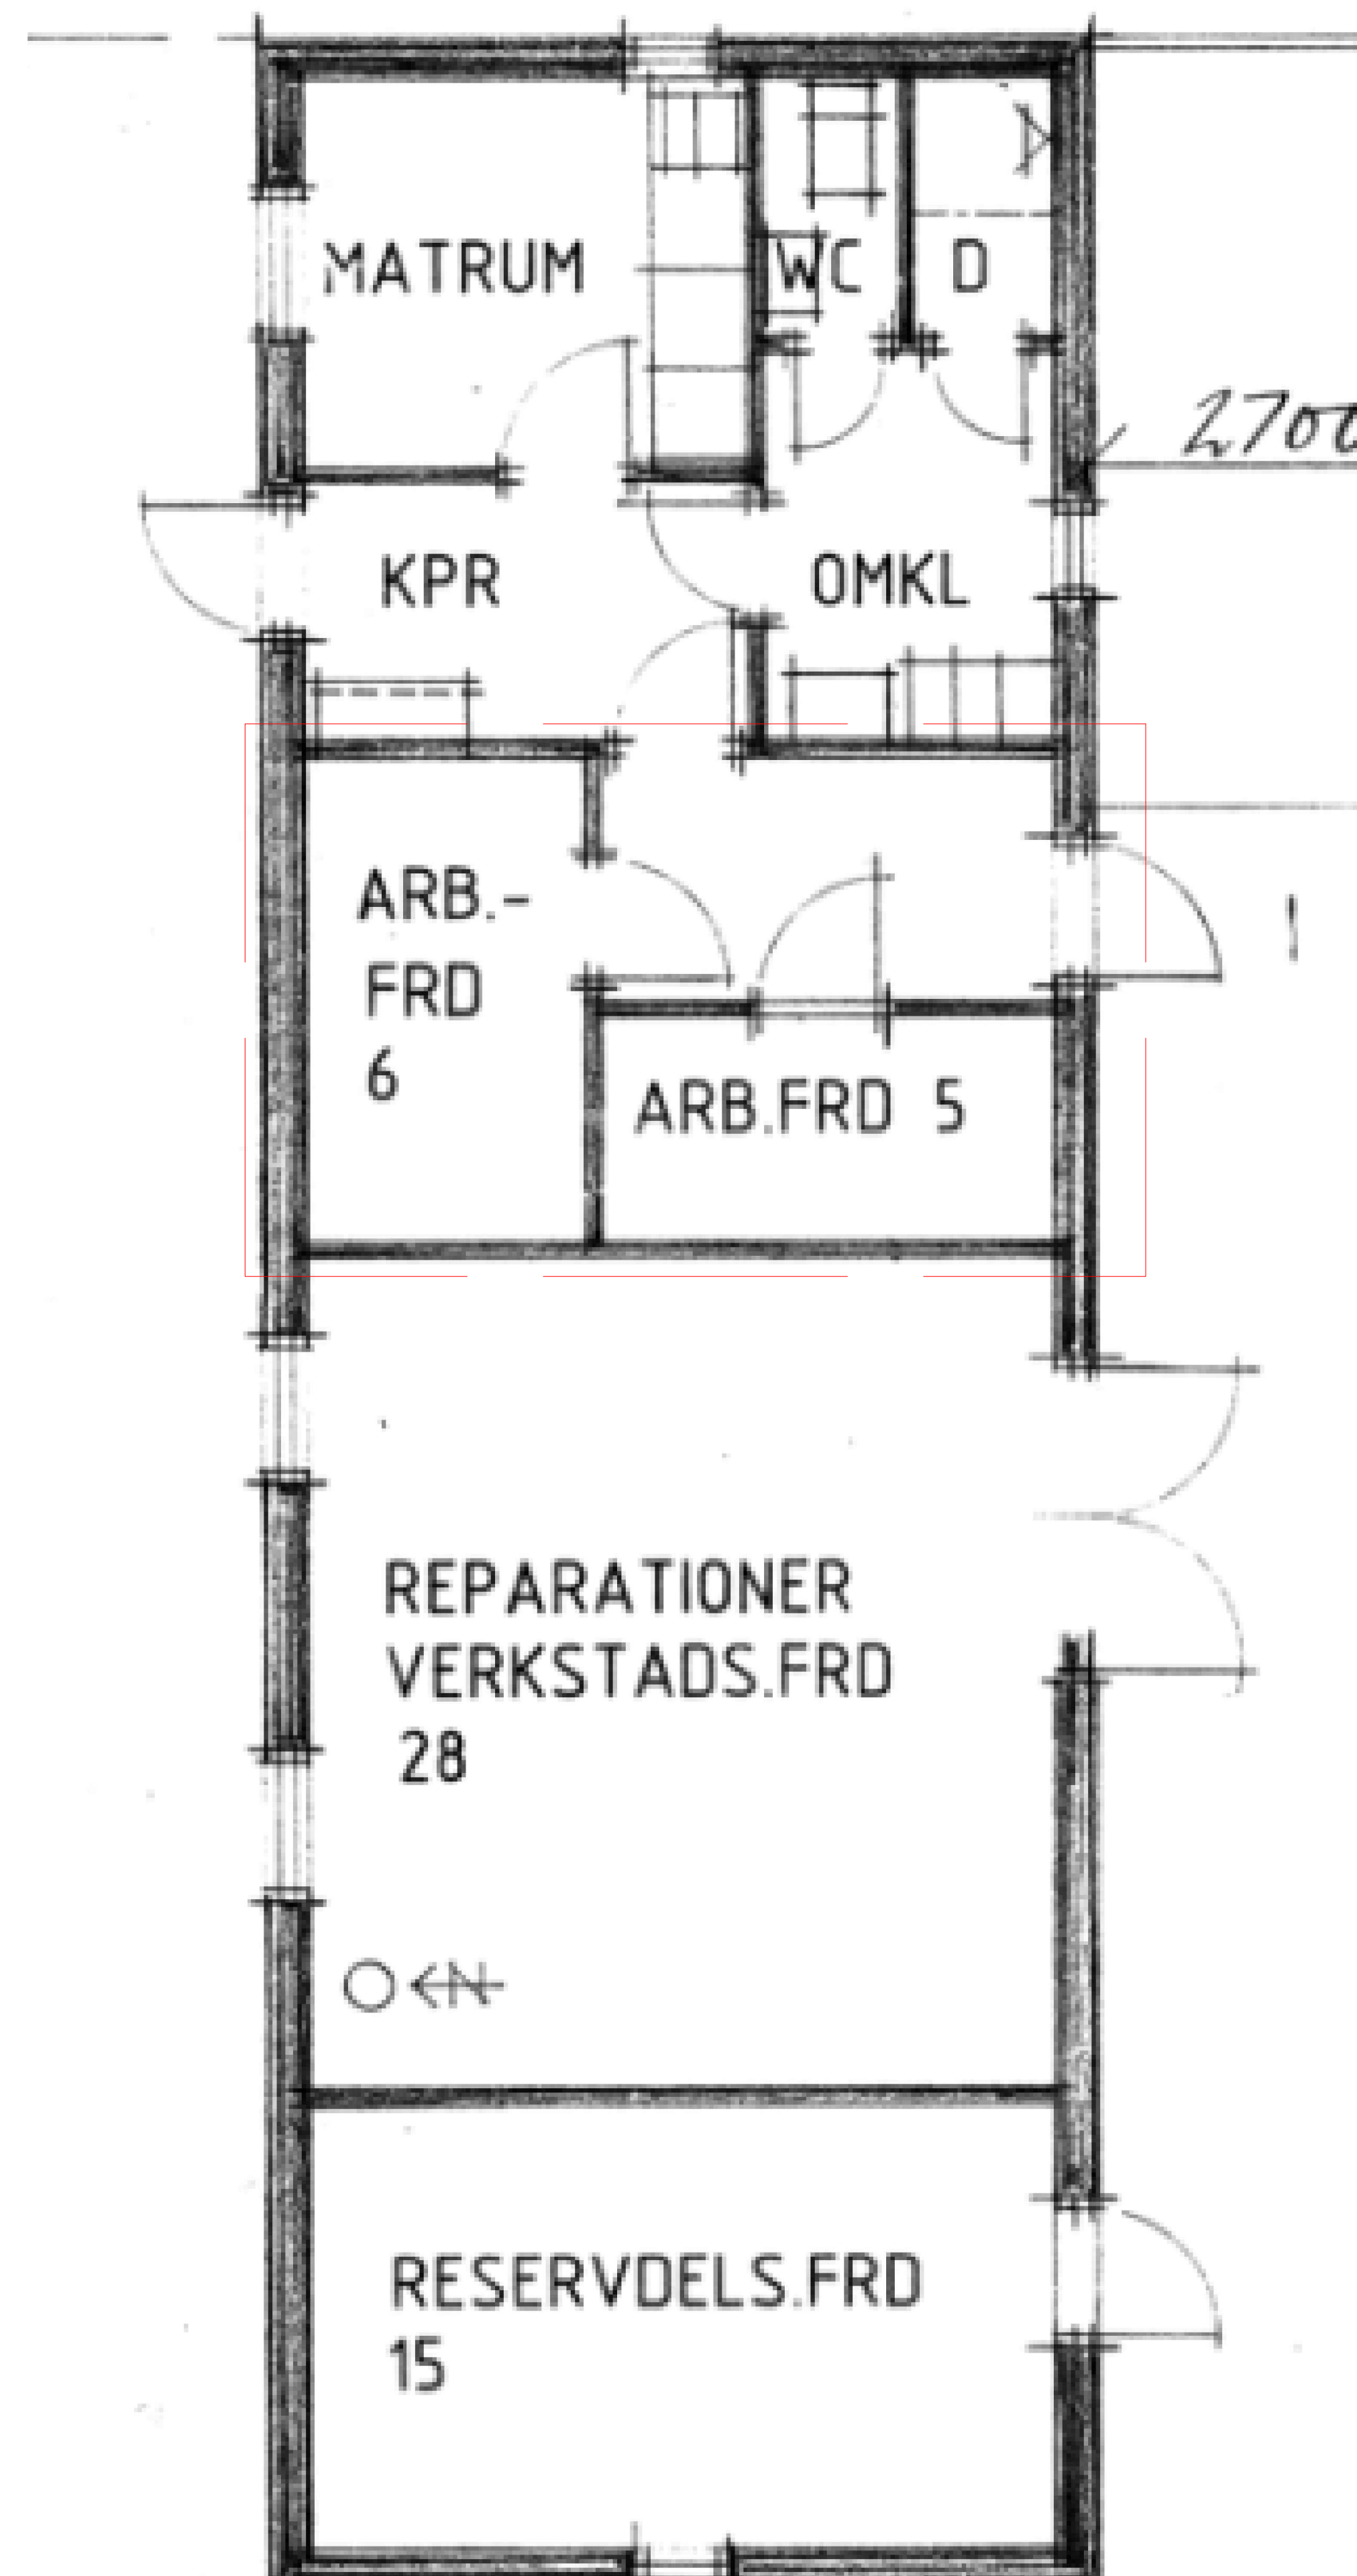
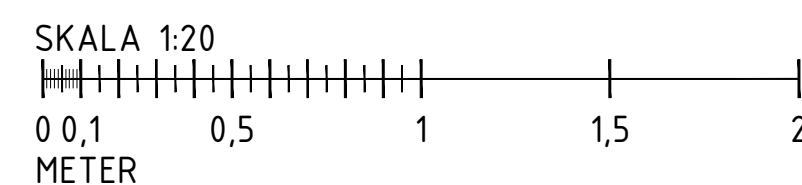


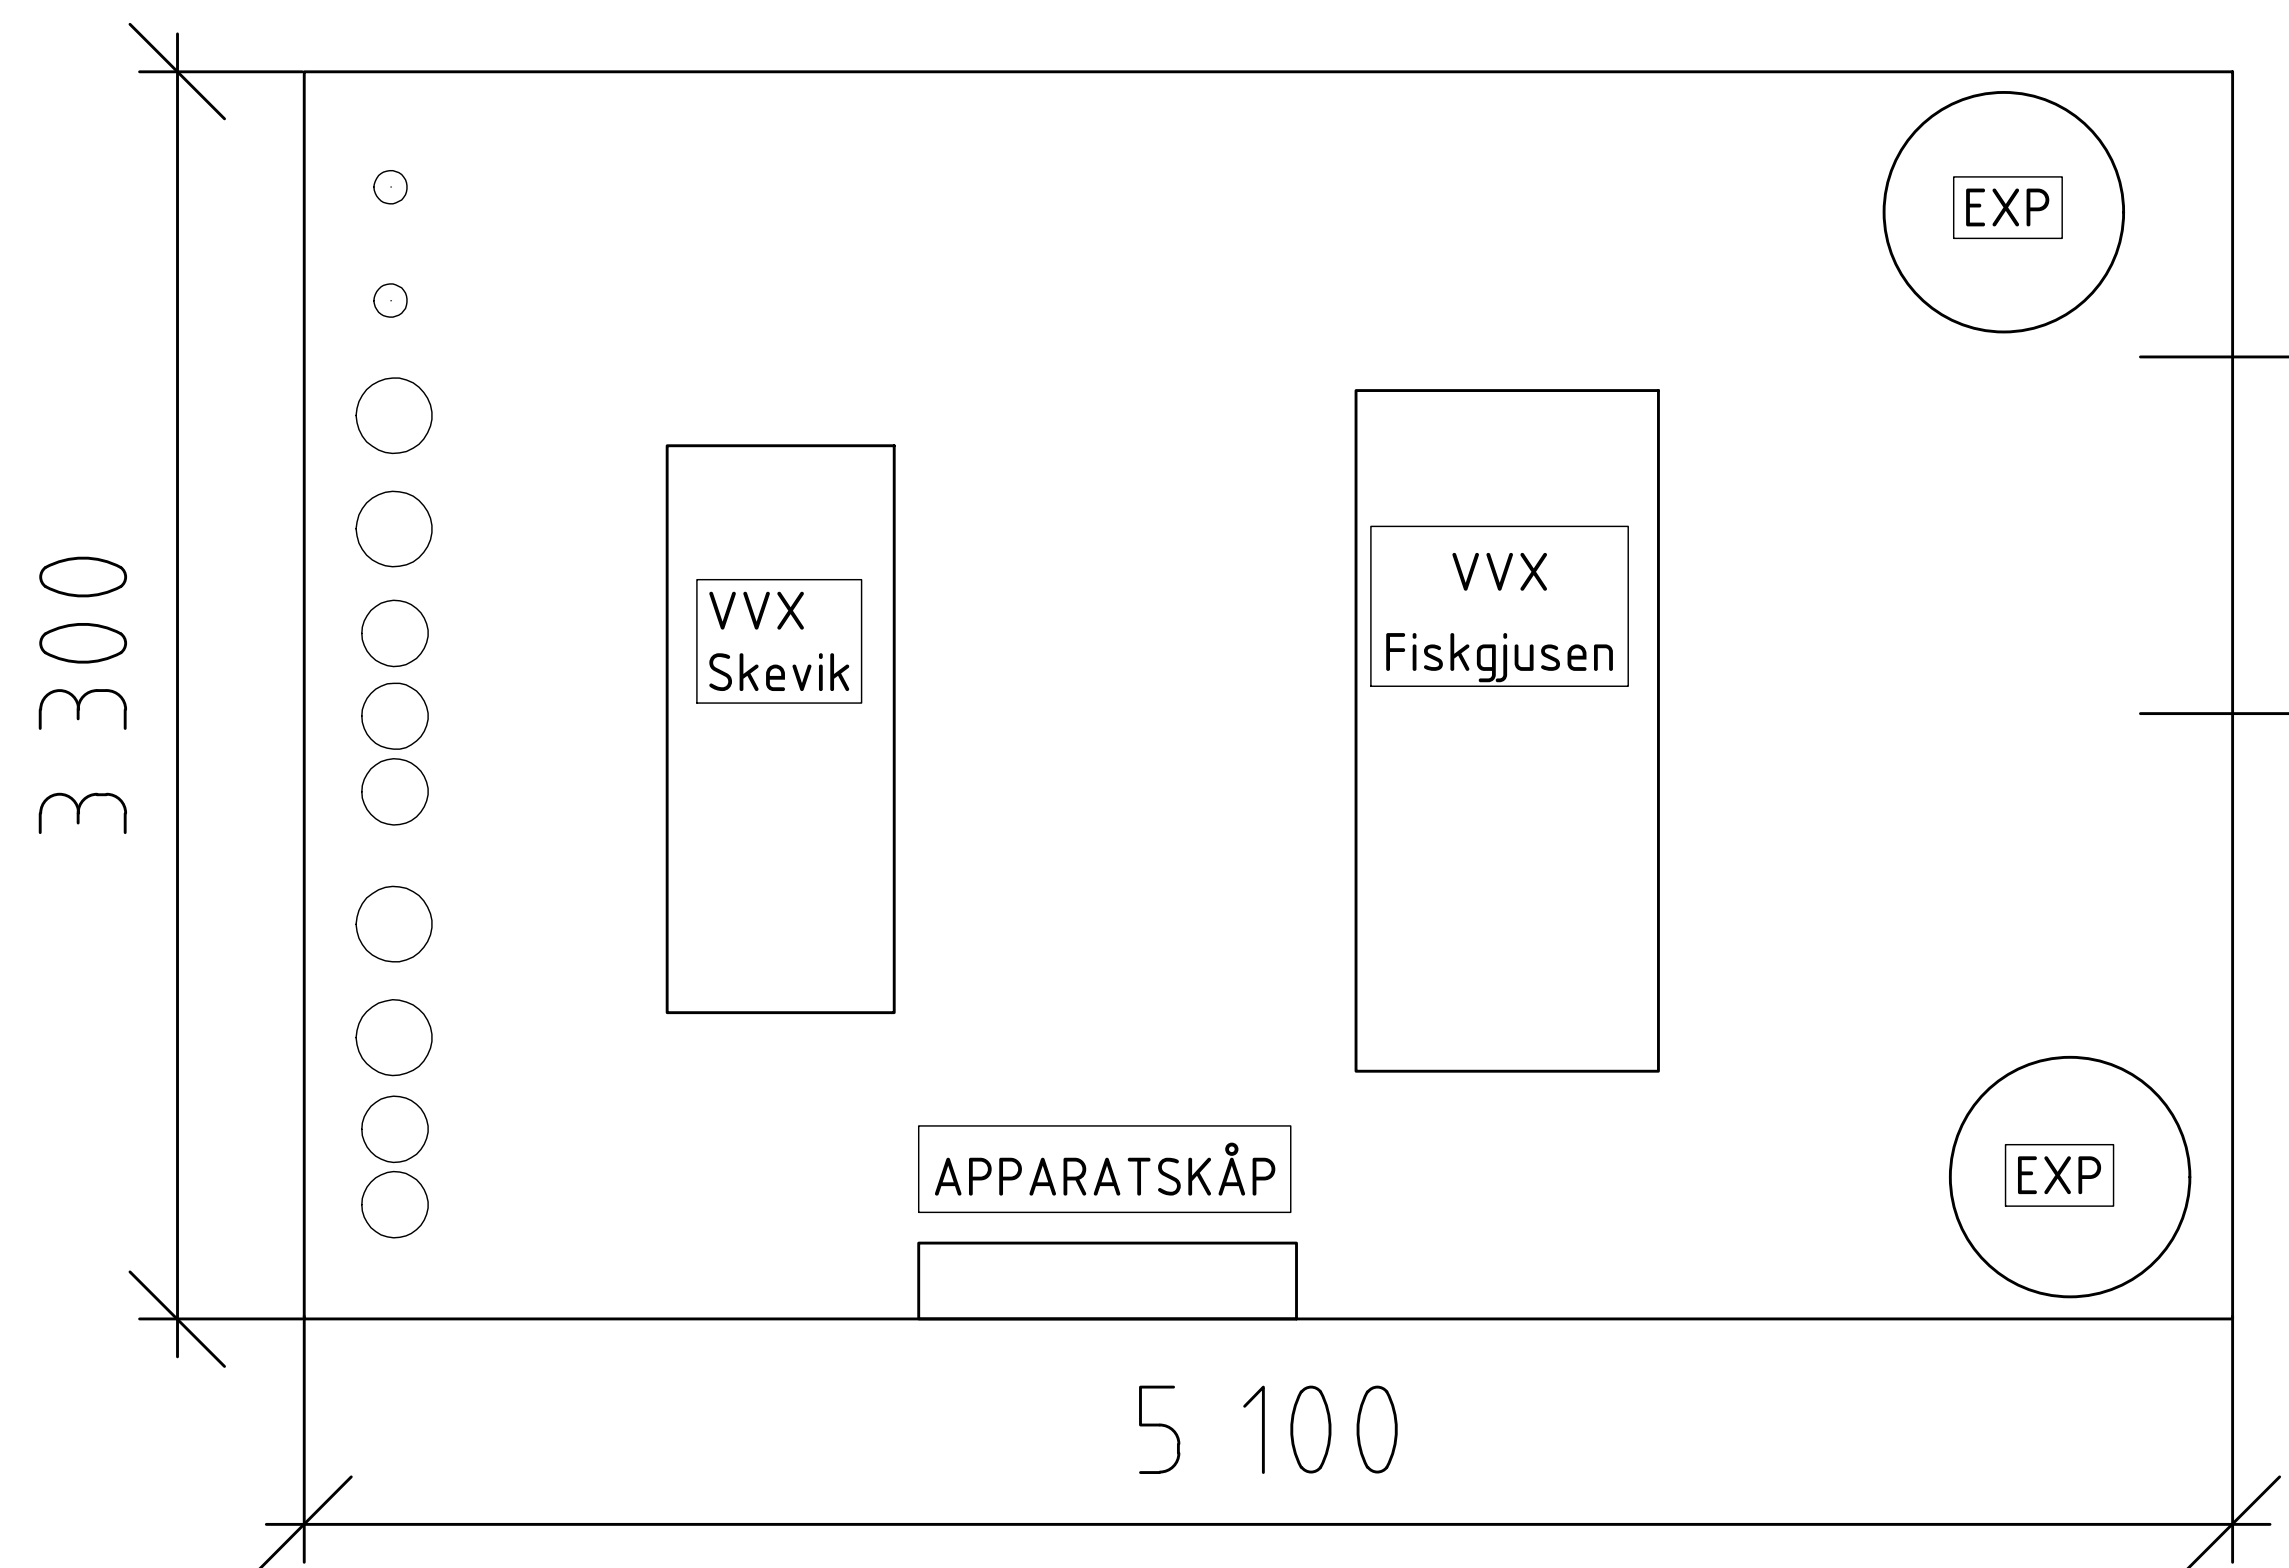

EJ I SKALA

BET	ANT	ÄNDRINGEN AVSER	SIGN	DATUM
BILAGA 3				
 FACIL CONSULT AB VVS-PROJEKTERING TEL: 08-500 240 50 FAX: 08-504 401 47				
UPPDRAG NR 24049		RITAD AV HJN		HANDLÄGGARE HJN
DATUM 2024-11-29		ANSVARIG PHS		
SKEVIK 1:190 FISKGJUSEVÄGEN				
NY UNDERCENTRAL				
APPARAT PLACERINGAR				
SKALA 1:20/A1 1:40/A3	RITNING NR V-50-UC			BET