
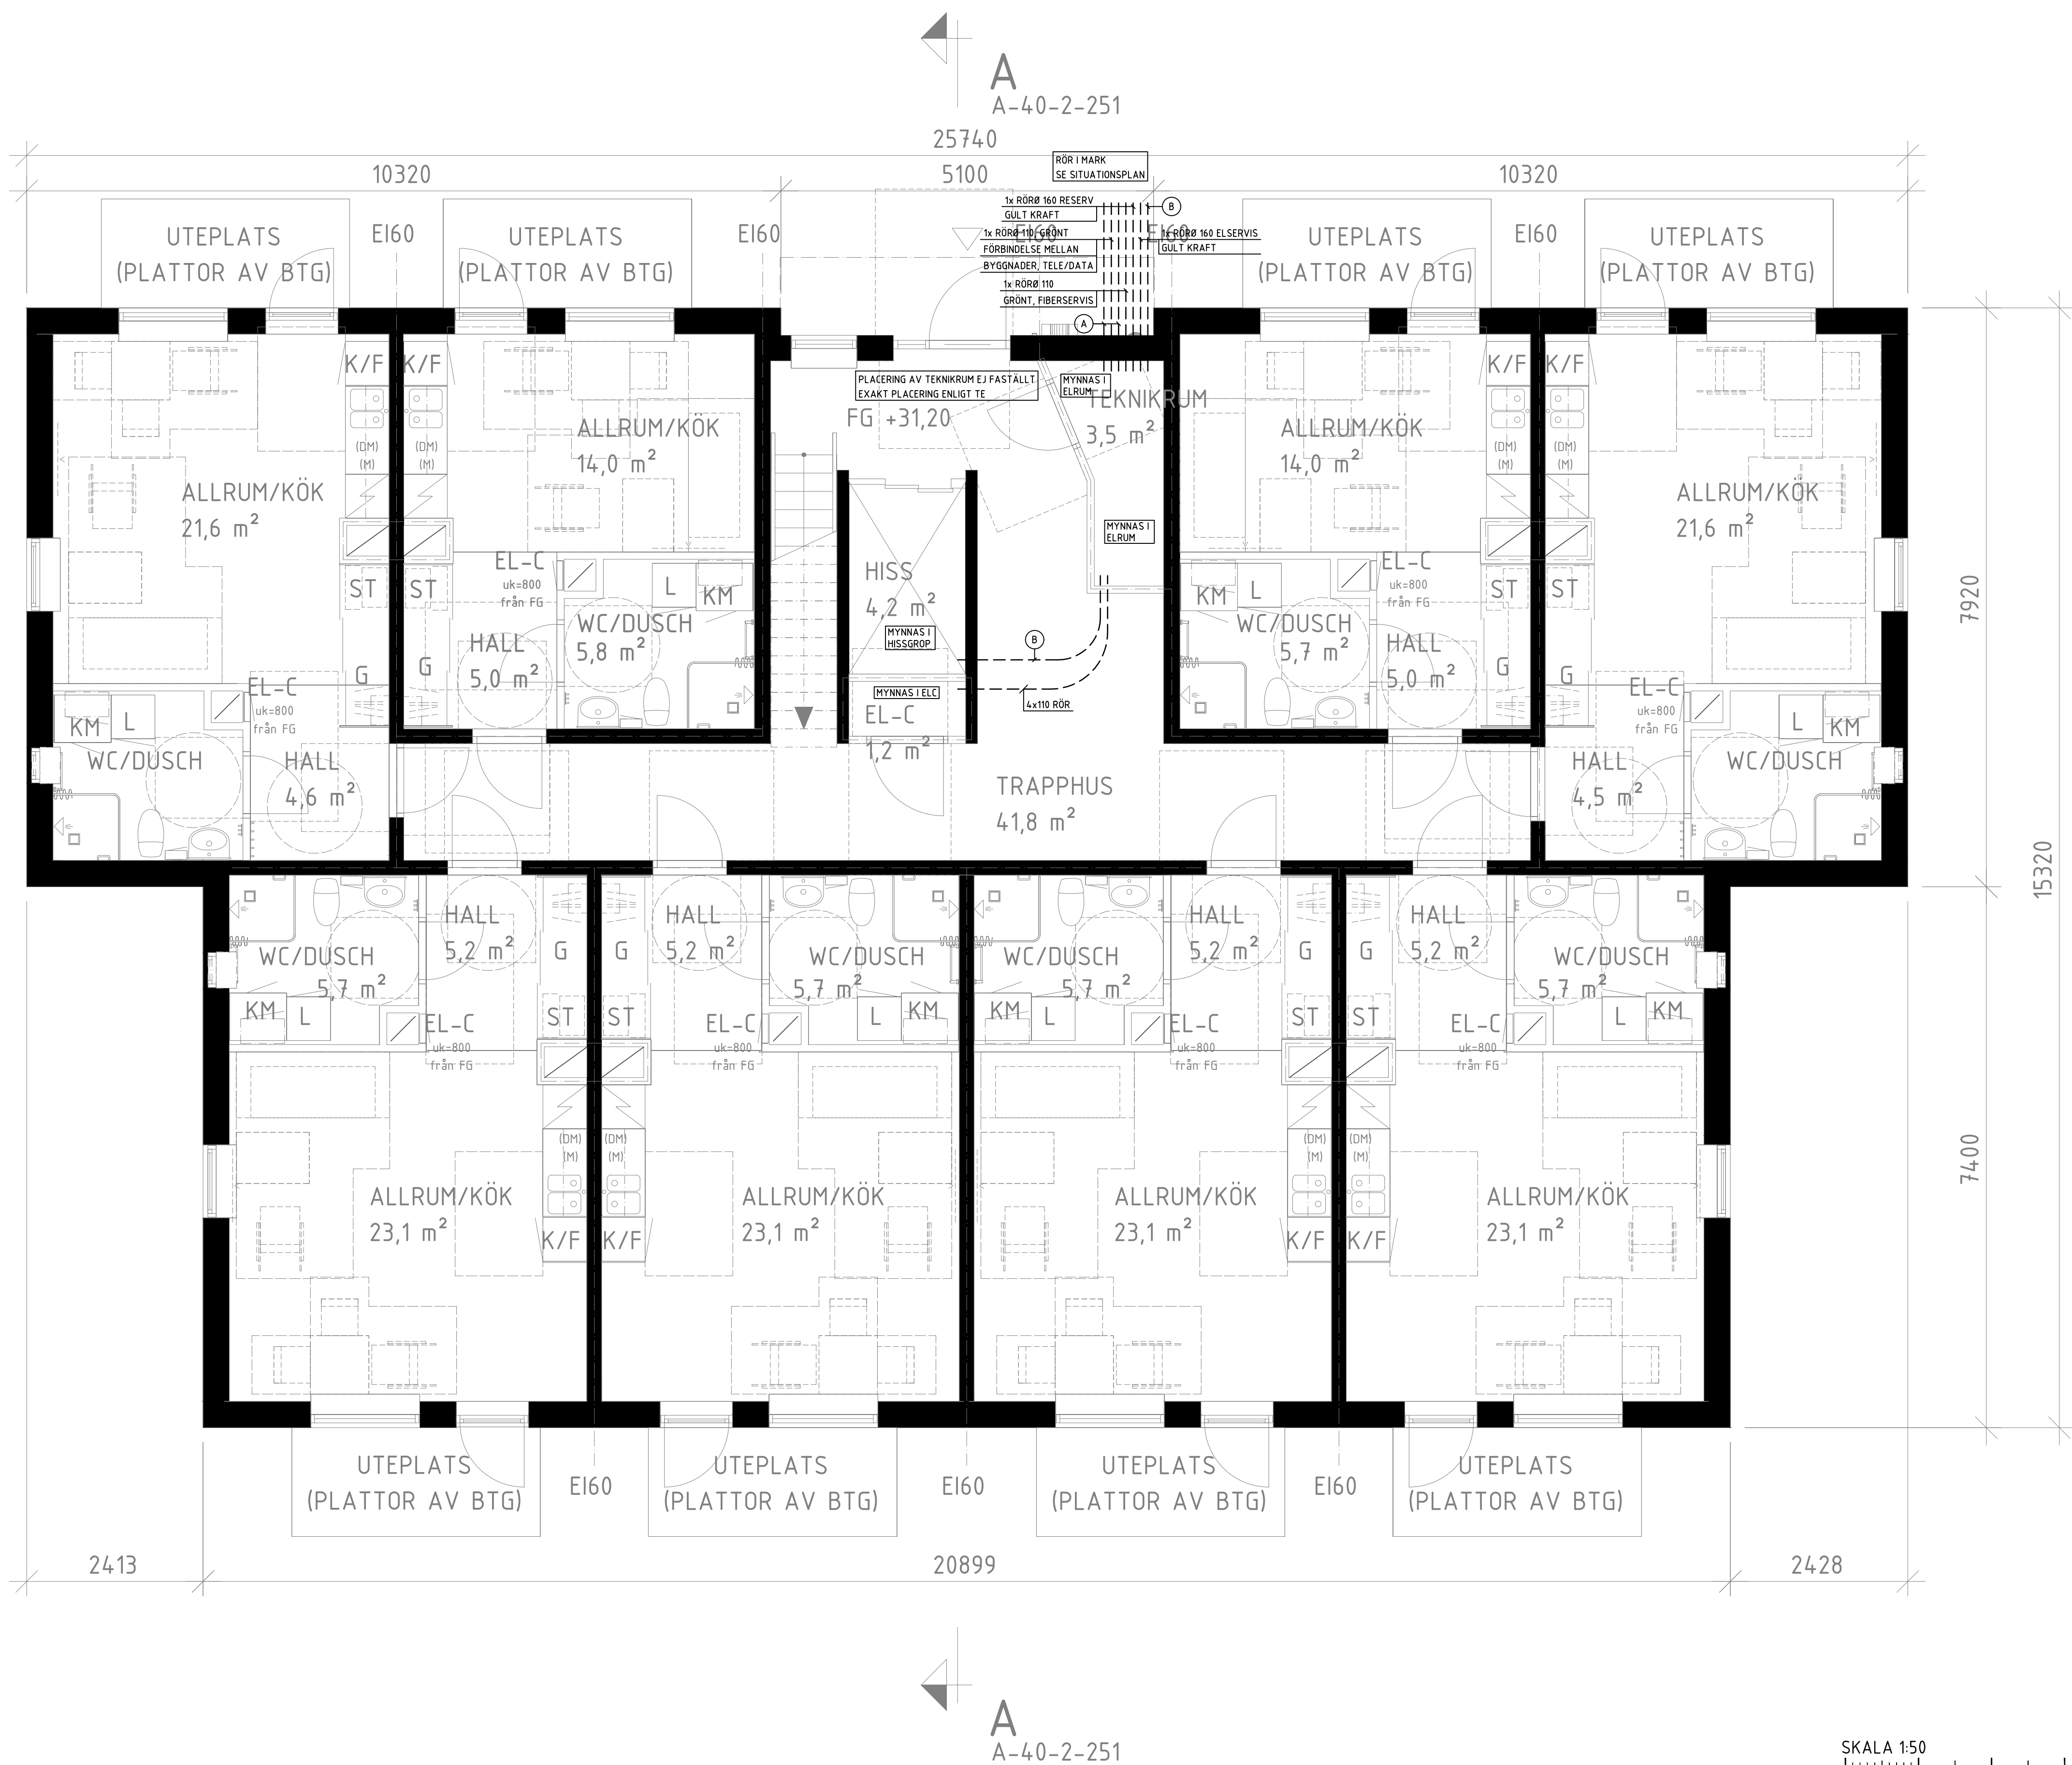


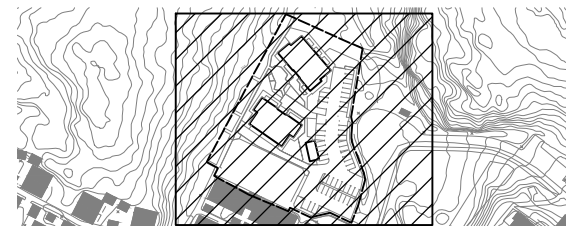

- FÖRKLARINGAR
- RÖR I MARK, ANTAL OCH AREA ANGIVET MED LITTRA
 - KABELBRUNN
 - BELYSNINGSSTOLPE INKL. FUNDAMENT MED ERF. MATERIAL
 - Ⓐ TOMRÖR GUL 50, INKL. LEDNING AVSETT FÖR BELYSNING LEDNINGSTYP/AREA BERÄKNAS VID DETALJPROJEKTERING
 - Ⓑ TOMRÖR GUL 500, TOMRÖR GRÖN 500 LEDNINGSTYP/AREA BERÄKNAS VID DETALJPROJEKTERING
 - Ⓒ SKYDDSRÖR GULT SPS 500, LEDNING LYT BEF. SÄKERSTÄLLS VID DETALJPROJEKTERING

Bet	Ändringen avser	Datum	Sign
SYSTEMHANDLING			
			
Orienteringsfigur			
			
X	E ELKONSULT E-TEC AB	073-6655510	
G	TREELINE CONSULTING AB	073-0844329	
K	KÄVER & MELLIN	072-7326731	
L	C.F. MØLLER SVERIGE AB	08-55576000	
M	VIKEN MILJÖKONSULT AB	070-6526445	
V	DLV AB	076-0224797	
VA	NIRAS SWEDEN AB	08-50384400	
Uppdrag nr: 240026		Ritad/konstr.: av K.HOLM	Handläggare K.HOLM
Datum 2024-11-29		Ansvarig K.HOLM	
SKEVIK, VÄRMDÖ SKEVIK 1:190 BYGGNAD B, GRUNDPLATTA KANALISATION			
Skala a1 1:50	Skala a3 1:100	Nummer E-61-1-209	Bet.