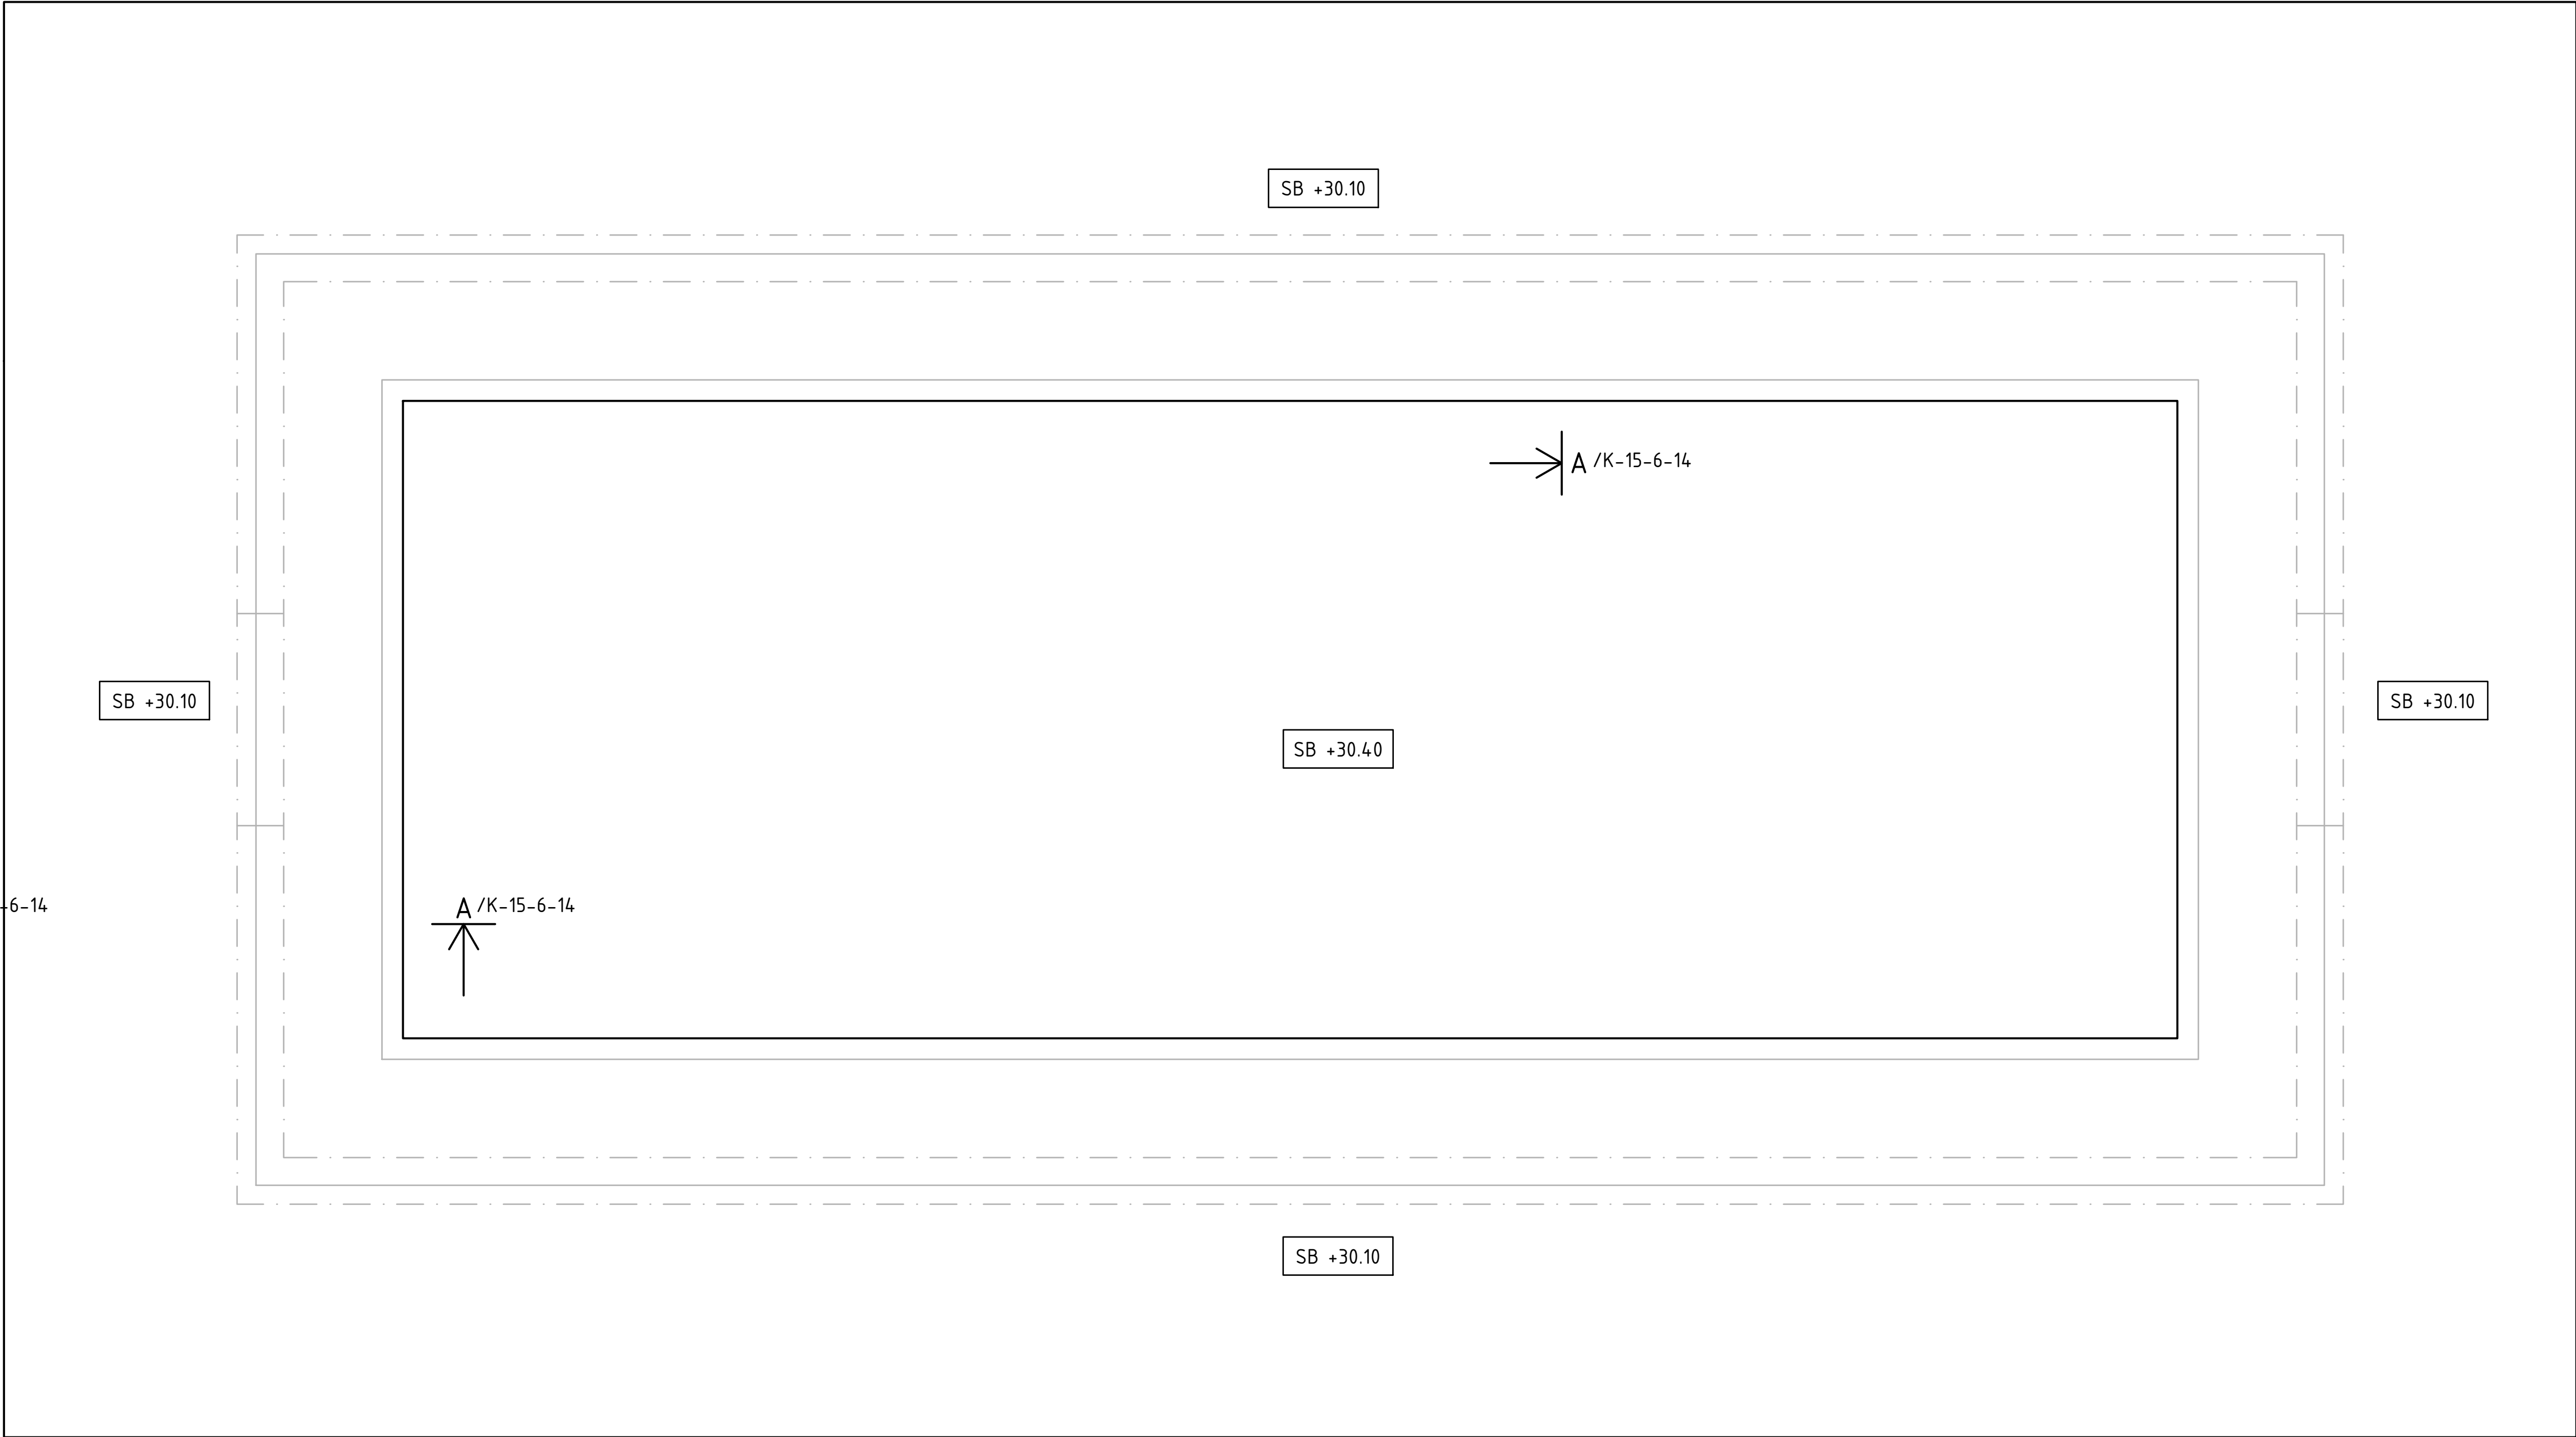


FÖRKLARINGAR

FÖRESKRIFTER

SE RITNING K-00-0-00

HÄNVISNINGAR


FÖRESKRIFTER K-00-0-00
PRINCIPDETALJER KOMPLEMENTBYGGNAD K-15-6-14

Bef.	Andringen avser	Datum	Sign
------	-----------------	-------	------

SYSTEMHANDLING



Orienteringsfigur

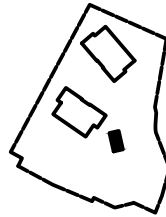

E	ELKONSULT E-TEC AB	073-6655510
G	TREELINE CONSULTING AB	073-0844329
K	KÅVER & MELLIN	072-7326731
L	C.F. MØLLER SVERIGE AB	08-55576000
M	VIKEN MILJÖKONSULT AB	070-6526445
V	DLV AB	076-0224797
VA	NIRAS SWEDEN AB	08-50384400

Uppdragsnr. 24222	Ritad/konstr. av FE	Handläggare FE
----------------------	------------------------	-------------------

Datum 2024-11-29	Ansvarig ANDERS HEDBERG
---------------------	----------------------------

SKEVIK, VÄRMDÖ
SKEVIK 1:190
Schaktplan Komplementbyggnad

Skala a1 1:20	Skala a3 1:40	Nummer K-11-1-01	Bef.
------------------	------------------	---------------------	------